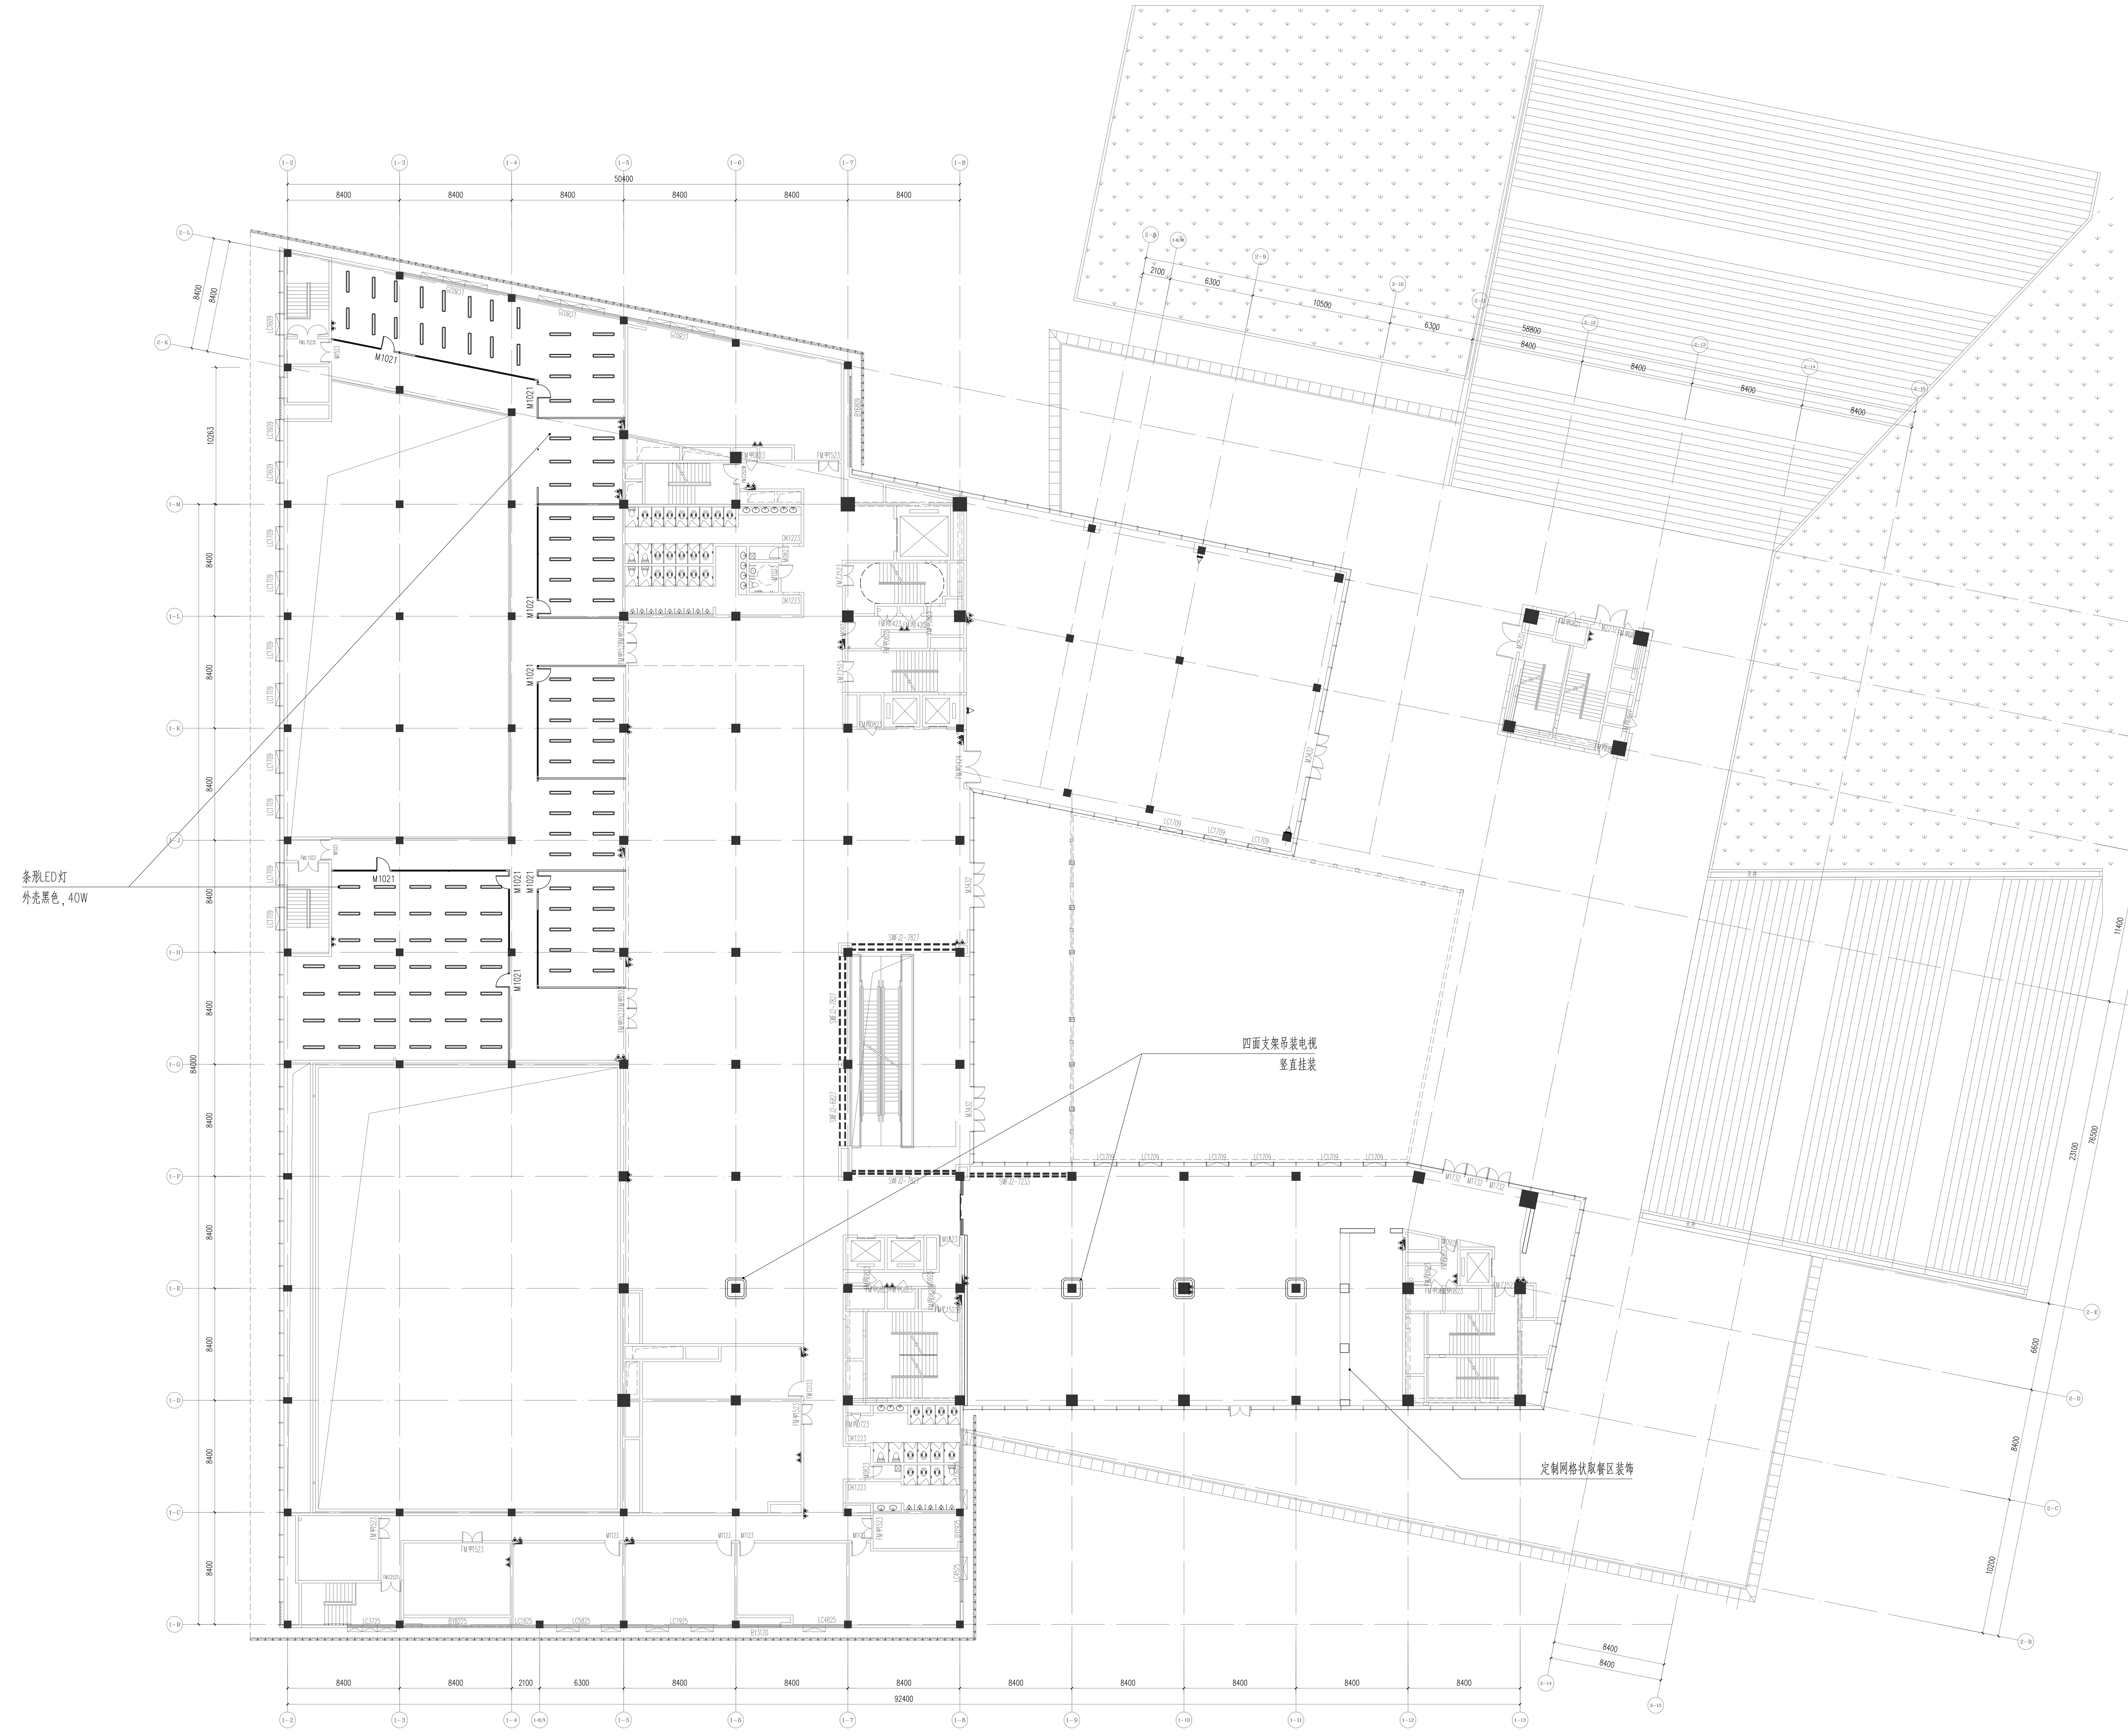

二层天花、灯具布置图 1:200

出图记录 ISSUE NOTES

版本 REV.	日期 DATE	备注 REMARK
A	2022.02	

注册执业栏 REGISTERED ARCHITECT/ENGINEER

姓名 NAME	
注册证书号码 REGISTRATION CERTIFICATE NO.	
注册印章号码 STAMP NO.	
设计号 JOB NO.	CD-20212856-F001
工程名称 PROJECT TITLE	成都大运会主新闻中心装饰搭建
子项名称 SUB ITEM	
建设单位 CLIENT	成都博雅文瑞文化传播有限公司
图名 DRAWING TITLE	二层天花、灯具布置图

单位 UNIT	mm	图别 DWG. CATEGORY	室施
比例 SCALE	1:200	图号 DWG. NO.	C02
日期 DATE	2022.02	版本 VER. NO.	A

制图 DRAWN BY	肖子颖
设计 DESIGNED BY	肖子颖
校对 CHECKED BY	李鼐文
专业负责人 DISCIPLINE CHIEF	肖子颖
设计总负责人 PROJECT CHIEF	张峻
审核 AUDIT	张峻
审定 APPROVED BY	华轲

基准方中
成都基准方中建筑设计股份有限公司
Chengdu JZFZ Architectural Design Co., Ltd.
中国 成都市 琉璃路8号华润广场A座7-15楼
电话：+86(28) 86333800 传真：+86(28) 86582990
7-15F, Tower A. Crland Plaza. No.8,LiuLi Road , Chengdu, P.R.C
tel. +86(28) 86333800 fax. +86(28) 86582990

工程设计资质证书编号：A151016191

电子文档编号：- CAD FILENAME

版 权 说 明
COPYRIGHT DECLARATION
此图版权为成都基准方中建筑设计股份有限公司所有，未经许可不得使用。