




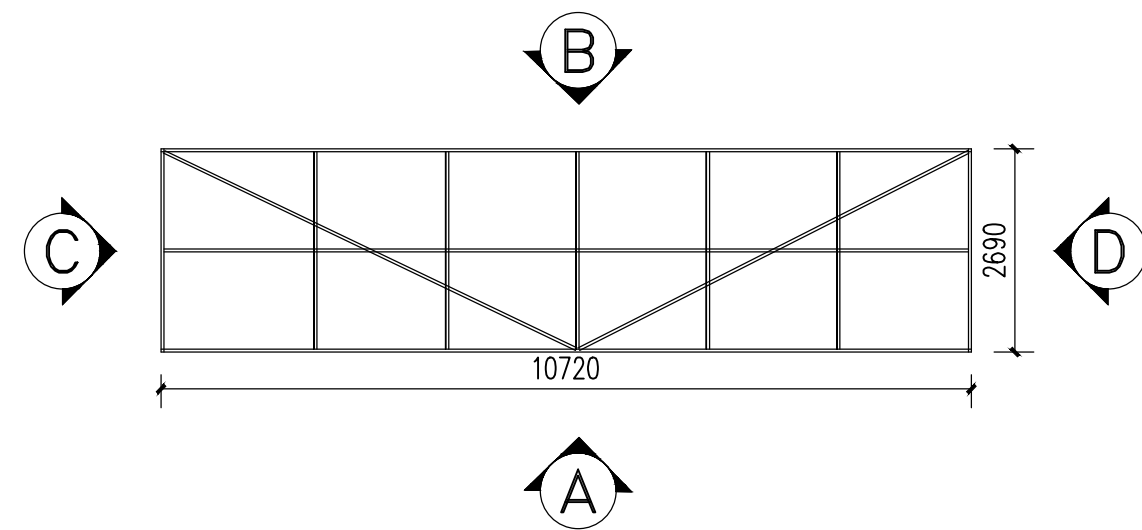

① 隔墙短边平面钢骨架图 1:100

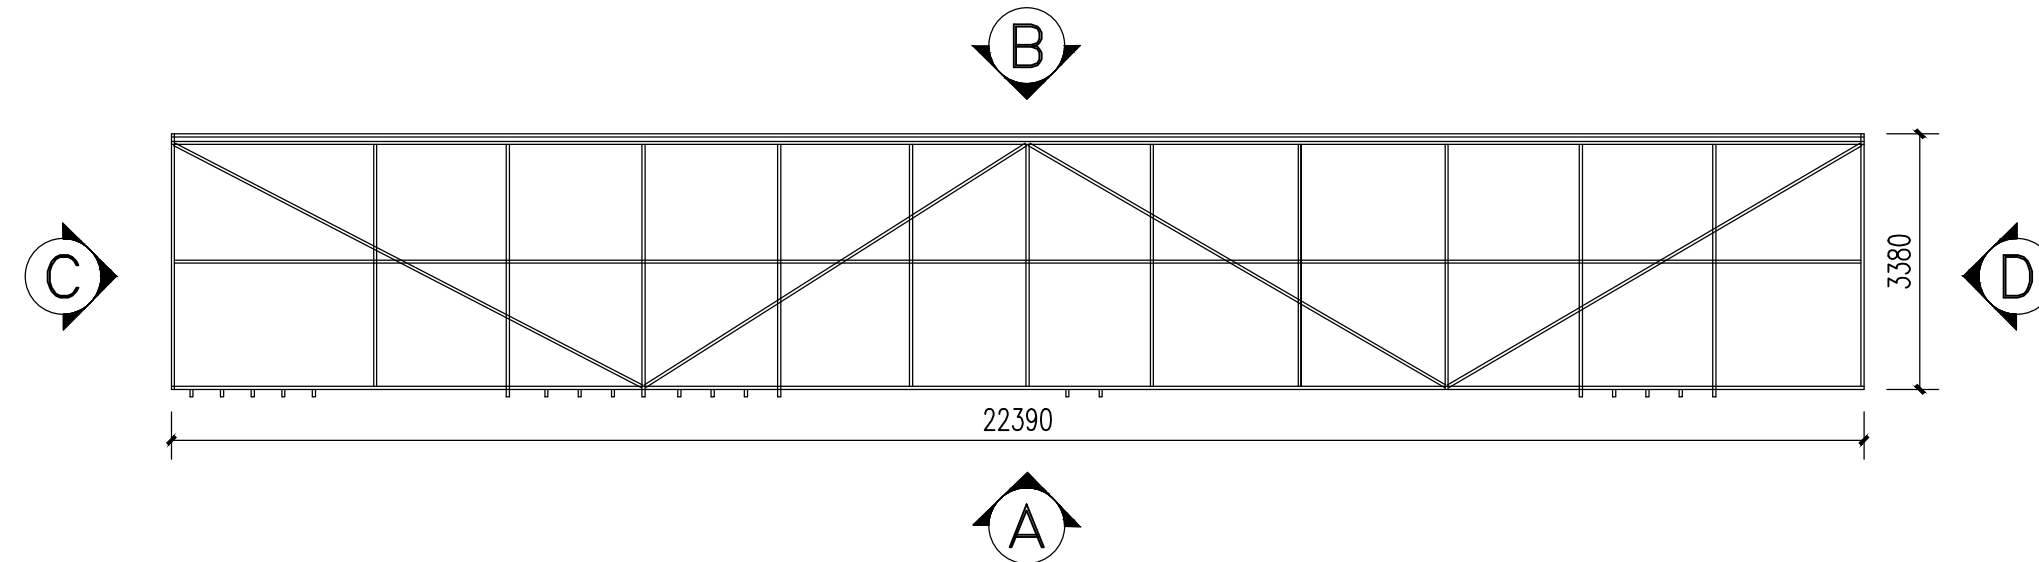


② 隔墙长边平面钢骨架图 1:100

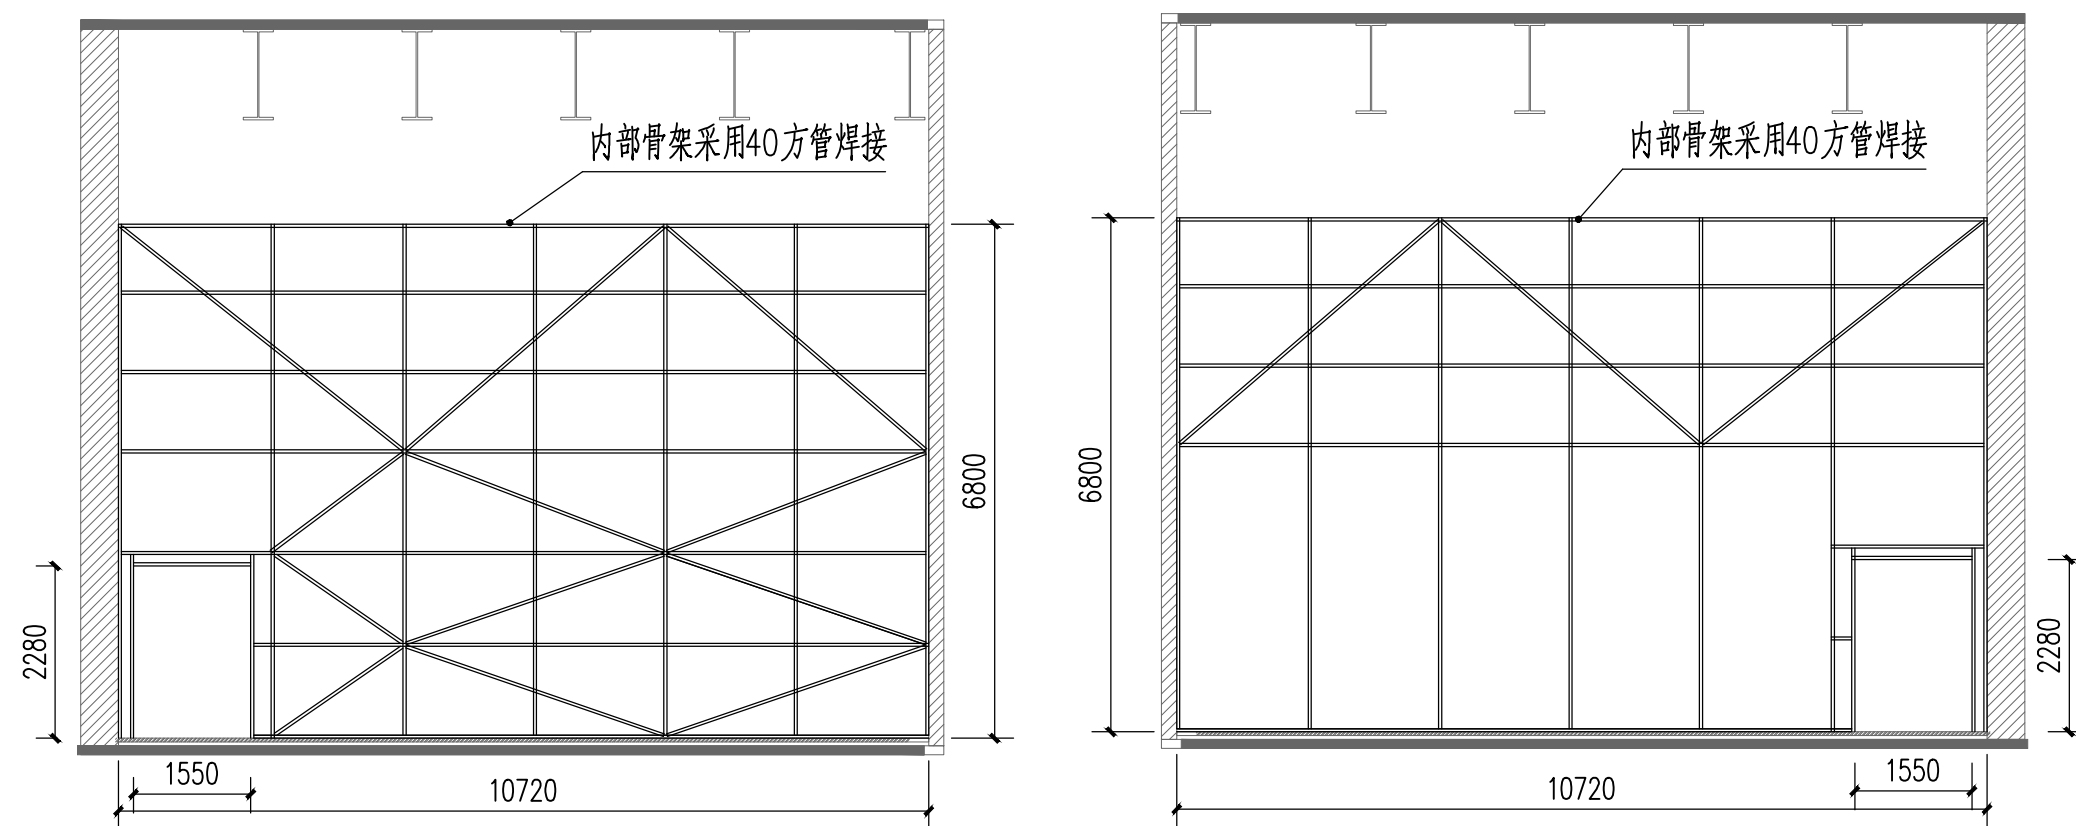


隔墙短边A立面钢骨架图 1:100

隔墙短边B立面钢骨架图 1:100

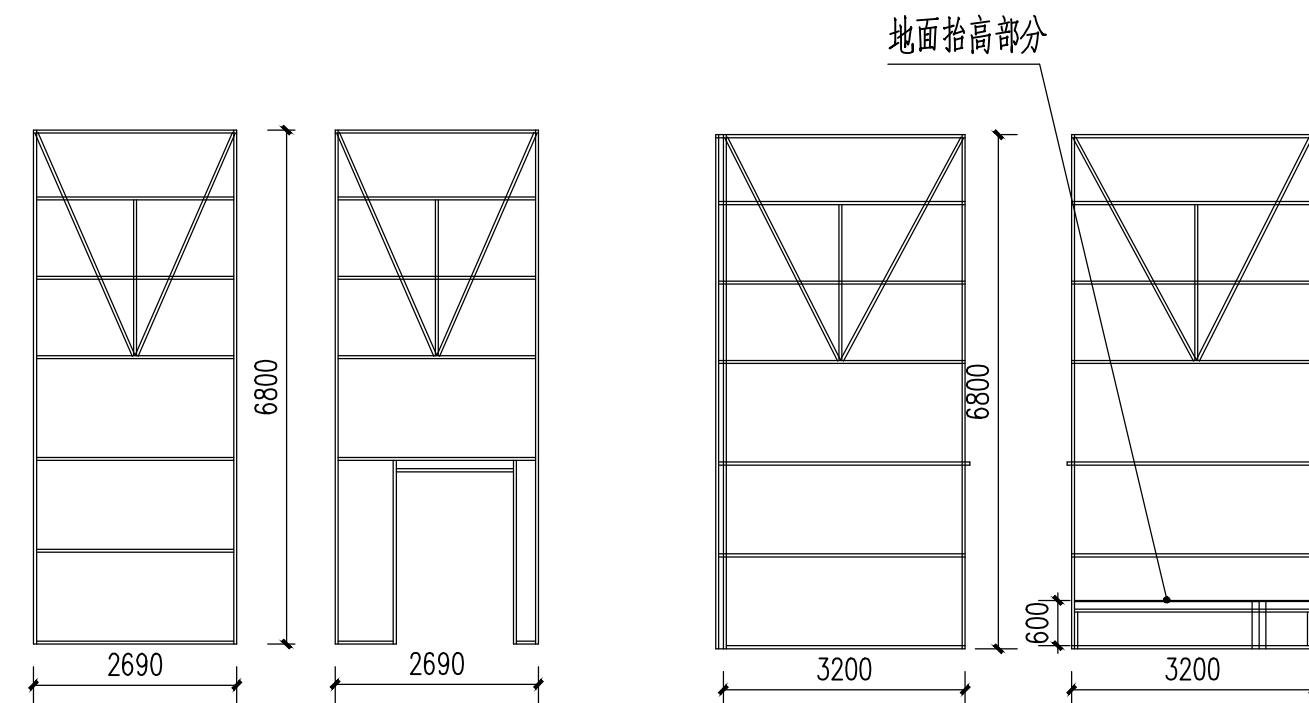

隔墙短边CD立面钢骨架图 1:100

隔墙长边CD立面钢骨架图 1:100

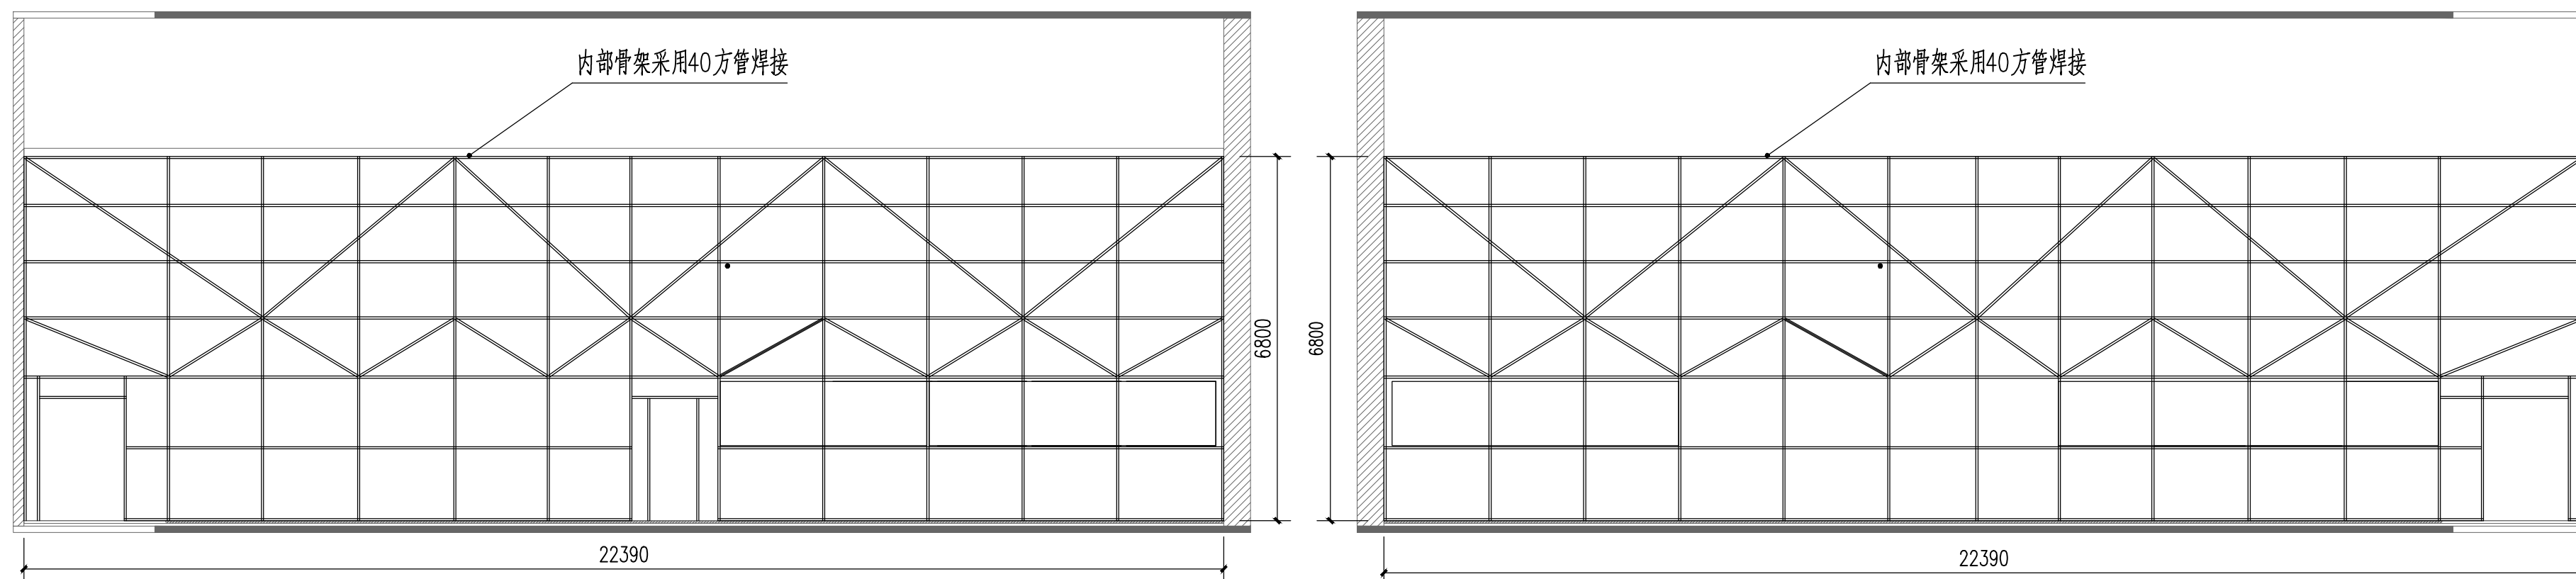

隔墙长边A立面钢骨架图 1:100

隔墙长边B立面钢骨架图 1:100

[illegible]

注册执业栏		REGISTERED ARCHITECT/ENGINEER	
姓 名		NAME	
注册证书号码		REGISTRATION CERTIFICATE NO.	
注册印章号码		STAMP NO.	
设计号: CD-20212856-F001		JOB NO.	
工程名称		PROJECT TITLE	
成都大运会主新闻中心装饰搭建			
子项名称		SUB ITEM	
建设单位:		CLIENT	
成都博雅文瑞文化传播有限公司			

图名		DRAWING NUMBER	
新闻发布厅隔墙钢骨架排布图			
单位	mm	UNIT	DWG. CATEGORY
比例	1:100	SCALE	DWG. NO.
日期	2022.02	DATE	VER. NO.
		图别	室施
		图号	D01
		版本	A

制 DRAWN BY	方苓	
设 DESIGNED BY	方苓	
校 CHECKED BY	李滢文	
专业负责人 DISCIPLINE CHIEF	肖子颖	
设计总负责人 PROJECT CHIEF	张峻	
审 AUDIT	张峻	
审 APPROVED BY	华轲	

中 方 基 准	
成都基准方中建筑设计股份有限公司	
Chengdu JZFY Architectural Design Co., Ltd.	
中国 成都市 琉璃路9号华润广场A座7-15楼	
电话: +86 (28) 86333800	传真: +86 (28) 86582990
7-15F, Tower A, Oriental Plaza, No.9Ruli Road, Chengdu, P.R.C	
tel. +86(28) 86333800	fax. +86(28) 86582990
工程投资资质证书编号: A151016191	
电子文档编号: -	
版 权 说 明	
COPYRIGHT DECLARATION	
此图版权为成都基准方中建筑设计股份有限公司所有, 未经许可不得使用。	