



采暖通风	总图		
电气	给排水		
暖通	结构		
五金	栏杆		

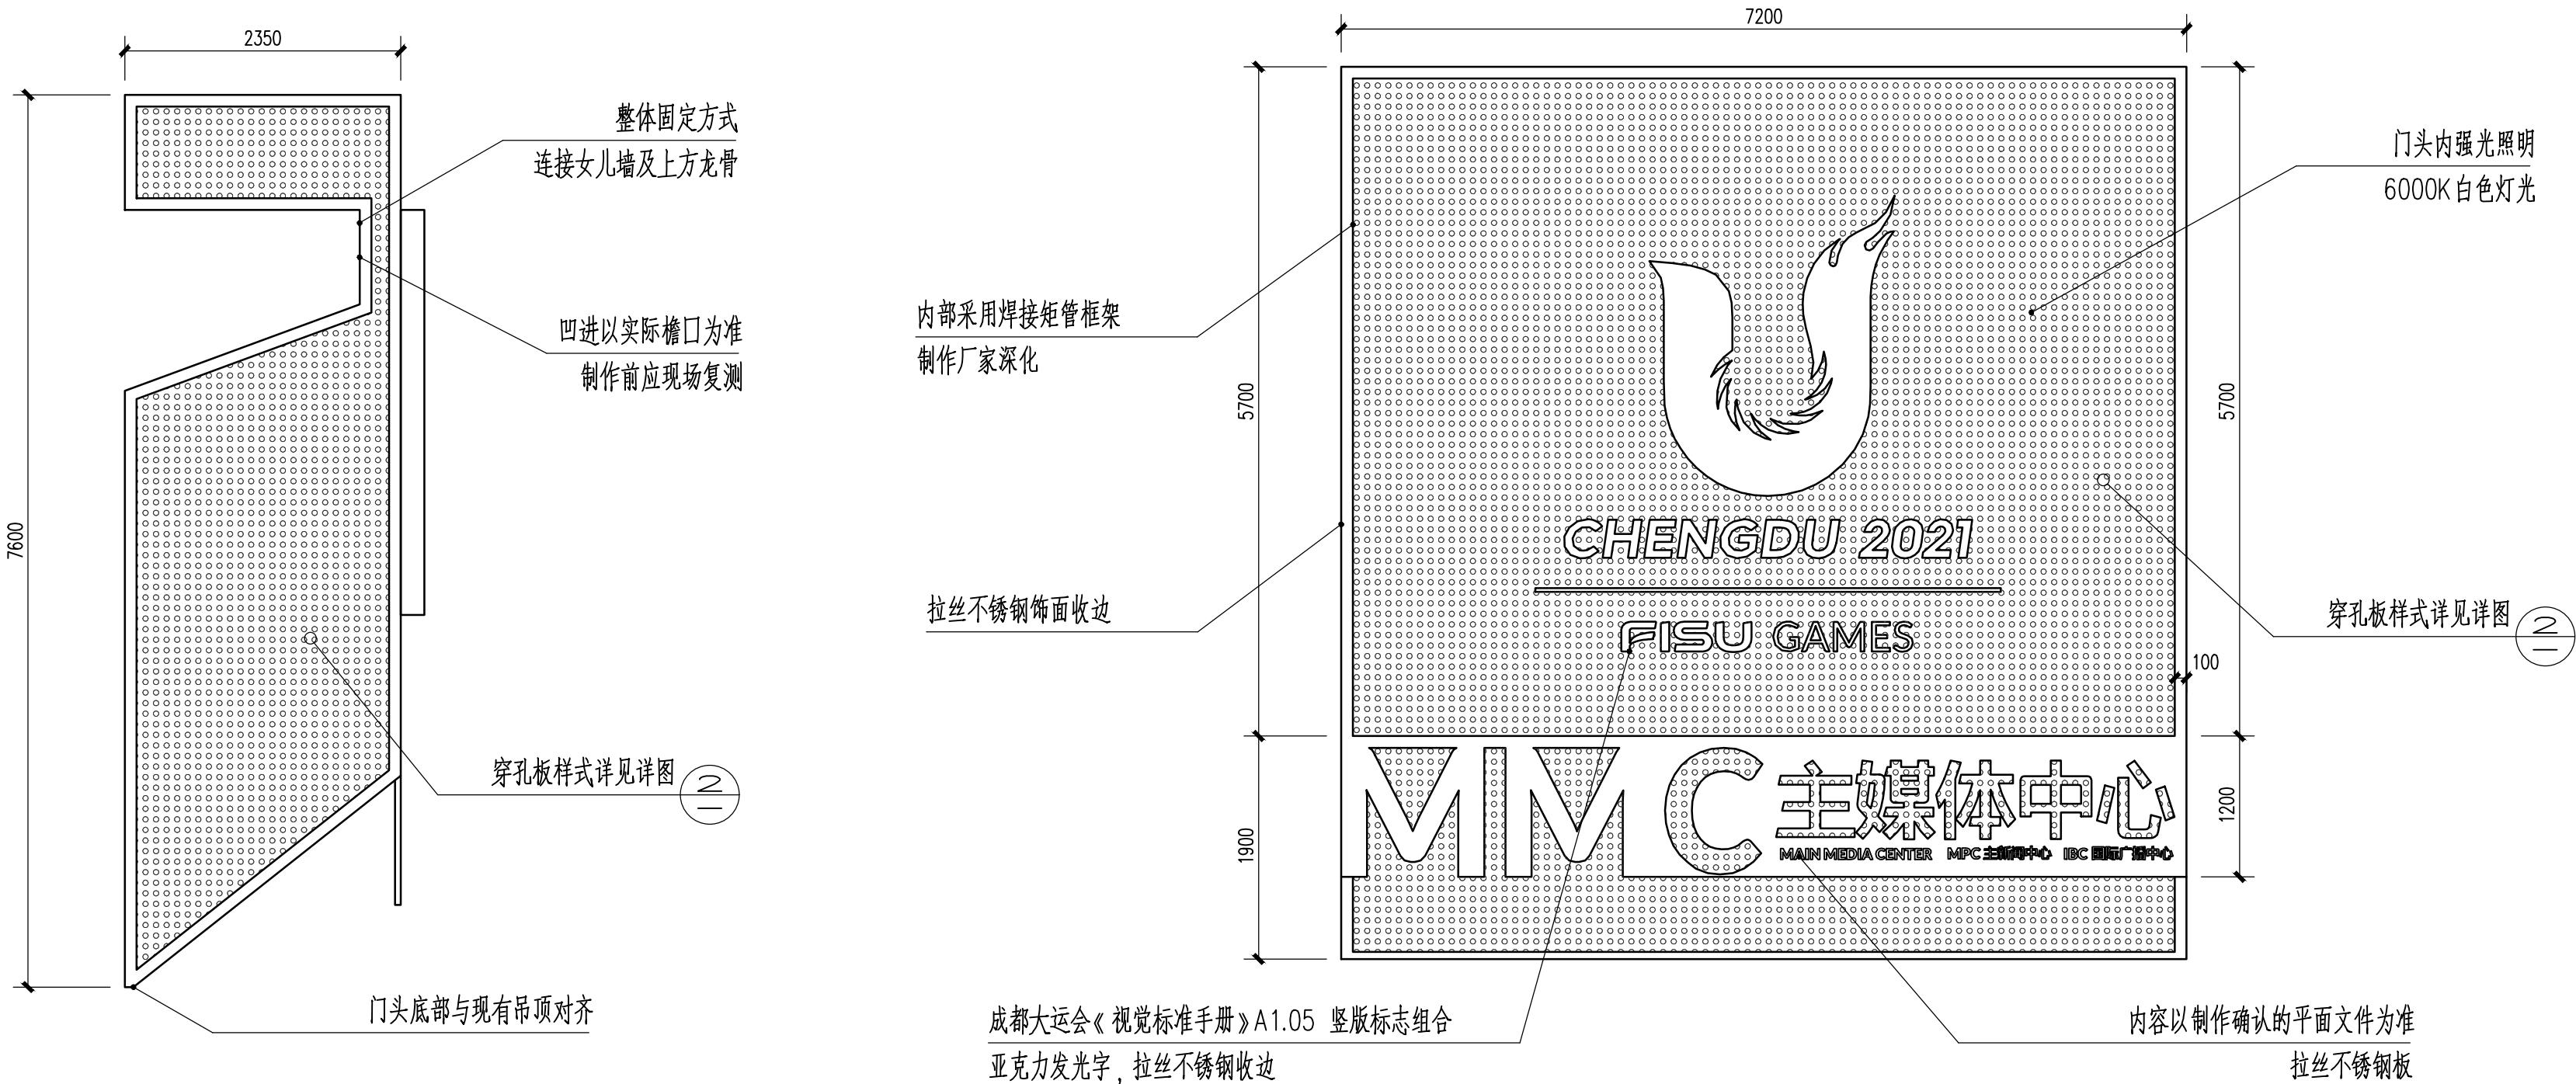


西入口门头侧视图 1:100

西入口门头正视图 1:100

① 西入口门头大样图 1:100

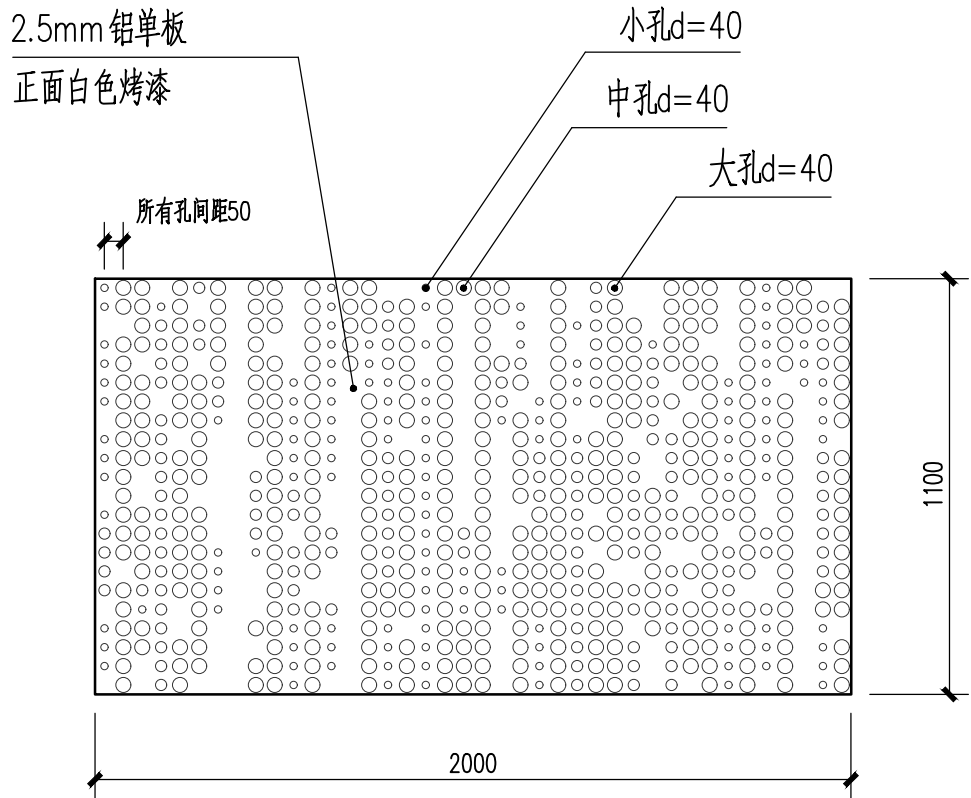

② 西入口门头穿孔板样式图 1:20

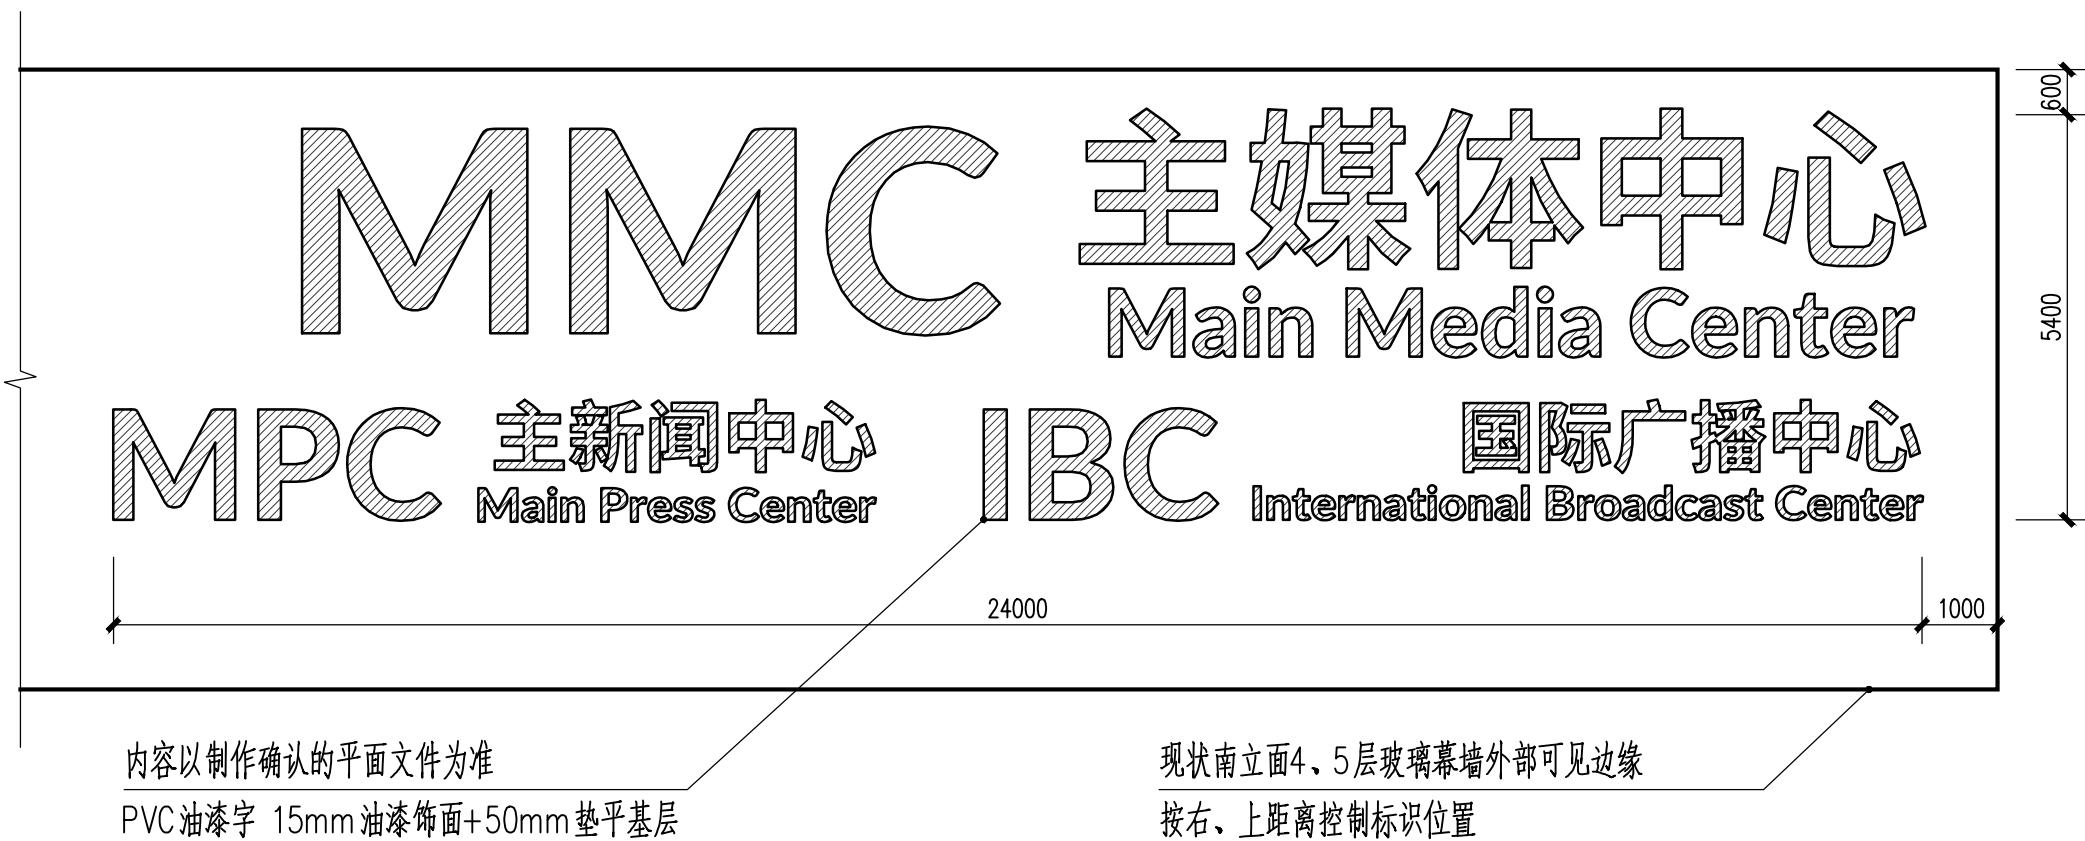

③ 南立面标识立面图 1:100

出图记录		ISSUE NOTES
版 本	日 期	备 注
REV.	DATE	REMARK
A	2022.02	
注册执业栏		REGISTERED ARCHITECT/ENGINEER
姓 名		NAME
注册证书号码		REGISTRATION CERTIFICATE NO.
注册印章号码		STAMP NO.
设计号: CD-20212856-F001		JOB NO.
工程名称		PROJECT TITLE
成都大运会主新闻中心装饰搭建		
子项名称		SUB ITEM
建设单位		CLIENT
成都博雅文瑞文化传播有限公司		
图 名		DRAWING TITLE
西入口门头、南立面标识大样图		
单 位	mm	UNIT
图 别	室 施	DWG. CATEGORY
比 例	—	SCALE
图 号	D02	DWG. NO.
日 期	2022.02	DATE
版 本	A	VER. NO.
制 图	张 丽	
设 计	肖子颖	
校 对	李 肅文	
专业负责人	肖子颖	
DISCIPLINE CHIEF		
设计总负责人	张 峻	
PROJECT CHIEF		
审 核	张 峻	
AUDIT		
审 定	华 柯	
APPROVED BY		
国 基准方中		
成都基准方中建筑设计股份有限公司		
Chengdu JZfZ Architectural Design Co., Ltd.		
中国 成都市 琉璃路8号华润广场A座7-15楼		
电话: +86(28) 86333800 传真: +86(28) 86582990		
7-15F, Tower A, Grand Plaza, No.8, Liuli Road, Chengdu, P.R.C		
tel. +86(28) 86333800 fax. +86(28) 86582990		
工程设计资质证书编号: A151016191		
电子文档编号: —		CAD FILENAME
版 权 说 明		
COPYRIGHT DECLARATION		
此图版权为成都基准方中建筑设计股份有限公司所有, 未经许可不得使用。		