




采暖通风					
总图					

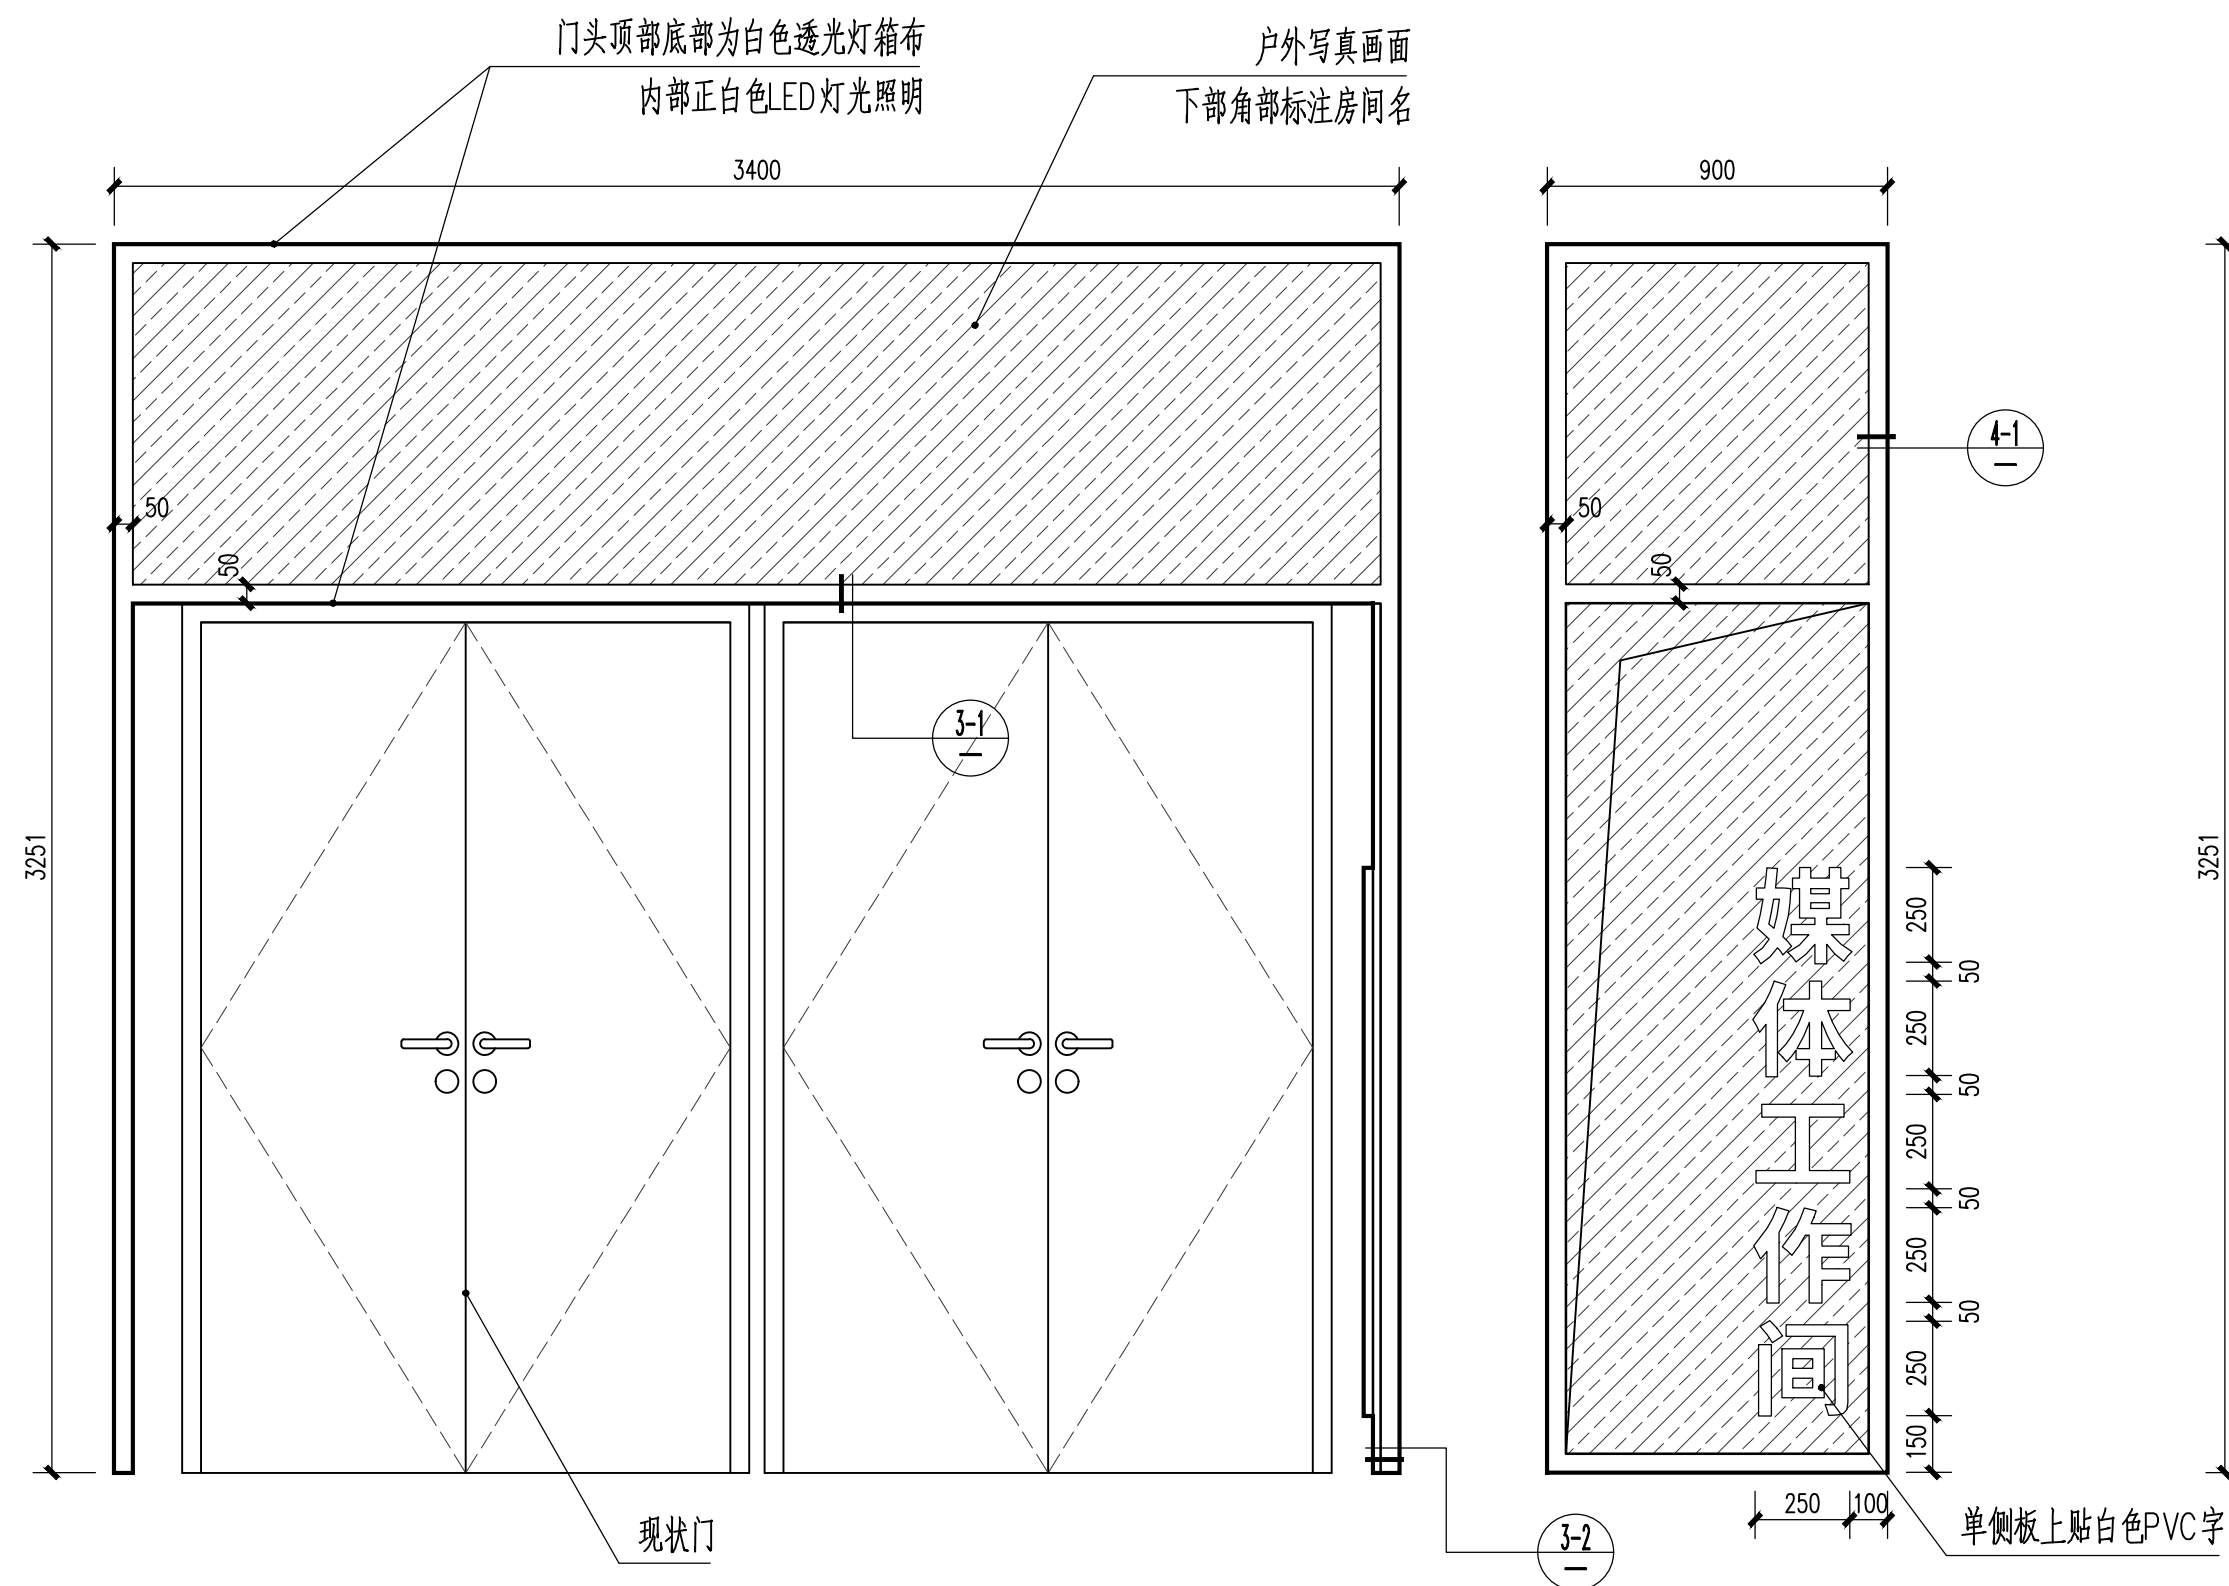


① 门框(大)正、侧立面图 1:20

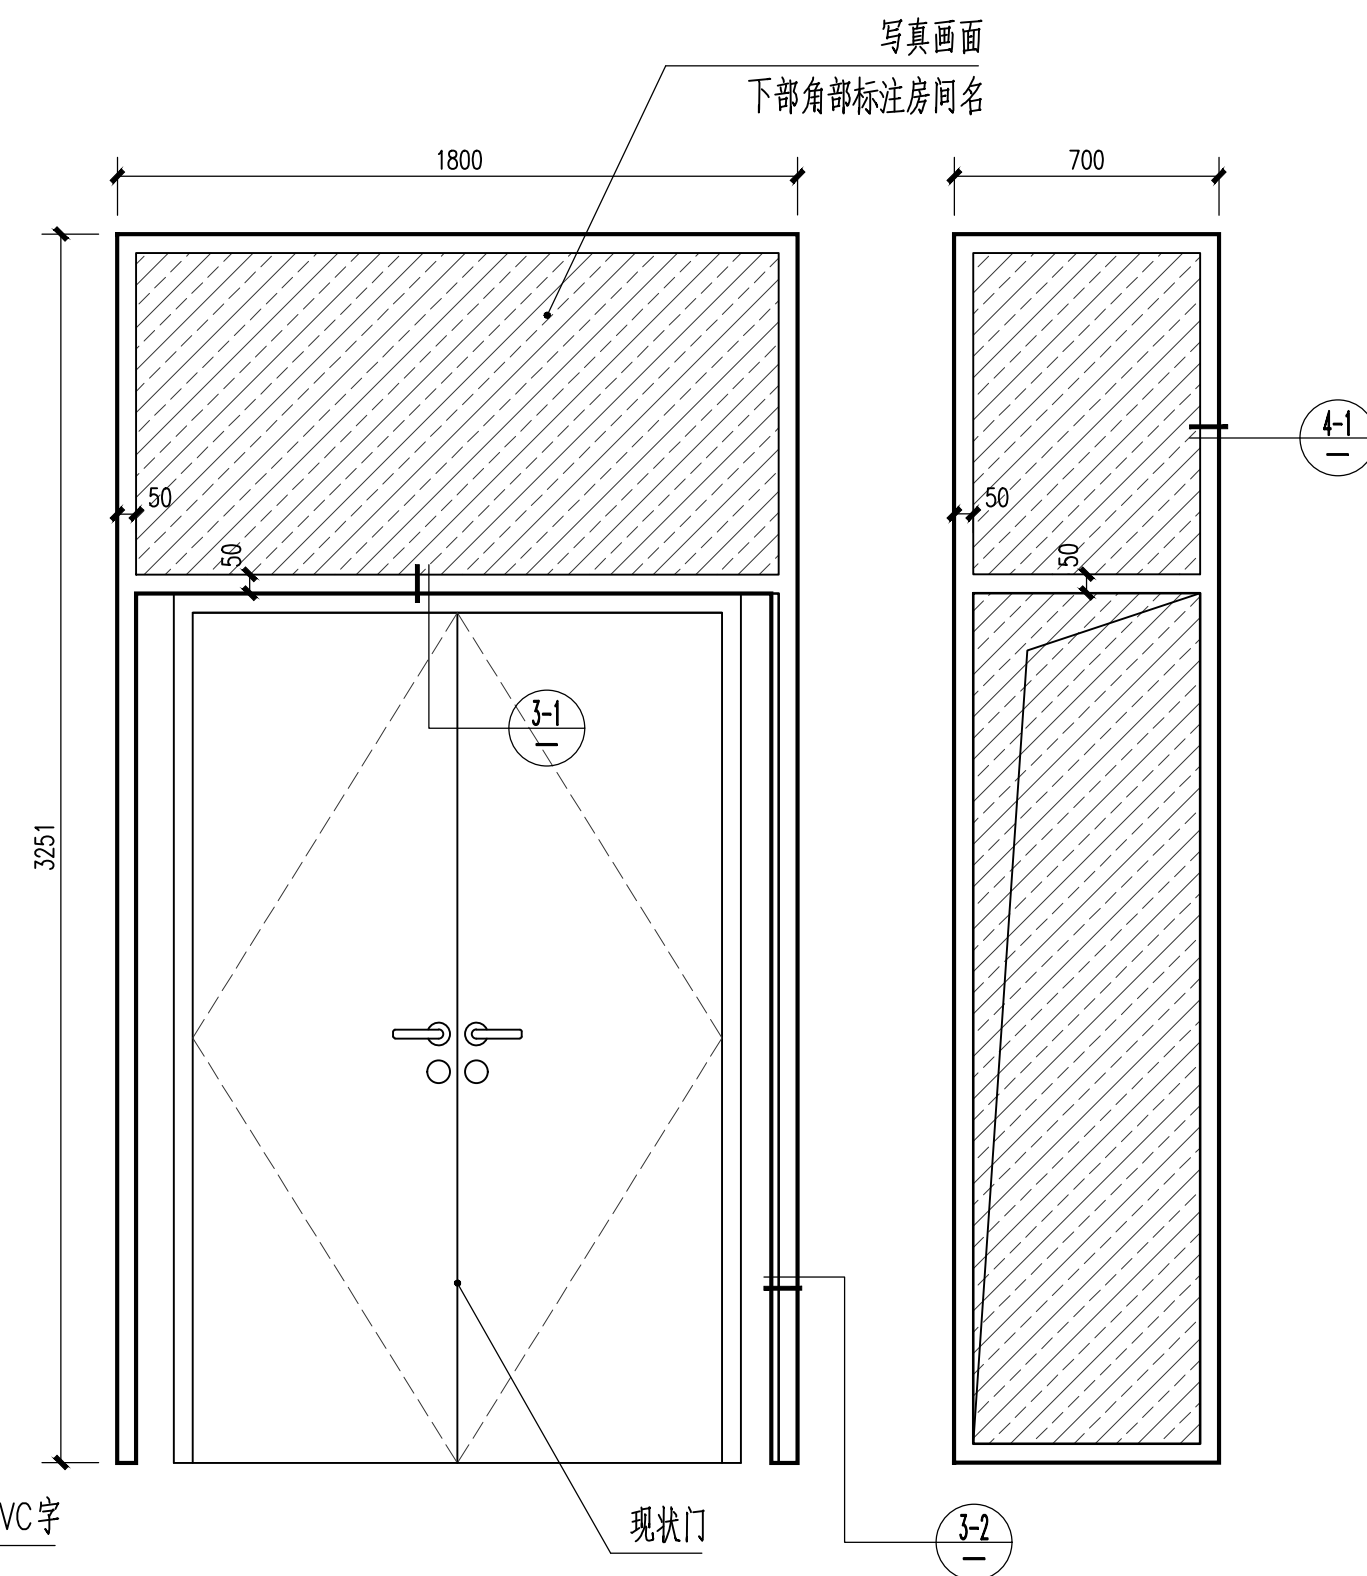

② 门框(小)正、侧立面图 1:20

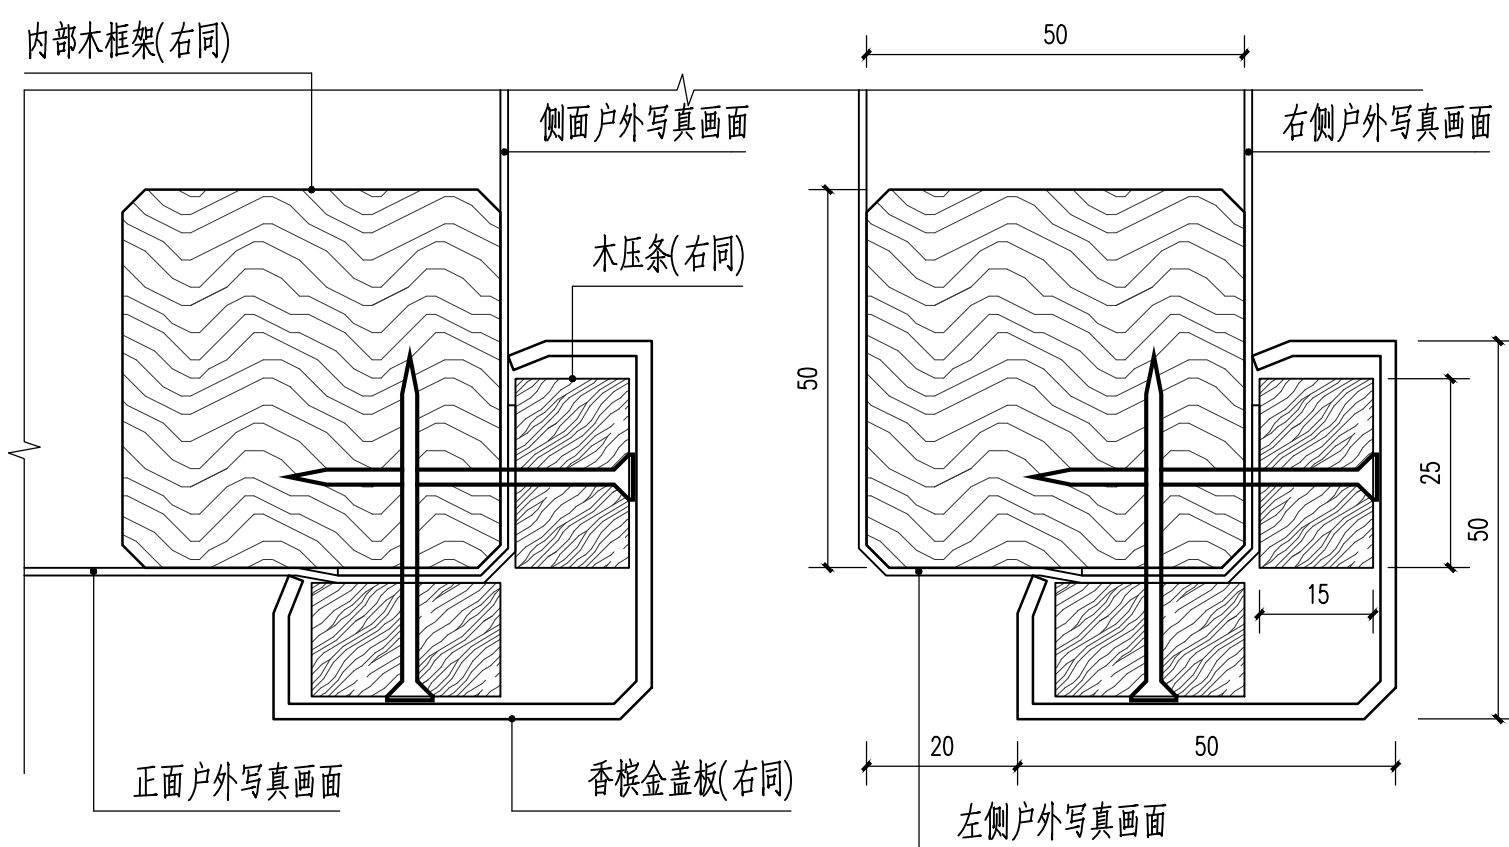

③-1 门框边框(角部)大样图 1:1 ③-2 门框边框(端部)大样图 1:1

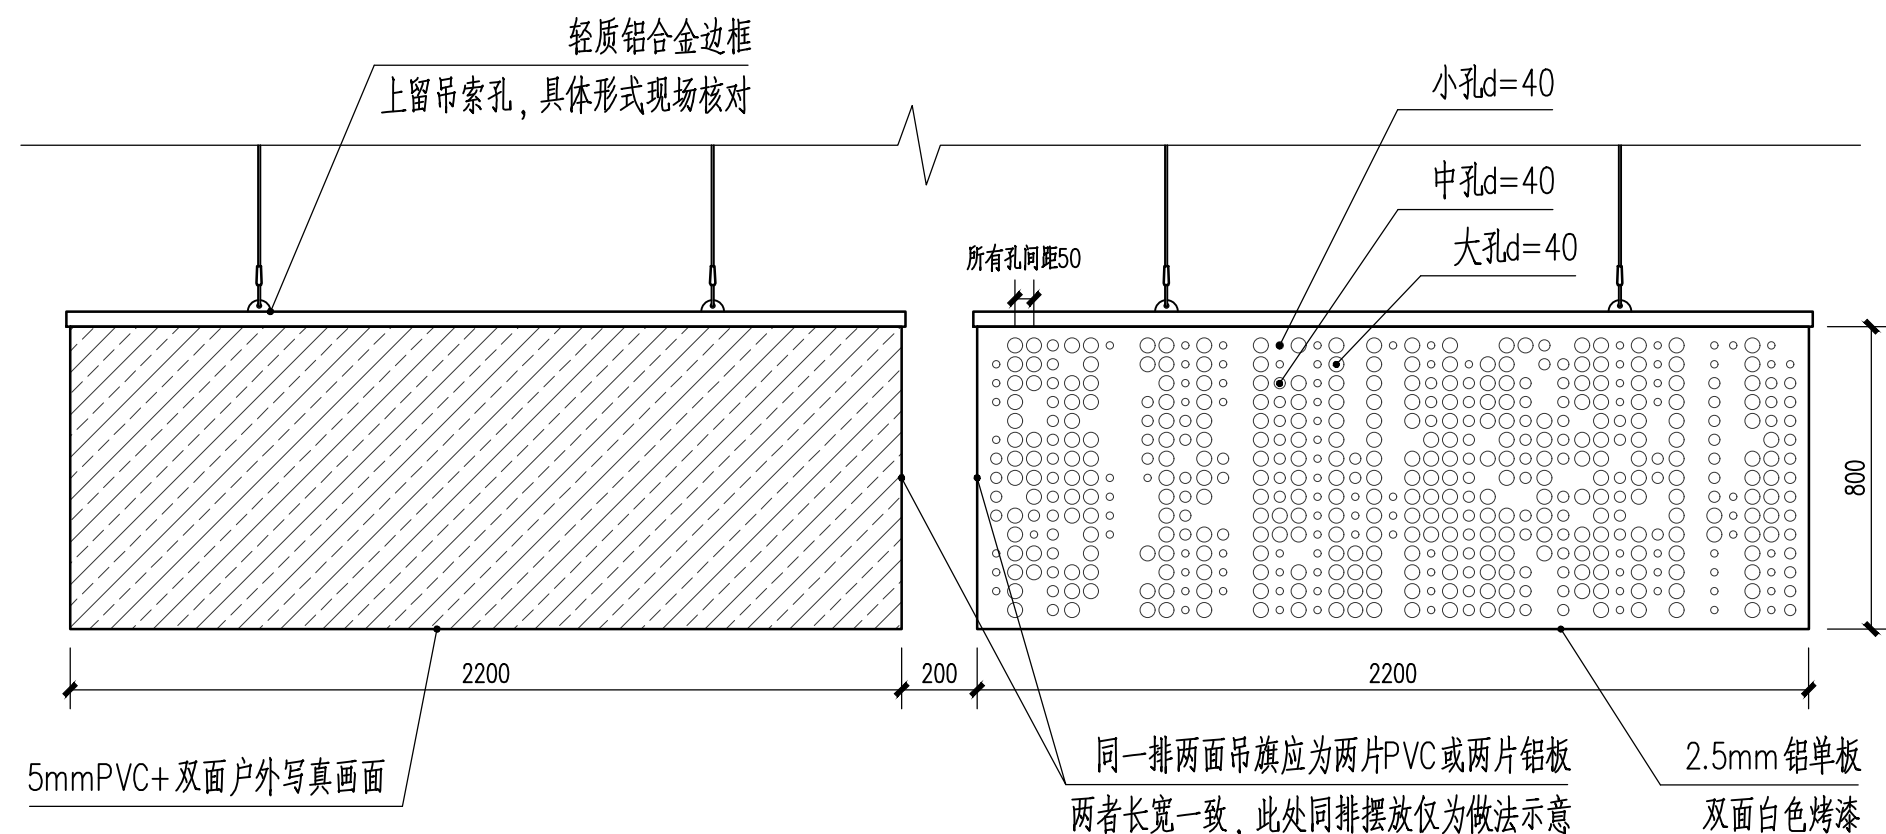

④ 吊旗大样图 1:20

出图记录			ISSUE NOTES		
版 本 REV.	日 期 DATE	备 注 REMARK			
A	2022.02				
注册执业栏 REGISTERED ARCHITECT/ENGINEER					
姓 名					NAME
注册证书号码					REGISTRATION CERTIFICATE NO.
注册印章号码					STAMP NO.
设计号：CD-20212856-F001					JOB NO.
工程名称					PROJECT TITLE
成都大运会主新闻中心装饰搭建					
子项名称					SUB ITEM
建设单位					
成都博雅文瑞文化传播有限公司					
图 名					DRAWING TITLE
西入口通道与发布厅外侧通道 门框大样图、吊旗大样图					
单 位： mm	UNIT	图 别	室 施	DWG. CATEGORY	
比 例 —	SCALE	图 号：	D03	DWG. NO.	
日 期 2022.02	DATE	版 本	A	VER. NO.	
制 图 DRAWN BY	雷鑫鹏				
设 计 DESIGNED BY	肖子颖				
校 对 CHECKED BY	李耀文				
专业负责人 DISCIPLINE CHIEF	肖子颖				
设计总负责人 PROJECT CHIEF	张竣				
审 核 AUDIT	张竣				
审 定 APPROVED BY	华柯				
成都基准方中建筑设计股份有限公司 Chengdu JZFY Architectural Design Co., Ltd. 中国 成都市 琉璃路8号华润广场A座7-15楼 电话：+86(28) 86333800 传真：+86(28) 86582990 7-15F, Tower A, Criland Plaza, No.8Jinhu Road , Chengdu, P.R.C tel. +86(28) 86333800 fax. +86(28) 86582990 工程设计资质证书编号： A151016191 CAD FILENAME 电子档编号： — 版 权 说 明 COPYRIGHT DECLARATION 此图版权为成都基准方中建筑设计股份有限公司所有，未经许可不得使用。					