

白色pvc板A，共28个
宽1600，高1200，12厚，间隔200

白色pvc板，贴画面，共31个
宽1100，高1000,8厚，间隔150

深灰亚克力灯箱
长2900，高960，宽1290

无色半透明亚克力板，共28个
宽2440，高840,8厚，间隔200

白色pvc板B，共21个
宽2440，高330,12厚，间隔250

印刷标识文字
按照标准字体
蓝色亚克力灯箱
长2440，高600，宽1000



大运会KV喷绘布

白色漆面


蓝色印刷标识文字
按照标准字体

印刷标识文字
按照标准字体


时钟，共5个
半径200

白色书架，亚克力背板，共13列，4排
宽400，高2500，左右间隔240，上下间隔550


西服务台效果图

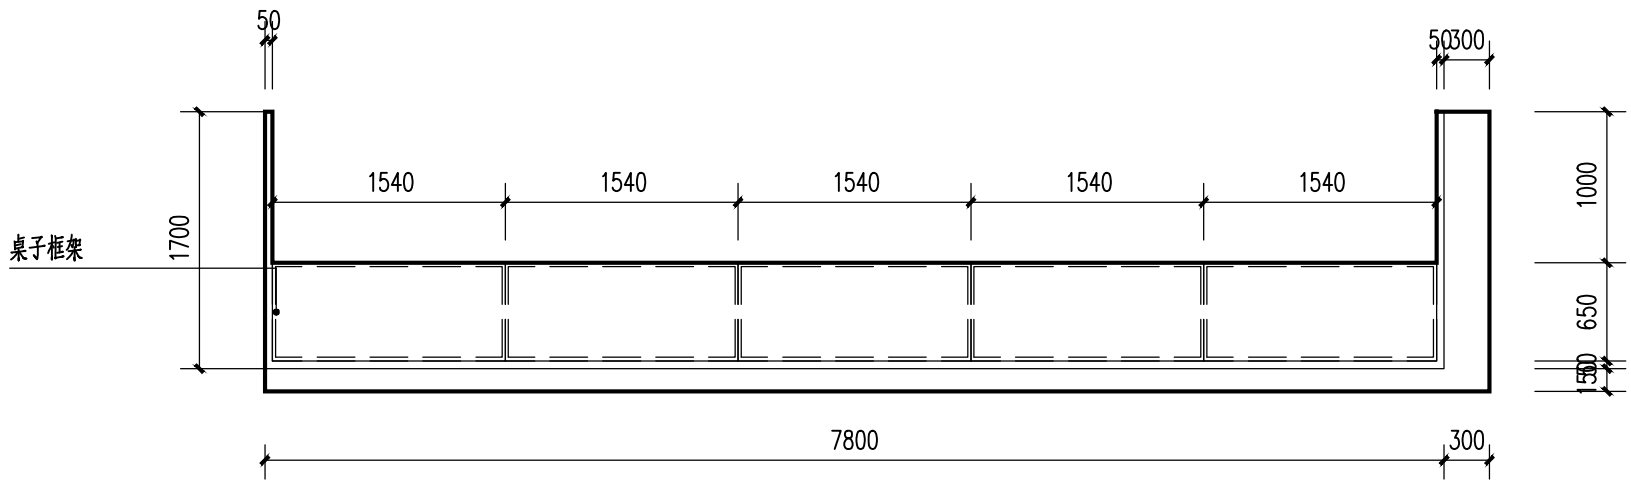


西服务台 顶视图 1:50

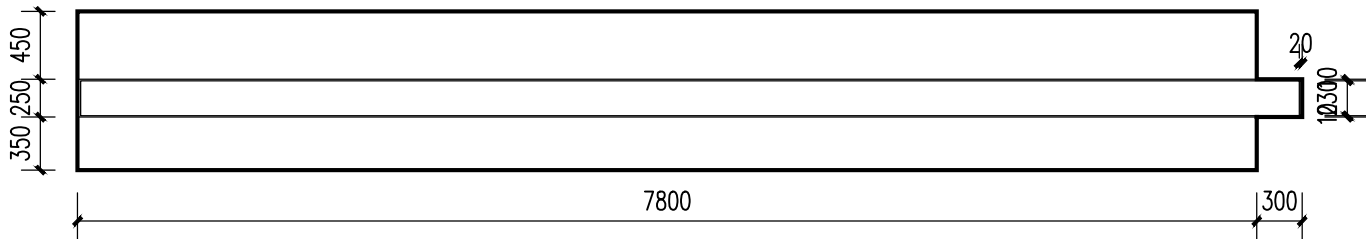

西服务台 前视图 1:50

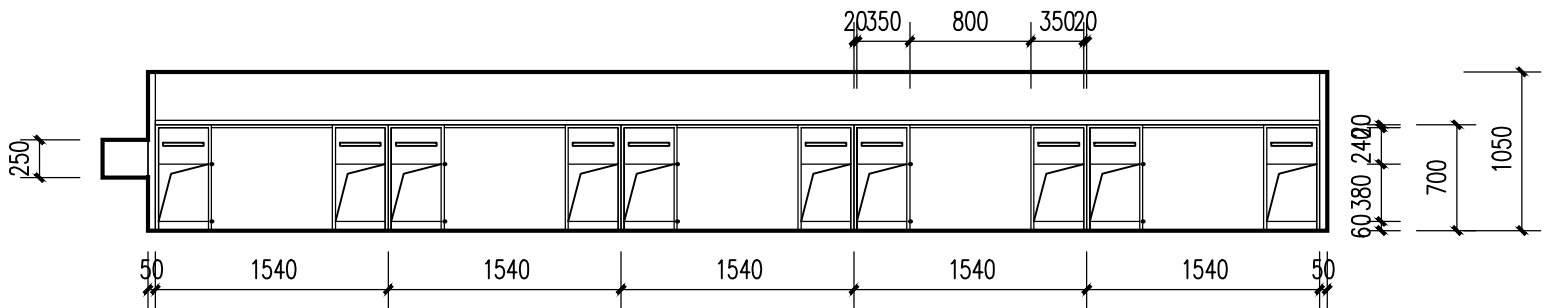

西服务台 后视图 1:50

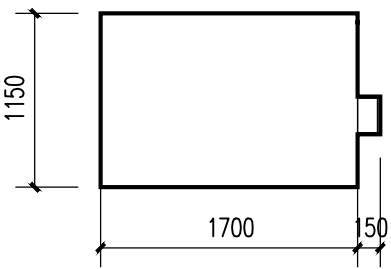

西服务台 侧视图 1:50

西服务台大样图 1:50

出图记录		ISSUE NOTES
版本	日期	备注
REV.	DATE	REMARK
A	2022.02	
注册执业栏		REGISTERED ARCHITECT/ENGINEER
姓名		NAME
注册证书号码		REGISTRATION CERTIFICATE NO.
注册印章号码		STAMP NO.
设计号		JOB NO.
工程名称		PROJECT TITLE
子项名称		SUB ITEM
建设单位		CLIENT
成都博雅文瑞文化传播有限公司		
图名		DRAWING TITLE
西服务台大样图		
单位	mm	UNIT
图别	室施	DWG. CATEGORY
比例	1:50	SCALE
图号	D06	DWG. NO.
日期	2022.02	DATE
版本	A	VER. NO.
制图	雷鑫鹏	
设计	肖子颖	
校对	李肅文	
专业负责人	肖子颖	
设计总负责人	张峻	
审核	张峻	
审定	华柯	
基准方中		
成都基准方中建筑设计股份有限公司		
Chengdu JZfZ Architectural Design Co., Ltd.		
中国 成都市 琉璃路8号华润广场A座7-15楼		
电话: +86 (28) 86333800 传真: +86 (28) 86582990		
7-15F, Tower A, Grand Plaza, No.8, Liuli Road, Chengdu, P.R.C		
tel. +86(28) 86333800 fax. +86(28) 86582990		
工程设计资质证书编号: A151016191		
电子文档编号: -		
CAD FILENAME		
版权说明		
COPYRIGHT DECLARATION		
此图版权为成都基准方中建筑设计股份有限公司所有，未经许可不得使用。		