

白色pvc板A, 共23个
宽1600, 高1050, 12厚, 间隔200

白色pvc板, 贴画面, 共18个
宽1120, 高900, 8厚, 间隔280

无色半透明亚克力板, 共23个
宽3400, 高500, 8厚, 间隔200

白色pvc板C, 共17个
宽2440, 高270, 12厚, 间隔250



南服务台效果图

木色免漆板

大运会KV喷绘布

白色漆面

深灰色亚克力灯箱

长2900, 高690, 宽1290


蓉宝立体吉祥物

蓝色亚克力灯箱


长2400, 高600, 宽1080

白色书架, 亚克力背板, 共21列, 3排


宽400, 高2300, 左右间隔210, 上下间隔590

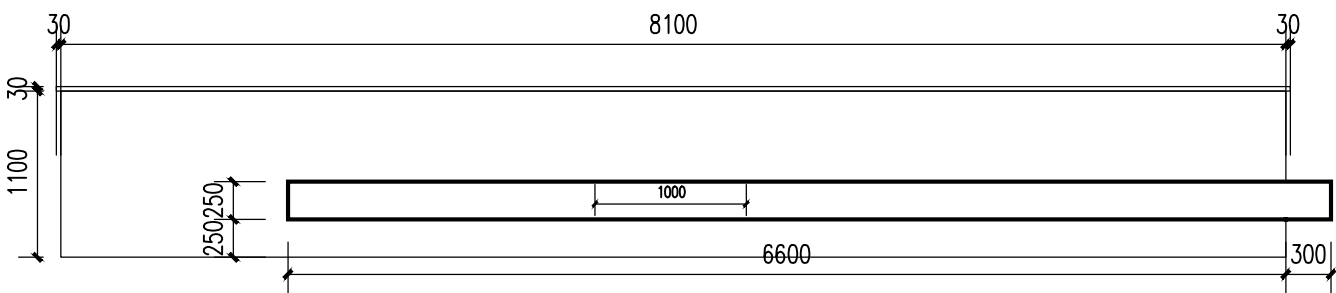


南欢迎台 前视图 1:50

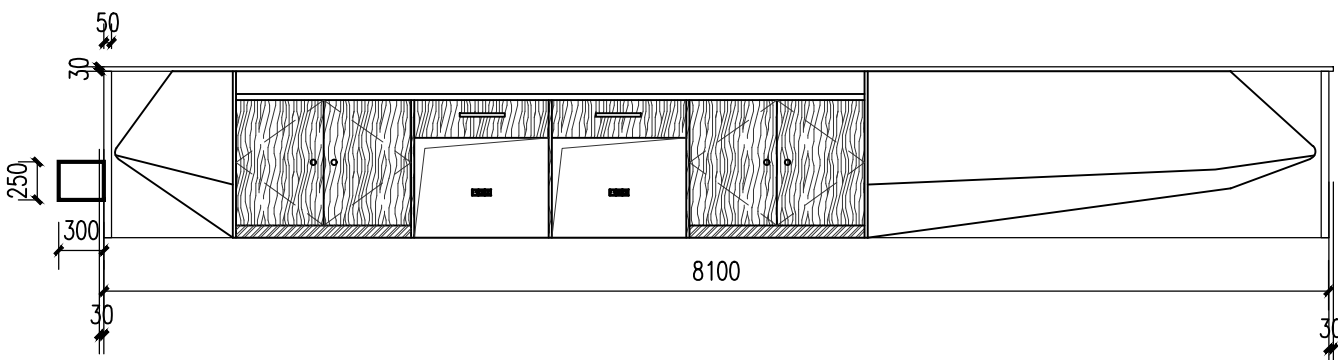

南欢迎台 后视图 1:50

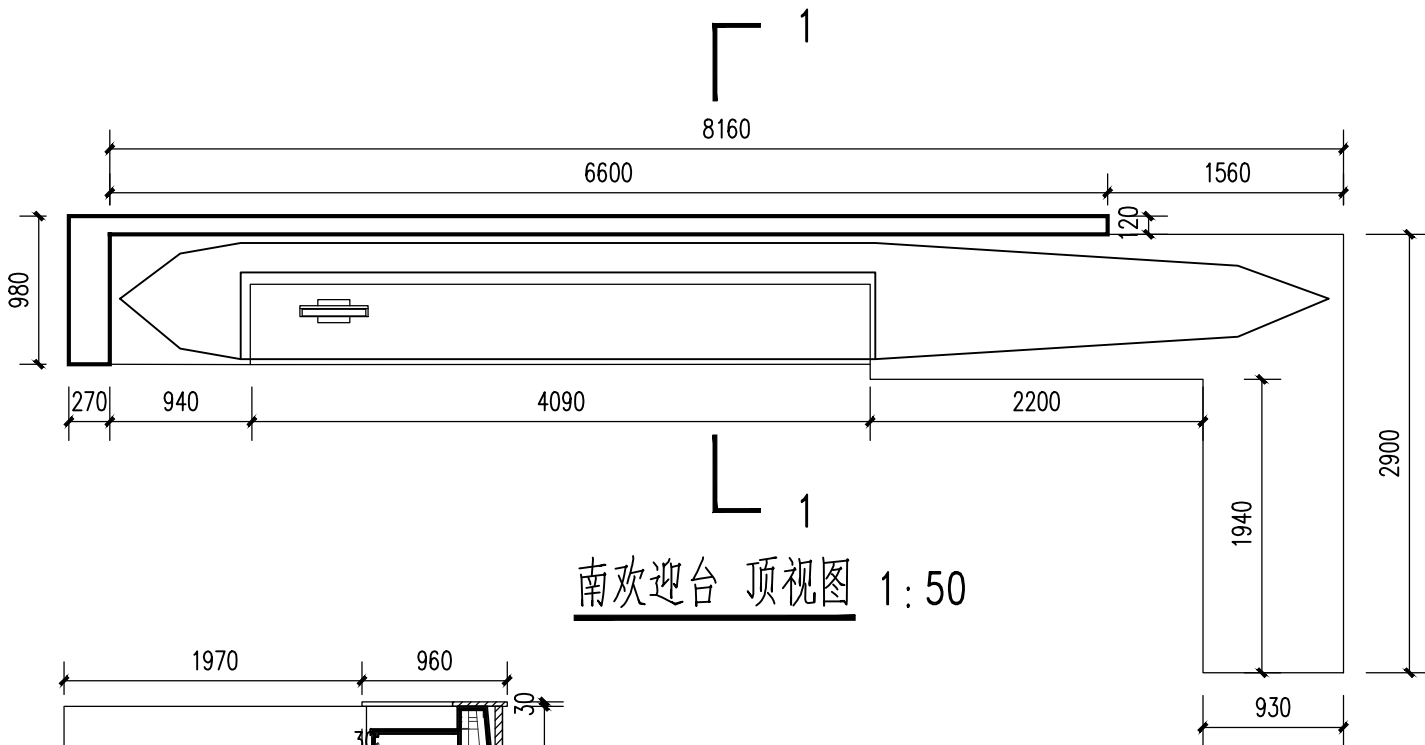

南欢迎台 顶视图 1:50

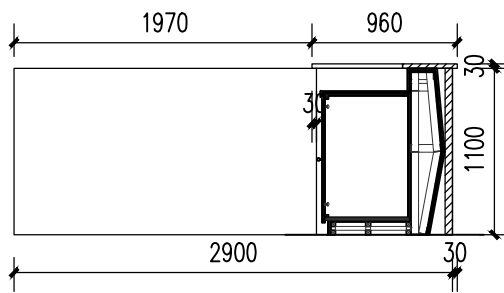

南欢迎台 1-1剖视图 1:50

南服务台大样图 1:50

出图记录		ISSUE NOTES
版 本	日 期	备 注
REV.	DATE	REMARK
A	2022.02	
注册执业栏		REGISTERED ARCHITECT/ENGINEER
姓 名		NAME
注册证书号码		REGISTRATION CERTIFICATE NO.
注册印章号码		STAMP NO.
设计号: CD-20212856-F001		JOB NO.
工程名称		PROJECT TITLE
成都大运会主新闻中心装饰搭建		
子项名称		SUB ITEM
建设单位		CLIENT
成都博雅文瑞文化传播有限公司		
图 名		DRAWING TITLE
南服务台大样图		
单 位	mm	UNIT
图 别	室 施	DWG. CATEGORY
比 例	1:50	SCALE
图 号	D07	DWG. NO.
日 期	2022.02	DATE
版 本	A	VER. NO.
制 图	雷鑫鹏	
设 计	肖子颖	
校 对	李肅文	
专业负责人	肖子颖	
DISCIPLINE CHIEF		
设计总负责人	张峻	
PROJECT CHIEF		
审 核	张峻	
AUDIT		
审 定	华柯	
APPROVED BY		
基准方中		
成都基准方中建筑设计股份有限公司		
Chengdu JZfZ Architectural Design Co., Ltd.		
中国 成都市 琉璃路8号华润广场A座7-15楼		
电话: +86(28) 86333800 传真: +86(28) 86582990		
7-15F, Tower A, Crtand Plaza, No.8, Liuli Road, Chengdu, P.R.C		
tel. +86(28) 86333800 fax. +86(28) 86582990		
工程设计资质证书编号: A151016191		
电子文档编号: -		
CAD FILENAME		
版 权 说 明		
COPYRIGHT DECLARATION		
此图版权为成都基准方中建筑设计股份有限		
公司所有, 未经许可不得使用。		