




服务台A 前视图 1:25

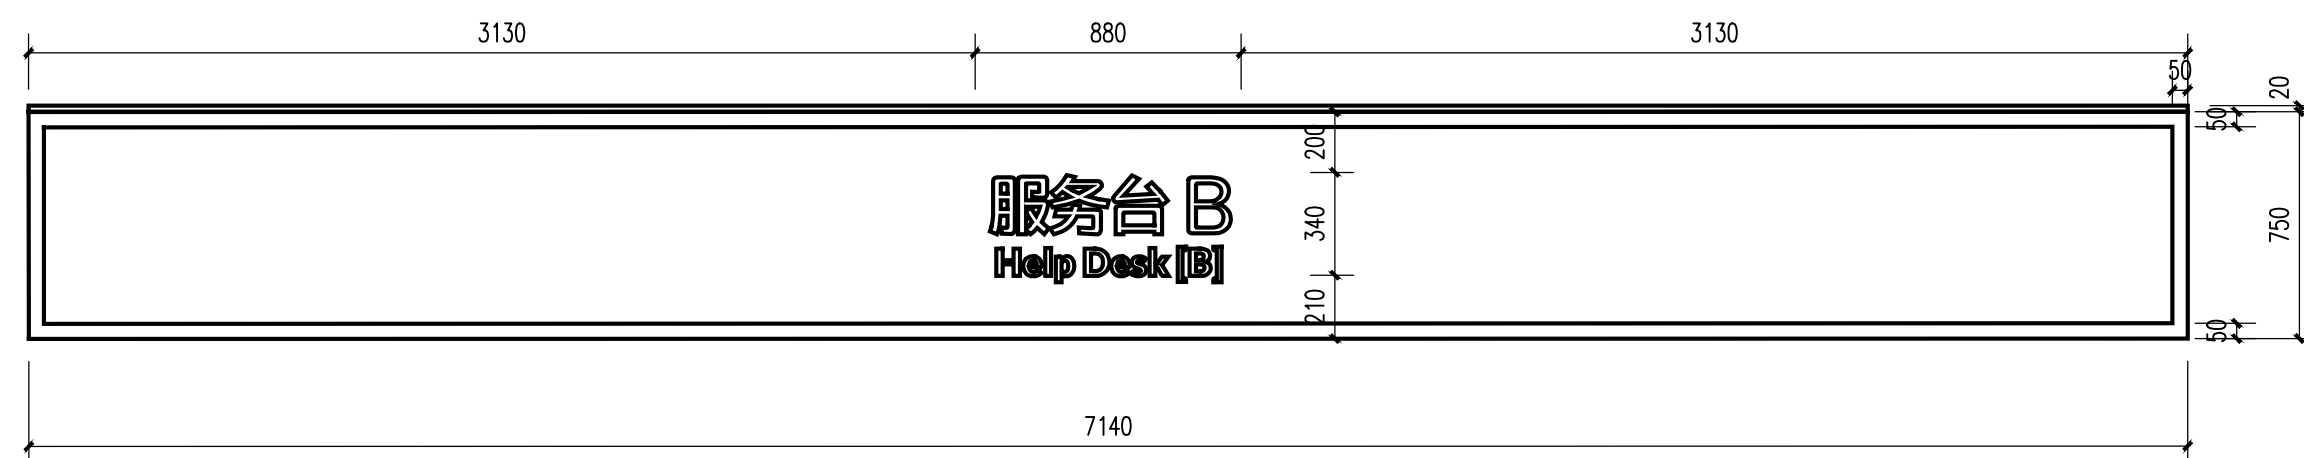


服务台B 前视图 1:25

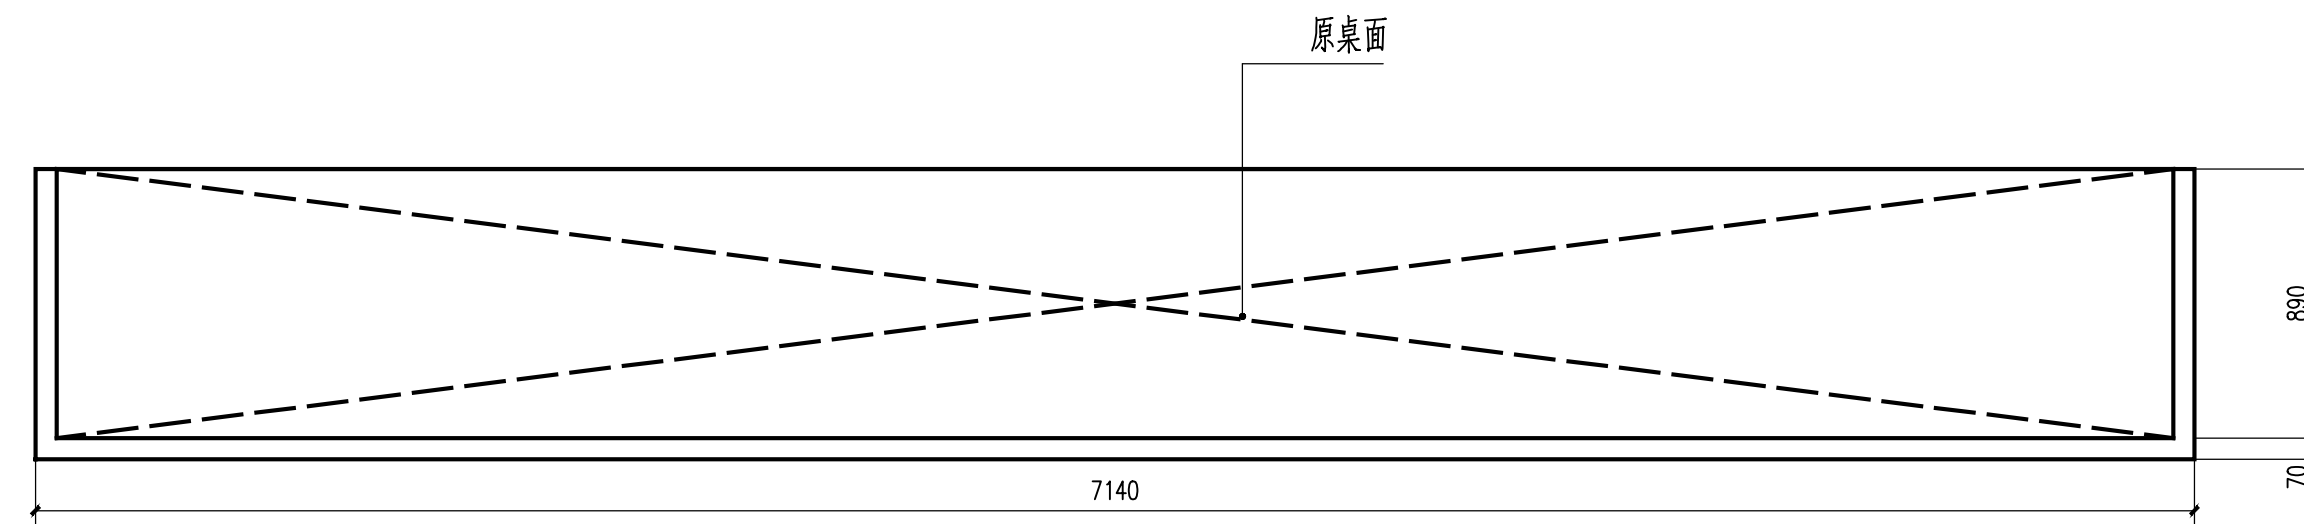


服务台AB 顶视图 1:25

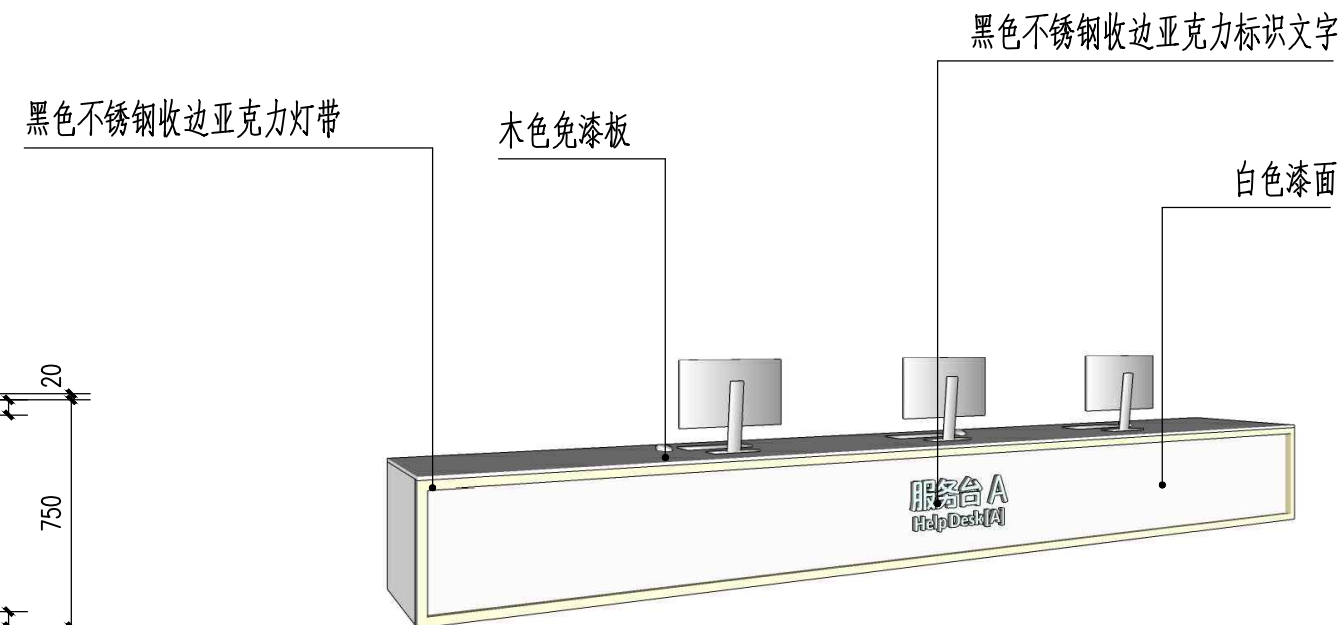

服务台A 效果图

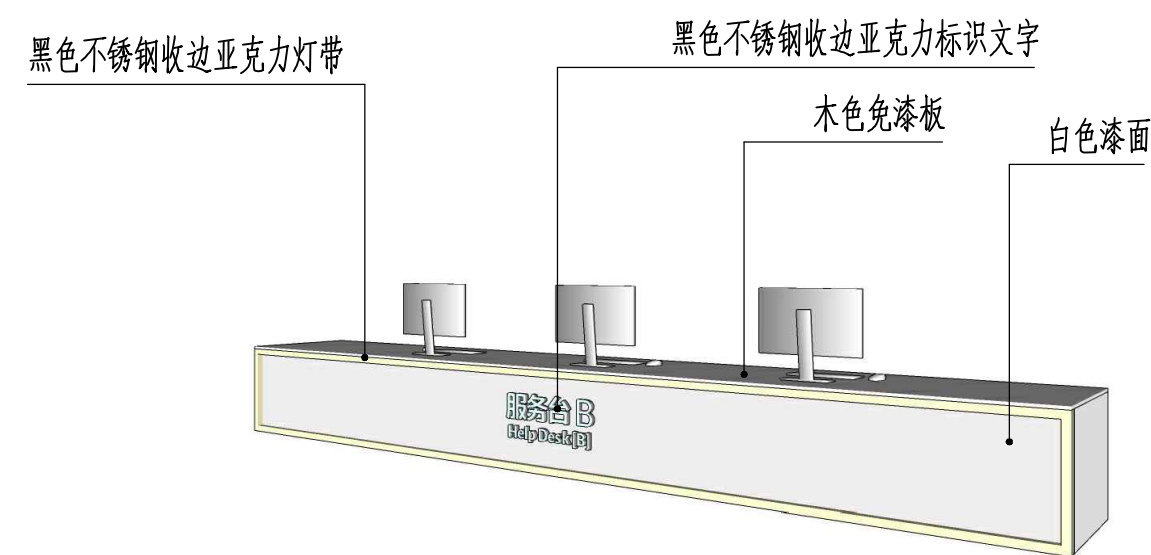

服务台B 效果图

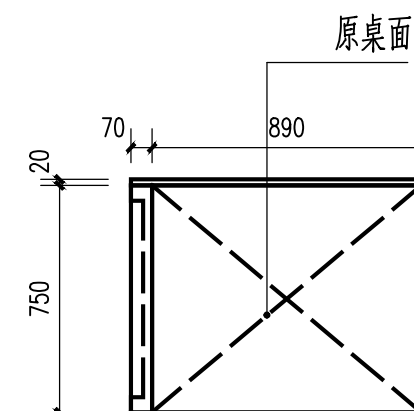

服务台AB 侧视图 1:25



出图记录			ISSUE NOTES	
版 本 REV.	日 期 DATE	备 注 REMARK		
A	2022.02			
注册执业栏 REGISTERED ARCHITECT/ENGINEER				
姓 名				NAME
注册证书号码				REGISTRATION CERTIFICATE NO.
注册印章号码				STAMP NO.
设计号: CD-20212856-F001				JOB NO.
工程名称				PROJECT TITLE
成都大运会主新闻中心装饰搭建				
子项名称				SUB ITEM
建设单位				CLIENT
成都博雅文瑞文化传播有限公司				
图 名				DRAWING TITLE
服务台A、B大样图				
单 位 mm	UNIT	图 别	室 施	DWG. CATEGORY
比 例 1:25	SCALE	图 号 D08		DWG. NO.
日 期 2022.02	DATE	版 本 A		VER. NO.
制 图 DRAWN BY	雷鑫鹏			
设 计 DESIGNED BY	肖子颖			
校 对 CHECKED BY	李瀛文			
专业负责人 DISCIPLINE CHIEF	肖子颖			
设计总负责人 PROJECT CHIEF	张峻			
审 核 AUDIT	张峻			
审 定 APPROVED BY	华轲			
图 基 准 方 中 成都基准方中建筑设计股份有限公司 Chengdu JZfz Architectural Design Co., Ltd. 中国 成都市 琉璃路8号华润广场A座7-15楼 电话: +86(28) 86333800 传真: +86(28) 86582990 7-15F, Tower A, Criland Plaza, No.8, Liuli Road, Chengdu, P.R.C tel. +86(28) 86333800 fax. +86(28) 86582990 工程投资资质证书编号: A151016191 电子文档编号: - 版 权 说 明 COPYRIGHT DECLARATION 此图版权为成都基准方中建筑设计股份有限公司所有, 未经许可不得使用。				