




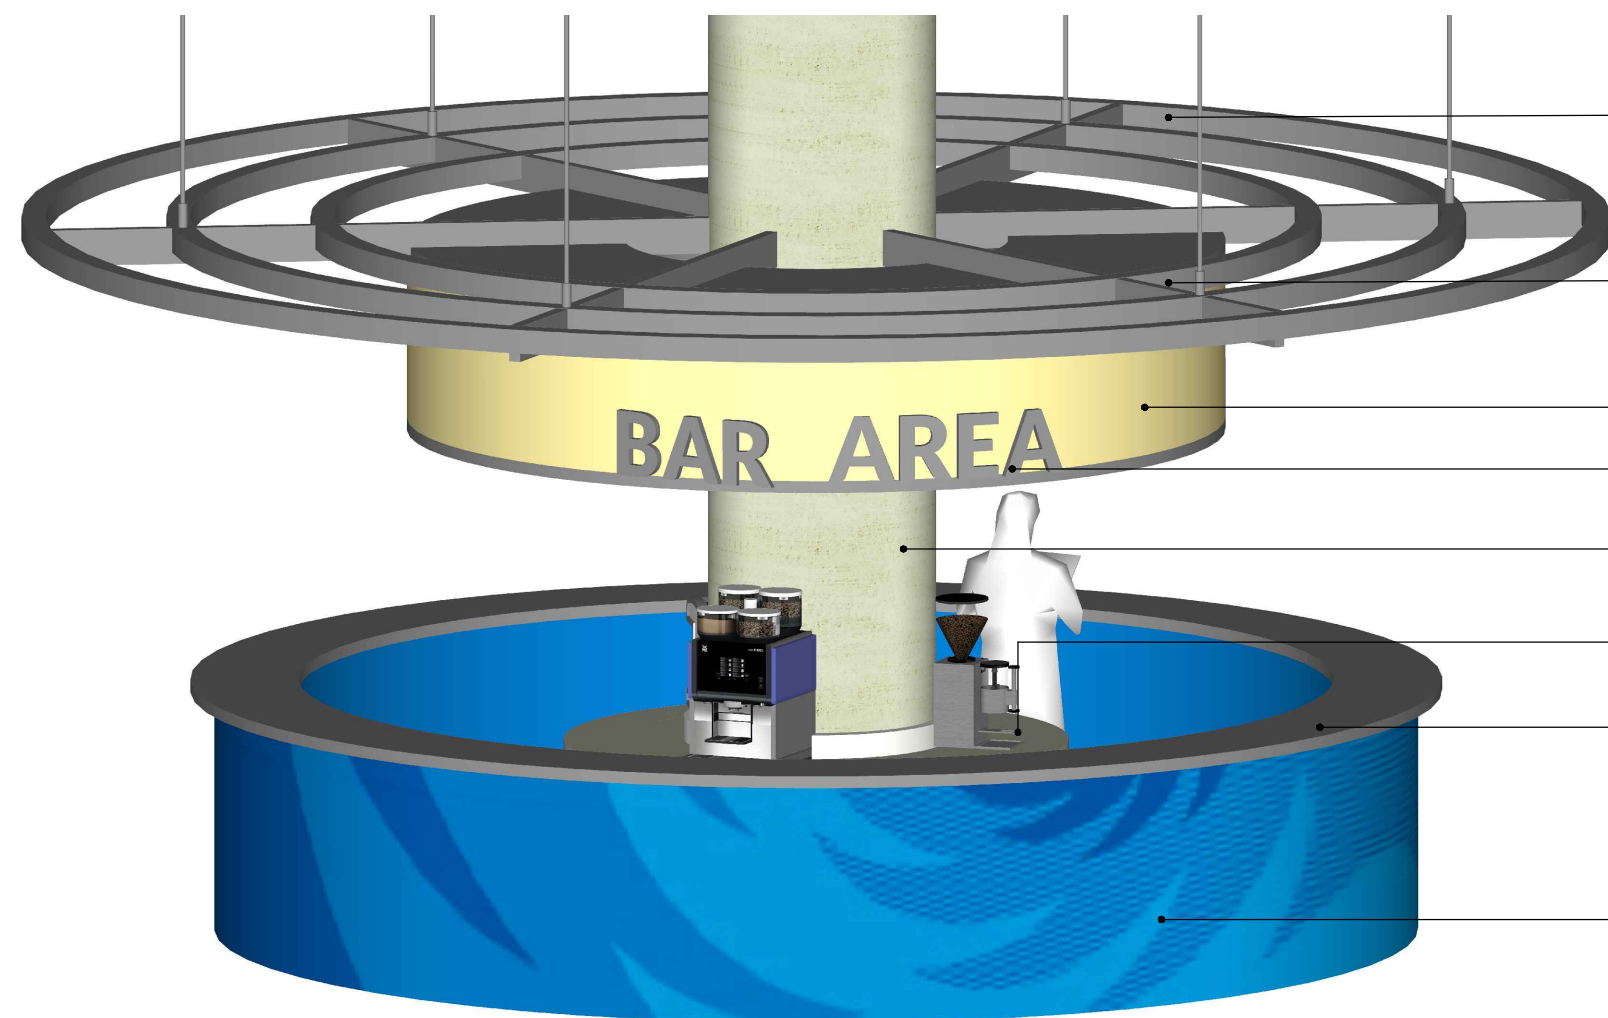



水吧效果图

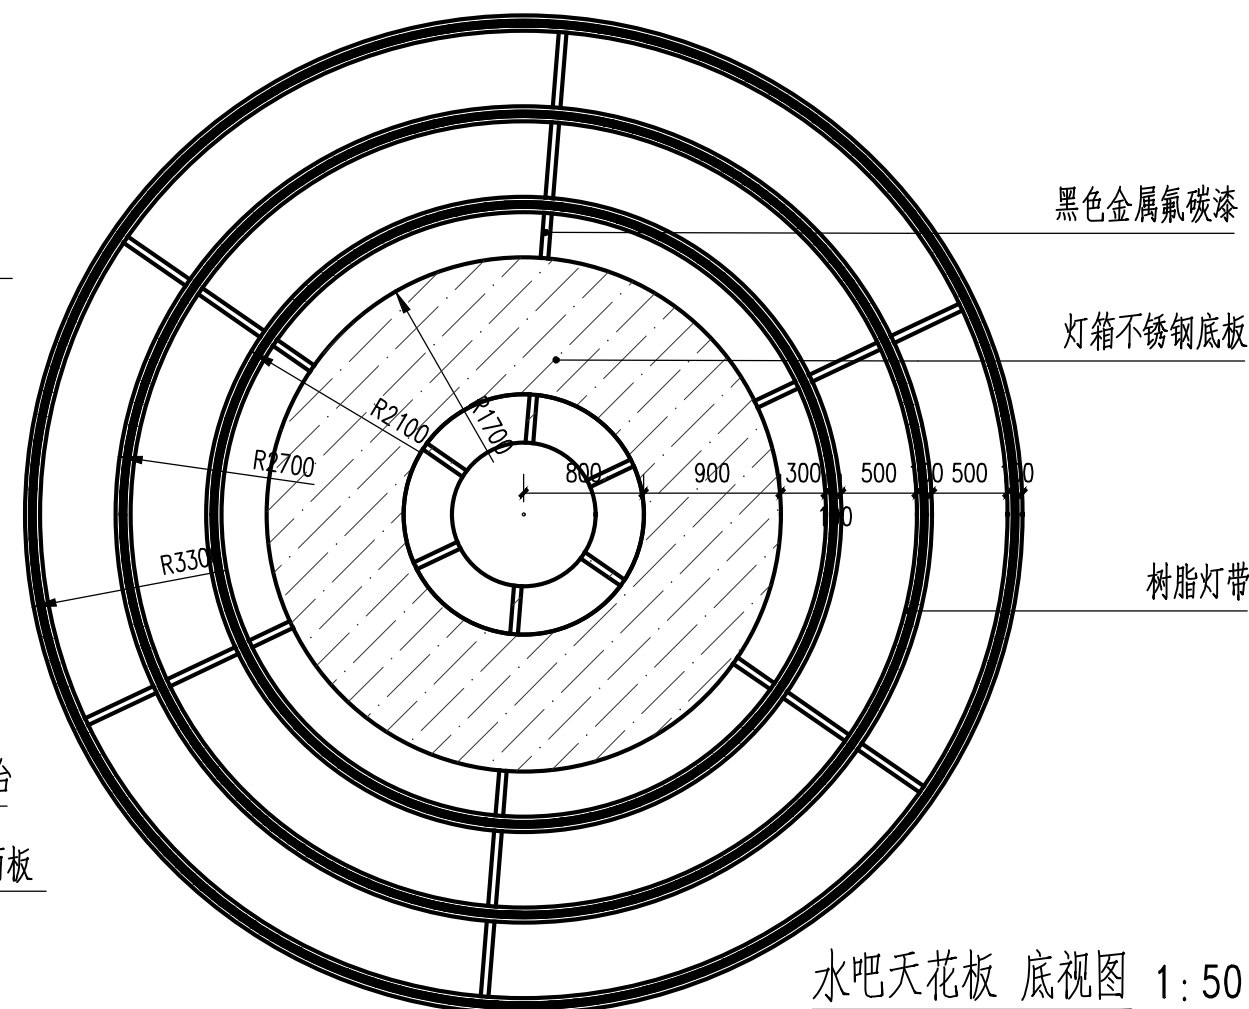


水吧天花板 底视图 1:50

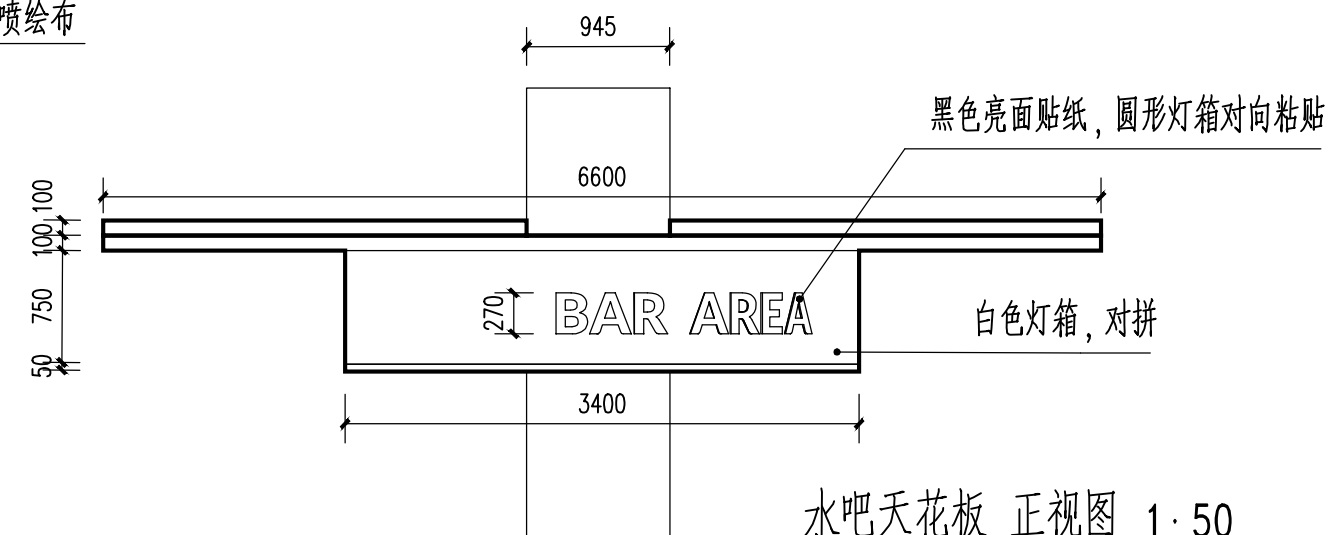


水吧天花板 正视图 1:50

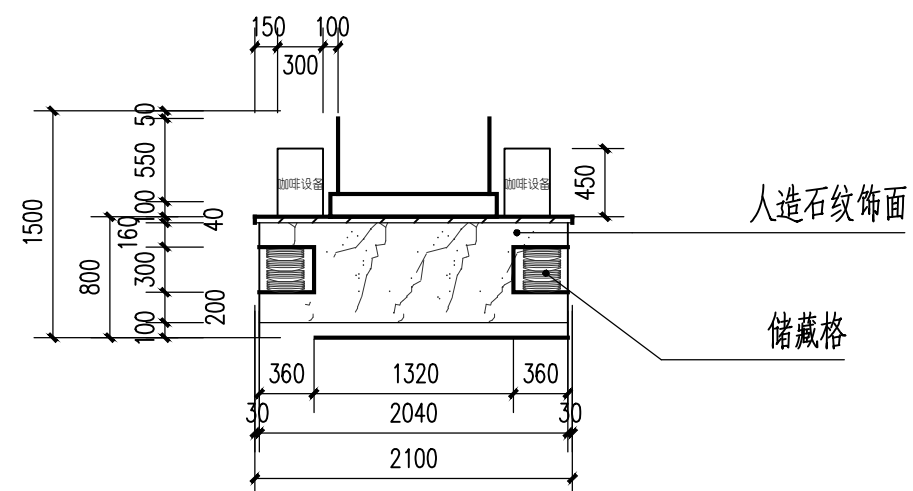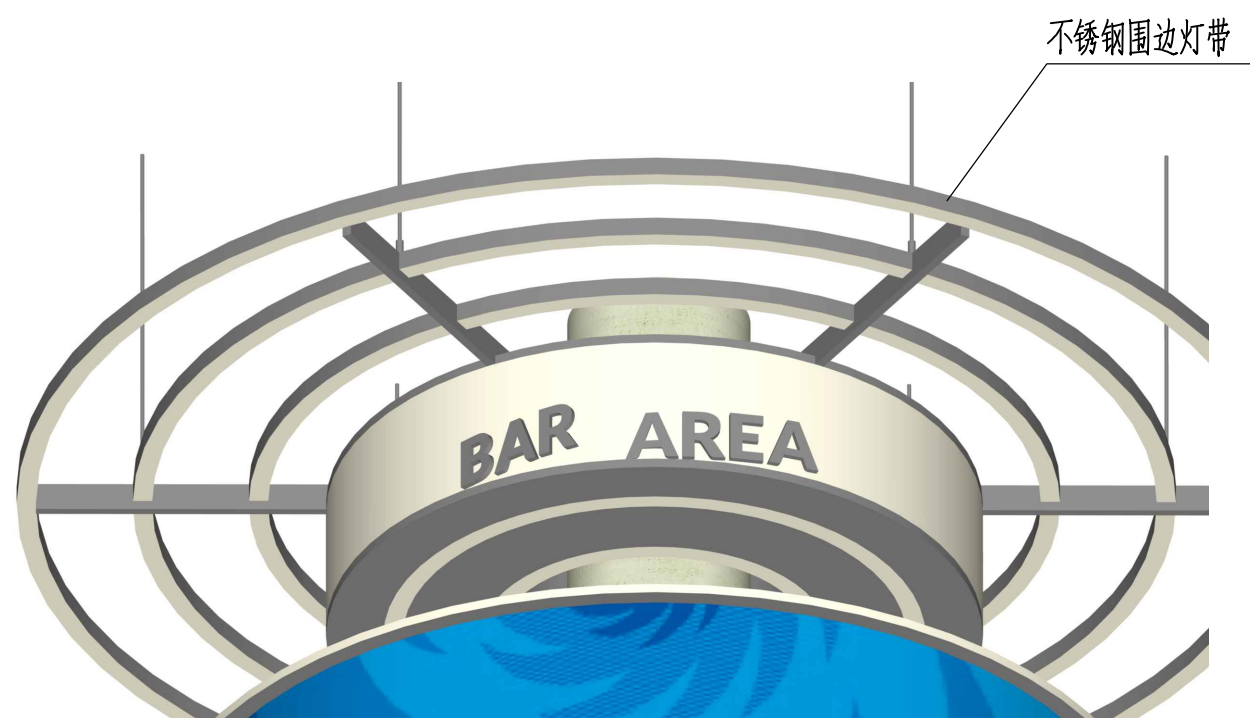


水吧内吧台 侧视图 1:50

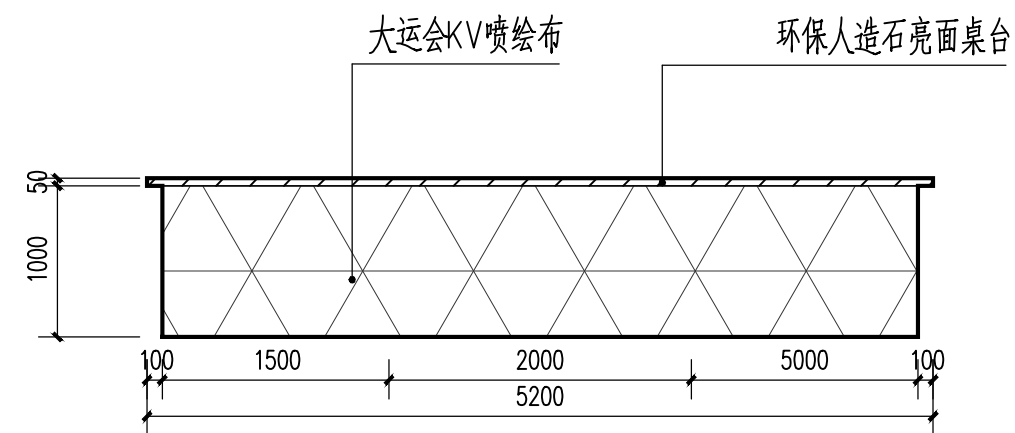

水吧外吧台 正视图 1:50

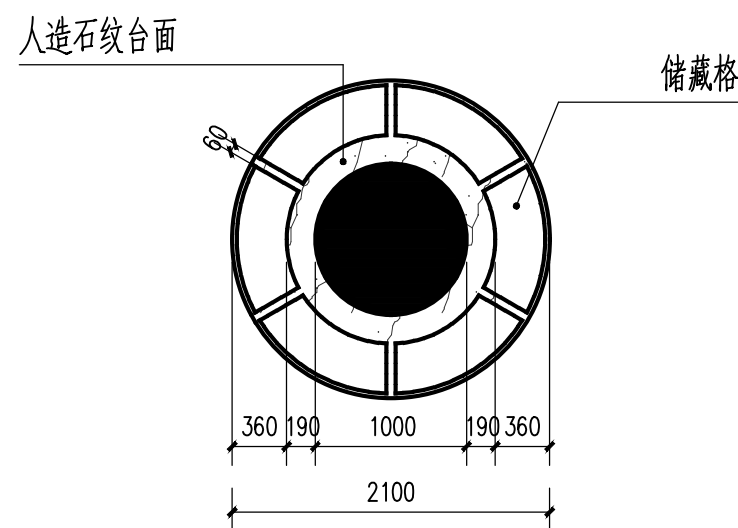

水吧内吧台 平面图 1:50

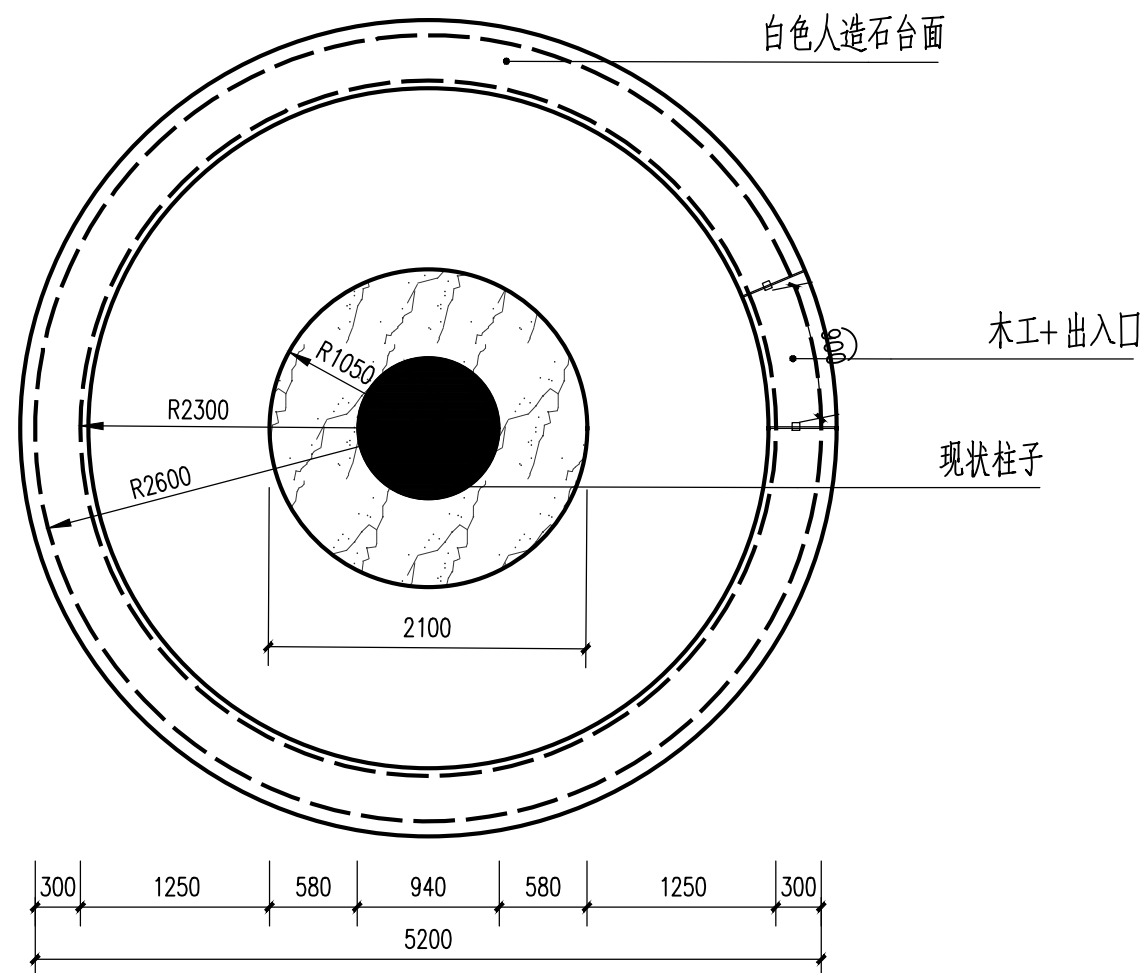

水吧 平面图 1:50

出图记录			ISSUE NOTES		
版 本 REV.	日 期 DATE	备 注 REMARK			
A	2022.02				
注册执业栏					
REGISTERED ARCHITECT/ENGINEER					
姓 名					NAME
注册证书号码					REGISTRATION CERTIFICATE NO.
注册印章号码					STAMP NO.
设计号: CD-20212856-F001					JOB NO.
工程名称					PROJECT TITLE
成都大运会主新闻中心装饰搭建					
子项名称					SUB ITEM
建设单位					CLIENT
成都博雅文瑞文化传播有限公司					
图 名					DRAWING TITLE
水吧大样图					
单 位	mm	UNIT	图 号	室 施	DWG. CATEGORY
比 例	1:50	SCALE	图 号	D09	DWG. NO.
日 期	2022.02	DATE	版 本	A	VER. NO.
制 图	罗 匀				
DESIGNED BY	肖子颖				
校 对	李 瀛 文				
CHECKED BY					
专业负责人	肖子颖				
DISCIPLINE CHIEF					
设计总负责人	张 峻				
PROJECT CHIEF					
审 核	张 峻				
AUDIT					
审 定	华 轲				
APPROVED BY					
成都基准方中建筑设计股份有限公司					
Chengdu JZfZ Architectural Design Co., Ltd.					
中国 成都市 琉璃路8号华润广场A座7-15楼					
电话: +86(28) 86333800 传真: +86(28) 86582990					
7-15F, Tower A, Criland Plaza, No.8, Liuli Road, Chengdu, P.R.C					
tel. +86(28) 86333800 fax. +86(28) 86582990					
工程投资资质证书编号: A151016191					
电子文档编号: -					CAD FILENAME
版 权 说 明					
COPYRIGHT DECLARATION					
此图版权为成都基准方中建筑设计股份有限公司所有, 未经许可不得使用。					