



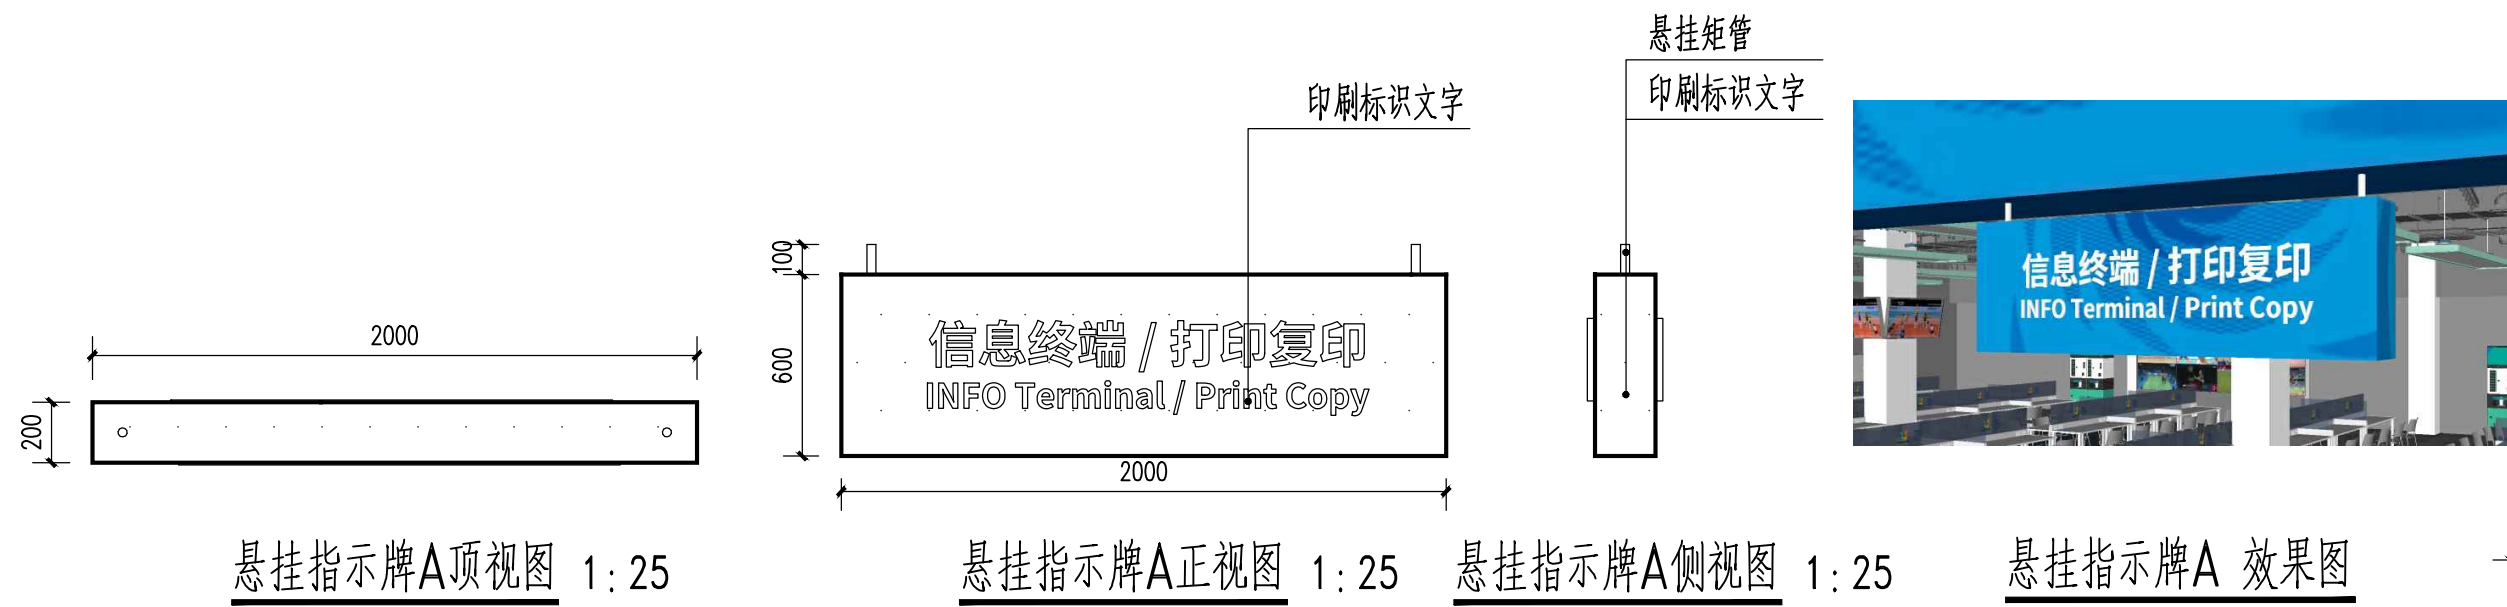

悬挂指示牌A正视图 1:25

悬挂指示牌A 效果图

① 悬挂指示牌A大样图 1:25

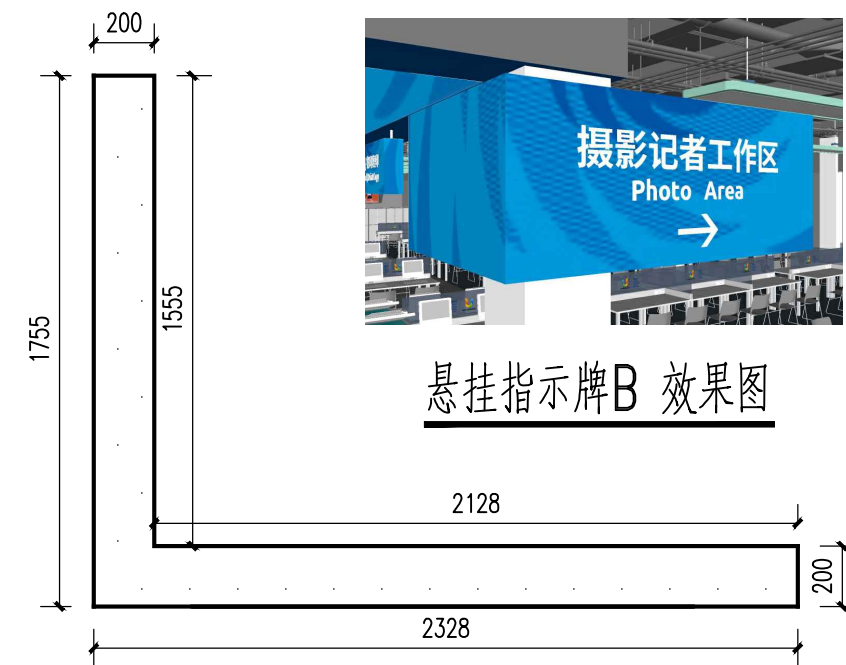

Technical drawing of a rectangular plate. The overall dimensions are 1000 mm (height) and 1355 mm (width). A vertical line is drawn 200 mm from the left edge. The area to the right of this line is divided into a grid of 10 columns and 10 rows by dashed lines.

② 悬挂指示牌B大样图 1:25

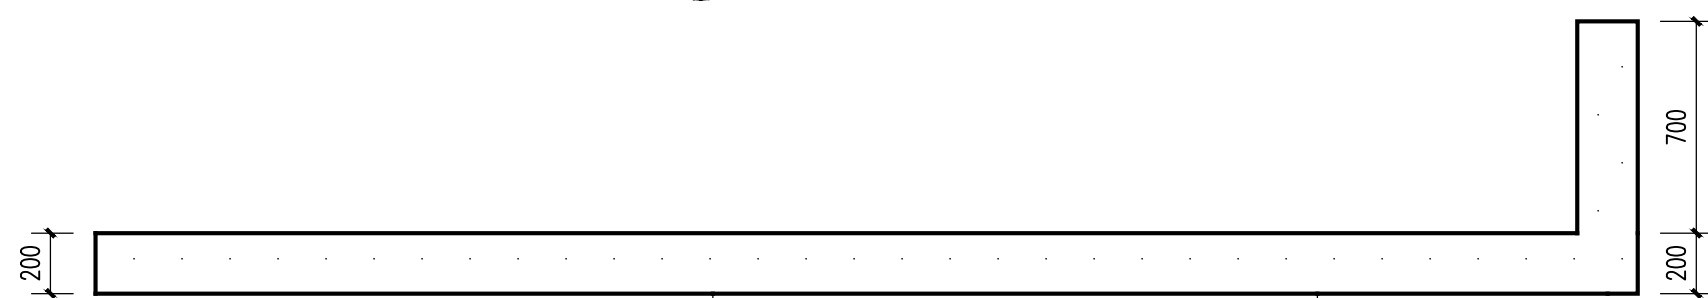


Figure 1 illustrates the dimensions of the printing area. The central area is labeled "文字记者工作区" (Text Journalist Work Area). The overall width is 4900 and the height is 968. A 200-unit margin is indicated on the right side. A label "印刷标识文字" (Printing Identification Text) points to the central area.

A diagram of a rectangular field divided into two sections. The left section is 200 units wide and the right section is 600 units wide. The total width is 800 units.

③ 指示牌围挡大样图 1:25



④ 吊旗大样图 1:25

出图记录		ISSUE NOTES
版 本 REV.	日 期 DATE	备 注 REMARK
A	2022.02	
注册执业栏 REGISTERED ARCHITECT/ENGINEER		
姓 名		NAME
注册证书号码		REGISTRATION CERTIFICATE NO.
注册印章号码		STAMP NO.
设计号: CD-20212856-F001		JOB NO.
工程名称		PROJECT TITLE
成都大运会主新闻中心装饰搭建		
子项名称		SUB ITEM
建设单位		CLIENT
成都博雅文瑞文化传播有限公司		
图 名		DRAWING TITLE
媒体工作间指示及吊旗大样图		
单 位 mm	UNIT	图 别 室 施 DWG. CATEGORY
比 例 1:25	SCALE	图 号: D11 DWG. NO.
日 期 2022.02	DATE	版 本: A VER. NO.
制 图 DRAWN BY	张 丽	
设 计 DESIGNED BY	肖子颖	
校 对 CHECKED BY	李耀文	
专业负责人 DISCIPLINE CHIEF	肖子颖	
设计总负责人 PROJECT CHIEF	张 竣	
审 核 AUDIT	张 竣	
审 定 APPROVED BY	华 轲	
国 基准方中 成都基准方中建筑设计股份有限公司 Chengdu JZFC Architectural Design Co., Ltd. 中国 成都市 琉璃场8号华润广场A座7-15楼 电话: +86(28) 86333800 传真: +86(28) 86582990 7-15F, Tower A, Criad Plaza, No.8Jiuli Road, Chengdu, P.R.C tel. +86(28) 86333800 fax. +86(28) 86582990 工程设计资质证书编号: A151016191 电子文档编号: - CAD FILENAME 版 权 说 明 COPYRIGHT DECLARATION 此图版权为成都基准方中建筑设计股份有限公司所有, 未经许可不得使用。		