



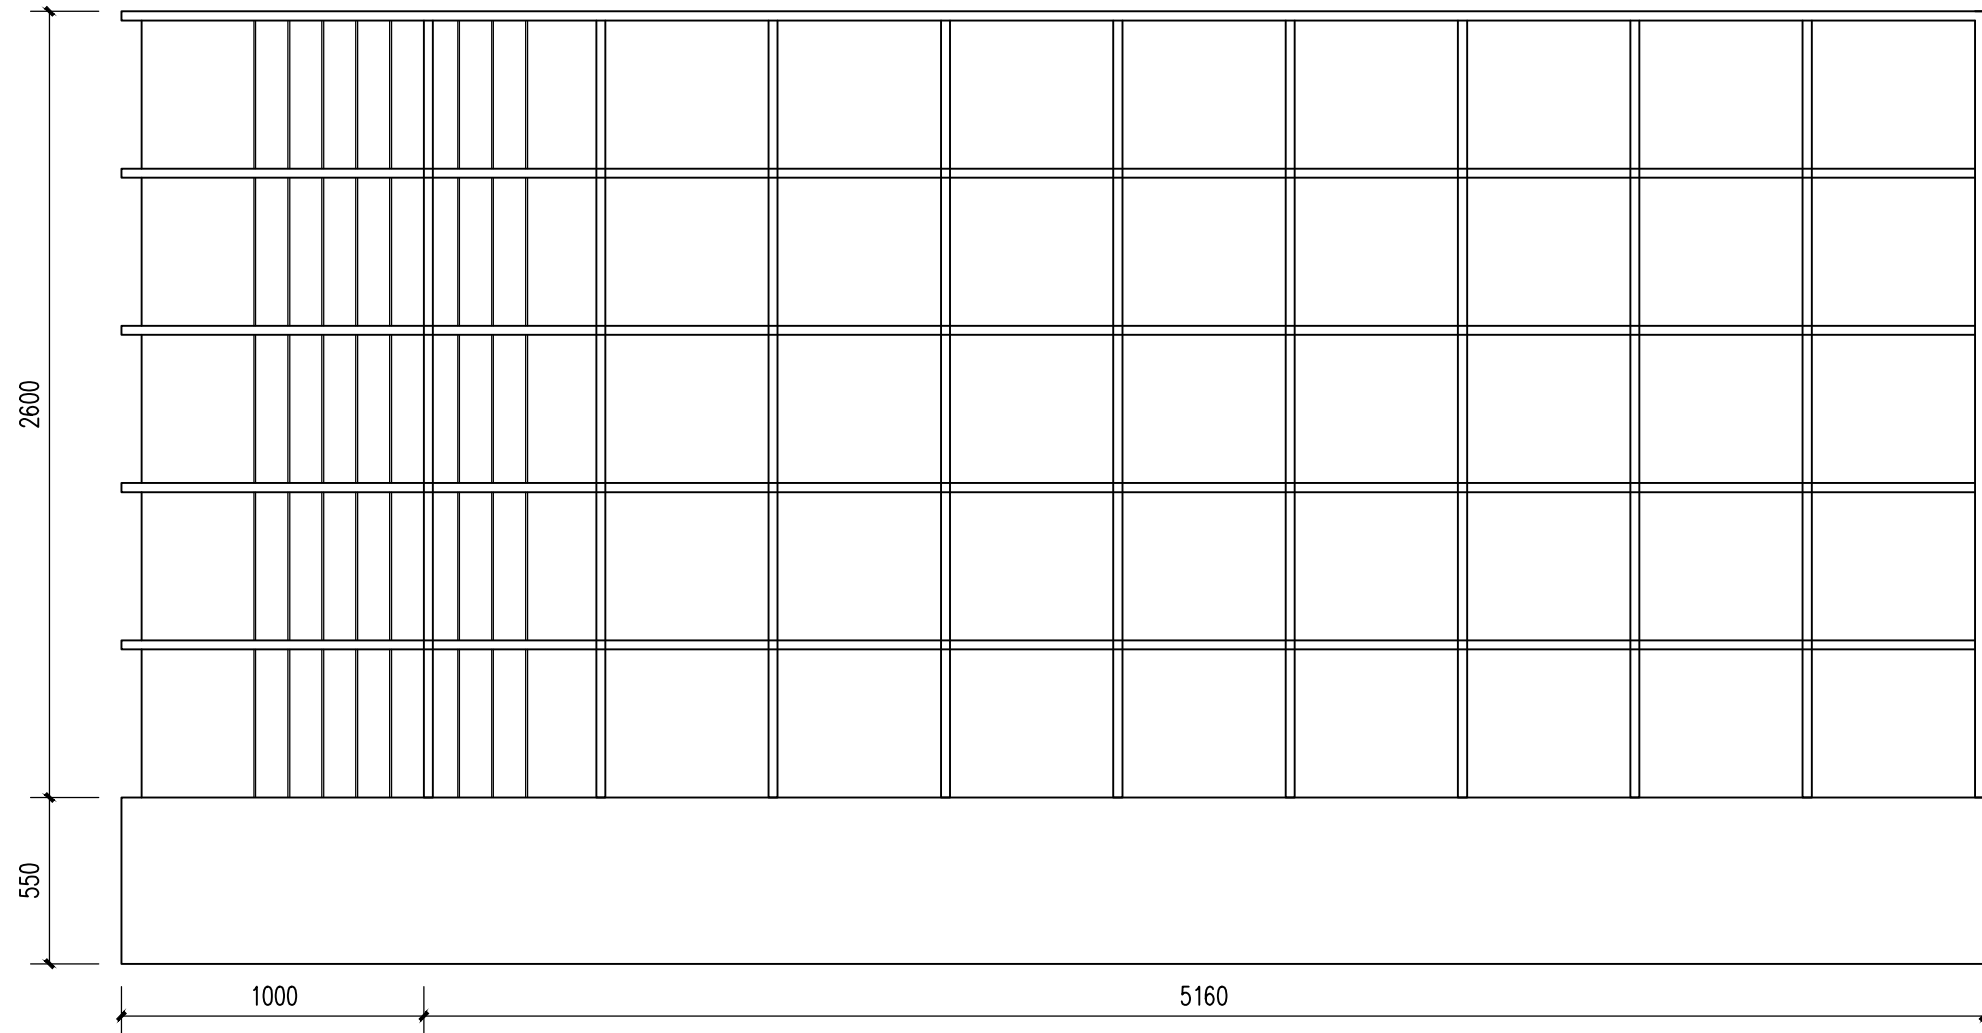


书架 B 立面视图 1:25

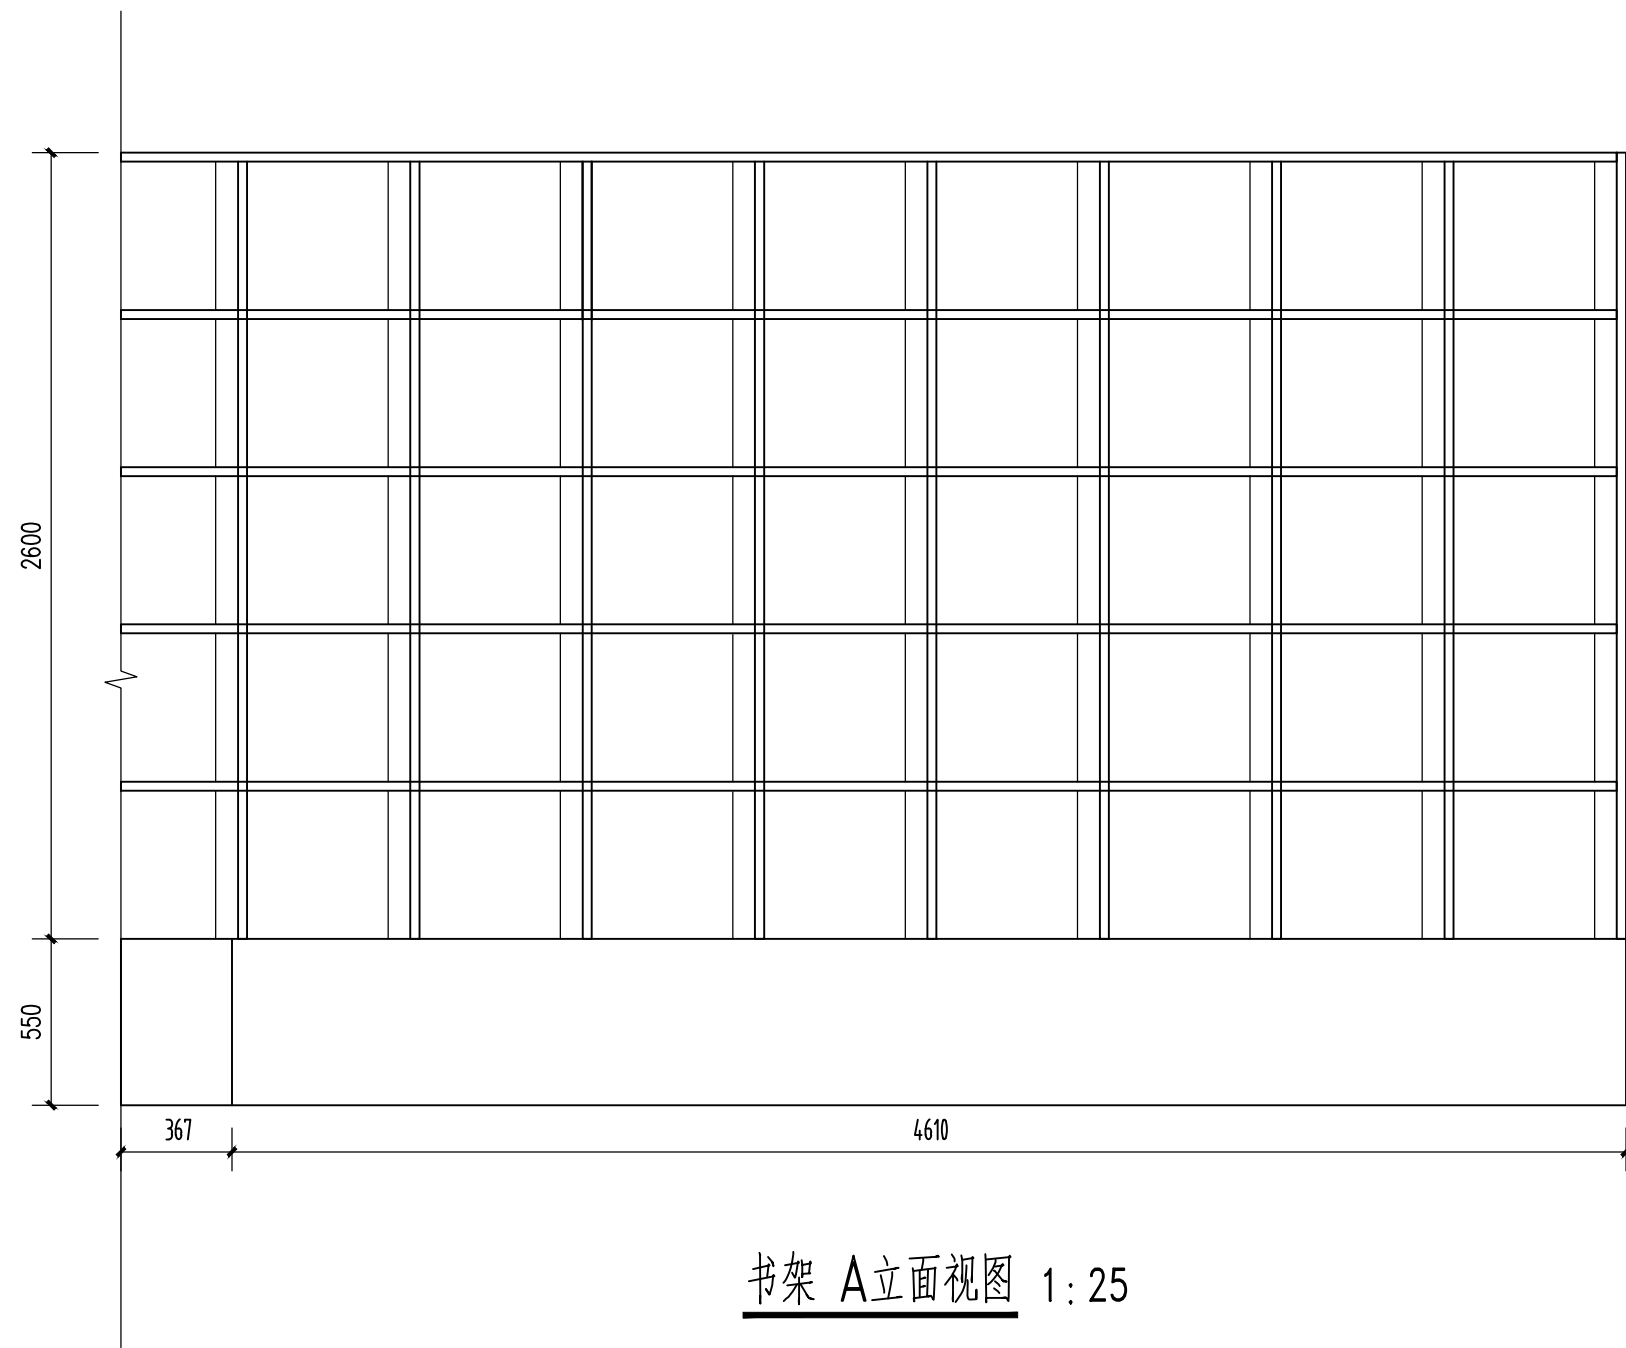


书架 A立面视图 1:25

① 媒体工作间书架大样图 1:25

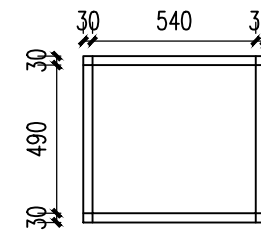

书架标准格子详图 1:25

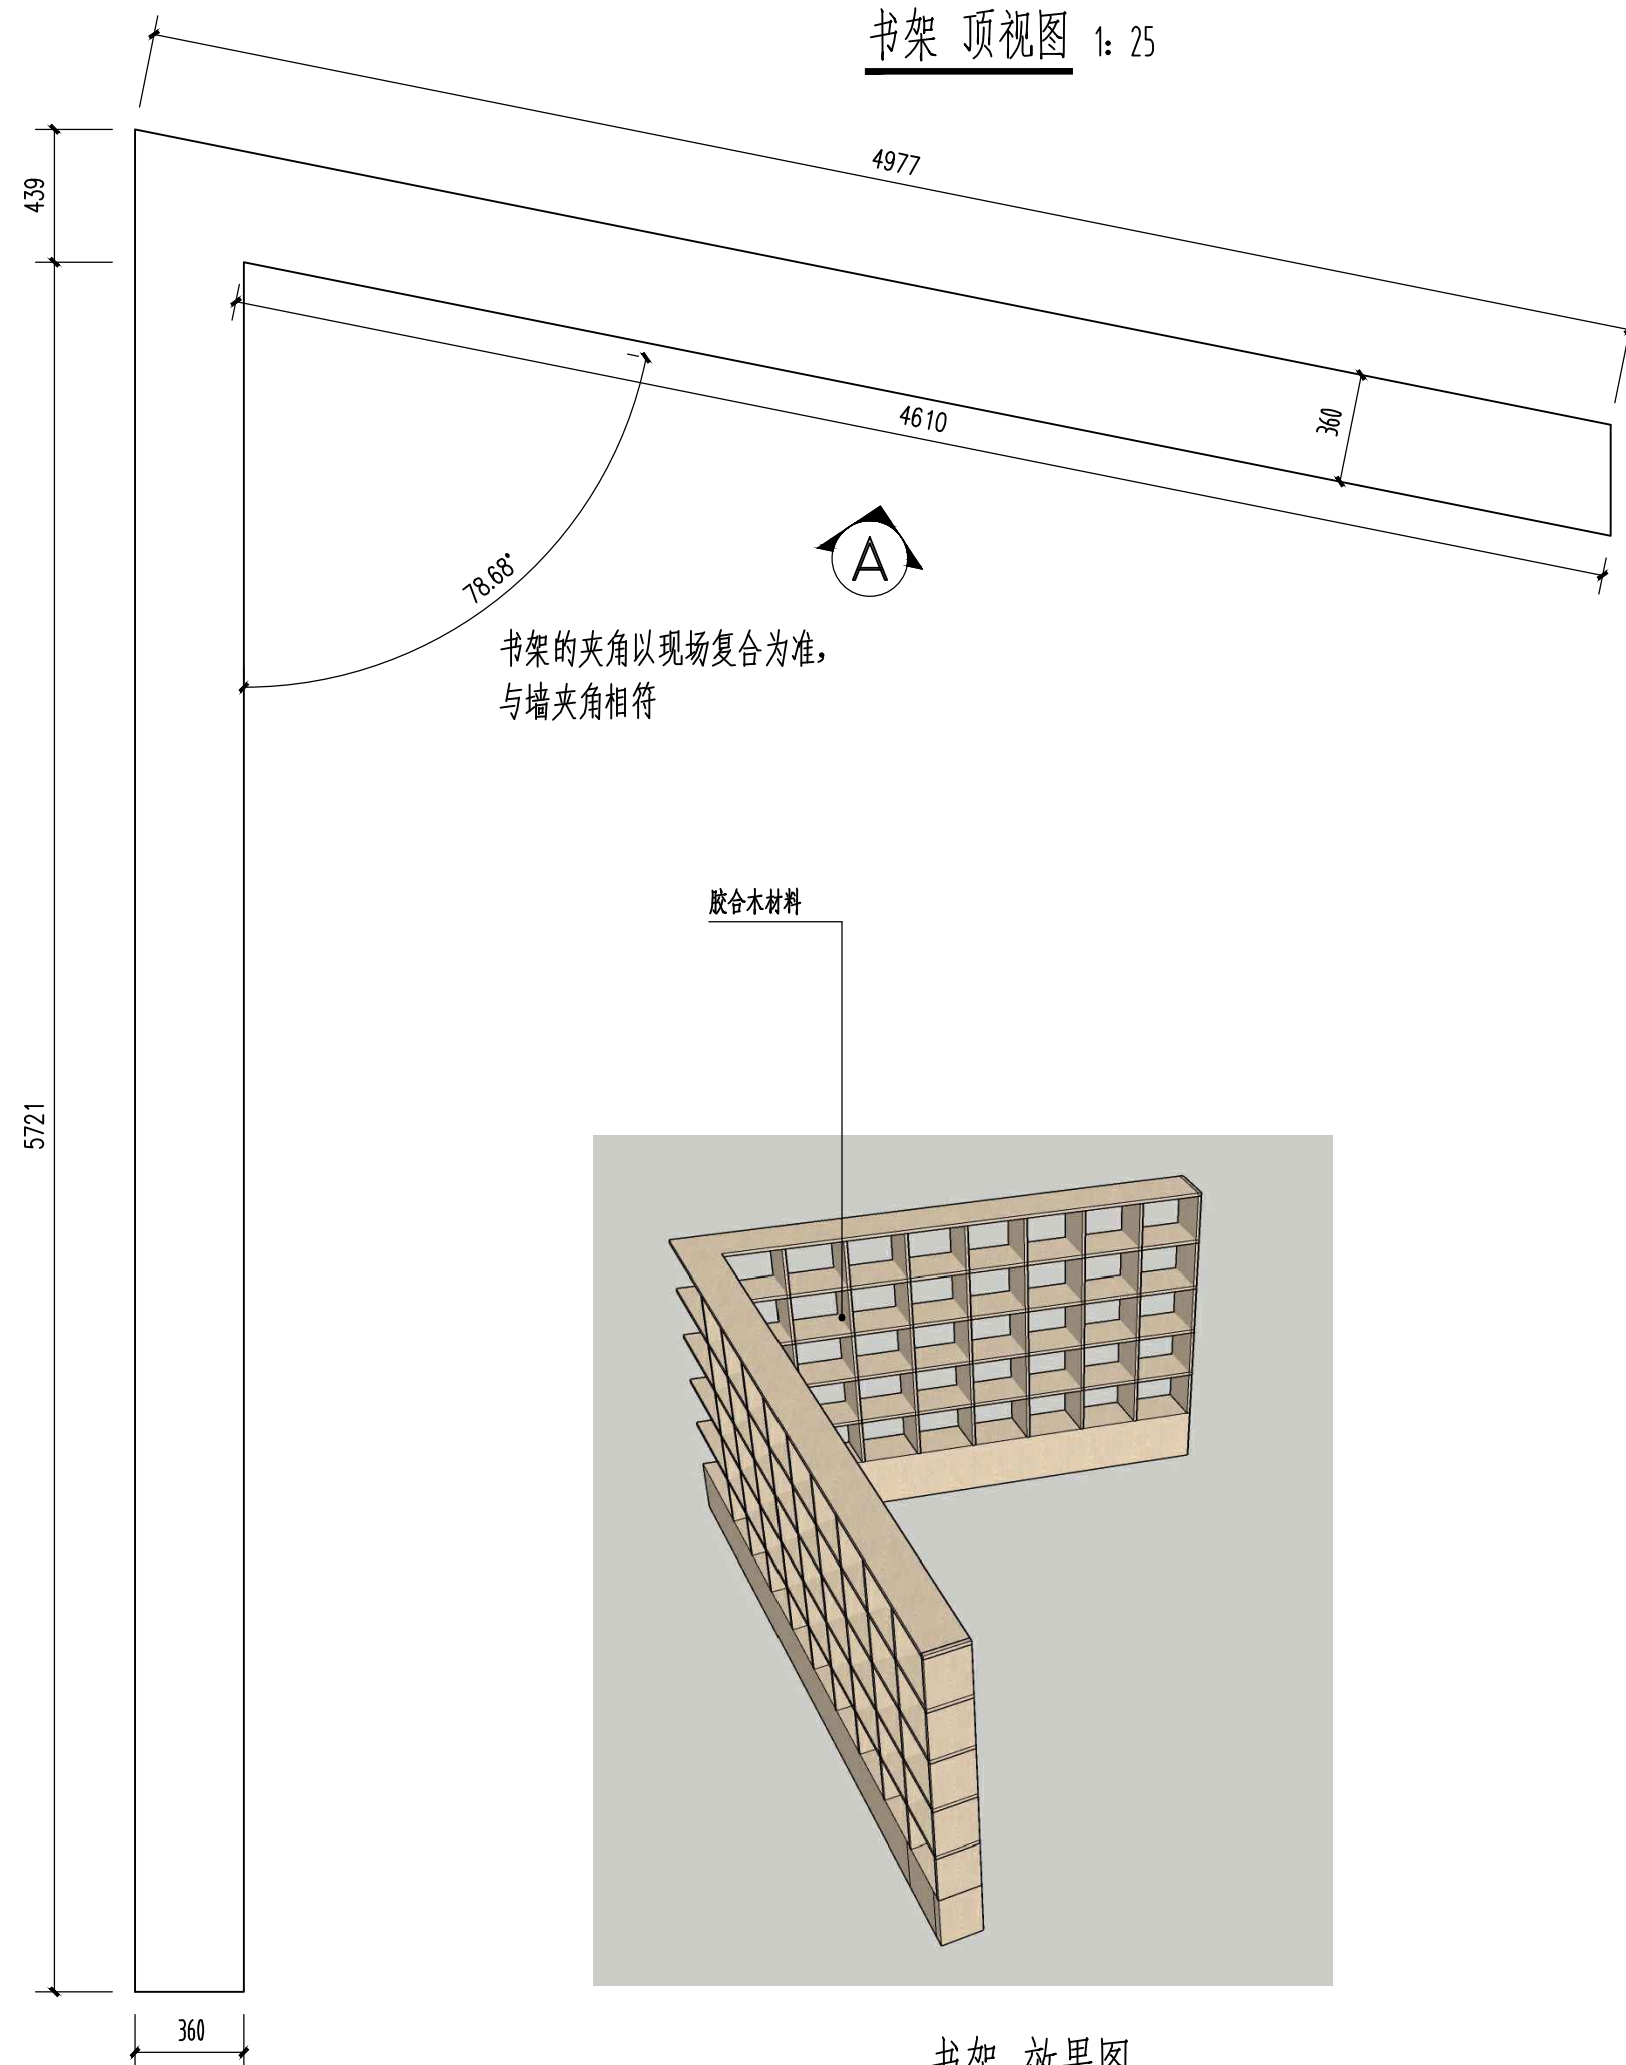

书架效果图

[illegible]