
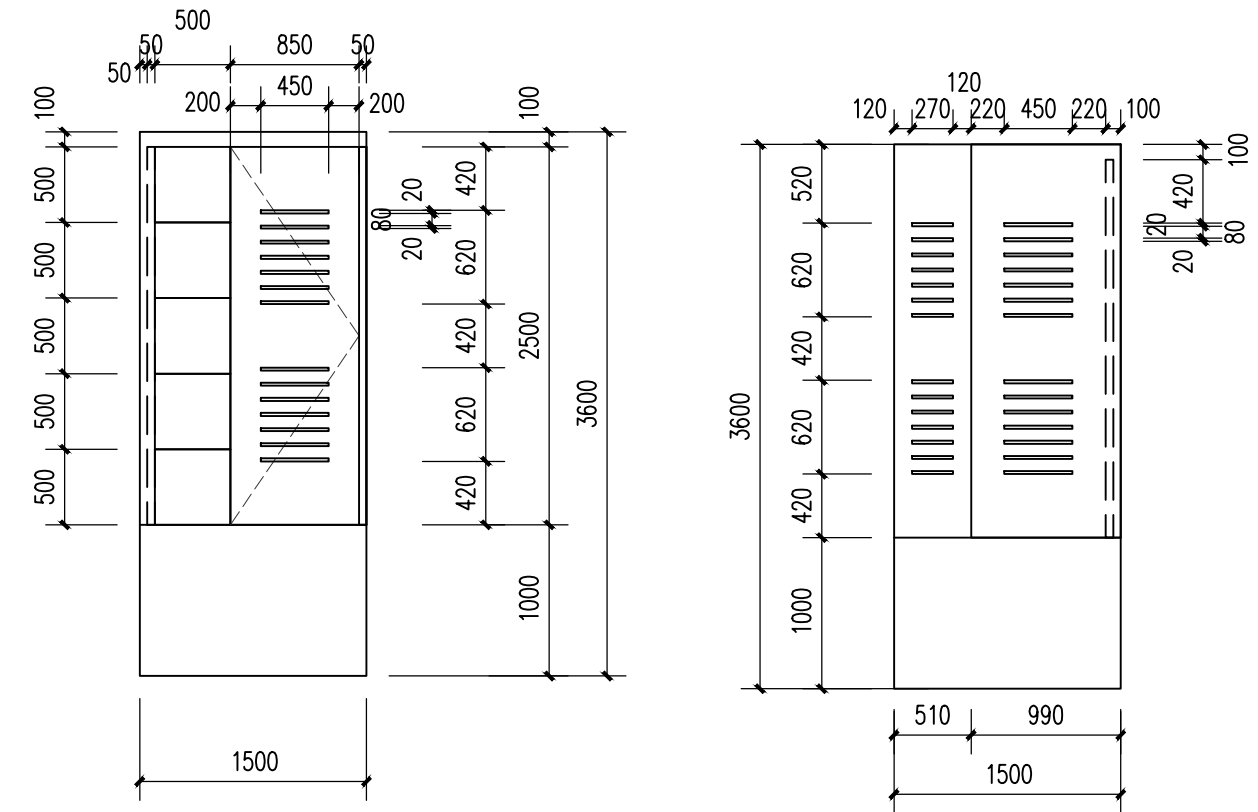
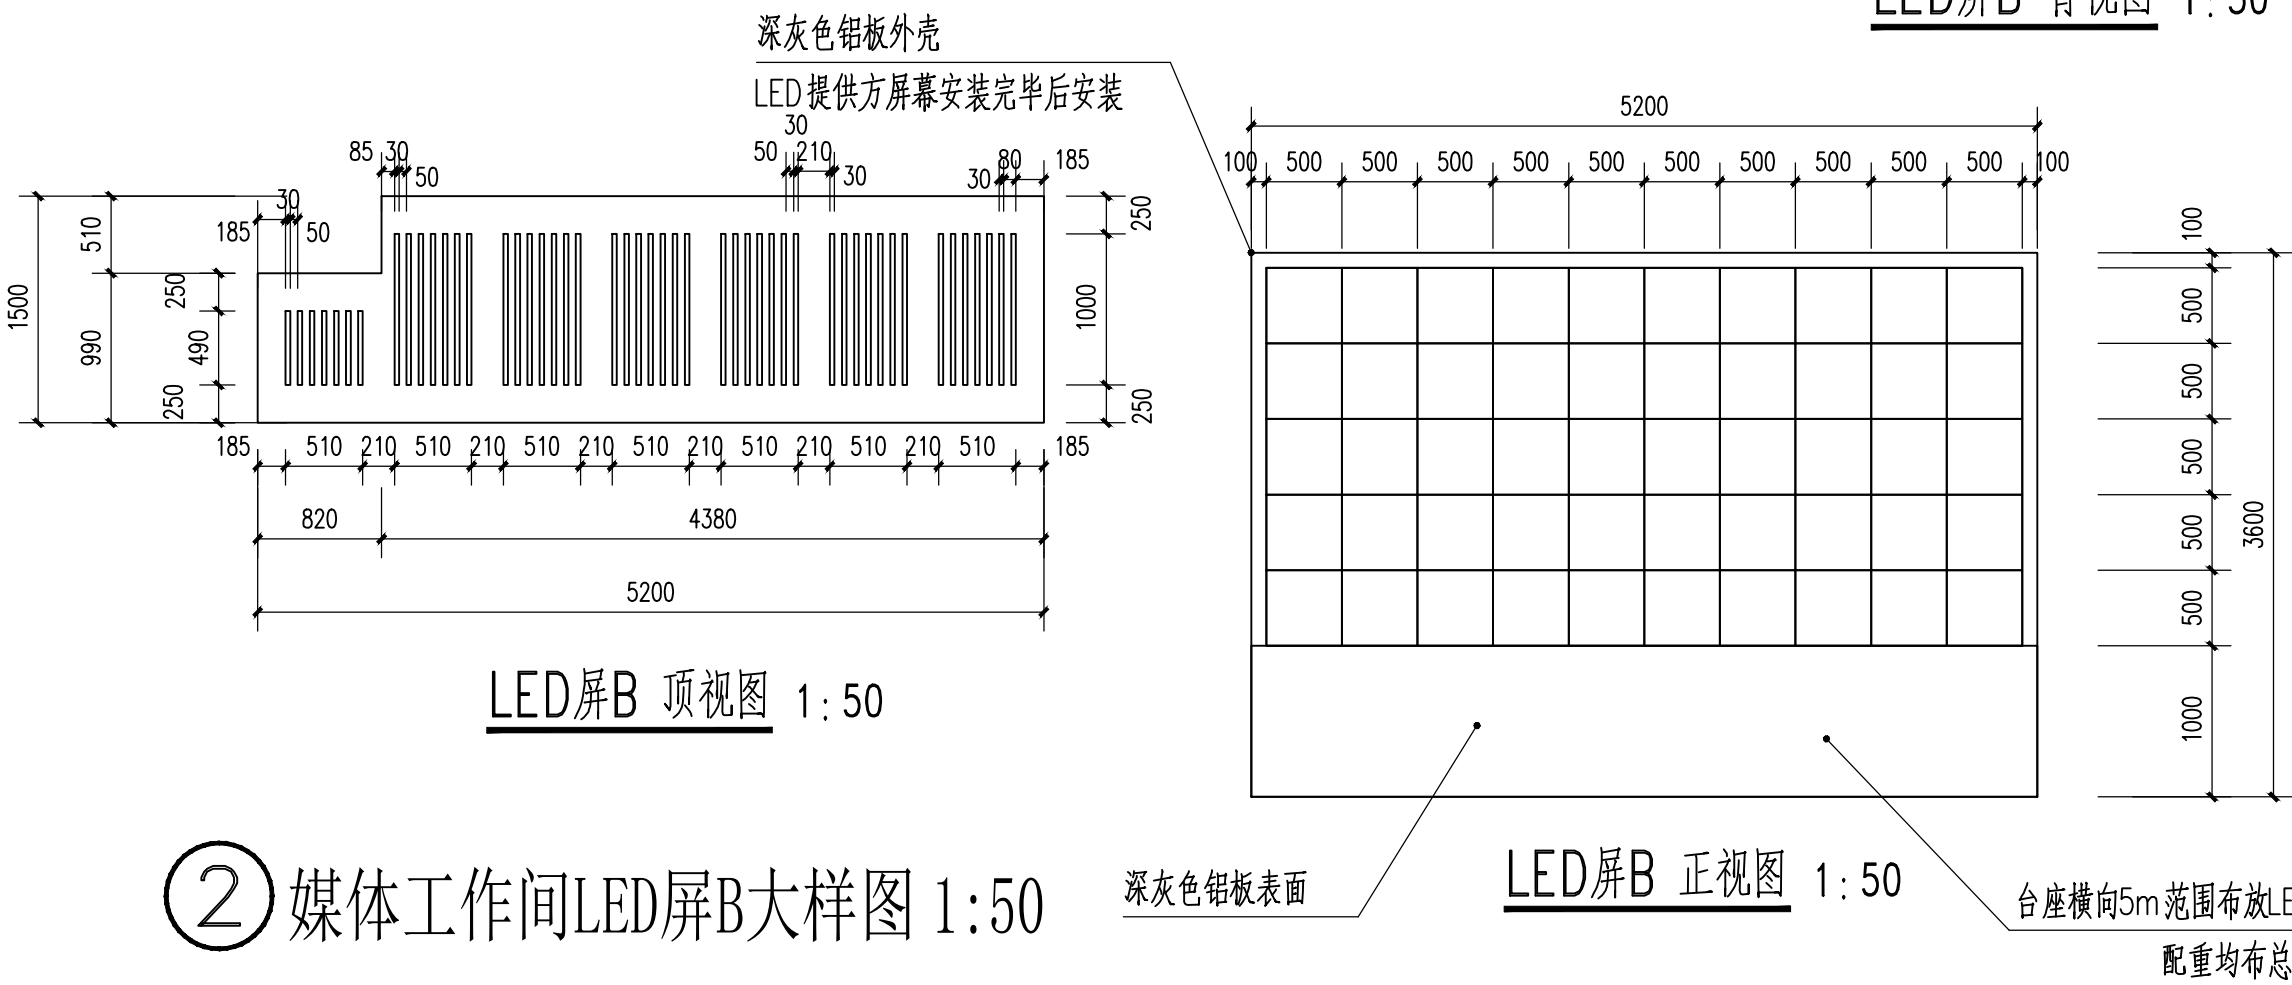
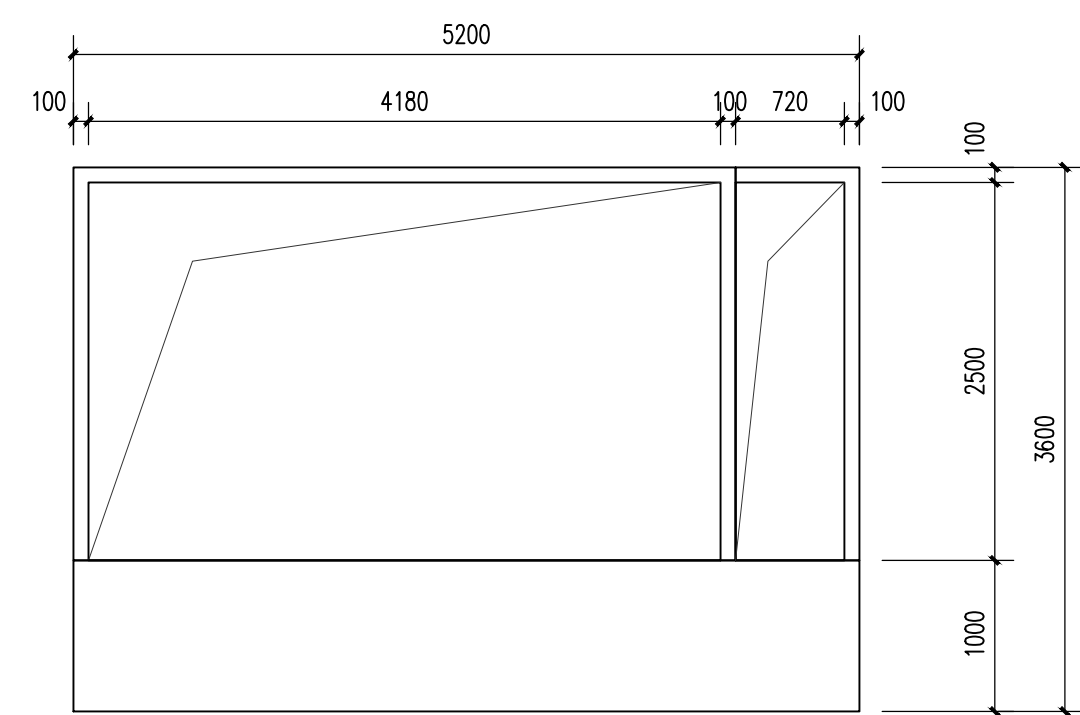
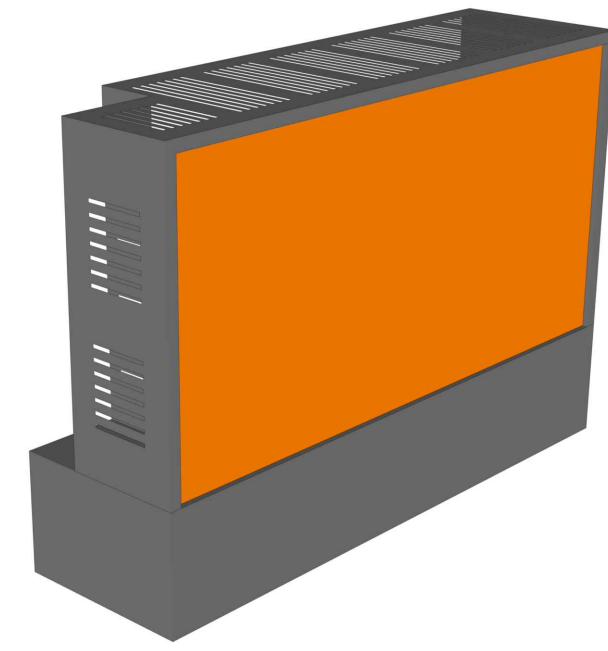
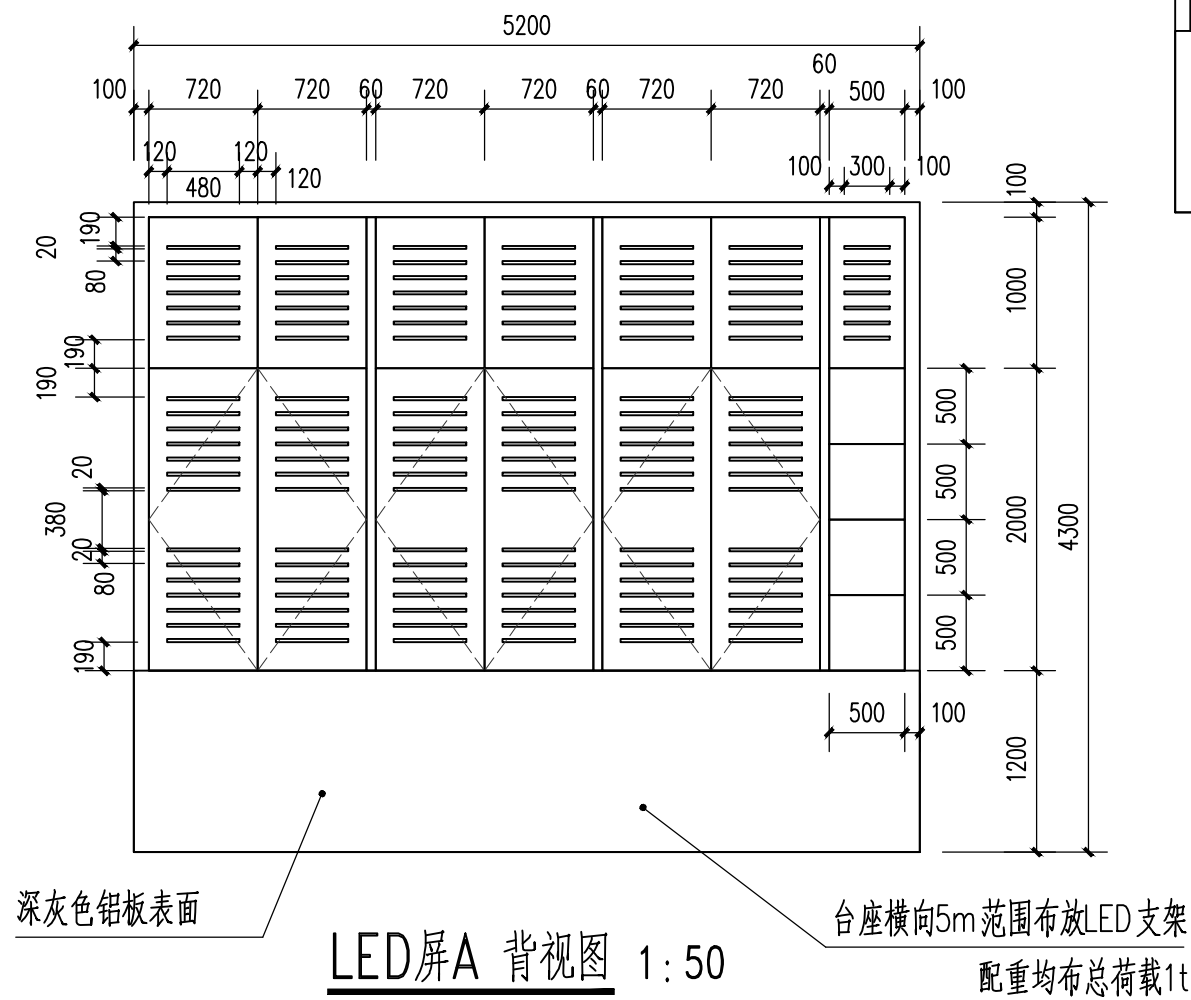
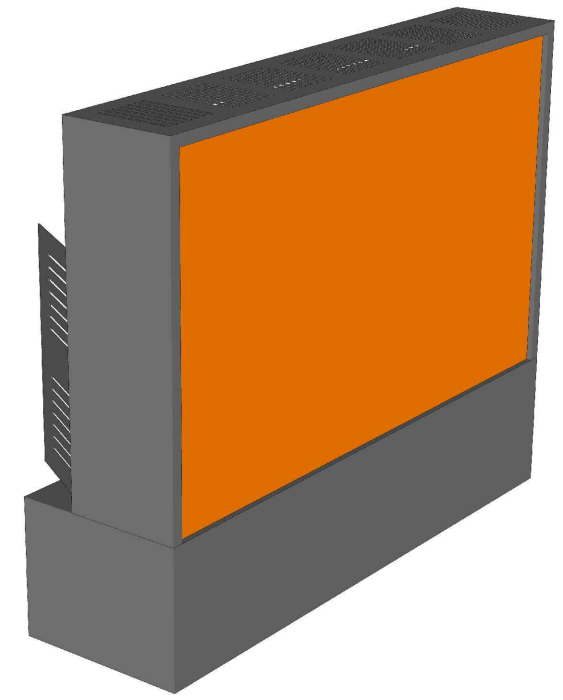


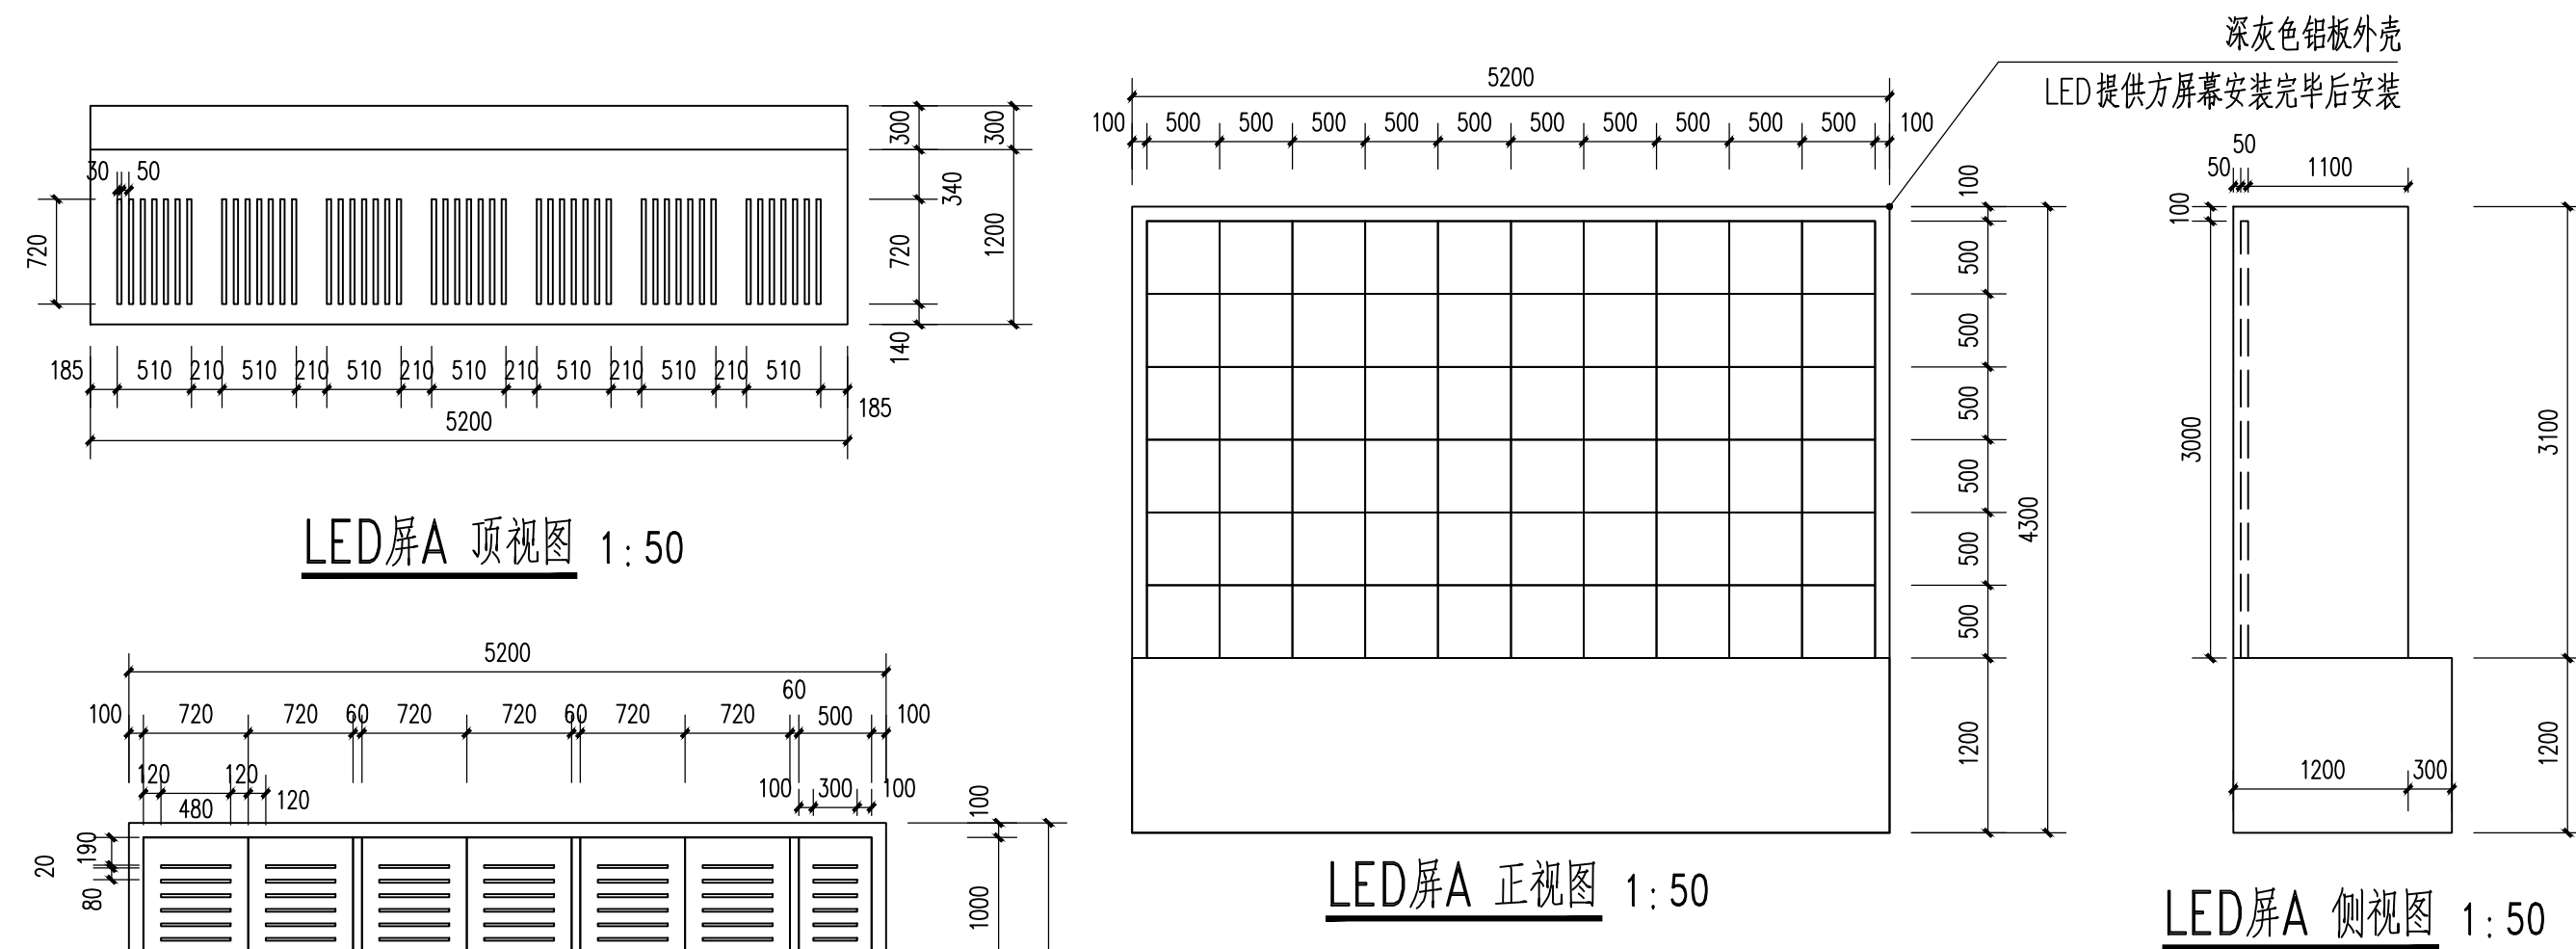

出图记录			ISSUE NOTES		
版 本 REV.	日 期 DATE	备 注 REMARK			
A	2022.02				
注册执业栏					
REGISTERED ARCHITECT/ENGINEER					
姓 名					
NAME					
注册证书号码					
REGISTRATION CERTIFICATE NO.					
注册印章号码					
STAMP NO.					
设计号: CD-20212856-F001					
JOB NO.					
工程名称					
PROJECT TITLE					
成都大运会主新闻中心装饰搭建					
子项名称					
SUB ITEM					
建设单位					
CLIENT					
成都博雅文瑞文化传播有限公司					
图 名					
DRAWING TITLE					
媒体工作间LED屏大样图					
单 位	mm	UNIT	图 别	室 施	DWG. CATEGORY
比 例	1:50	SCALE	图 号	D13	DWG. NO.
日 期	2022.02	DATE	版 本	A	VER. NO.
制 图	雷鑫鹏				
DRAWN BY					
设 计	李灏文				
DESIGNED BY					
校 对	李灏文				
CHECKED BY					
专业负责人	肖子颖				
DISCIPLINE CHIEF					
设计总负责人	张峻				
PROJECT CHIEF					
审 核	张峻				
AUDIT					
审 定	华轲				
APPROVED BY					
中 基 方					
成都基准方中建筑设计股份有限公司					
Chengdu JZfZ Architectural Design Co., Ltd.					
中国 成都市 琉璃路8号华润广场A座7-15楼					
电话: +86(28) 86333800 传真: +86(28) 86582990					
7-15F, Tower A, Criland Plaza, No.8, Liuli Road , Chengdu, P.R.C					
tel. +86(28) 86333800 fax. +86(28) 86582990					
工程设计资质证书编号: A151016191					
CAD 文件编号: -					
版 权 说 明					
COPYRIGHT DECLARATION					
此图版权为成都基准方中建筑设计股份有限公司所有, 未经许可不得使用。					