
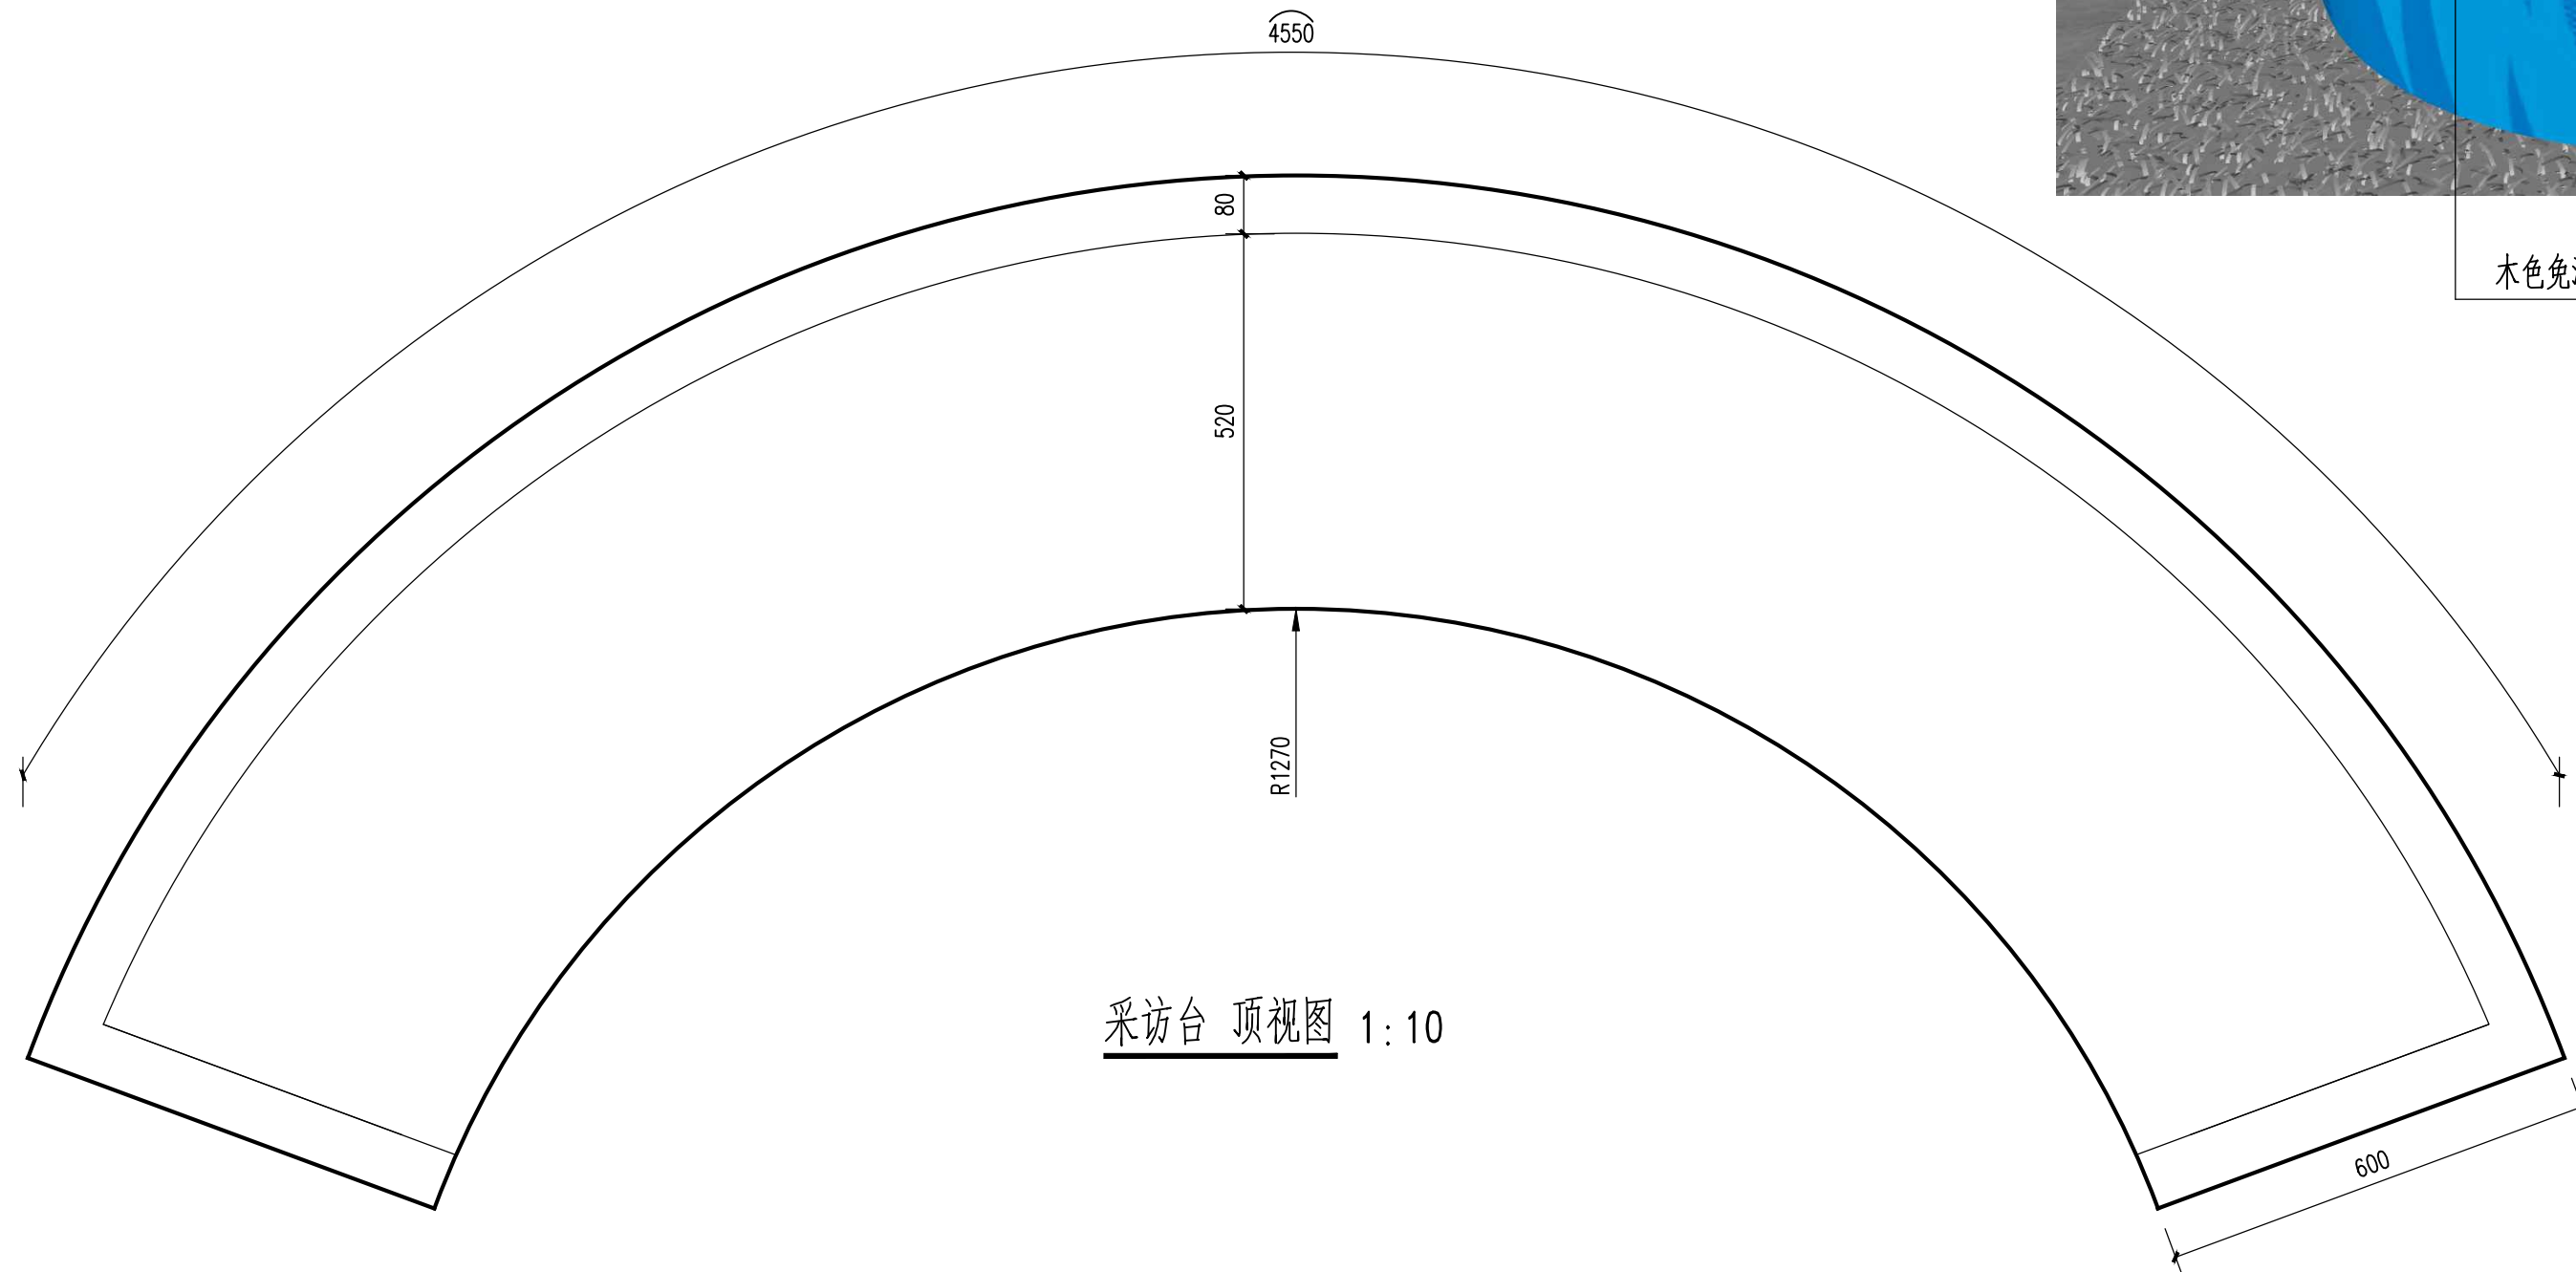


采访台 正面展开图 1:10

① 直播/采访间采访台大样图 1:10

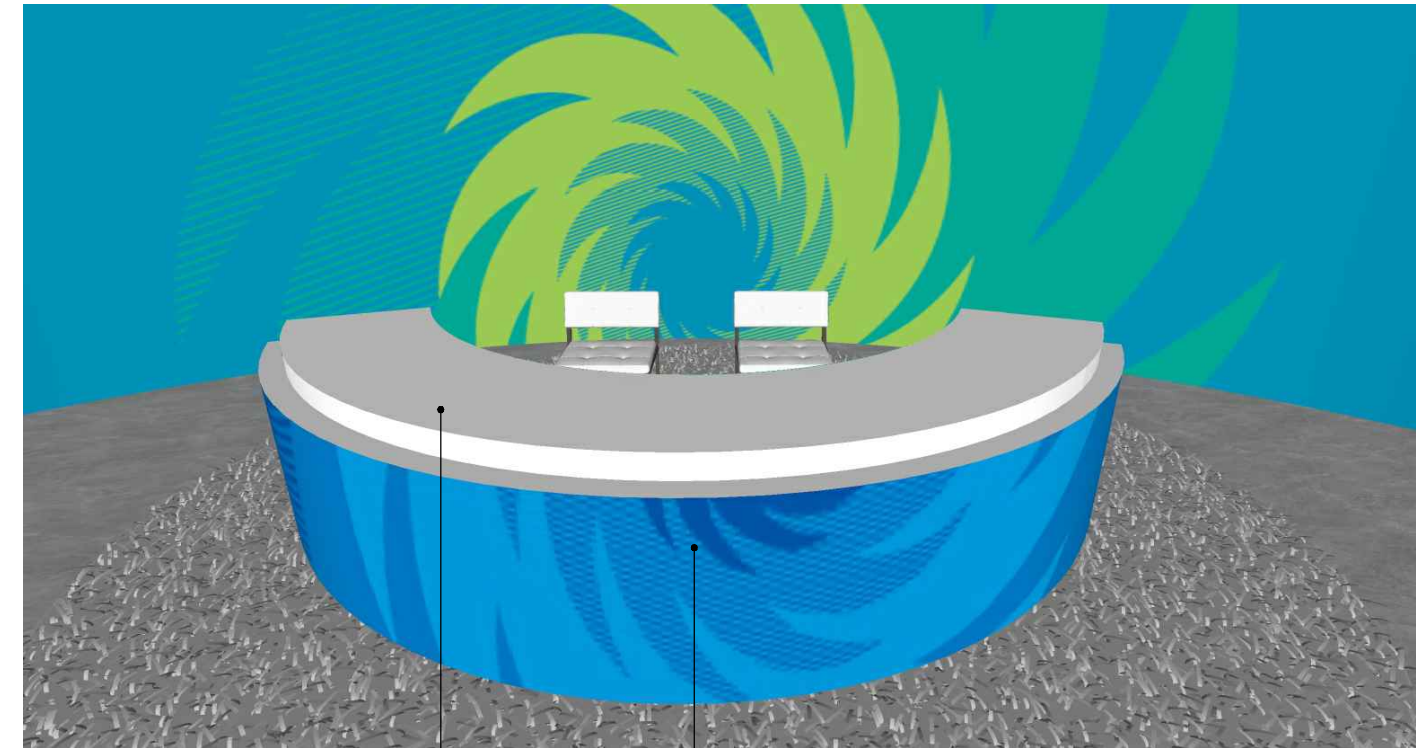

木色免漆板

大运会KV喷绘布

采访台 效果图

[illegible]

注册执业栏		REGISTERED ARCHITECT/ENGINEER	
姓 名		NAME	
注册证书号码		REGISTRATION CERTIFICATE NO.	
注册印章号码		STAMP NO.	
设计号: CD-2012856-F001		JOB NO.	
工程名称		PROJECT TITLE	
成都大运会主新闻中心装饰搭建			
子项名称		SUB ITEM	
弧形采访台 透视图			
建设单位:		CLIENT	
成都博雅文瑞文化传播有限公司			

图名		DRAWING	
直播/采访间采访台大样图			
单位	mm	UNIT	DWG. CATEGORY
比例	1:10	SCALE	图号 D15
日期	2022.02	DATE	版本 A
			VER. NO.

制 DRAWN BY	雷鑫鹏	
设 DESIGNED BY	雷鑫鹏	
校 CHECKED BY	李滢文	
专业负责人 DISCIPLINE CHIEF	肖子颖	
设计总负责人 PROJECT CHIEF	张峻	
审 AUDIT	张峻	
审 APPROVED BY	华轲	

中 方 基 准	
成都基准方中建筑设计股份有限公司	
Chengdu JZFY Architectural Design Co., Ltd.	
中国 成都市 琉璃路9号华润广场A座7-15楼	
电话: +86 (28) 86333800	传真: +86 (28) 86582990
7-15F, Tower A, Oriental Plaza, No.9Ruli Road., Chengdu, P.R.C	
tel. +86(28) 86333800	fax. +86(28) 86582990
工程投资资质证书编号: A151016191	
电子文档编号: -	
版 权 说 明	
COPYRIGHT DECLARATION	
此图版权为成都基准方中建筑设计股份有限公司所有, 未经许可不得使用。	