




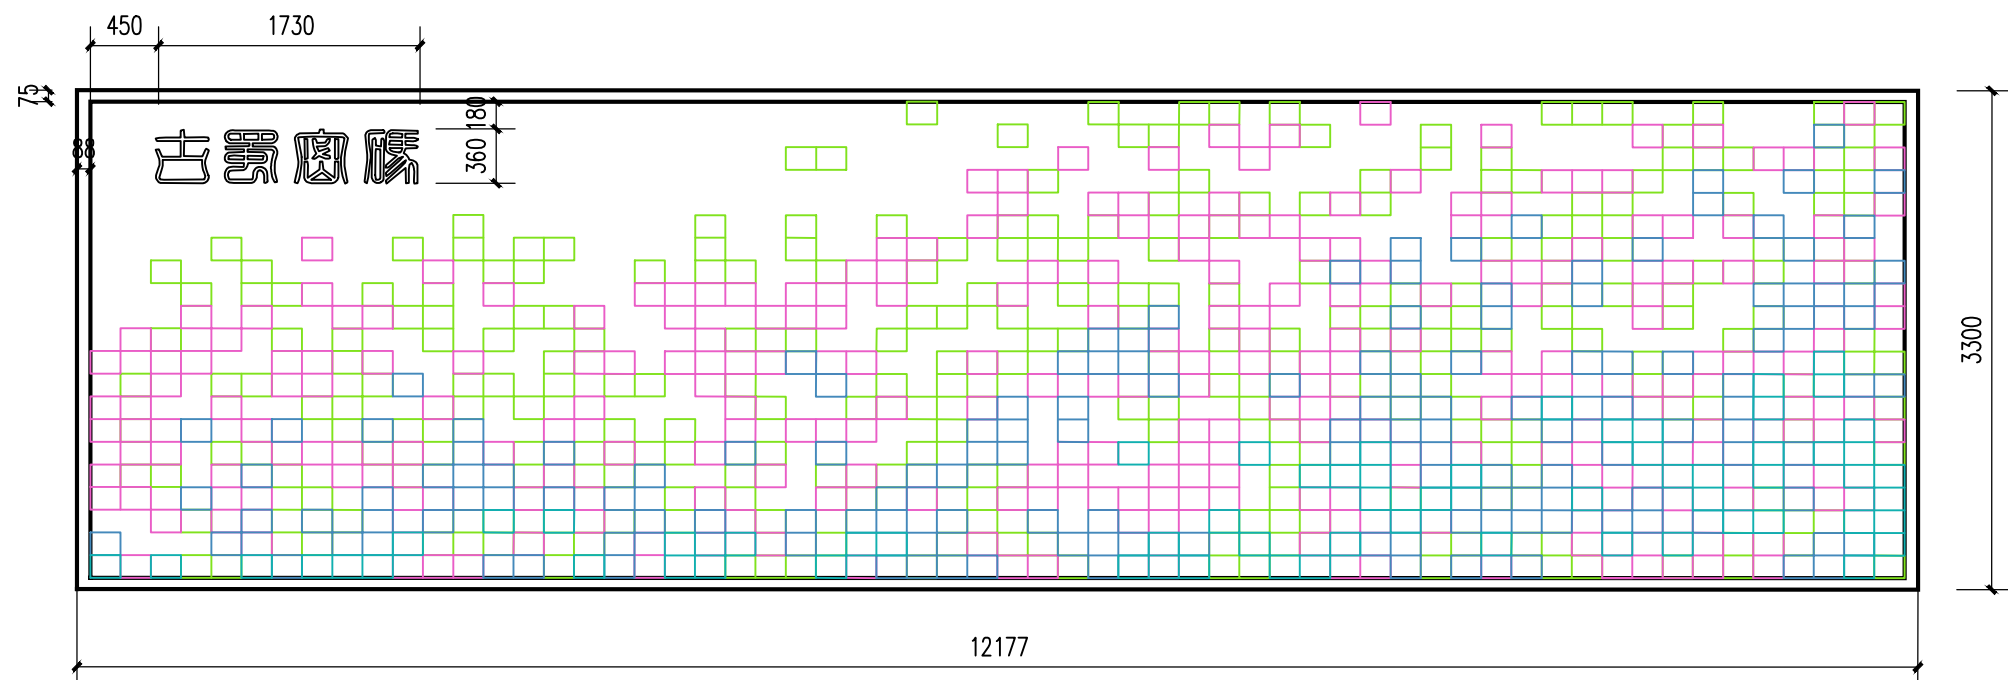


古蜀密码 正视图 1:50

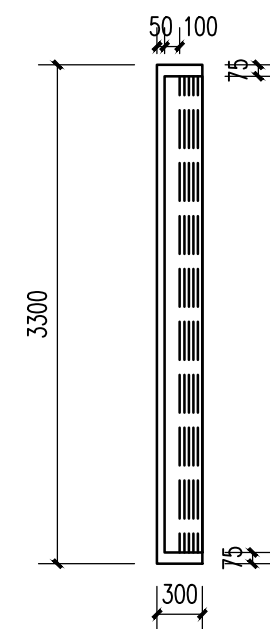

古蜀密码 侧视图 1:50

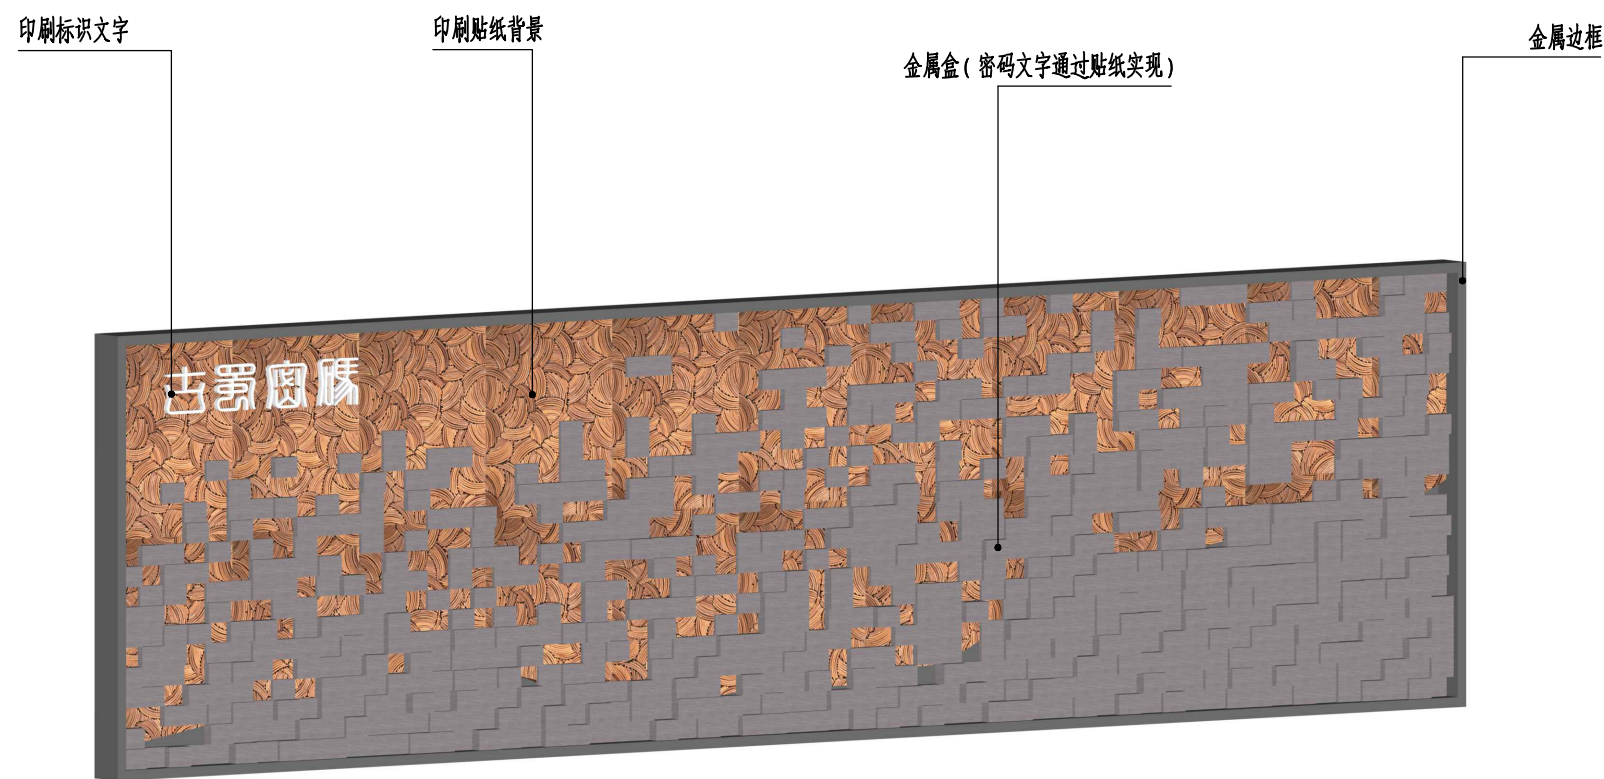

古蜀密码 效果图

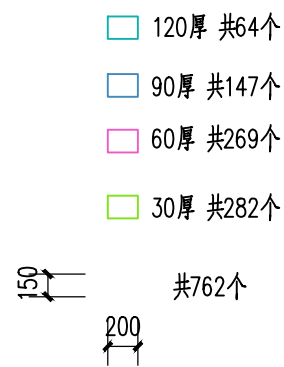

古蜀密码标准块详图 1:50

[illegible]

注册执业栏		REGISTERED ARCHITECT/ENGINEER	
姓 名		NAME	
注册证书号码		REGISTRATION CERTIFICATE NO.	
注册印章号码		STAMP NO.	
设计号: CD—2021856—F001		JOB NO.	
工程名称		PROJECT TITLE	
成都大运会主新闻中心装饰搭建			
子项名称		SUB ITEM	

建设单位:	CLIENT
成都博雅文瑞文化传播有限公司	
图 名	DRAWING TITLE
古蜀密码大样图	

单位: mm	UNIT	图别: 室施	DWG. CATEGORY
比例: 1:50	SCALE	图号: D16	DWG. NO.
日期: 2022.02	DATE	版本: A	VER. NO.

制 DRAWN BY	雷鑫鹏	
设 计 DESIGNED BY	罗匀	
校 对 CHECKED BY	李肅文	
专业负责人 DISCIPLINE CHIEF	肖子颖	
设计总负责人 PROJECT CHIEF	张峻	
审 核 AUDIT	张峻	
审 定 APPROVED BY	华轲	

基准方中

成都基准方中建筑设计股份有限公司
Chengdu JZFY Architectural Design Co., Ltd.

中国 成都市 琉璃路8号华润广场A座7-15楼
电话: +86(28) 86333800 传真: +86(28) 86582990
7-15F, Tower A. Criland Plaza. No.8, Liuli Road, Chengdu, P.R.C.
tel. +86(28) 86333800 fax. +86(28) 86582990

工程设计资质证书编号: A151016191

电子文档编号: —

版 权 说 明

COPYRIGHT DECLARATION

此图版权为成都基准方中建筑设计股份有限公司所有，未经许可不得使用。

① 古蜀密码大样图 1:50