




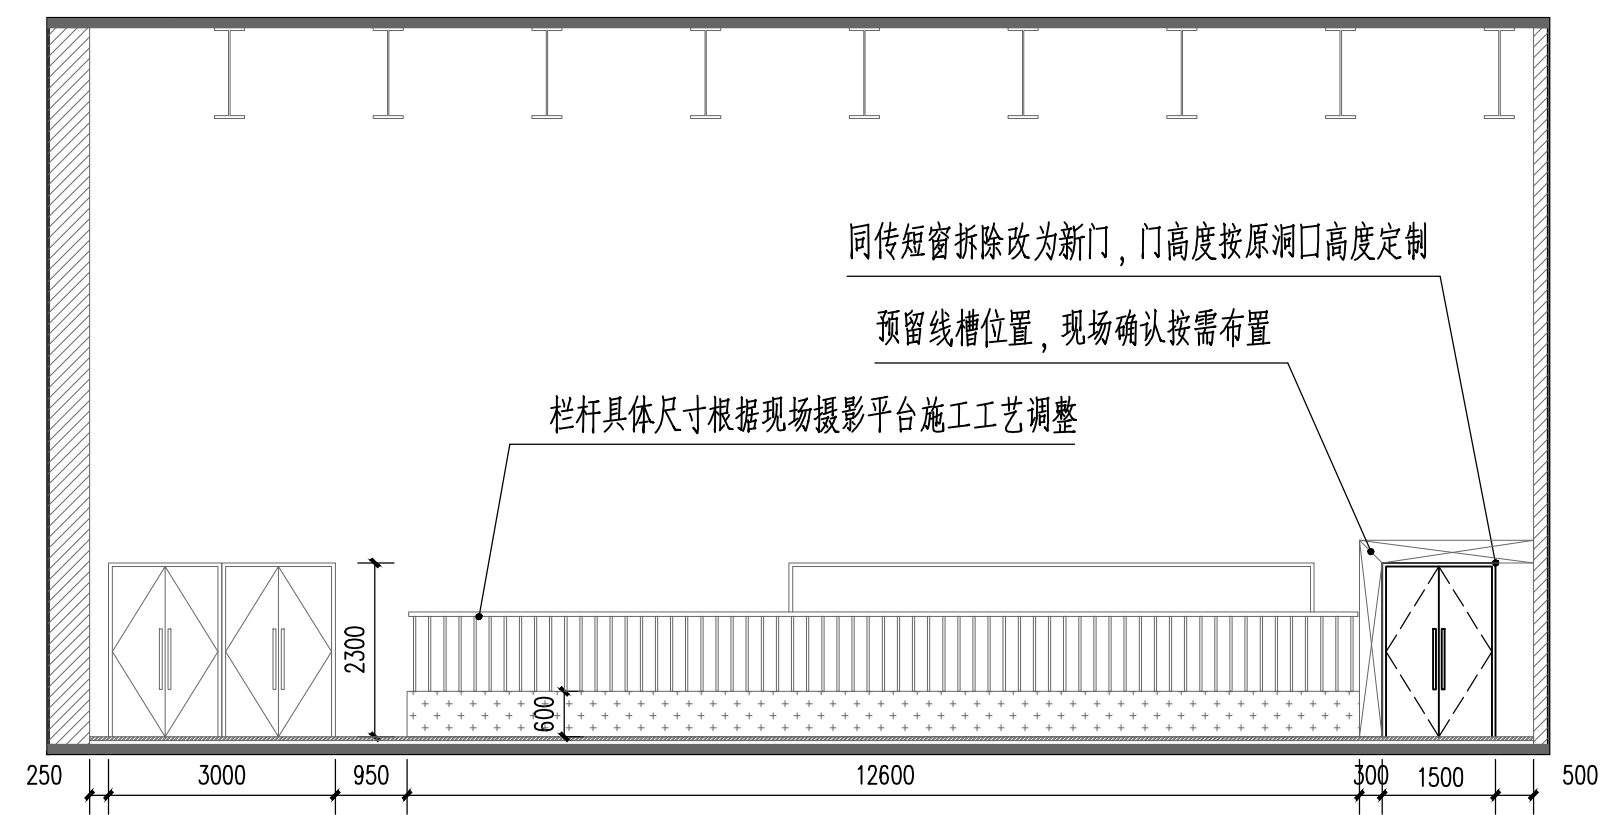




发布厅1 A立面图 1:100

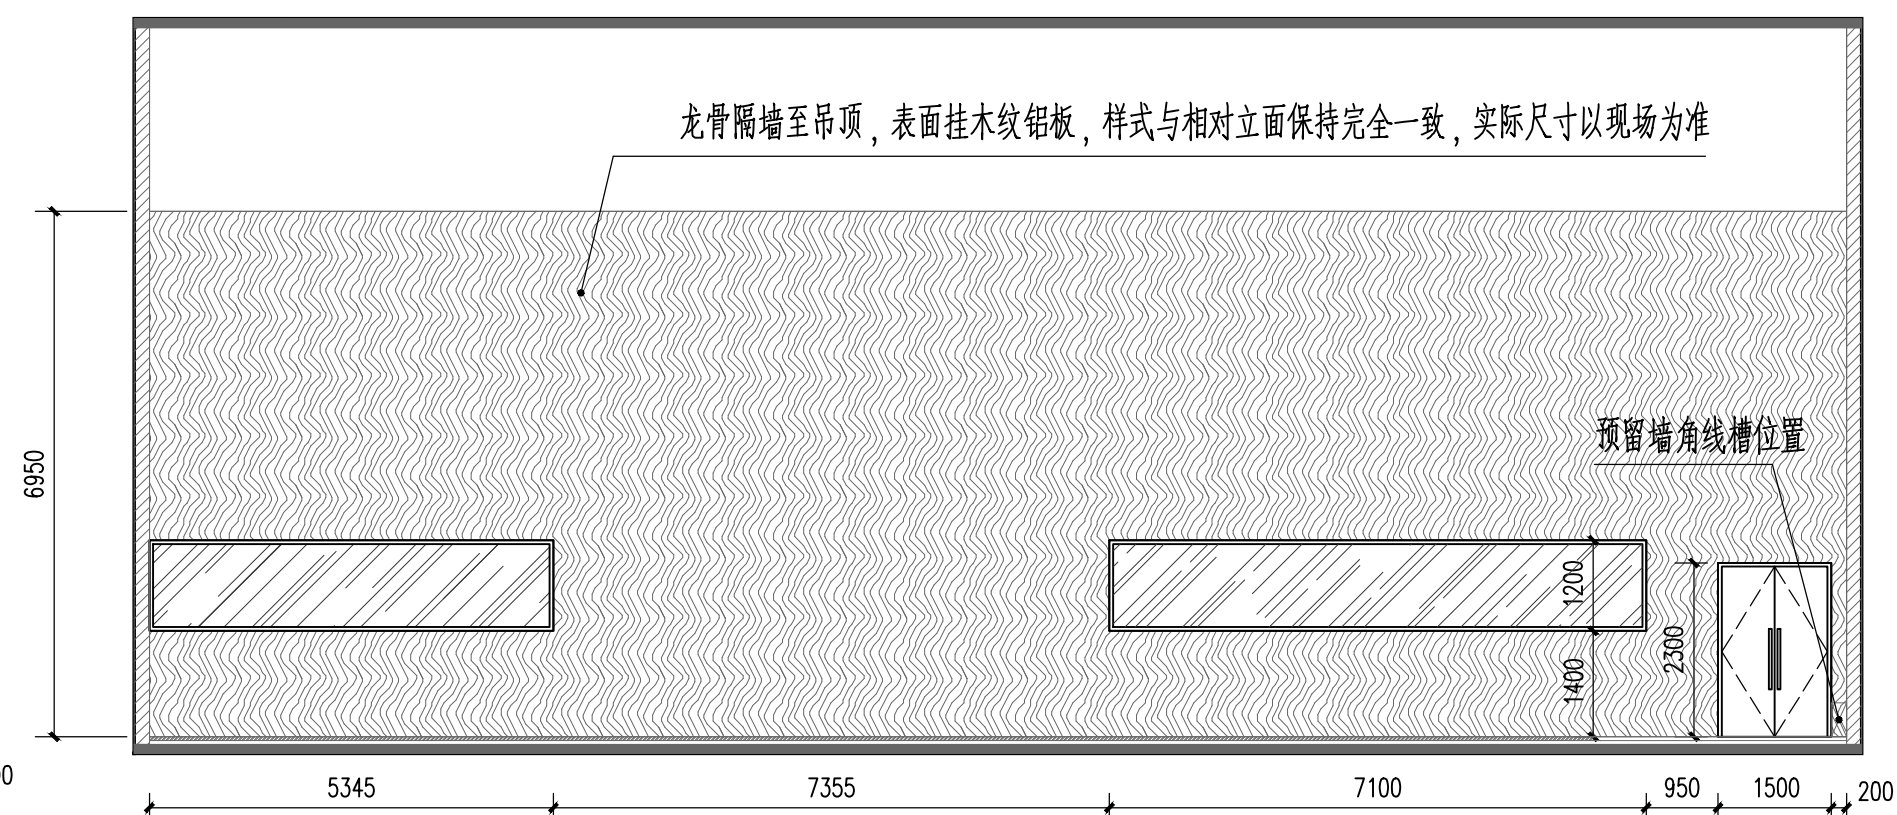

发布厅1 B立面图 1:100

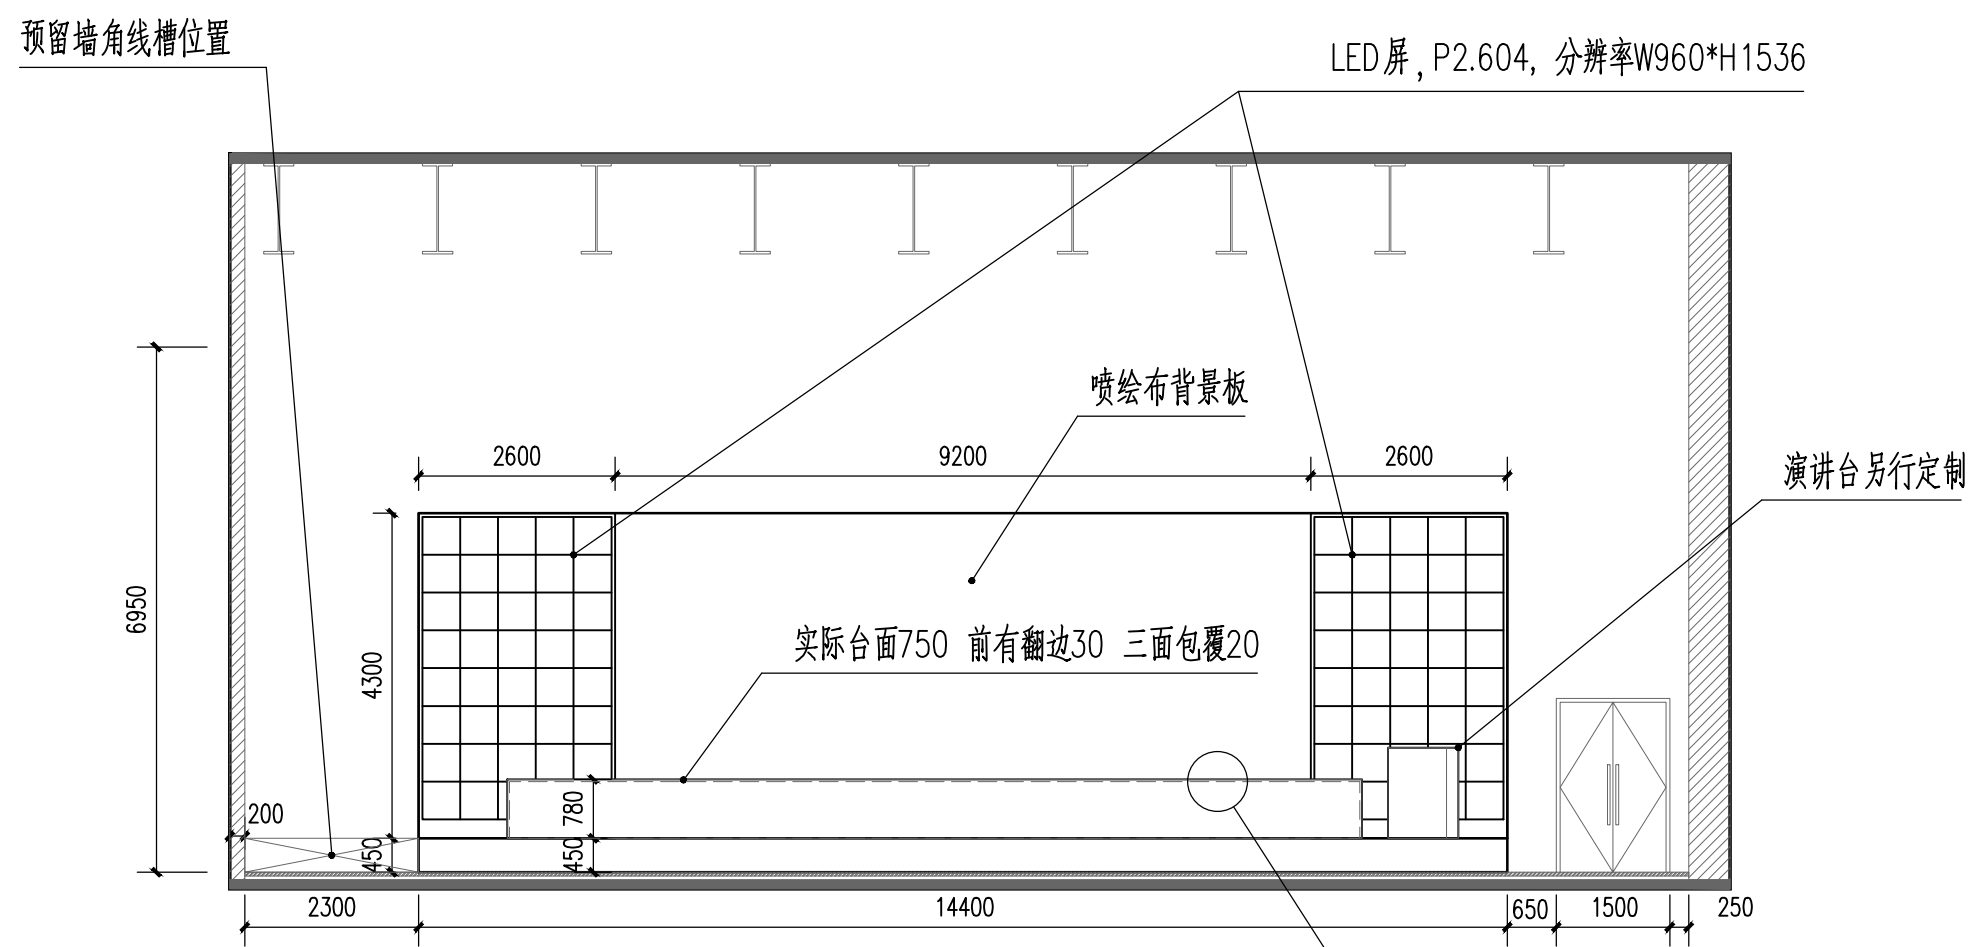

发布厅1 C立面图 1:100

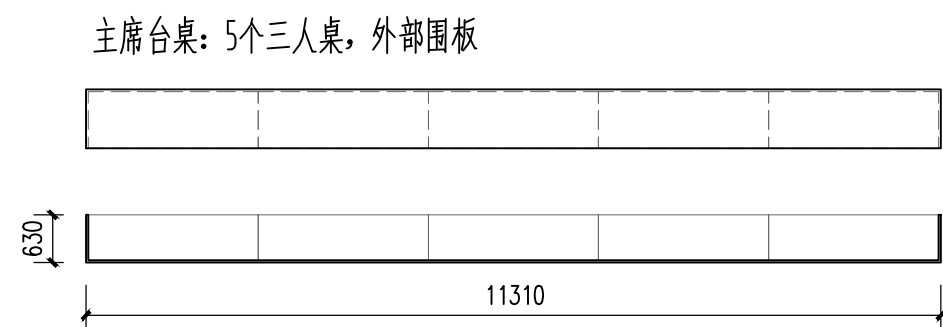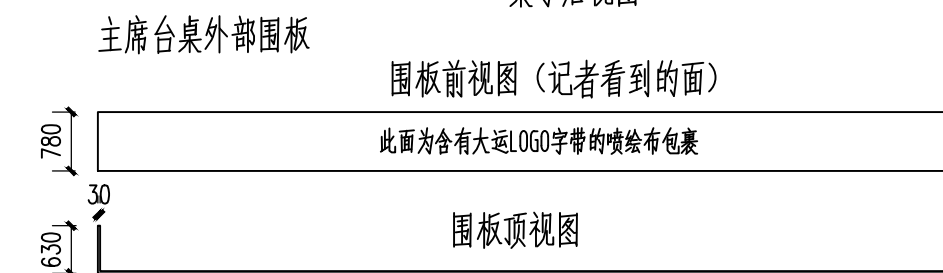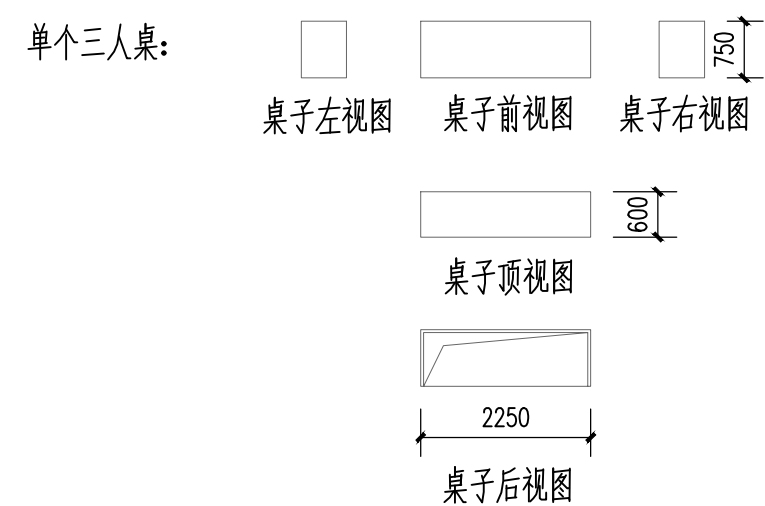

① 发布厅1主席台桌子详图 1:100

出图记录		ISSUE NOTES	
版 本 REV.	日 期 DATE	备 注 REMARK	
A	2022.02		
注册执业栏 REGISTERED ARCHITECT/ENGINEER			
姓 名		NAME	
注册证书号码		REGISTRATION CERTIFICATE NO.	
注册印章号码		STAMP NO.	
设计号：CD-20212856-F001		JOB NO.	
工程名称		PROJECT TITLE	
成都大运会主新闻中心装饰搭建			
子项名称		SUB ITEM	
建设单位		CLIENT	
成都博雅文瑞文化传播有限公司			
图 名		DRAWING TITLE	
新闻发布厅1立面图			
单 位mm	UNIT	图 别室施	DWG. CATEGORY
比 例1:100	SCALE	图 号E03	DWG. NO.
日 期2022.02	DATE	版 本A	VER. NO.
制 图 DRAWN BY	李晚洁		
设 计 DESIGNED BY	陈星杭		
校 对 CHECKED BY	李瀛文		
专业负责人 DISCIPLINE CHIEF	肖子顺		
设计总负责人 PROJECT CHIEF	张峻		
审 核 AUDIT	张峻		
审 定 APPROVED BY	华轲		
基准方中 成都基准方中建筑设计股份有限公司 Chengdu JZfz Architectural Design Co., Ltd.			
中国·成都市·琉璃路9号华润广场A座7-15楼 电话：+86(28) 86333800 传真：+86(28) 86582990 7-15F, Tower A, Criland Plaza, No.8,Liuli Road , Chengdu, P.R.C tel. +86(28) 86333800 fax. +86(28) 86582990			
工程设计资质证书编号：A151016191			
电子文档编号：-		CAD FILENAME	
版 权 说 明 COPYRIGHT DECLARATION 此图版权为成都基准方中建筑设计股份有限公司所有，未经许可不得使用。			