

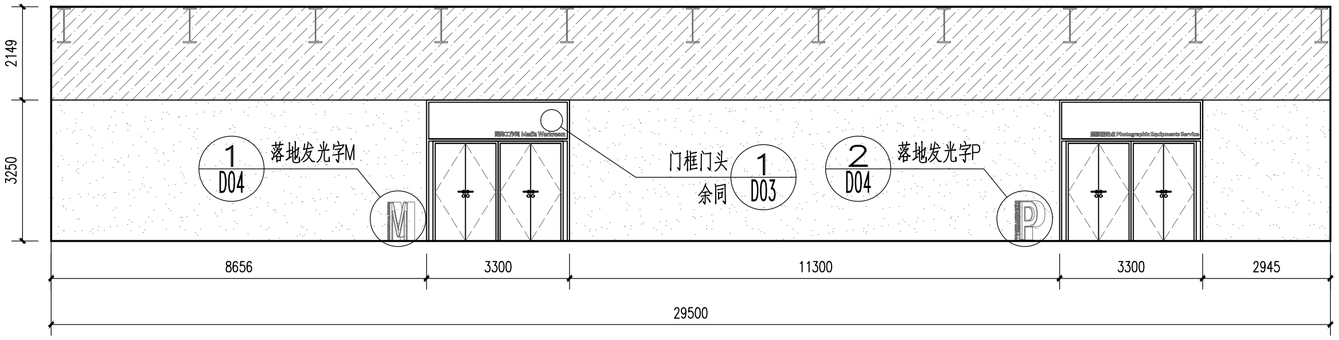


西入口区域 A立面图 1:100

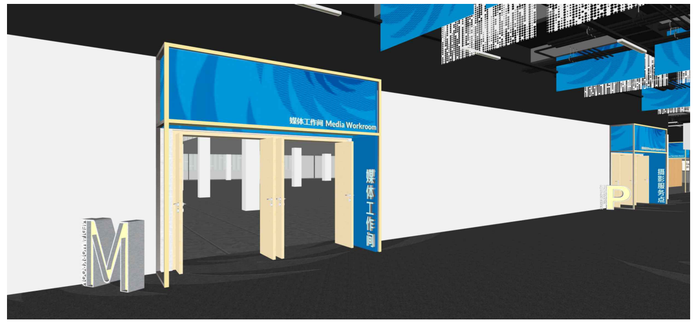


西入口区域 A立面效果图

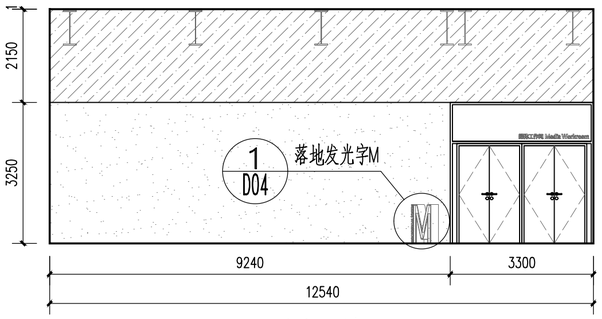


西入口区域 B立面图 1:100




西入口区域 B立面效果图

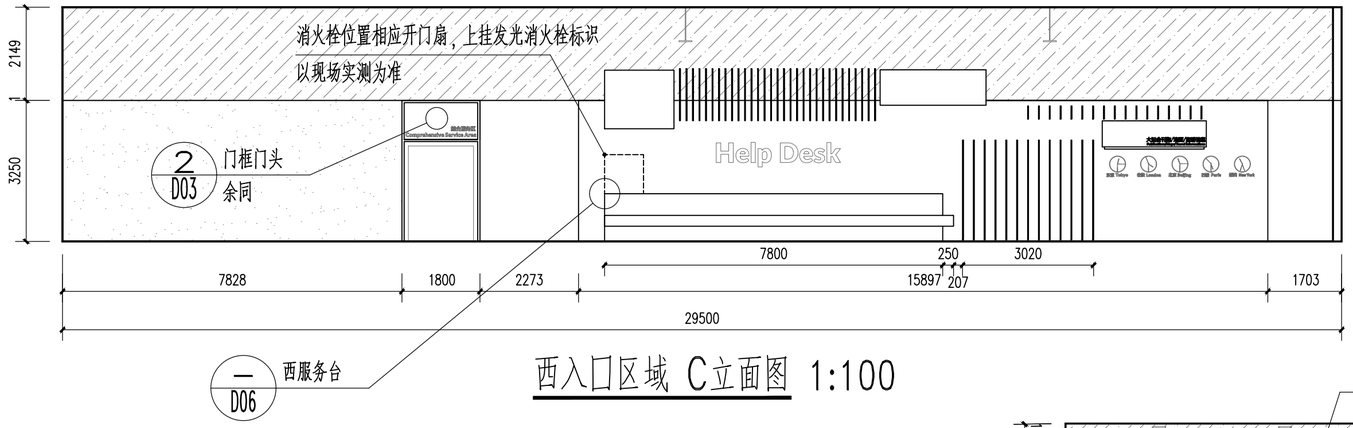


西入口区域 C立面图 1:100

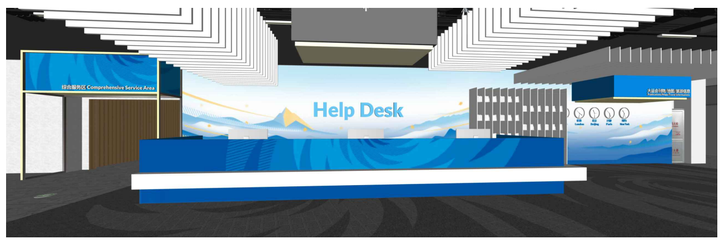

西入口区域 C立面效果图

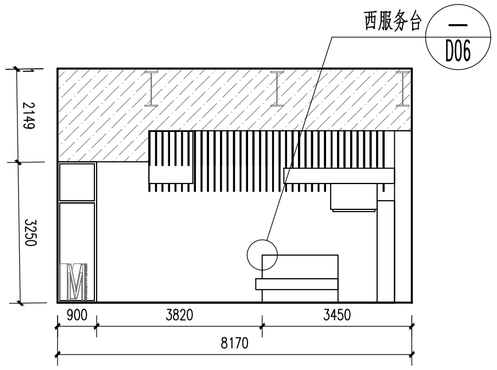

西入口区域 D立面图 1:100

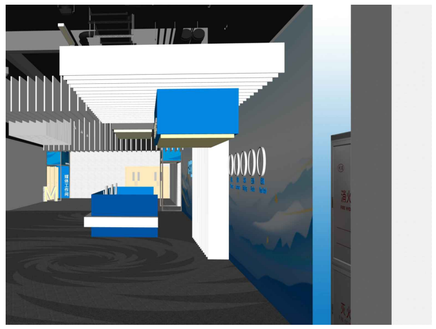

西入口区域 D立面效果图

出图记录 ISSUE NOTES

版本 REV.	日期 DATE	备注 REMARK
A	2022.02	

注册执业栏 REGISTERED ARCHITECT/ENGINEER

姓名: NAME

注册证书号码: REGISTRATION CERTIFICATE NO.

注册印章号码: STAMP NO.

设计号: CD-20212856-F001 JOB NO.

工程名称: PROJECT TITLE
成都大运会主新闻中心装饰搭建

子项名称: SUB ITEM

建设单位: CLIENT
成都博雅文瑞文化传播有限公司

图名: DRAWING TITLE
西入口区域立面图（一）

单位: UNIT	mm	图别 DWG. CATEGORY	室施
比例 SCALE	1:100	图号 DWG. NO.	E05
日期 DATE	2022.02	版本 VER. NO.	A

制图 DRAWN BY	方苓	
设计 DESIGNED BY	肖子颖	
校对 CHECKED BY	李潮文	
专业负责人 DISCIPLINE CHIEF	肖子颖	
设计总负责人 PROJECT CHIEF	张峻	
审核 AUDIT	张峻	
审定 APPROVED BY	华柯	

基准方中
成都基准方中建筑设计股份有限公司
Chengdu JZFZ Architectural Design Co., Ltd.
中国 成都市 琉璃路8号华润广场A座7-15楼
电话：+86(28) 86333800 传真：+86(28) 86582990
7-15F, Tower A, Criand Plaza, No.8,LiuLi Road, Chengdu, P.R.C
tel. +86(28) 86333800 fax. +86(28) 86582990
工程设计资质证书编号: A151016191

电子文档编号: - CAD FILENAME

版权说明
COPYRIGHT DECLARATION
此图版权为成都基准方中建筑设计股份有限公司所有，未经许可不得使用。