


采暖通风					
总图					

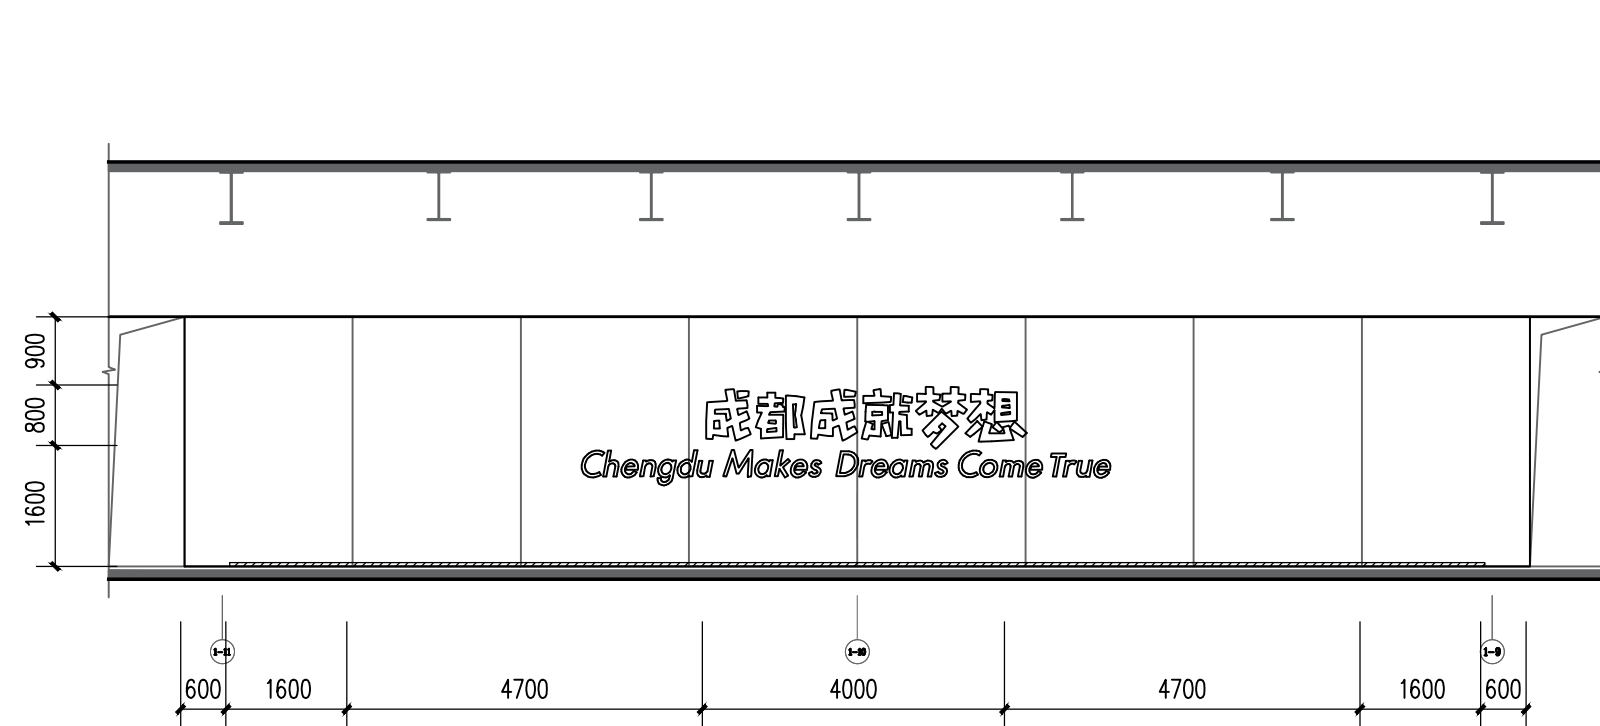


综合服务区 D立面图 1:100



综合服务区 D立面效果图



综合服务区 E立面效果图

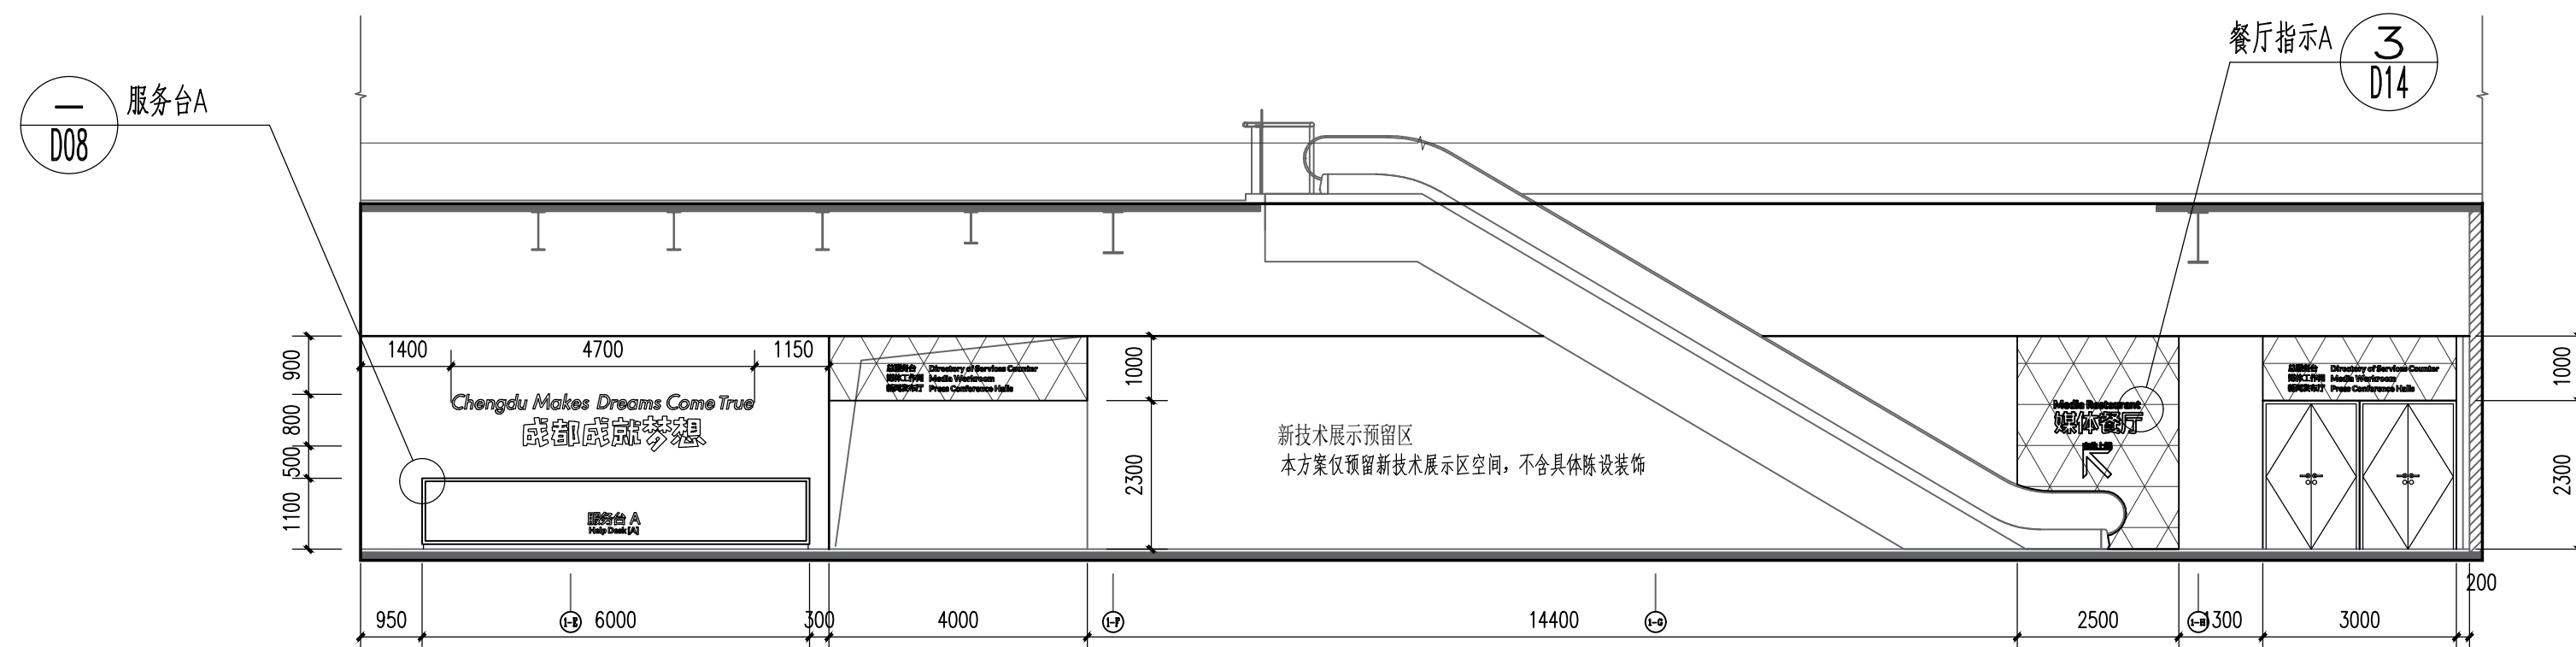

综合服务区 E立面图 1:100

出图记录						ISSUE NOTES	
版 本 REV.		日 期 DATE		备 注 REMARK			
A		2022.02					
注册执业栏 REGISTERED ARCHITECT/ENGINEER							
姓 名NAME							
注册证书号码REGISTRATION CERTIFICATE NO.							
注册印章号码STAMP NO.							
设计号：CD-20212856-F001JOB NO.							
工程名称PROJECT TITLE							
成都大运会主新闻中心装饰搭建							
子项名称SUB ITEM							
建设单位CLIENT 成都博雅文瑞文化传播有限公司							
图 名DRAWING TITLE							
综合服务区立面图（二）							
单 位mmUNIT		图 别室 施DWG. CATEGORY					
比 例1:100SCALE		图 号E08DWG. NO.					
日 期2022.02DATE		版 本AVER. NO.					
制 图DRAWN BY肖子颖							
设 计DESIGNED BY肖子颖							
校 对CHECKED BY李璐文							
专业负责人DISCIPLINE CHIEF肖子颖							
设计总负责人PROJECT CHIEF张峻							
审 核AUDIT张峻							
审 定APPROVED BY华柯							
园 基准方中 成都基准方中建筑设计股份有限公司Chengdu JZFF Architectural Design Co., Ltd. 中国 成都市 琉璃路9号华润广场A座7-15楼电话：+86(28) 86333800 传真：+86(28) 865829907-15F., Tower A, Crystal Plaza, No.8,LiuLi Road , Chengdu, P.R.Ctel.: +86(28) 86333800 fax:. +86(28) 86582990 工程设计资质证书编号：A151016191 CAD FILENAME电子文档编号：— 版 权 说 明COPYRIGHT DECLARATION 此图版权为成都基准方中建筑设计股份有限公司所有，未经许可不得使用。							