







媒体餐厅 A 立面效果图

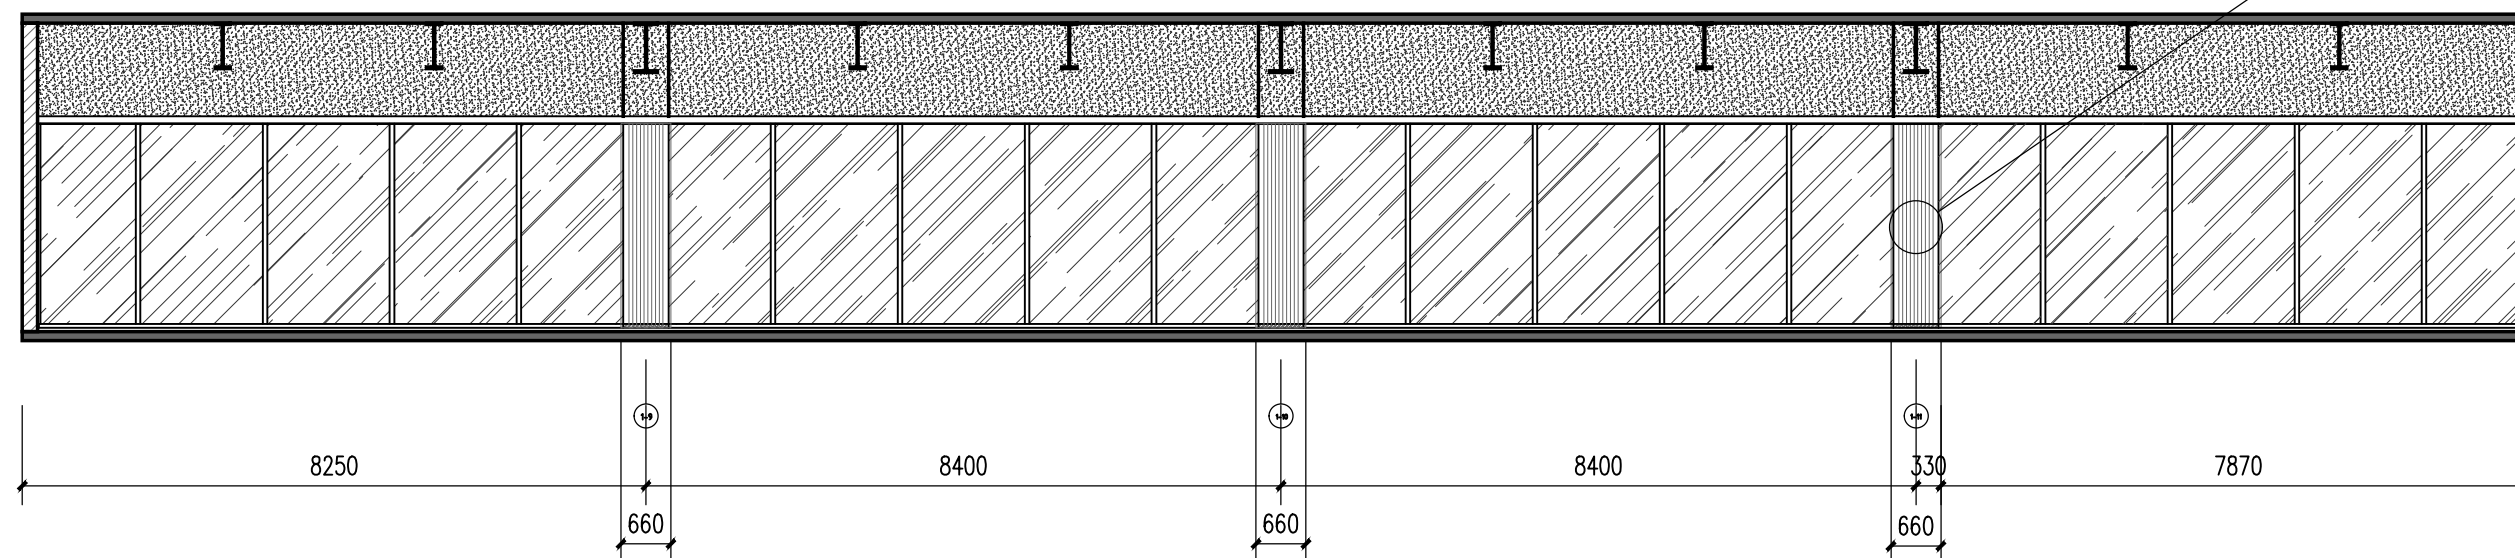



媒体餐厅 A立面图 1:100

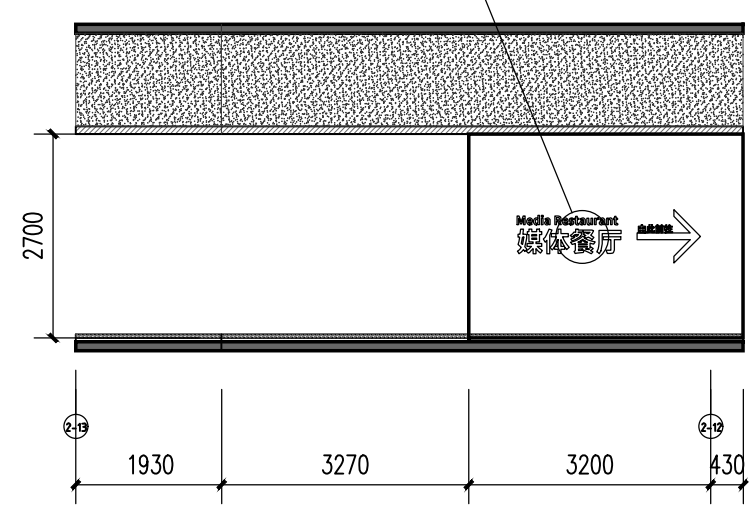



媒体餐厅 B立面图 1:100

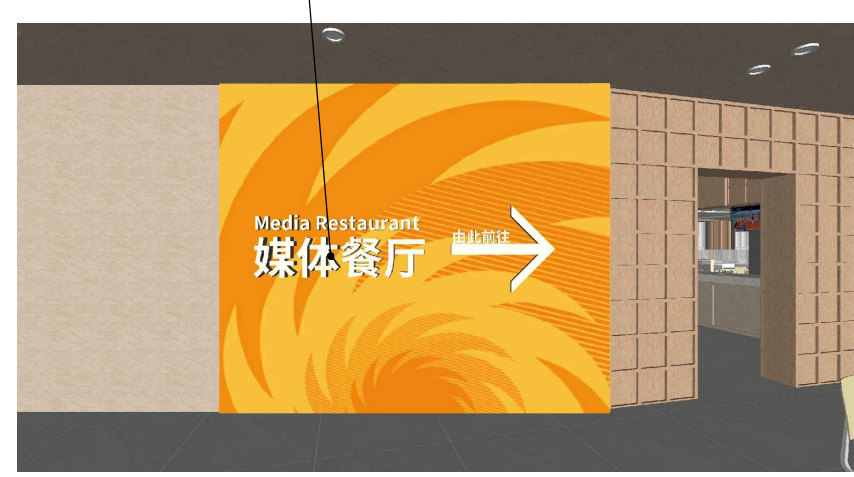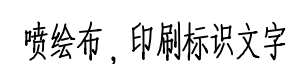


媒体餐厅 B立面效果图

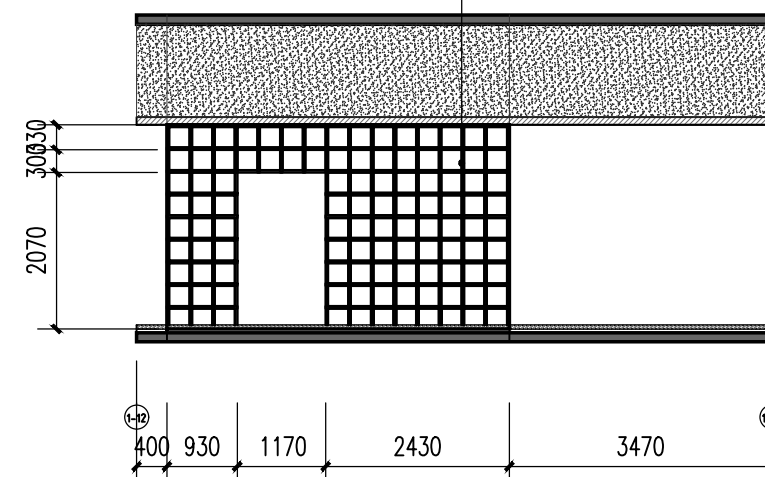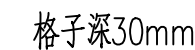


媒体餐厅 C立面图 1:100

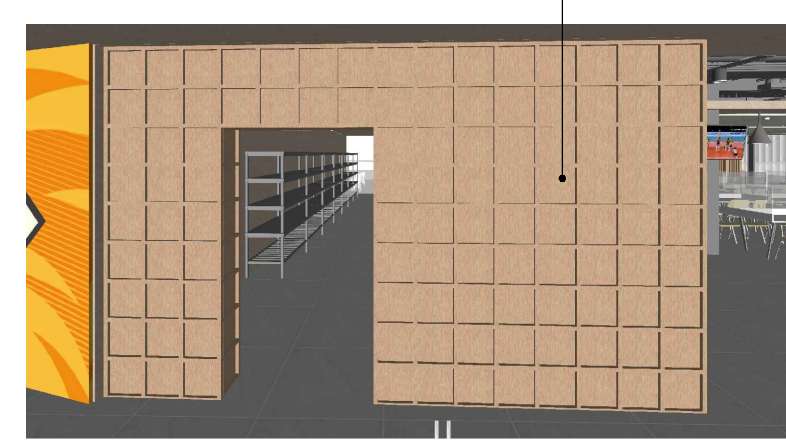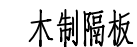

媒体餐厅 C立面效果图

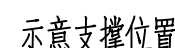

根据餐饮服务提供商窗口需求调整支撑位置与数量

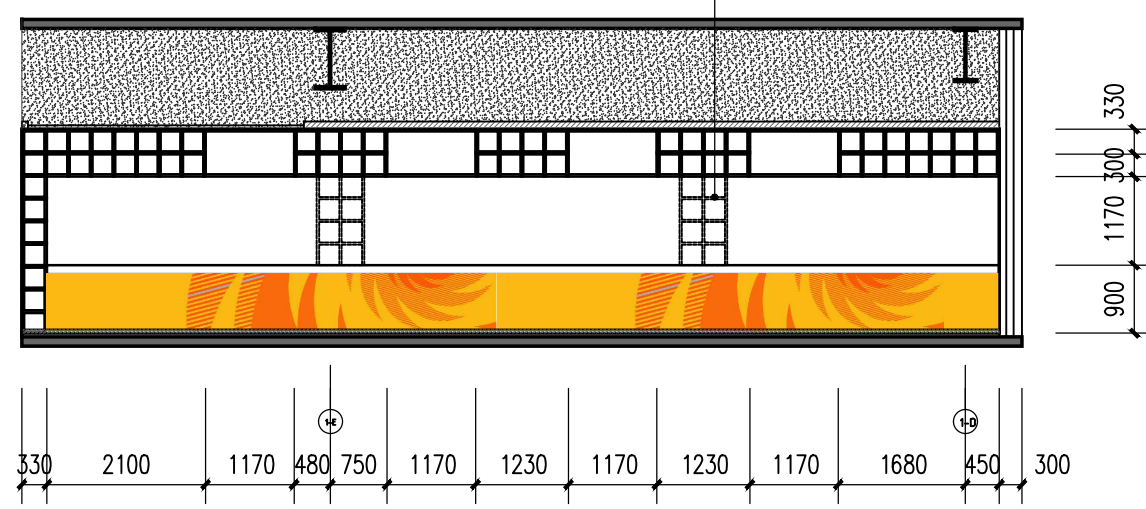

媒体餐厅 D立面图 1:100



媒体餐厅 D立面效果图

出图记录			ISSUE NOTES		
版 本 REV.	日 期 DATE	备 注 REMARK			
A	2022.02				
注册执业栏			REGISTERED ARCHITECT/ENGINEER		
姓 名			NAME		
注册证书号码			REGISTRATION CERTIFICATE NO.		
注册印章号码			STAMP NO.		
设计号			JOB NO.		
CD-20212856-F001					
工程名称			PROJECT TITLE		
成都大运会主新闻中心装饰搭建					
子项名称			SUB ITEM		
建设单位			CLIENT		
成都博雅文瑞文化传播有限公司					
图 名			DRAWING TITLE		
媒体餐厅立面图（一）					
单 位	mm	UNIT	图 别	室 施	DWG. CATEGORY
比 例	1:100	SCALE	图 号	E09	DWG. NO.
日 期	2022.02	DATE	版 本	A	VER. NO.
制 图	雷鑫鹏				
设 计	雷鑫鹏				
校 对	李耀文				
专业负责人	肖子颖				
设计总负责人	张竣				
审 核	张竣				
审 定	华轲				
成都基准方中建筑设计股份有限公司 Chengdu JZJZ Architectural Design Co., Ltd.					
中国 成都市 琉璃路8号华润广场A座7-15楼 电话: +86 (28) 86333800 传真: +86 (28) 86582990 7-15F, Tower A, Oriental Plaza, No.8, Liuli Road, Chengdu, P.R.C tel. +86(28) 86333800 fax. +86(28) 86582990					
工程注册资质证书编号: A151016191					
电子文档编号: - CAD FILENAME					
版 权 说 明 COPYRIGHT DECLARATION					
此图版权为成都基准方中建筑设计股份有限公司所有, 未经许可不得使用。					