


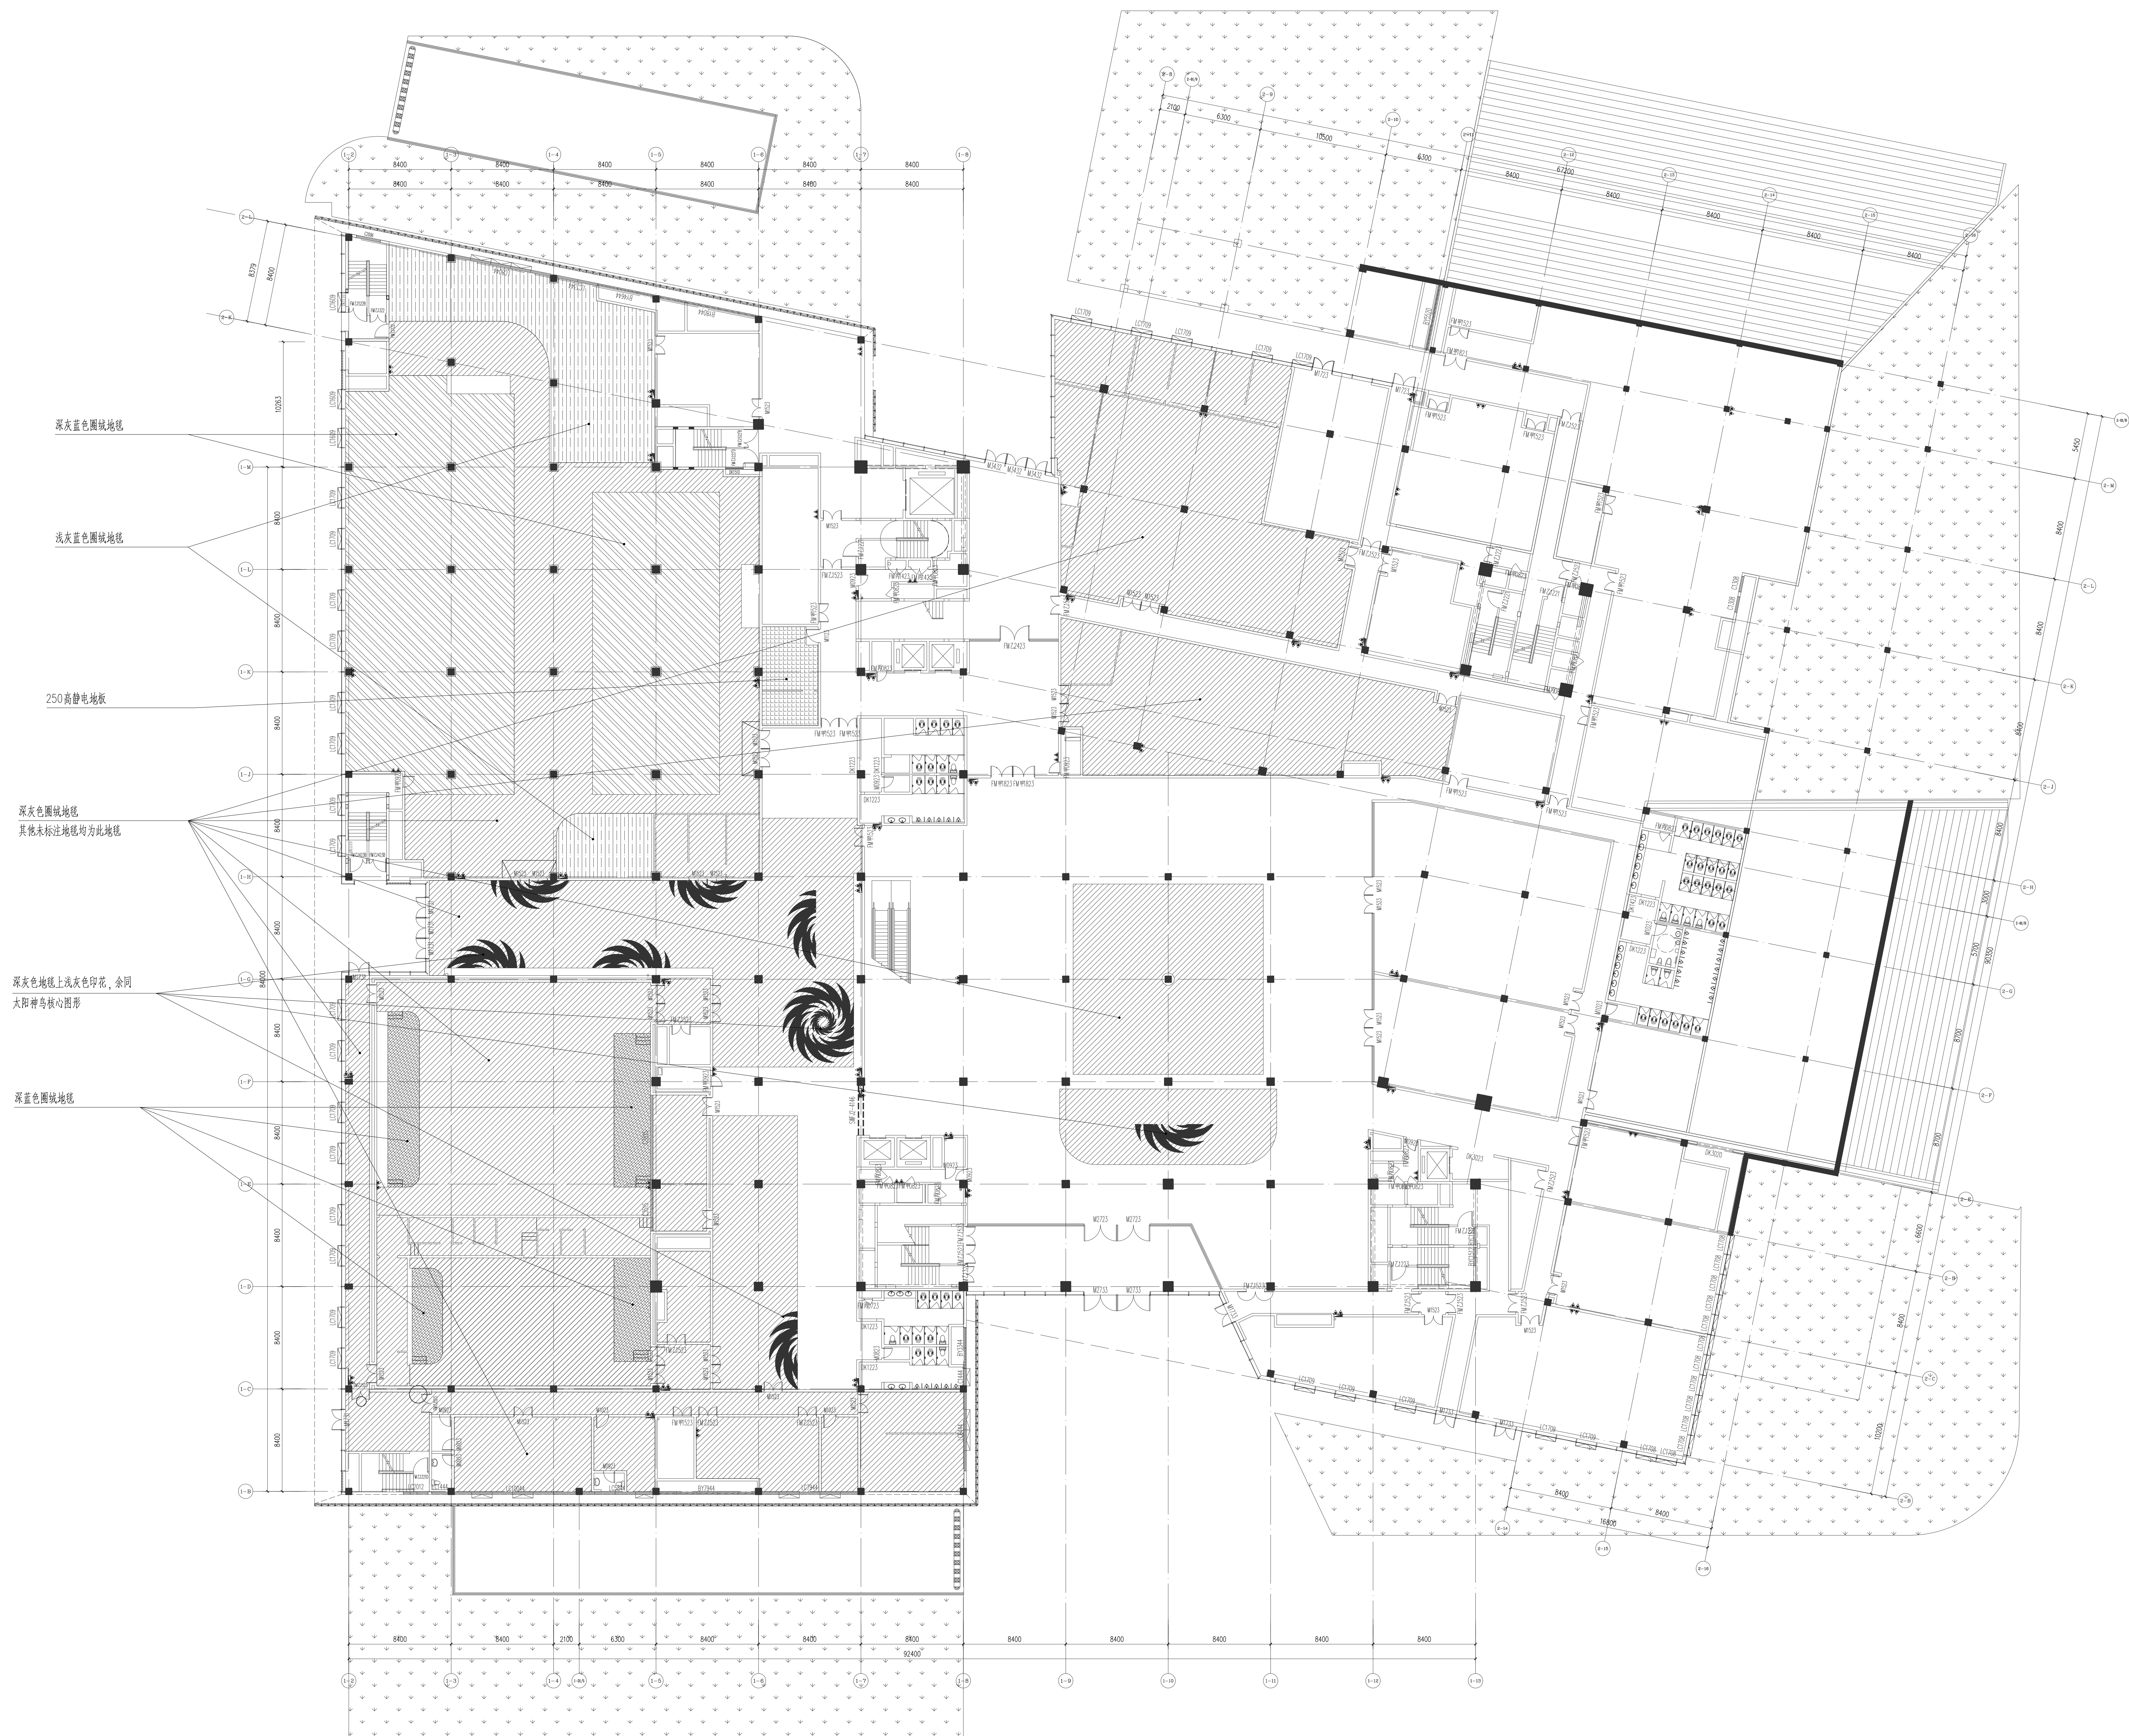

一层地面铺装图 1:200

[illegible]

注册执业栏		REGISTERED ARCHITECT (ENR)
姓 名	NAME	
注册证书号码	REGISTERED NUMBER (ENR)	
注册印章号码	STAMP NO.	
设计号	CD-20212856-F001	DESIGN NO.
工程名称	PROJECT TITLE	
成都大运会议中心装饰搭建		
子项名称	SUB TITLE	
建设单位	CLIENT	
成都博雅文瑞文化传播有限公司		
图 名	DRAWING TITLE	

一层地面铺装表图					
单位	mm	DWG	图名	DWC-02(2/2)	
比例	1:200	SCALE	图号	F01	DWG NO.
日期	2022.02	DATE	版本	A	REV. NO.
制图 DRAWN BY	陈子颖				
设计 DESIGNED BY	陈子颖				
校对 CHECKED BY	李敏文				
专业负责人 SPECIALIST CHECK	陈子颖				
设计阶段负责人 PROJECT CHIEF	张竣				
审核 APPROVED	张竣				
审批人 APPROVED BY	余树				

基准方中
成都基准方中建筑设计股份有限公司
Chengdu JZFZ Architectural Design Co., Ltd.

中国 成都市 民权路8号华兴广场A座7-14楼
电话: +86(28) 86533000 传真: +86(28) 86582990
7-15F, Tower A, Citrad Plaza, No.8Jialin Road, Chengdu, P.R.C
Tel: +86(28) 86533000 fax: +86(28) 86582990

工程设计资质证书编号: A151016191

版 权 说 明
COPYRIGHT DECLARATION

此图版权为成都基准方中建筑设计股份有限公司所有,未经许可不得使用。