


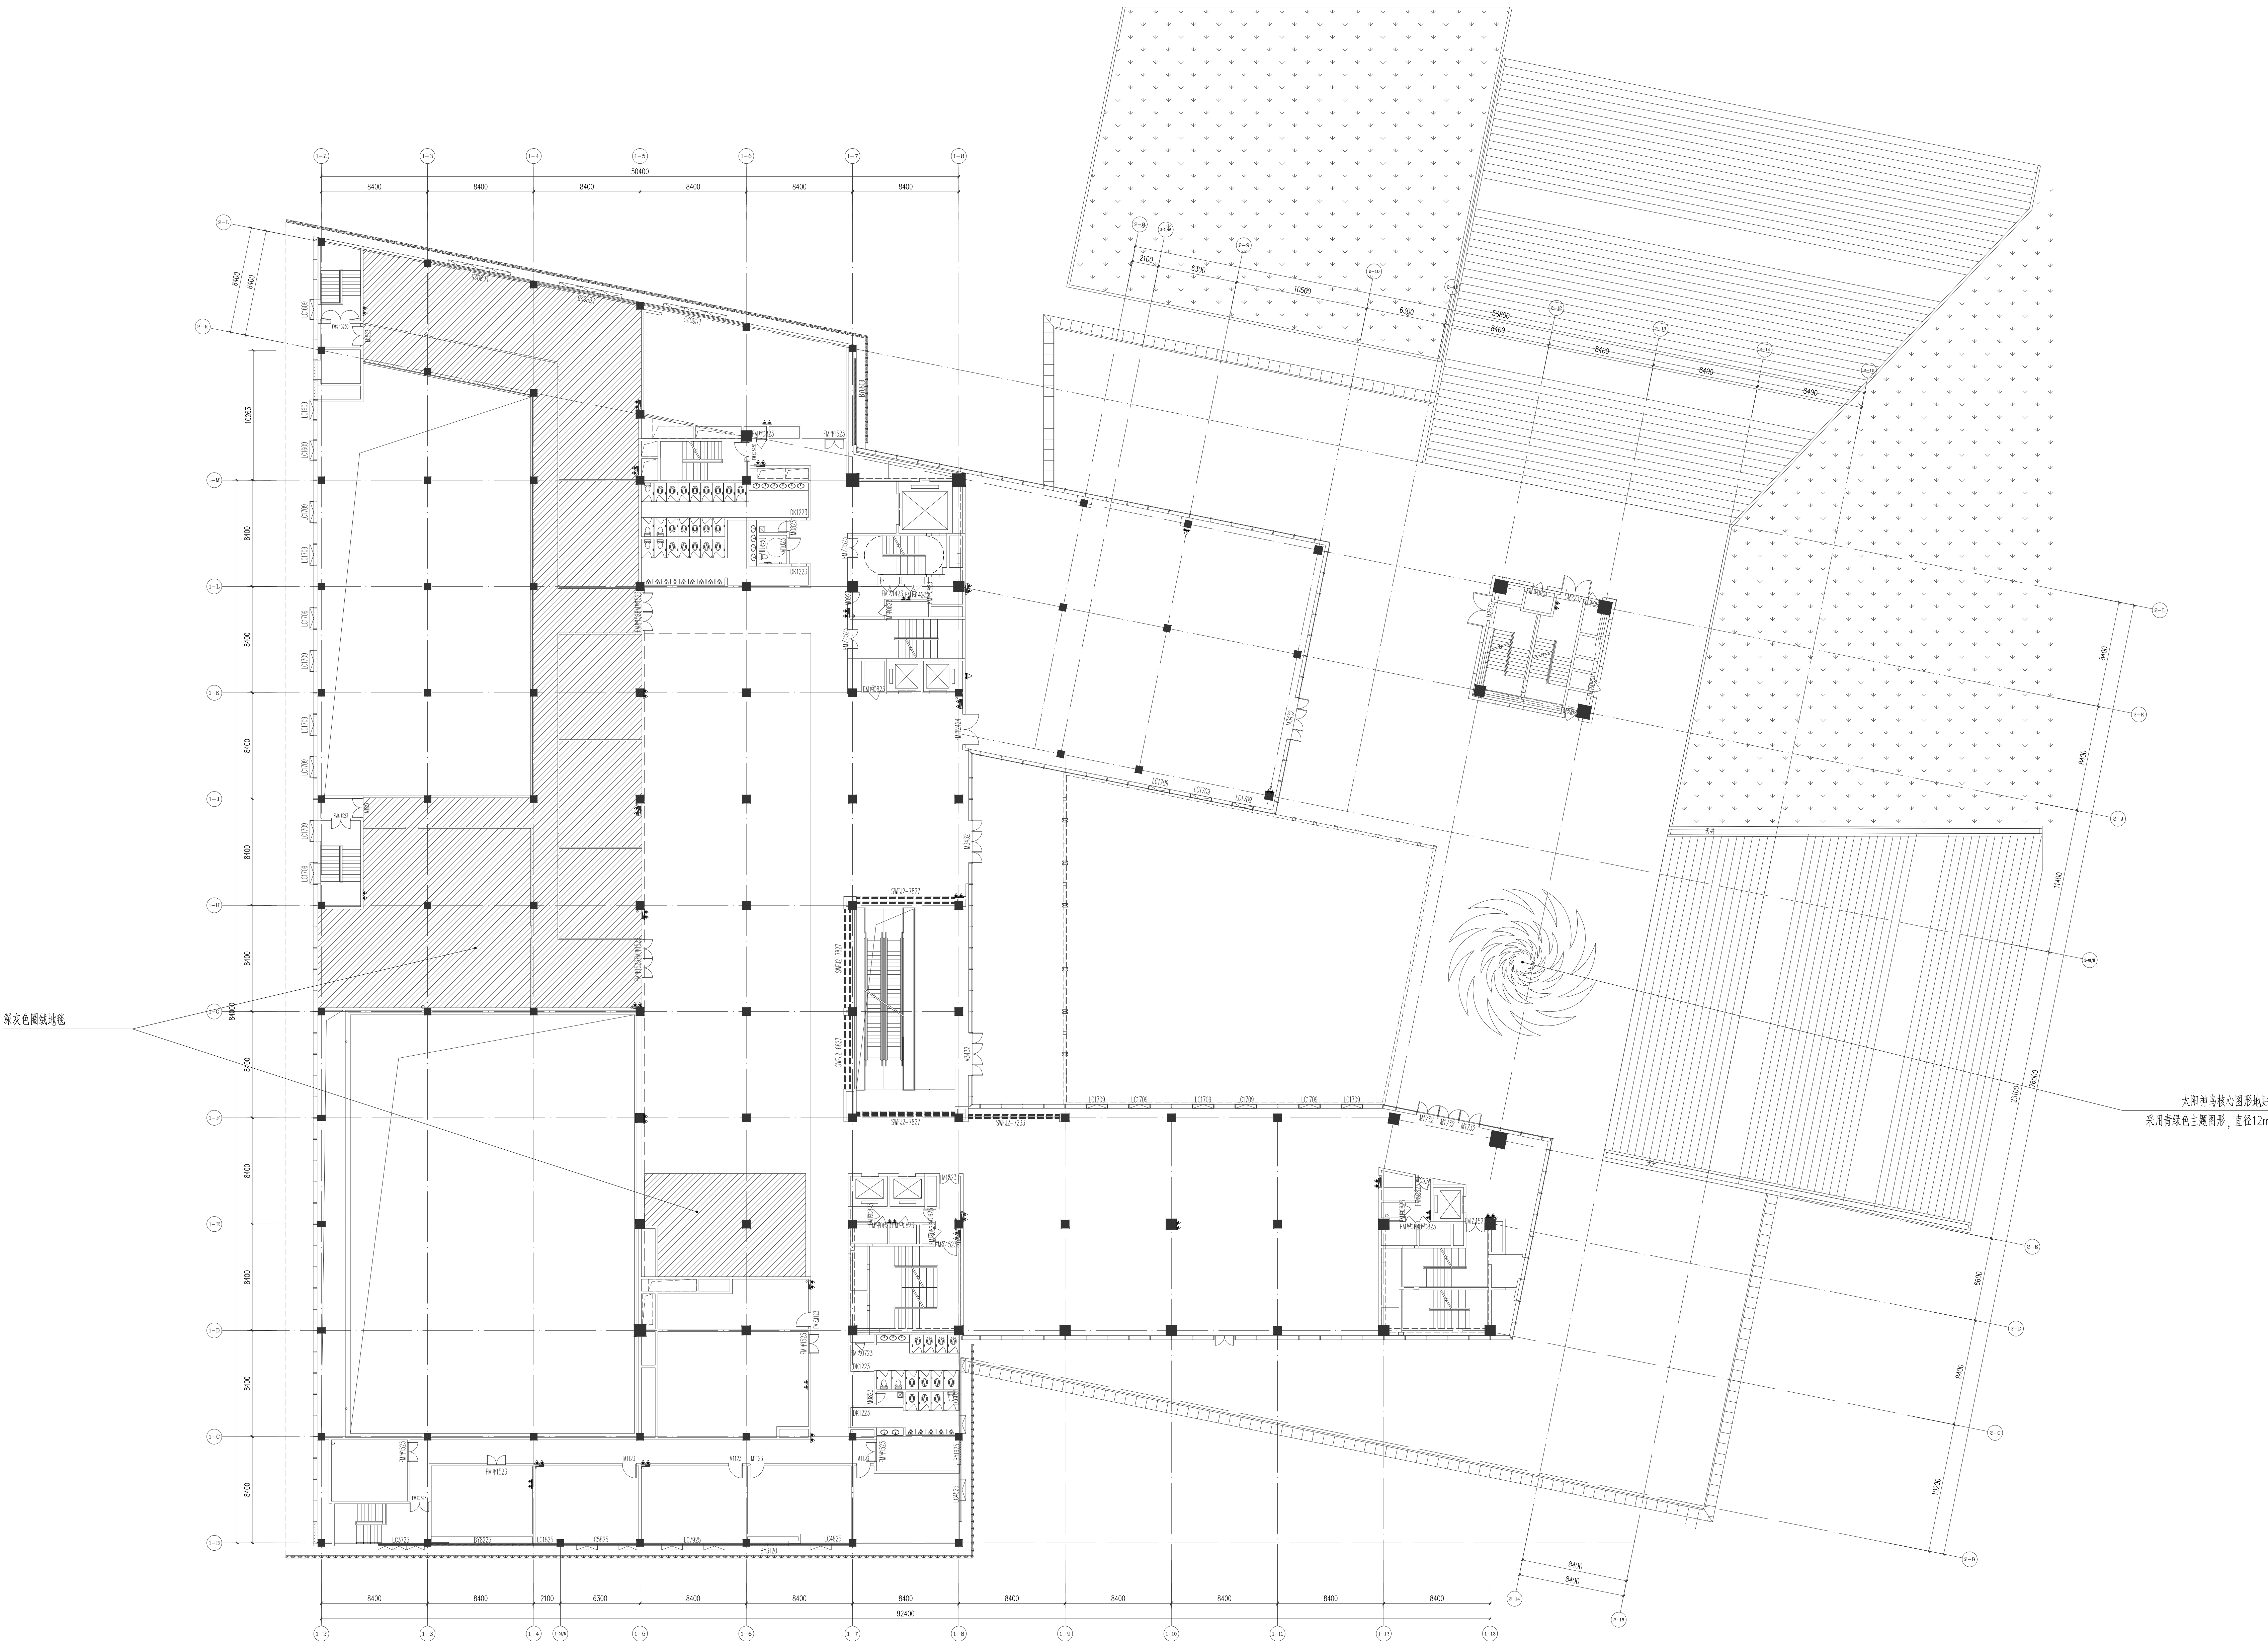

二层地面铺装图 1:200

平面示图: 01/14

图例记录		ISSUE NOTES	
版本	日期	名称	备注
A	2022.02		

注册执业栏		REGISTERED ARCHITECT (DAPAD)
姓名	NAME	
注册证书号	REGISTERED ARCHITECT NO.	
注册执业单位	REGISTERED UNIT	
设计人	DESIGNER	
审核人	CHECKER	
项目负责人	PROJECT LEAD	
专业名称	SPECIALTY	

注册执业栏		REGISTERED ARCHITECT (DAPAD)
姓名	NAME	
注册证书号	REGISTERED ARCHITECT NO.	
注册执业单位	REGISTERED UNIT	
设计人	DESIGNER	
审核人	CHECKER	
项目负责人	PROJECT LEAD	
专业名称	SPECIALTY	

注册执业栏		REGISTERED ARCHITECT (DAPAD)
姓名	NAME	
注册证书号	REGISTERED ARCHITECT NO.	
注册执业单位	REGISTERED UNIT	
设计人	DESIGNER	
审核人	CHECKER	
项目负责人	PROJECT LEAD	
专业名称	SPECIALTY	

注册执业栏		REGISTERED ARCHITECT (DAPAD)
姓名	NAME	
注册证书号	REGISTERED ARCHITECT NO.	
注册执业单位	REGISTERED UNIT	
设计人	DESIGNER	
审核人	CHECKER	
项目负责人	PROJECT LEAD	
专业名称	SPECIALTY	

成都基准方中建筑设计股份有限公司
Chengdu JZTZ Architectural Design Co., Ltd.