


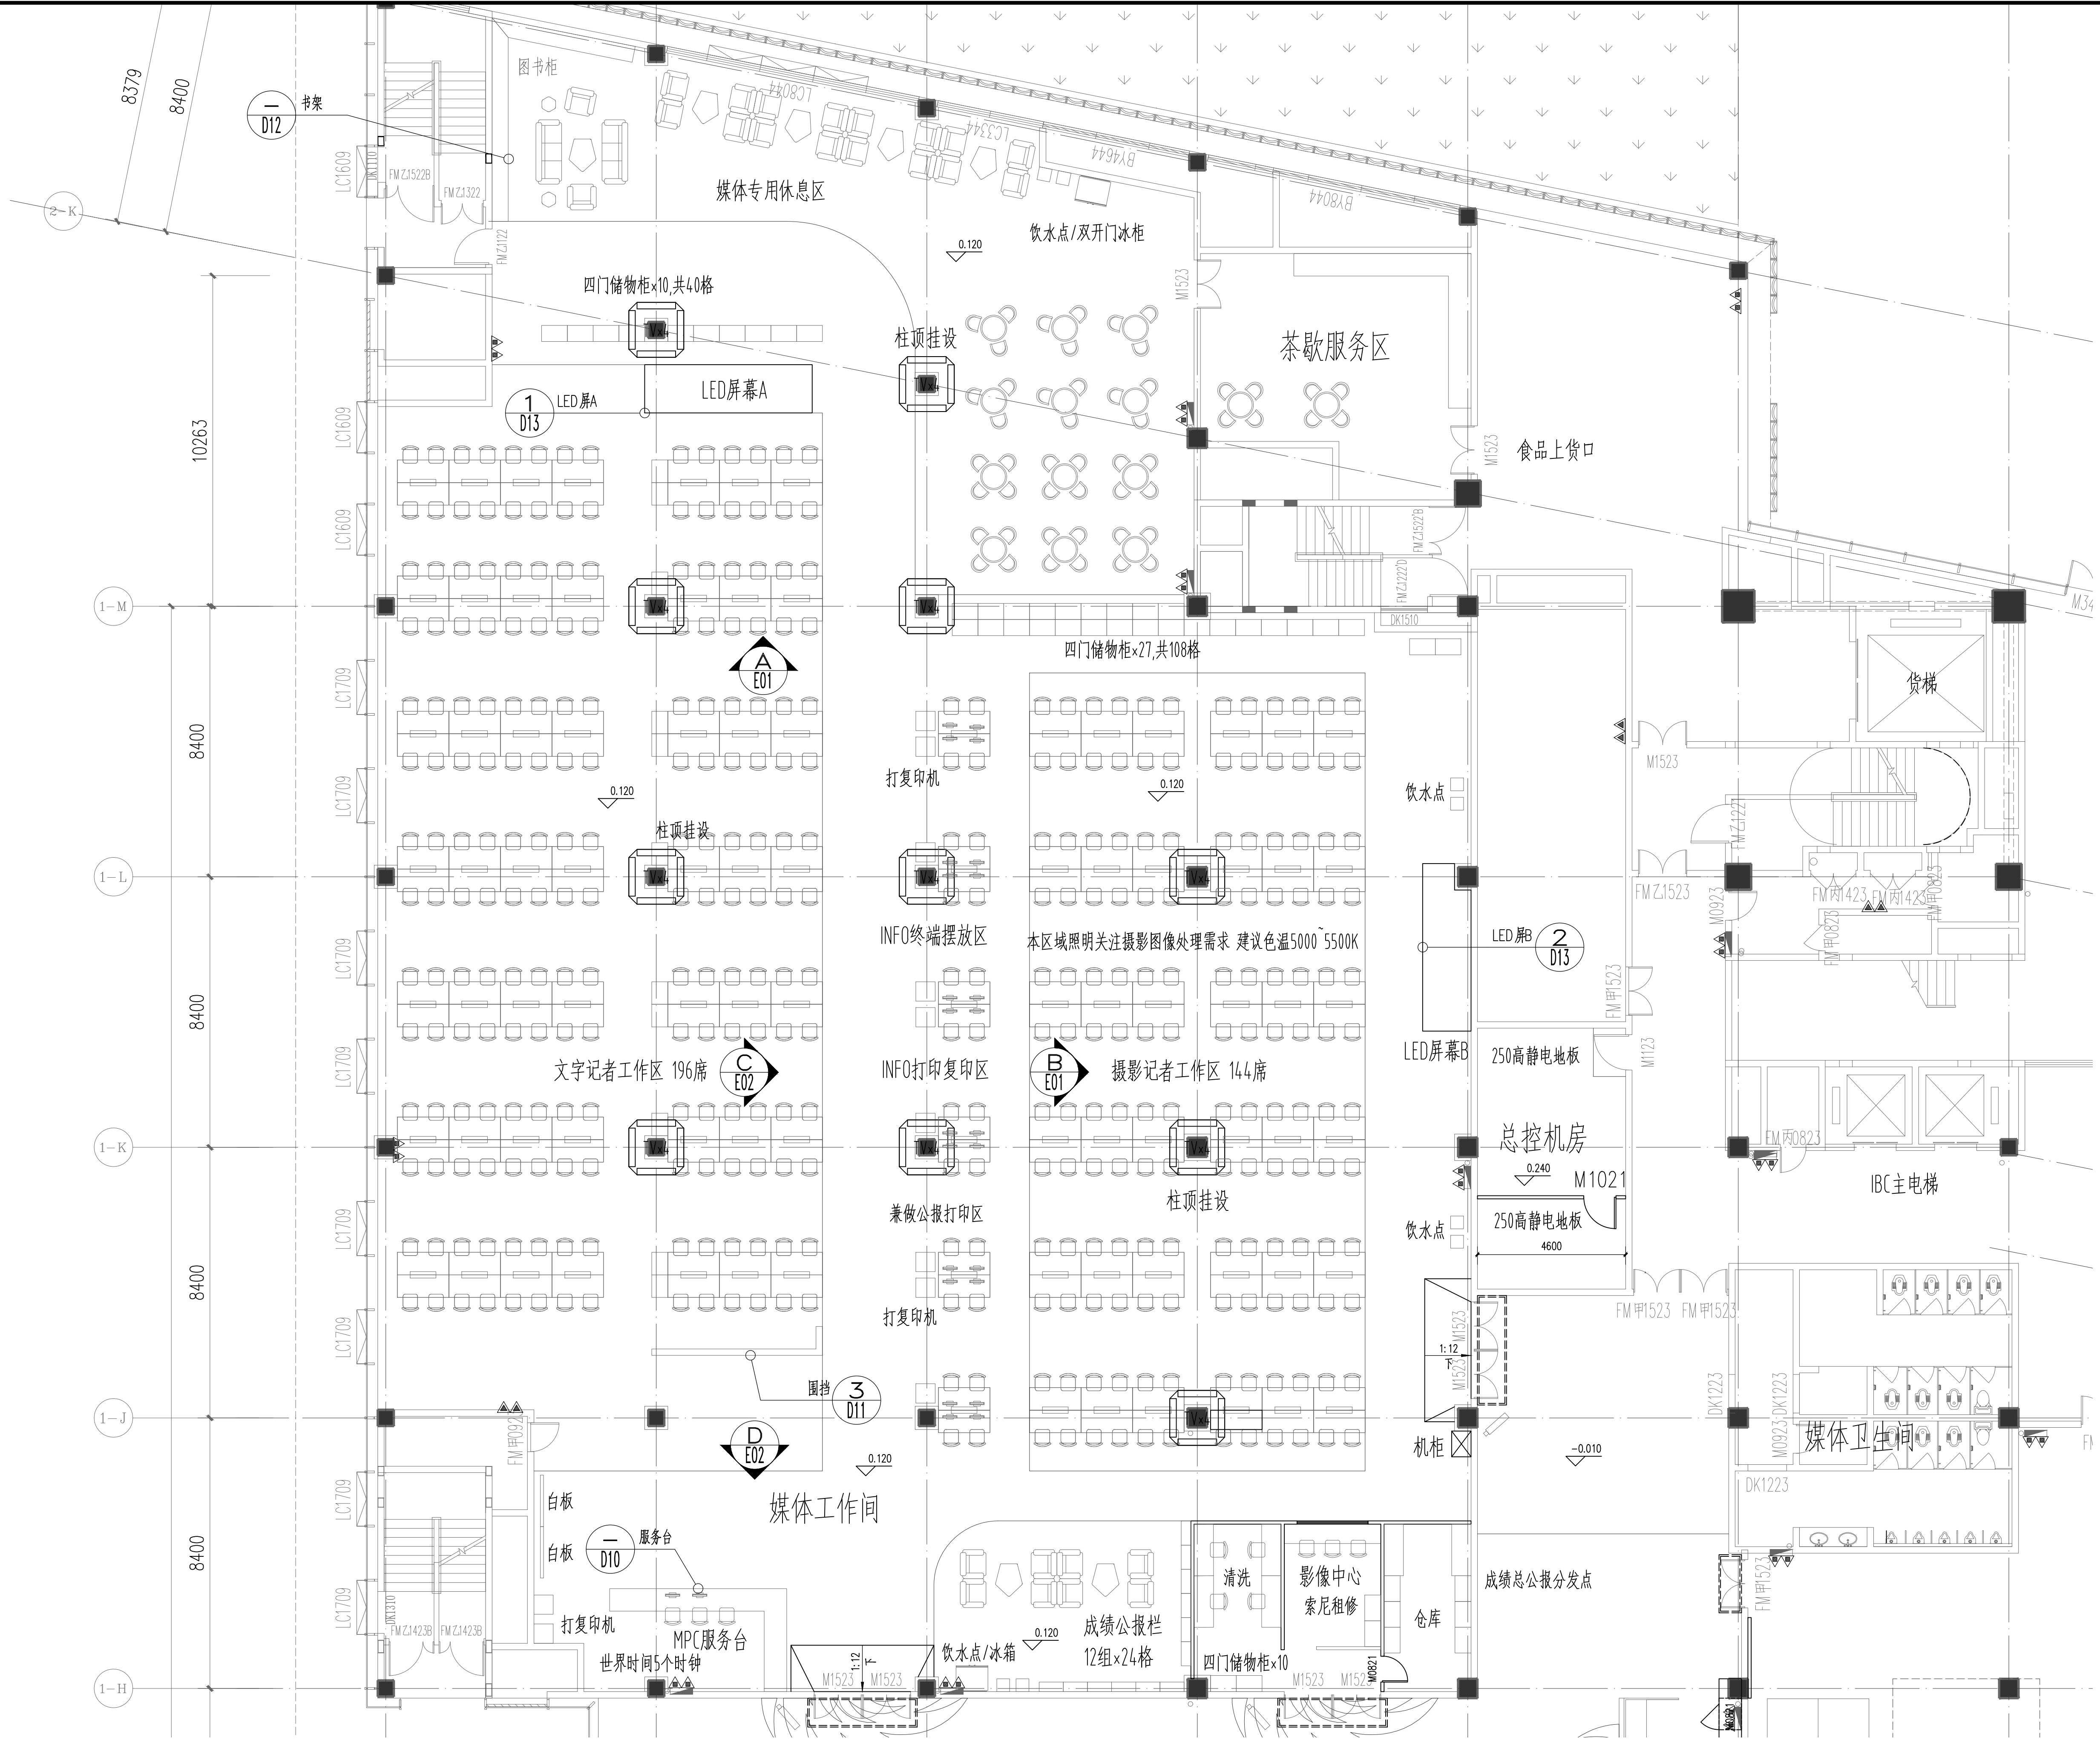

媒体工作间放大平面图 1:100

平面示意图		KEY PLAN	
注册执业栏		REGISTERED ARCHITECT/ENGINEER	
姓 名		NAME	
注册证书号码		REGISTRATION CERTIFICATE NO.	
注册印章号码		STAMP NO.	
设计号		JOB NO.	
工程名称		PROJECT TITLE	
事项名称		SUB-TITLE	
建设单位		CLIENT	
图 名		DRAWING TITLE	
单 位		UNIT	
比 例		SCALE	
日 期		DATE	
图 号		DRAWING NO.	
版 本		VERSION	
设 计		DESIGNED BY	
校 对		CHECKED BY	
专业负责人		DISCIPLINE CHIEF	
设计总负责人		PROJECT CHIEF	
审 核		REVIEWED BY	
审 定		APPROVED BY	
工程设计资质证书编号		A151016191	
电子文档编号		CDD FILENAME	
版 权 说 明		COPYRIGHT DECLARATION	
此图版权归成都基准方中建筑设计股份有限公司所有，未经许可不得使用。			