


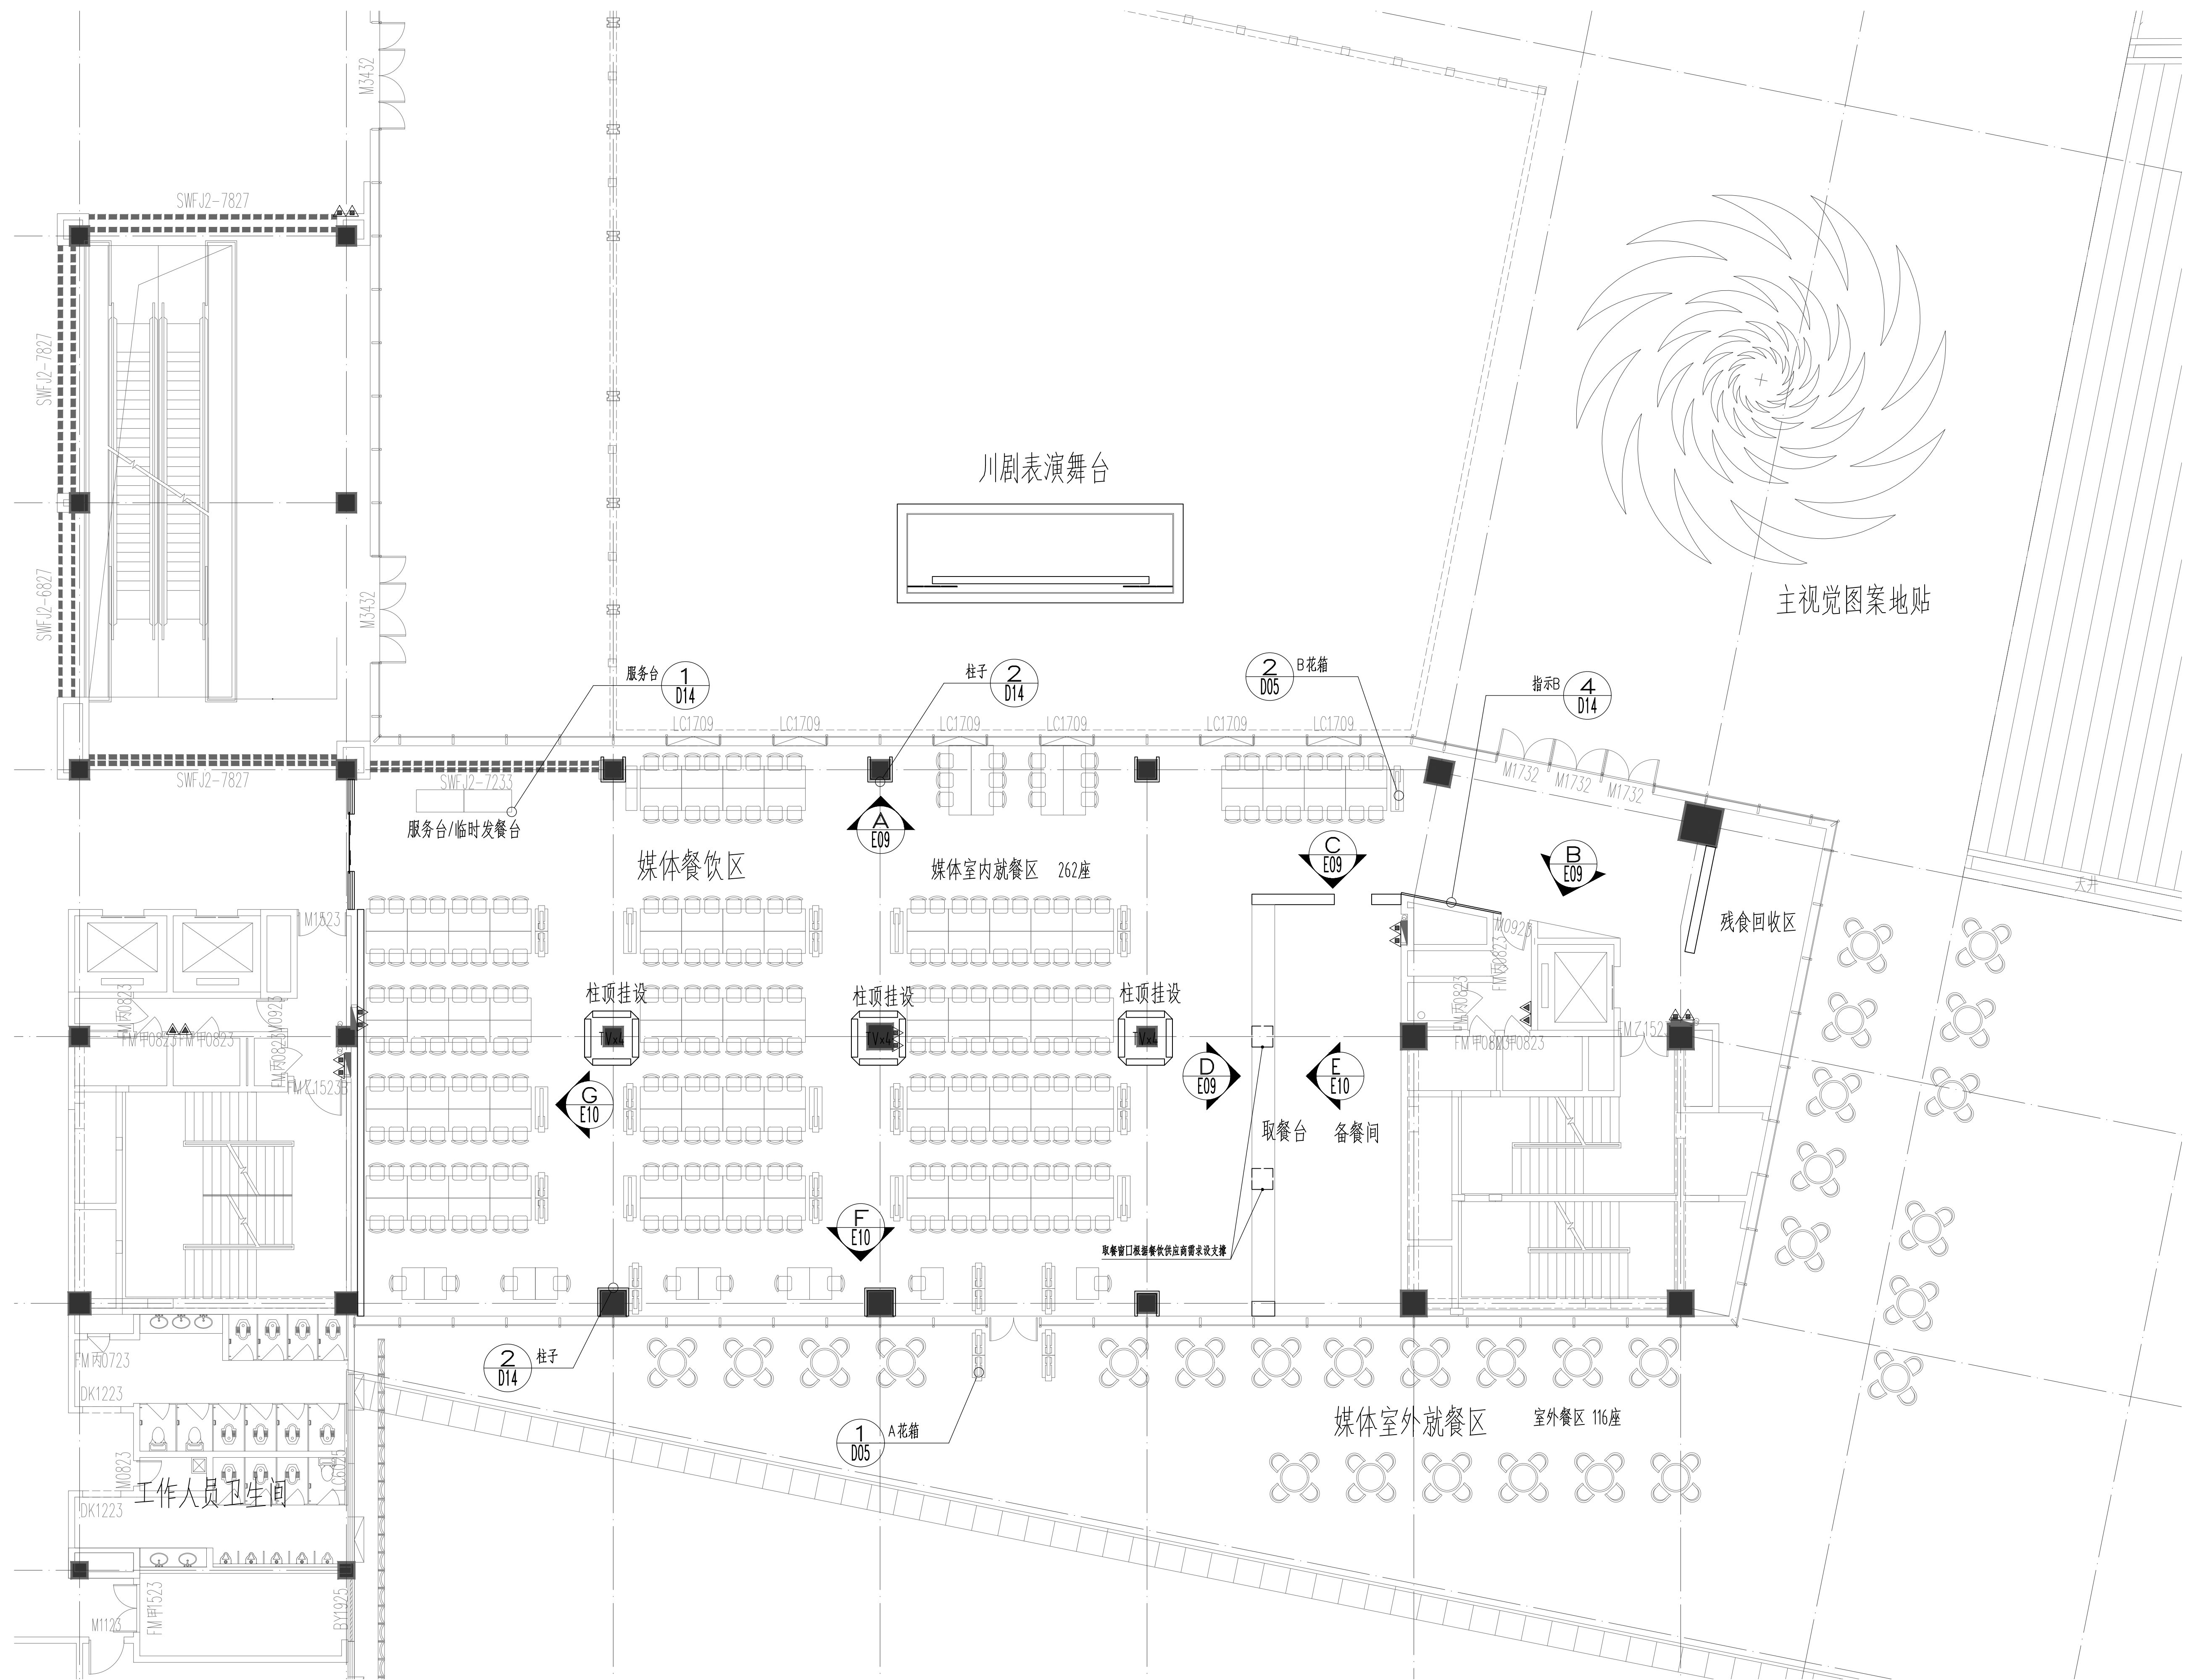

媒体餐厅放大平面图 1:100

平面示意: KEY PLAN

[illegible]

注册执业栏		REGISTERED ARCHITECT/ENGINEER
姓 名	NAME	
注册证书号码	REGISTRATION CERTIFICATE NO.	
注册印章号码	STAMP NO.	
设计号	CD-20212856-F001	JOB NO.
工程名称	PROJECT TITLE	
成都大运会主新闻中心装饰搭建		
子项名称	SUB ITEM	
建设单位	CLIENT	
成都博雅文瑞文化传播有限公司		
图 名	DRAWING TITLE	

单位	mm	UNIT	图 纸	室 施	DWG. CATEGORY
比例	1:100	SCALE	图 号:	MO4	DWG. NO.
日 期	2022.02	DATE	版 本	A	REV. NO.
制 图	肖子颖				
DRAWN BY	肖子颖				
设 计	肖子颖				
DESIGNED BY	肖子颖				
校 对	李璐文				
CHECKED BY	肖子颖				
专业负责人					
DISCIPLINE CHIEF					
设计总负责人	张峻				
PROJECT CHIEF	张峻				
审 核	张峻				
AUDIT	张峻				
审 定	华树				
APPROVED BY	华树				

基准方中

成都基准方中建筑设计股份有限公司
Chengdu JZfz Architectural Design Co., Ltd.

中国 成都市 琉璃路8号华润广场A座7-15楼
电话: +86 (28) 86333800 传真: +86 (28) 86582990
7-15F, Tower A, Citland Plaza, No.8, Liuli Road, Chengdu, P.R.C

工程设计资质证书编号: A151016191

电子文档编号: — CAD FILENAME

版 权 说 明
COPYRIGHT DECLARATION

此图版权为成都基准方中建筑设计股份有限公司所有，未经许可不得使用。