


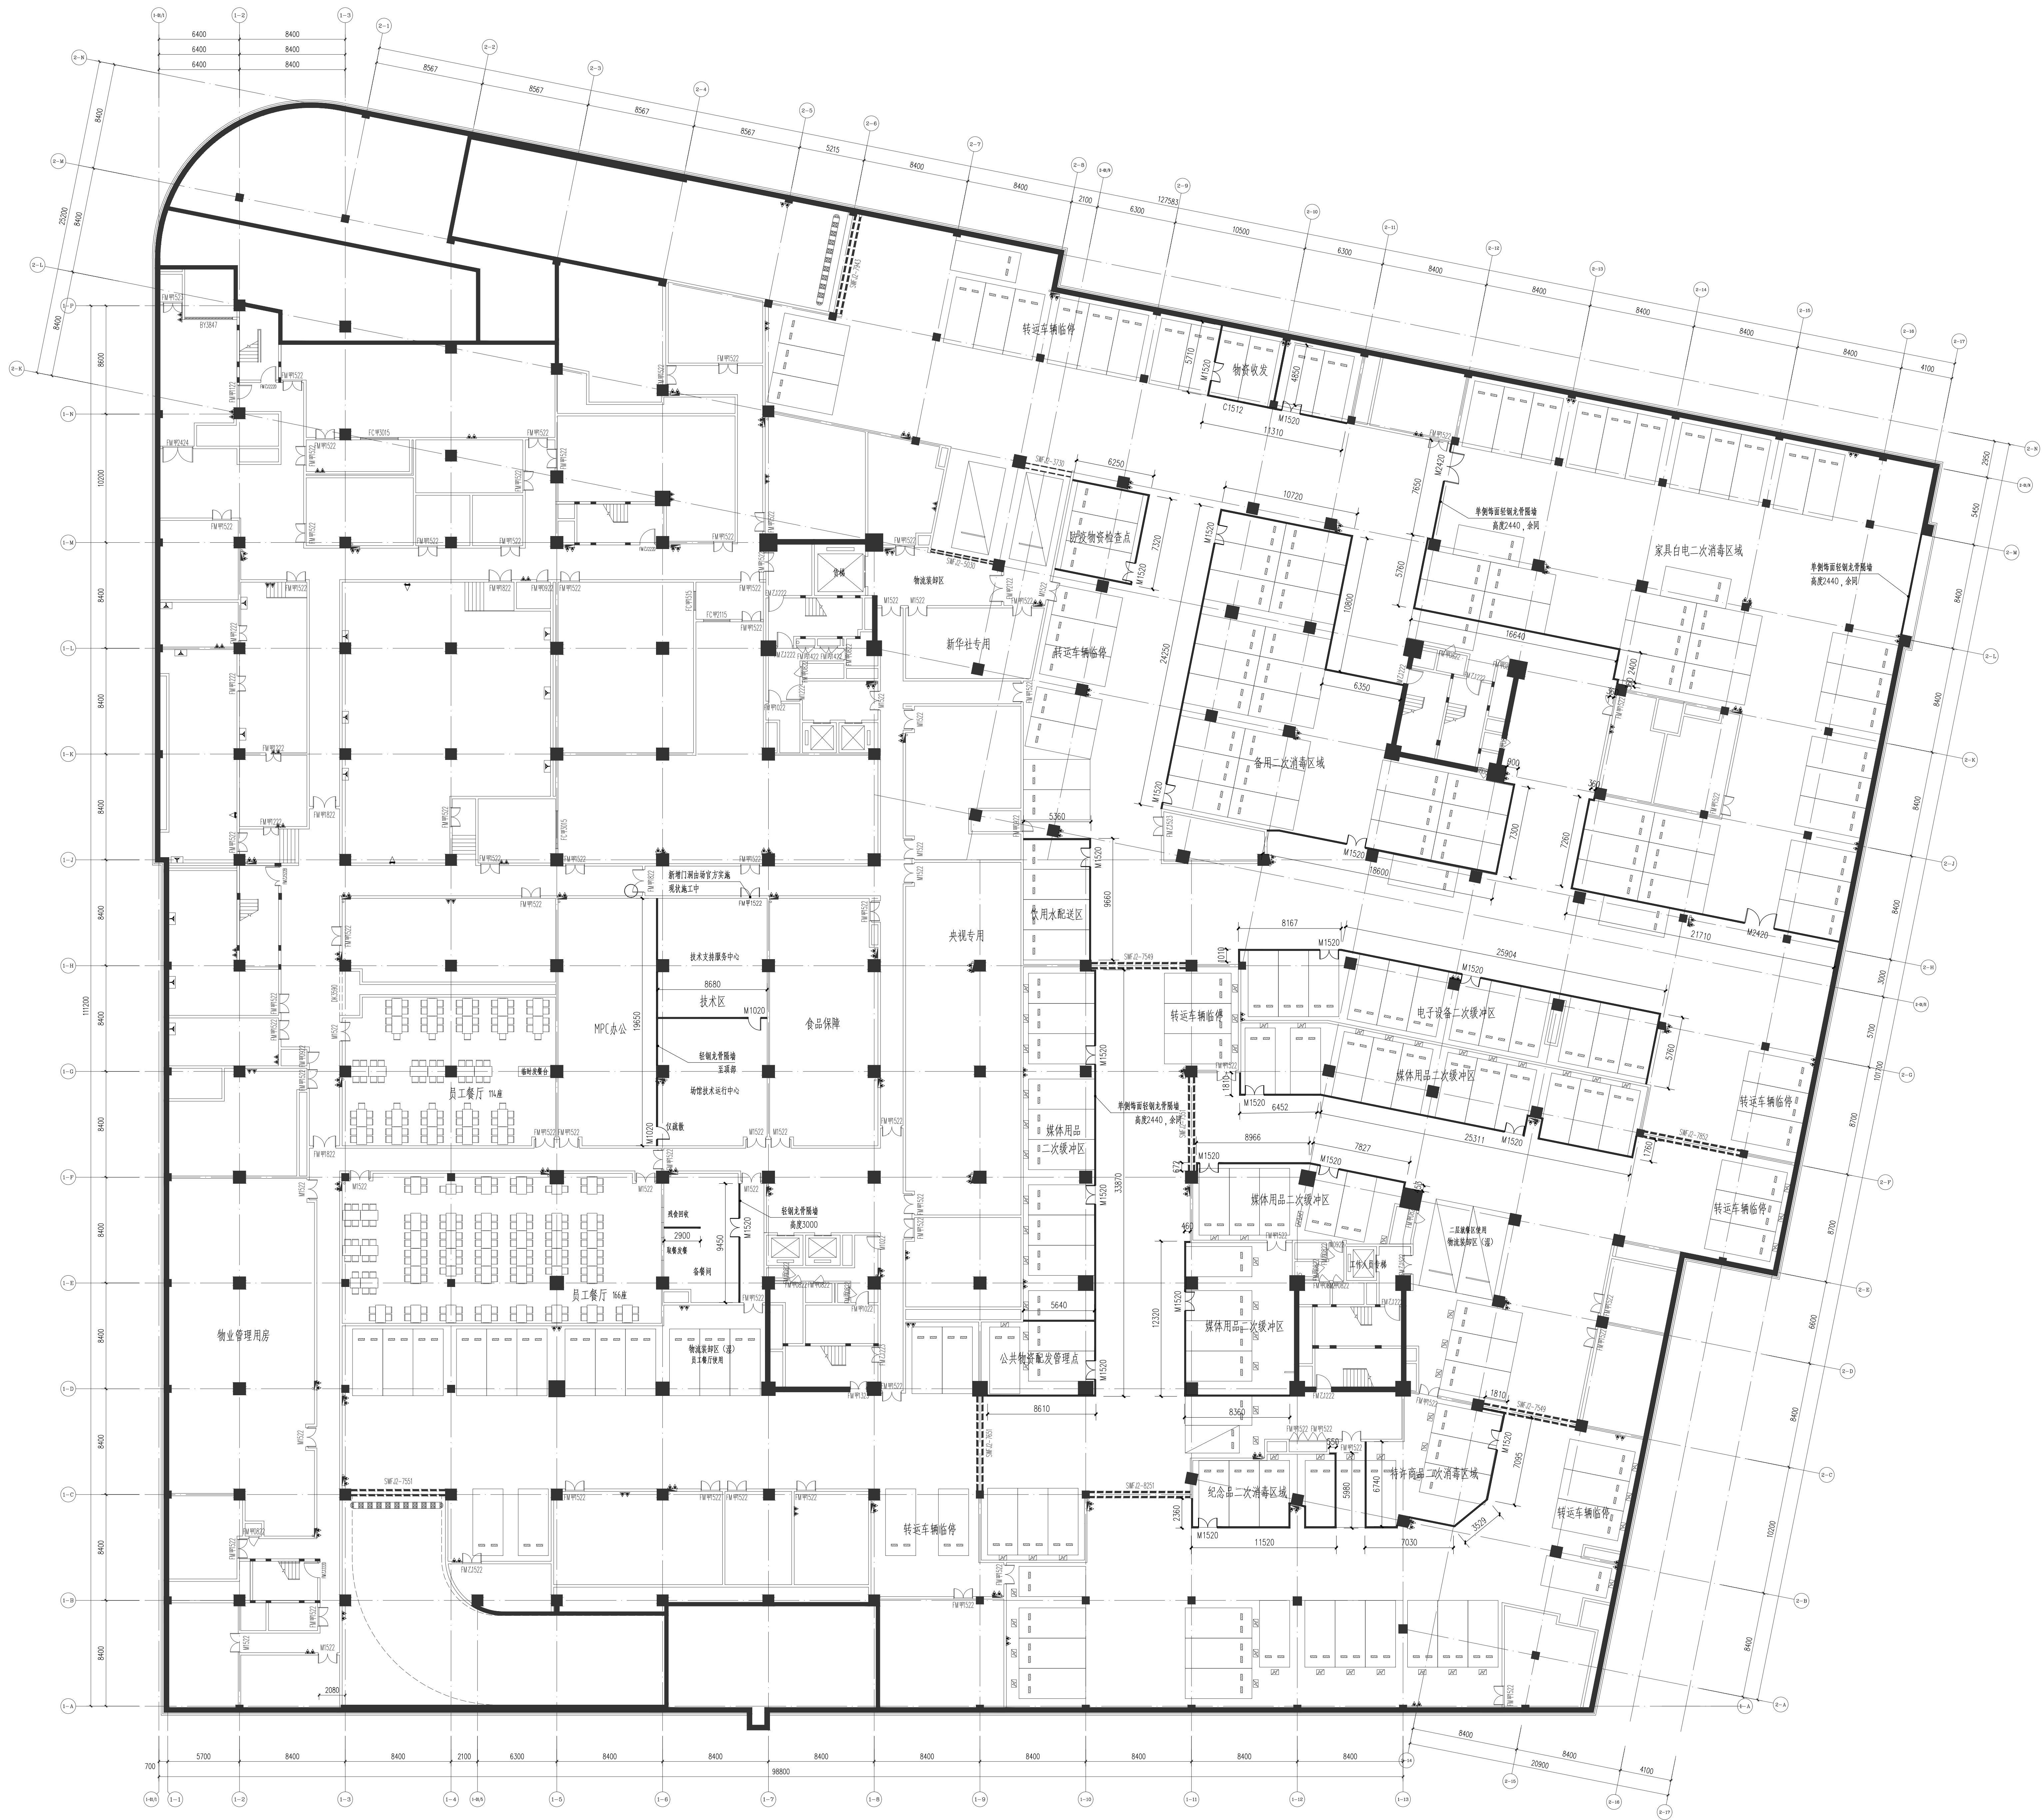

负一层平面布置图 1:200

[illegible]

注册执业栏	REGISTERED ARCHITECT/ENGINEER
姓名	NAME
资质证书号码	REGISTERED NO. (CERTIFICATE NO.)
注册印章号码	STAMP NO.
号: CD-20212856-F001	NO.
成都大运会主新闻中心装饰搭建	PROJECT TITLE
负责人	SUB ITEM
及单位	CLIENT
成都博雅文瑞文化传播有限公司	
表	DRAWING TITLE

负一层平面布置图					
位	mm	UNIT	附注	备注	DWG CATEGORY
比例	1:200		图号	P-01	DWG NO.
日期	2022.02	DATE	版本	A	REV. NO.
设计	陈子耀				
校核	陈子耀				
审核	李露文				
专业负责人	陈子耀				
项目负责人	张斌				
审批	张斌				
签字	李树				

成都基准方中
成都基准方中建筑设计股份有限公司
 Chengdu JZFC Architectural Design Co., Ltd.
 中国 成都市 琉璃场8号中国广场A座7-14楼
 电话: +86(28) 86533800 传真: +86(28) 86582999
 Tel: +86(28) 86533800 Fax: +86(28) 86582999
 工程设计资质证书编号: A151016191

版 权 说 明
COPYRIGHT DECLARATION

此图版权为成都基准方中建筑设计股份有限公司所有,未经许可不得使用。