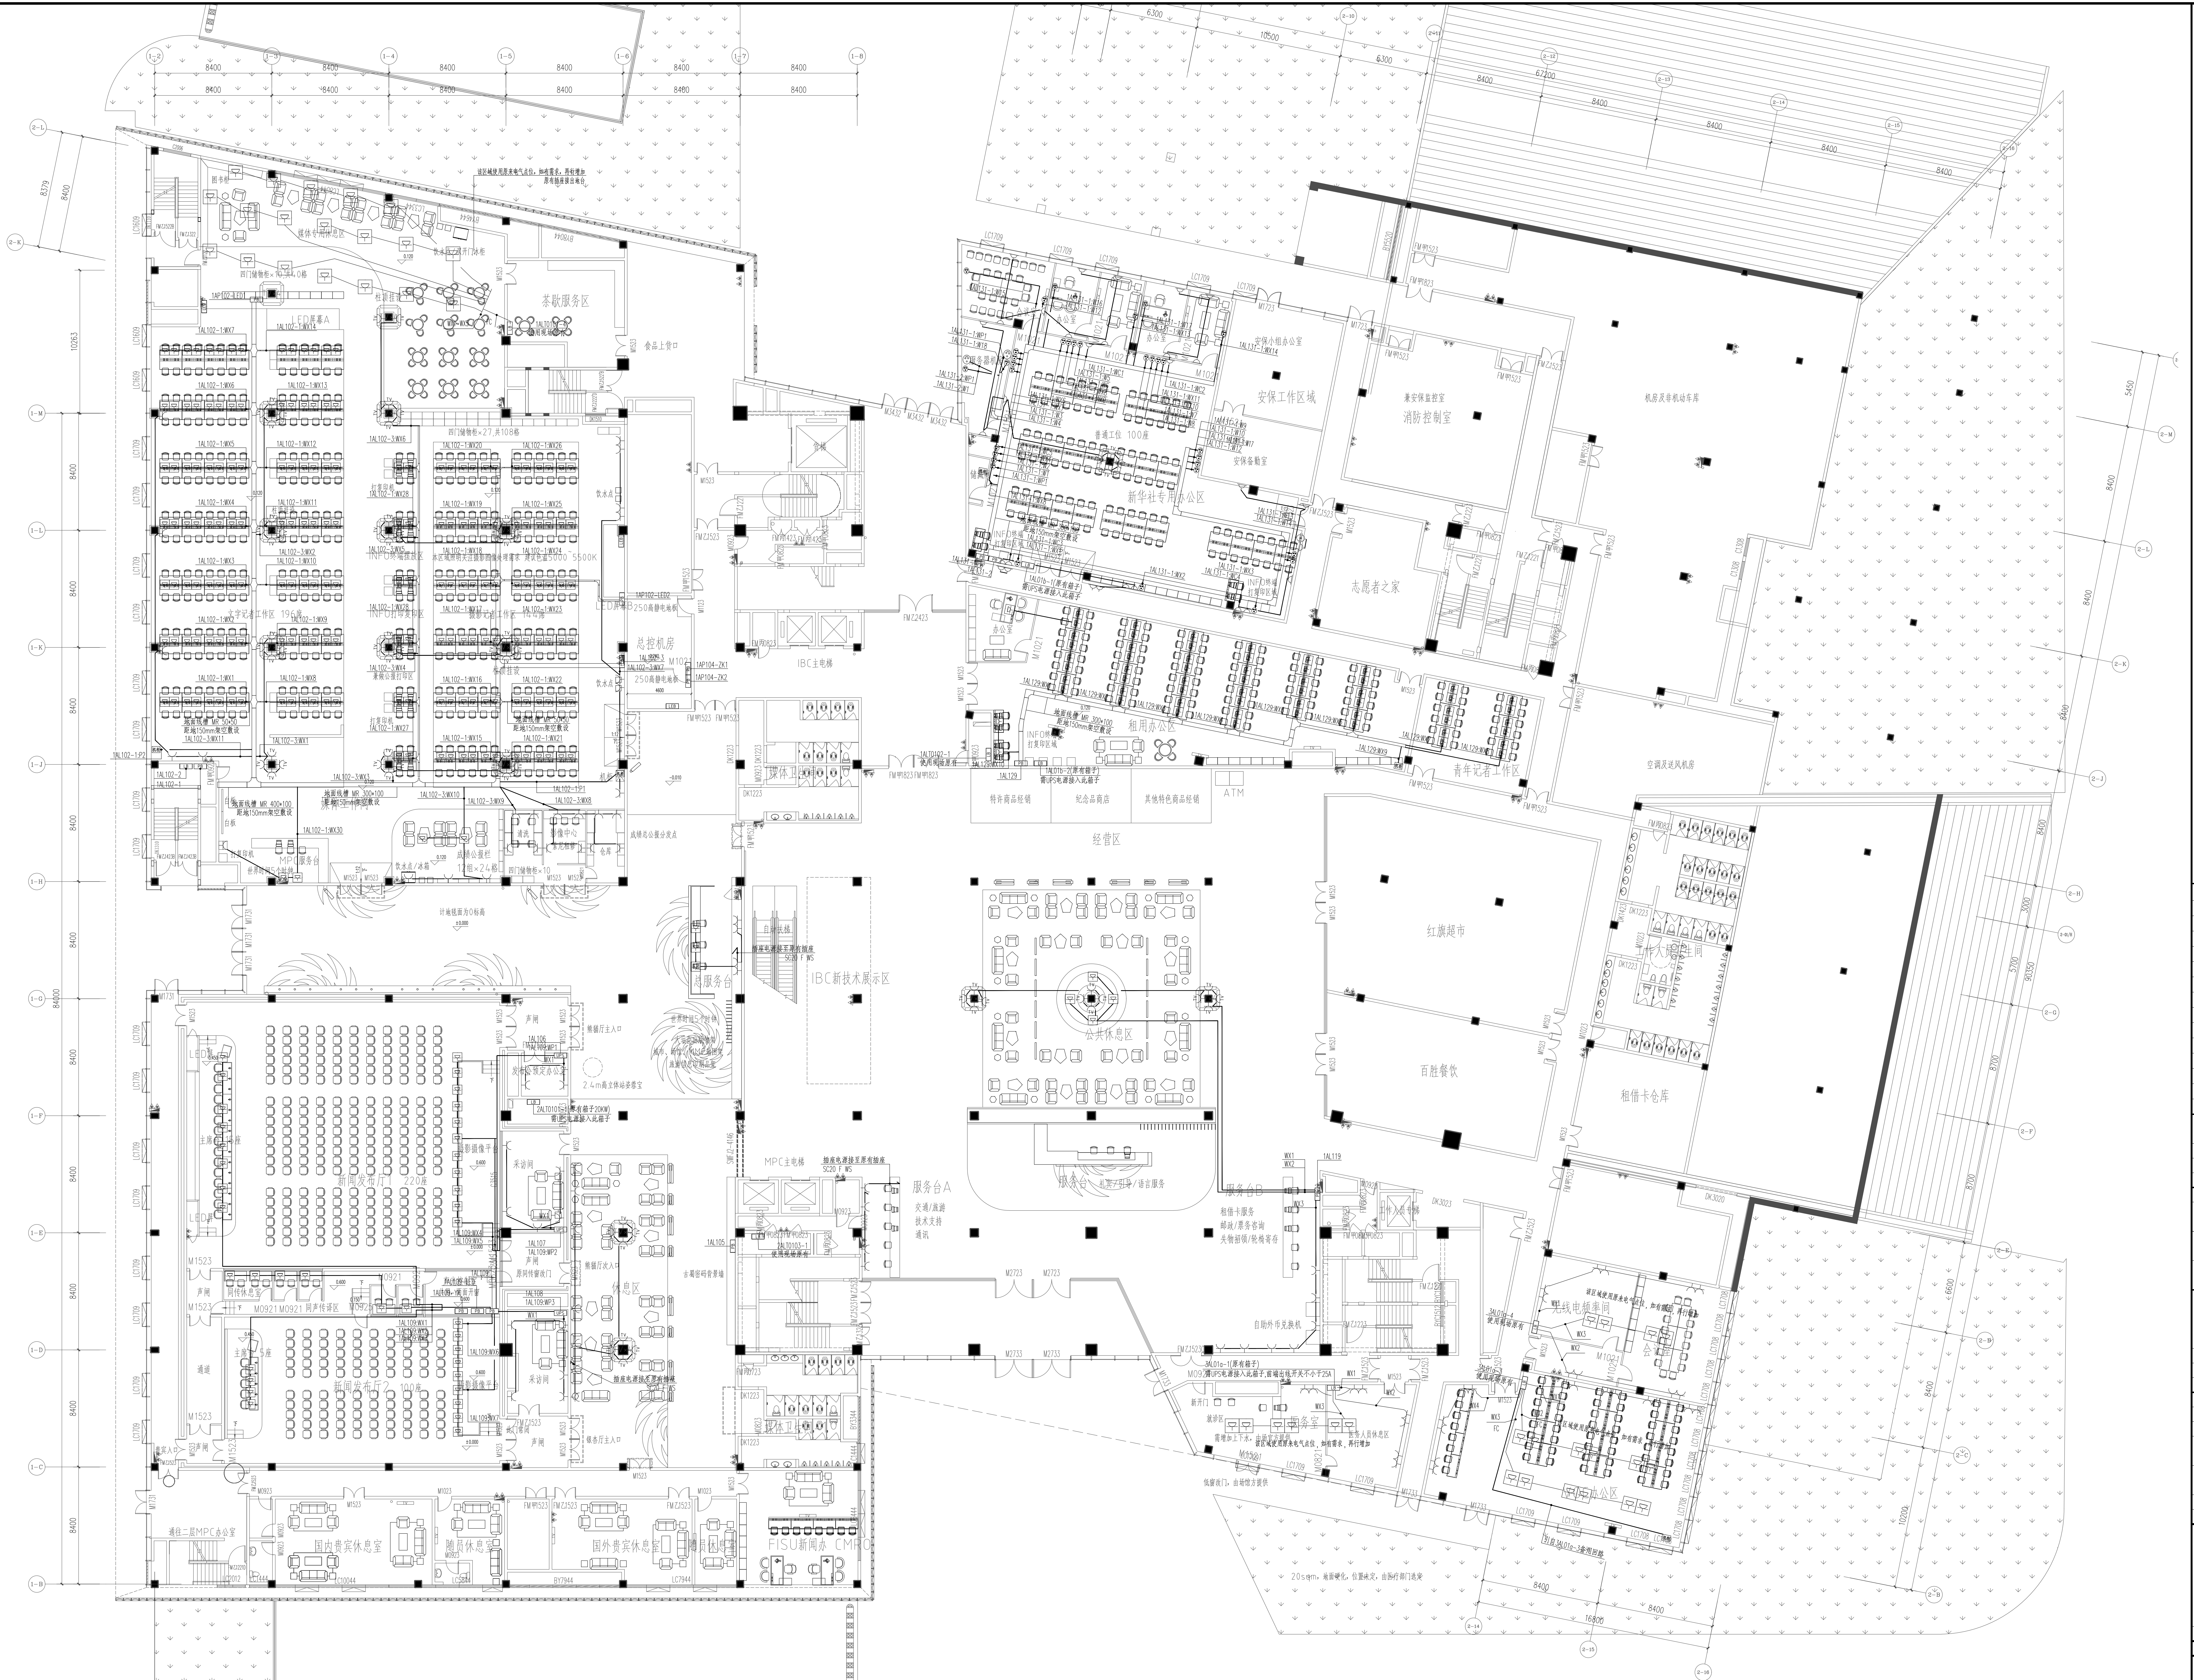


[illegible]

注册执业栏	REGISTERED ARCHITECT/ENGINEER
姓名	NAME
注册号	REGISTRATION IDENTIFICATION NO.
章号	STAMP NO.
CD-20121856-F001	JOINT NO.
名称	PROJECT TITLE
成都大运会主新闻中心装饰装修	
名称	SUB TITLE
名称	CLIENT
成都博雅文瑞文化传播有限公司	
	DRAWING TITLE

图	表位川	张	陈
计	表位川		
内	谢杰		
ED	方地		
表人	表位川		
表人			
OF			
装	方地		
家	陈立		

基准方中
成都基准方中建筑设计股份有限公司
Sichuan JZFZ Architectural Design Co., Ltd.

成都分行 锦江区中环路天府广场B座715楼
+86(28) 86333800 传真: +86(28) 86582990
Tower A, Orient Plaza, No.8Jinli Road, Chengdu, P.R.C
+86(28) 86333800 fax: +86(28) 86582990

文档编号: CAD FILENAME

图板为成都基准方中建筑设计股份有限公司所有，未经许可不得使用。