




采暖通风					
总图					

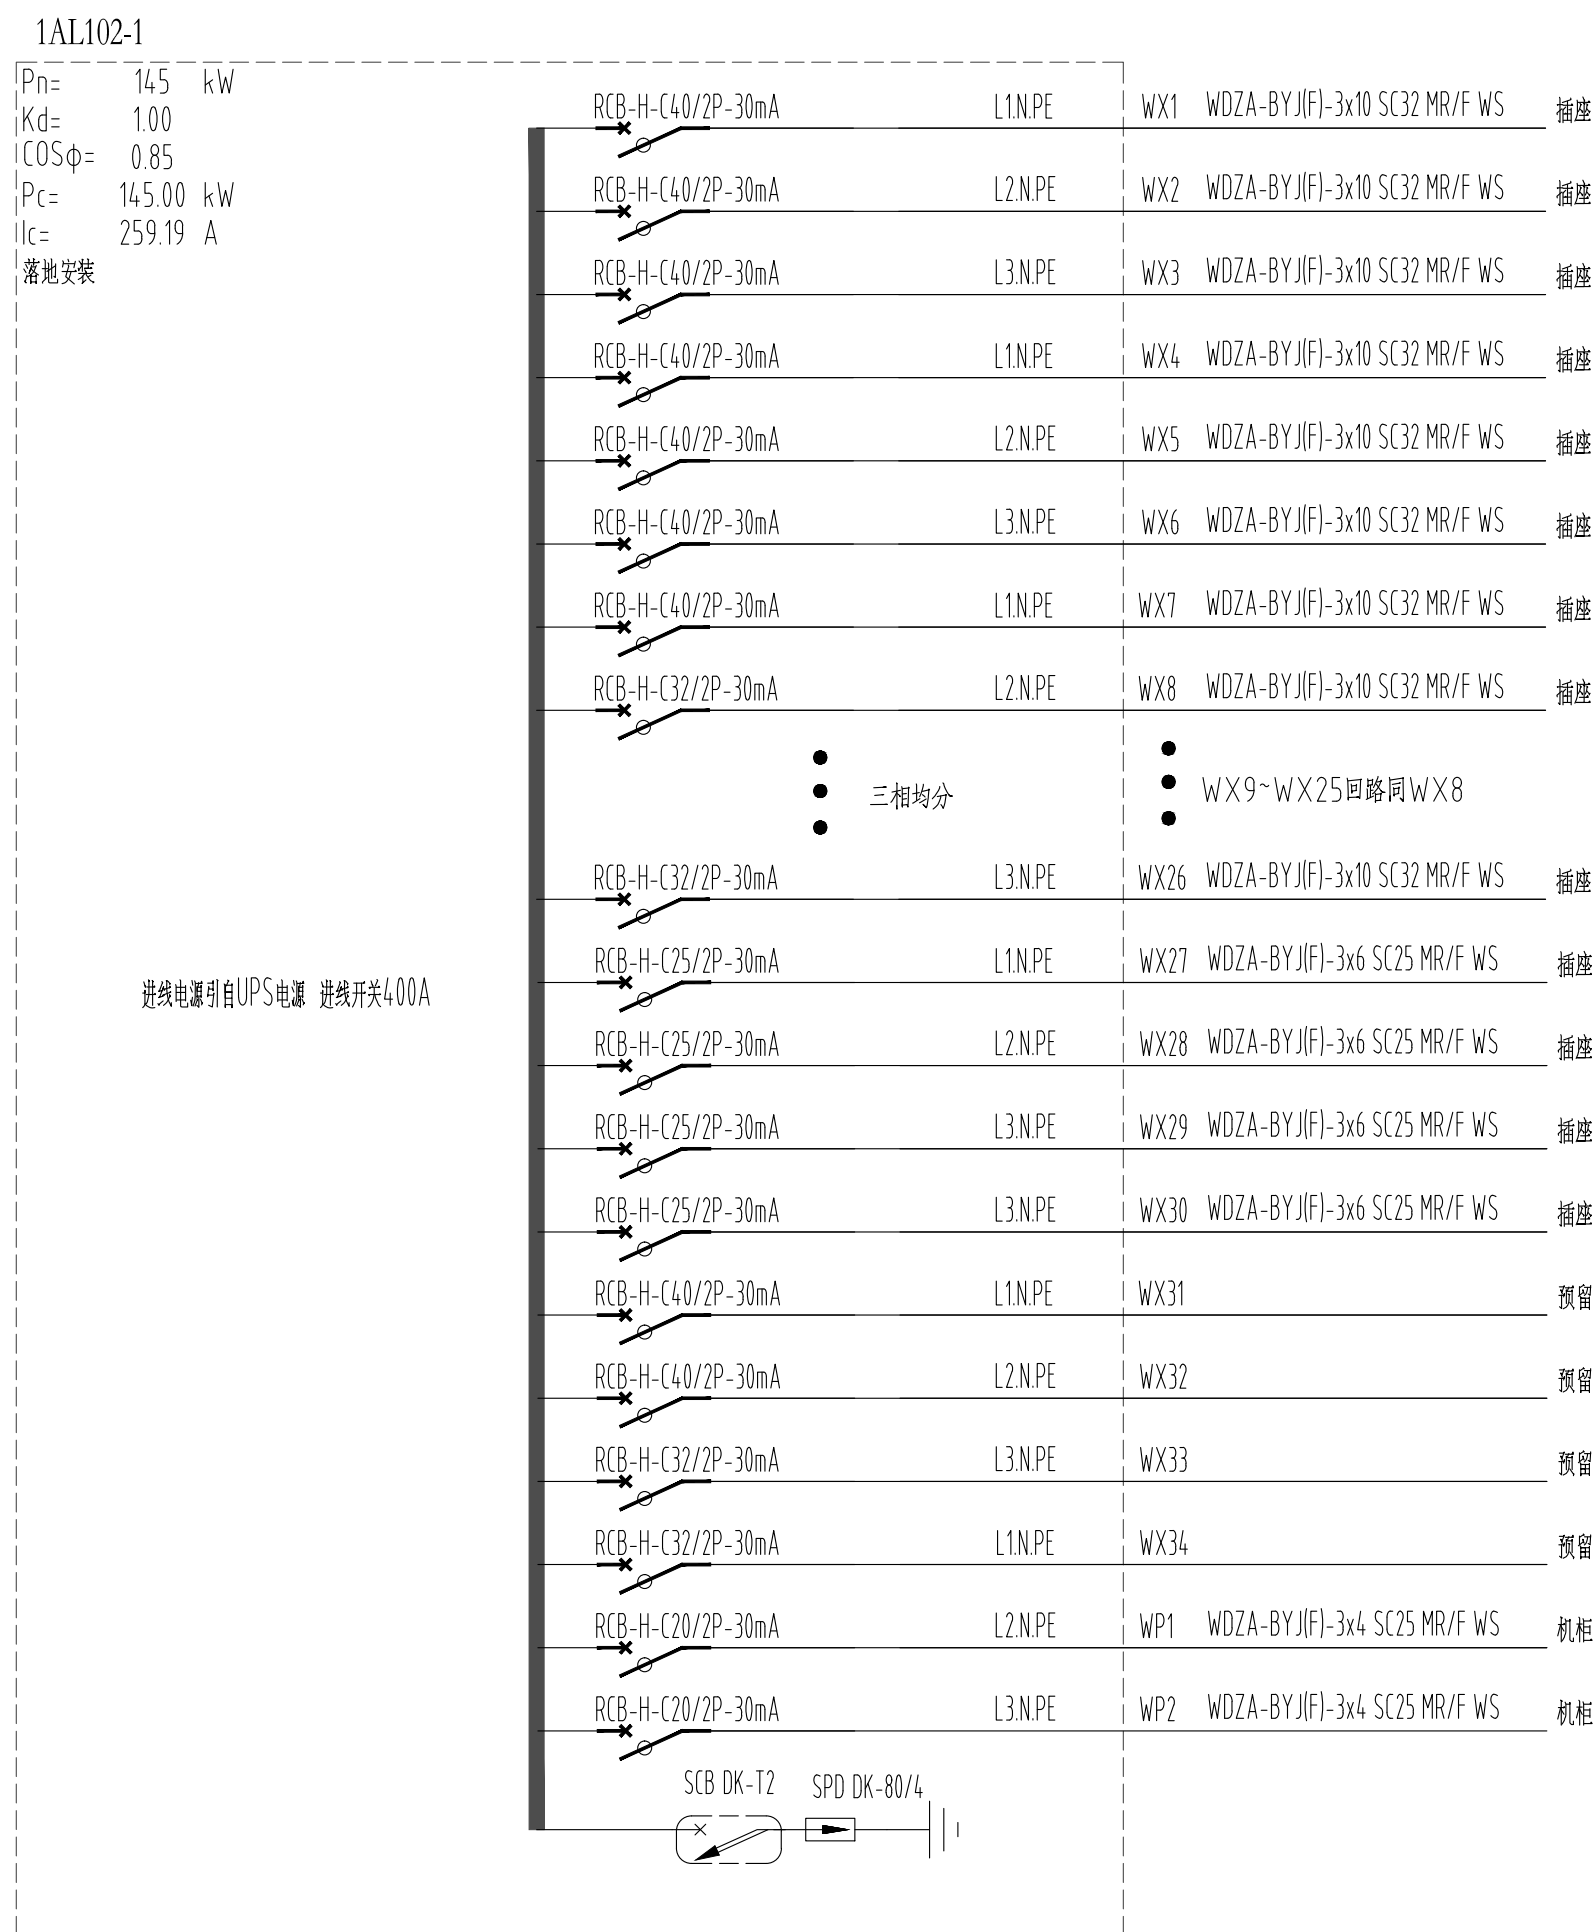


媒体工作间UPS电源动力插座用电配电箱

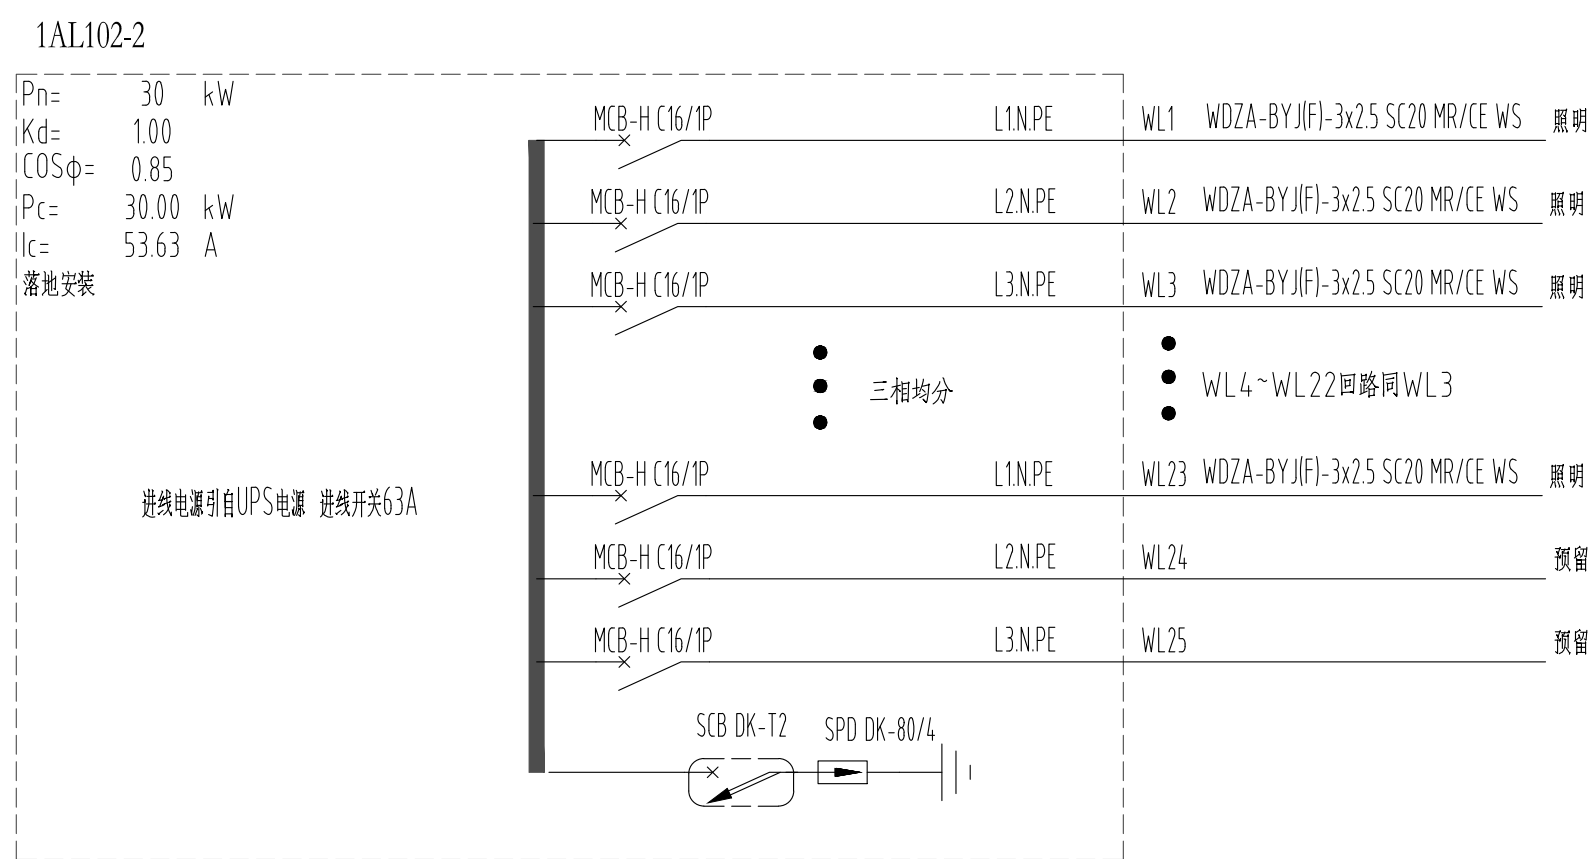


媒体工作间UPS电源照明用电配电箱

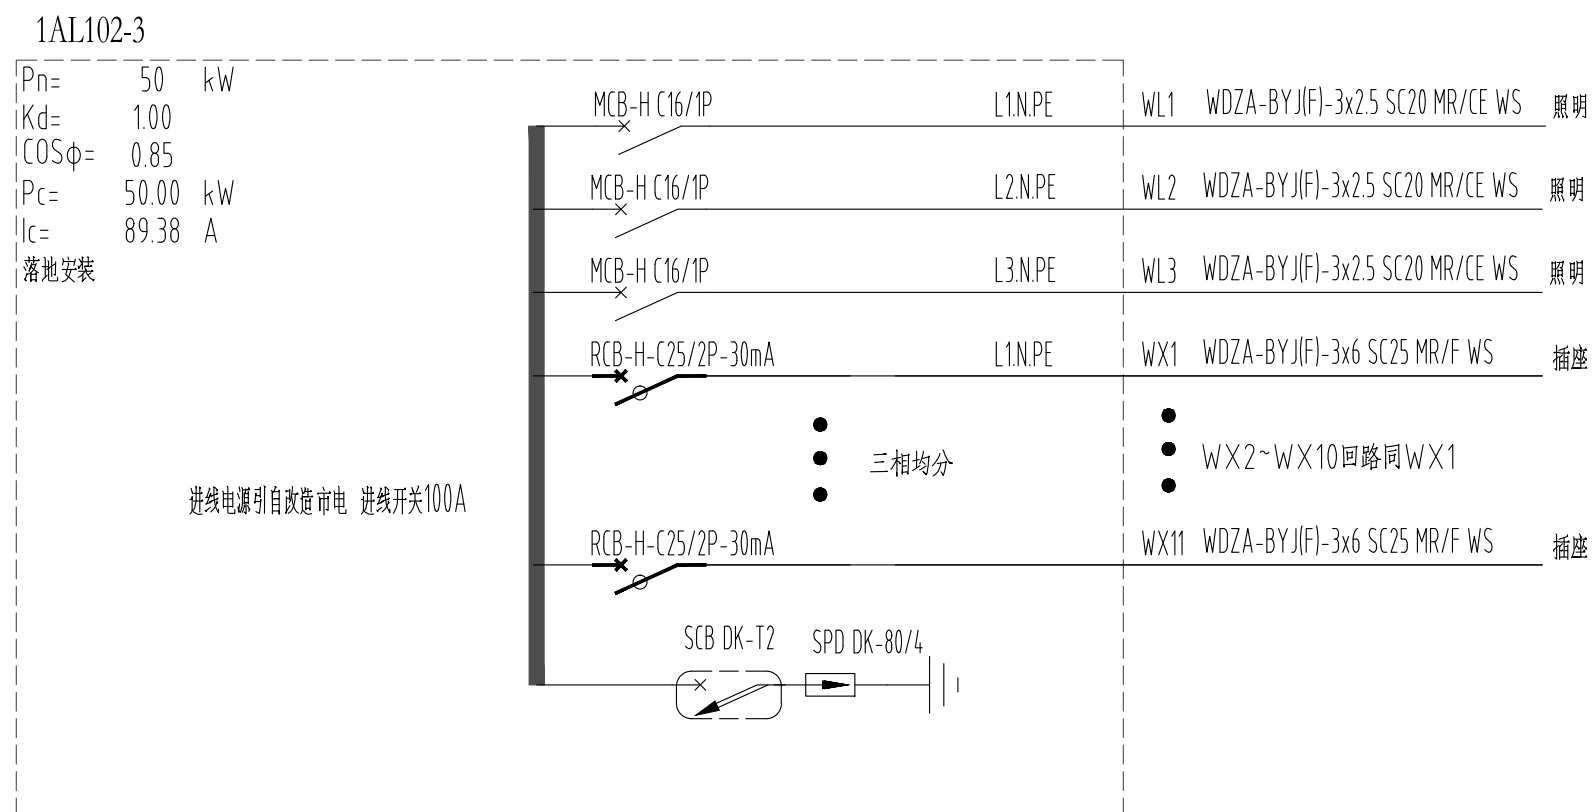


媒体工作普通用电配电箱

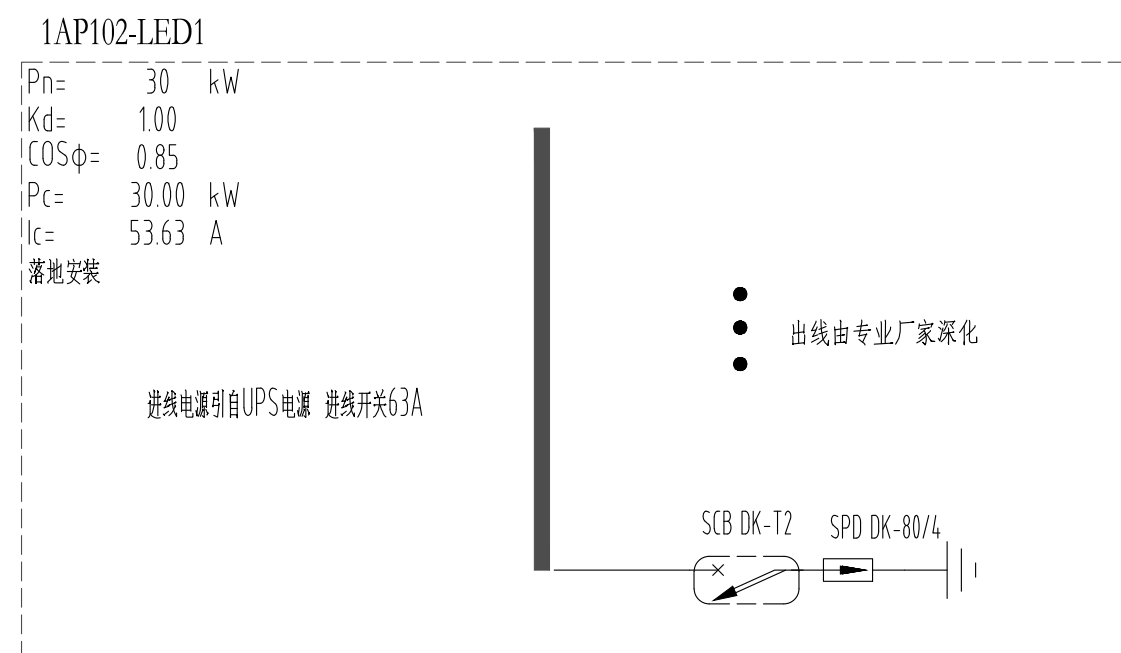


媒体工作间UPS电源LED配电箱1

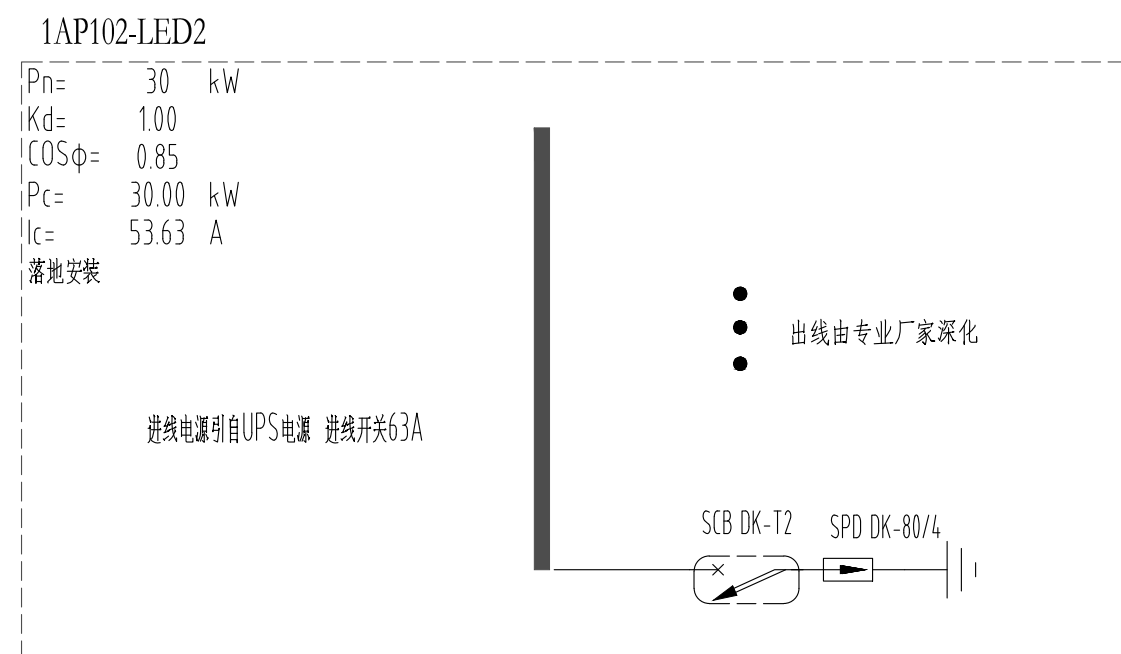

媒体工作间UPS电源LED配电箱2

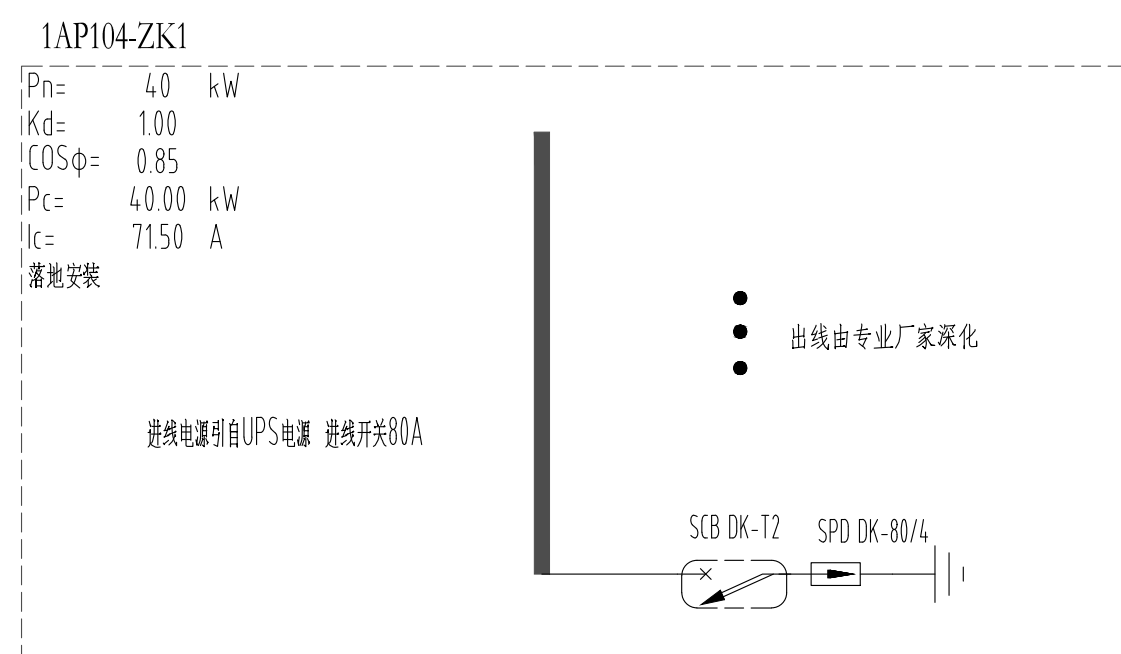

MPC总控机房配电箱1

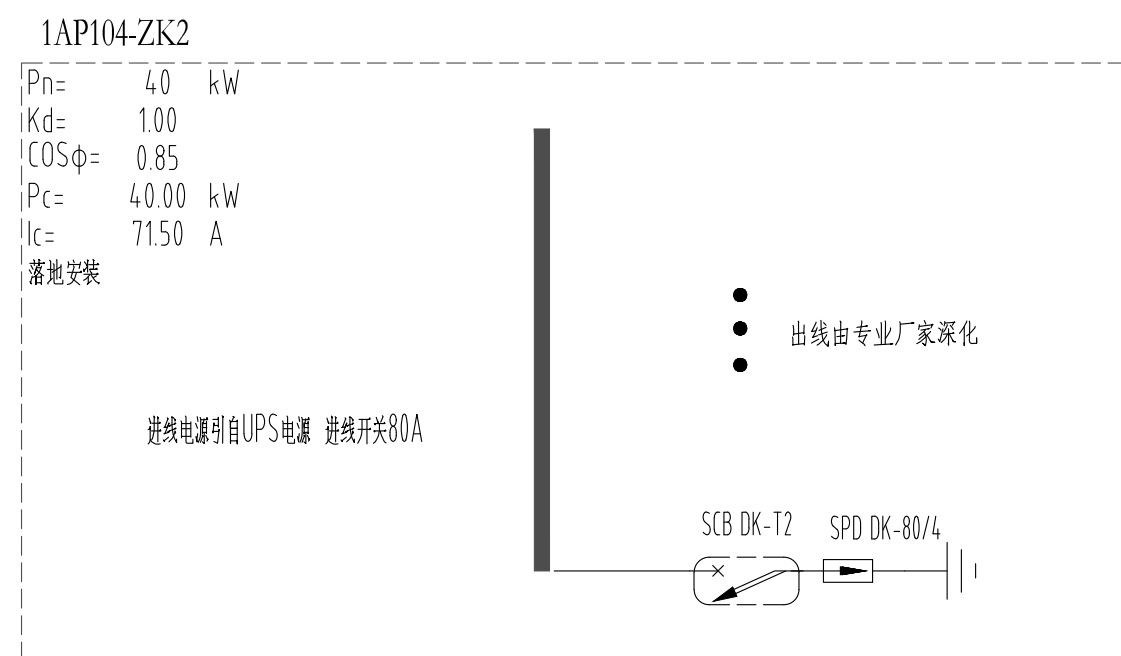

MPC总控机房配电箱2

平面示意:

KEY FINDINGS

[illegible]

注册执业栏		REGISTERED ARCHITECT/ENGINEER
姓 名	NAME	
注册证书号码	REGISTRATION CERTIFICATE NO.	
注册印章号码	STAMP NO.	
设计号	JOB NO.	
工程名称	PROJECT TITLE	
成都大运会主新闻中心装饰搭建		
子项名称	SUB TITLE	
建设单位:		CLIENT
成都博雅文瑞文化传播有限公司		

图 名		DRAWING TITLE			
配电箱系统图一					
单 位:	UNIT	图 号:	图 电 施	DWG. CATEGORY	
比 例	SCALE	图 号:	T01	DWG. NO.	
日 期	DATE	版 本	A	VER. NO.	
制 图	DRAWN BY	审 仕 川			
设 计	DESIGNED BY	赵仕川	赵		
校 对	CHECKED BY	鲜 杰	鲜		
专业负责人	DISCIPLINE CHIEF	方 统	方		
设计总负责人	PROJECT CHIEF	赵仕川	赵		
审 核	AUDIT	方 统	方		
审 定	APPROVED BY	陈 立	陈		

基准方中

成都基准方中建筑设计股份有限公司
Chengdu JZfz Architectural Design Co., Ltd.

中国 成都市 琉璃路8号华润广场A座7-15楼
中译: +86 (28) 86737950 传真: +86 (28) 86587996

7-15F, Tower A, Ciland Plaza, No.8, Liuli Road, Chengdu, P.R.C.
tel. +86(28) 86333800 fax. +86(28) 86582990

工程设计资质证书编号: A151016191

电子文档编号:

CAD FILENAME

版权说明

COPYRIGHT DECLARATION

此图版权为成都基准方中建筑设计股份有限公司所有，未经许可不得使用。