




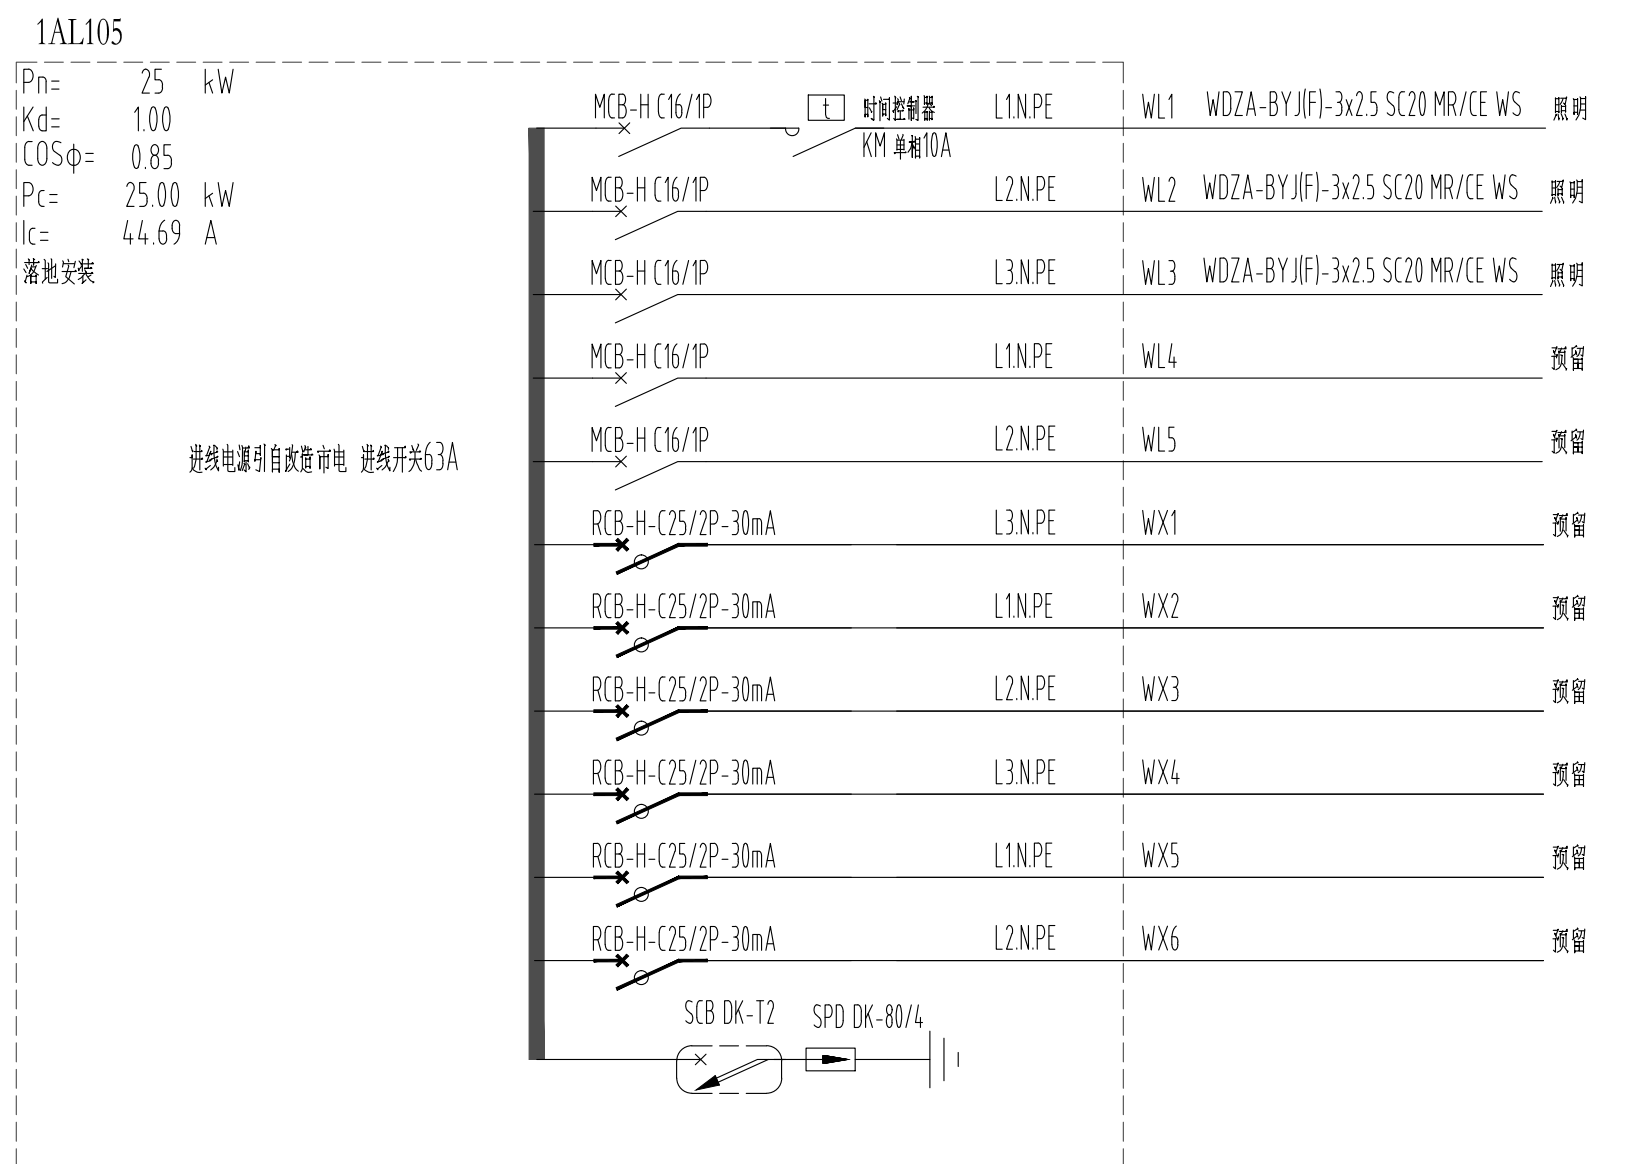


新闻发布厅外休息区用电配电箱

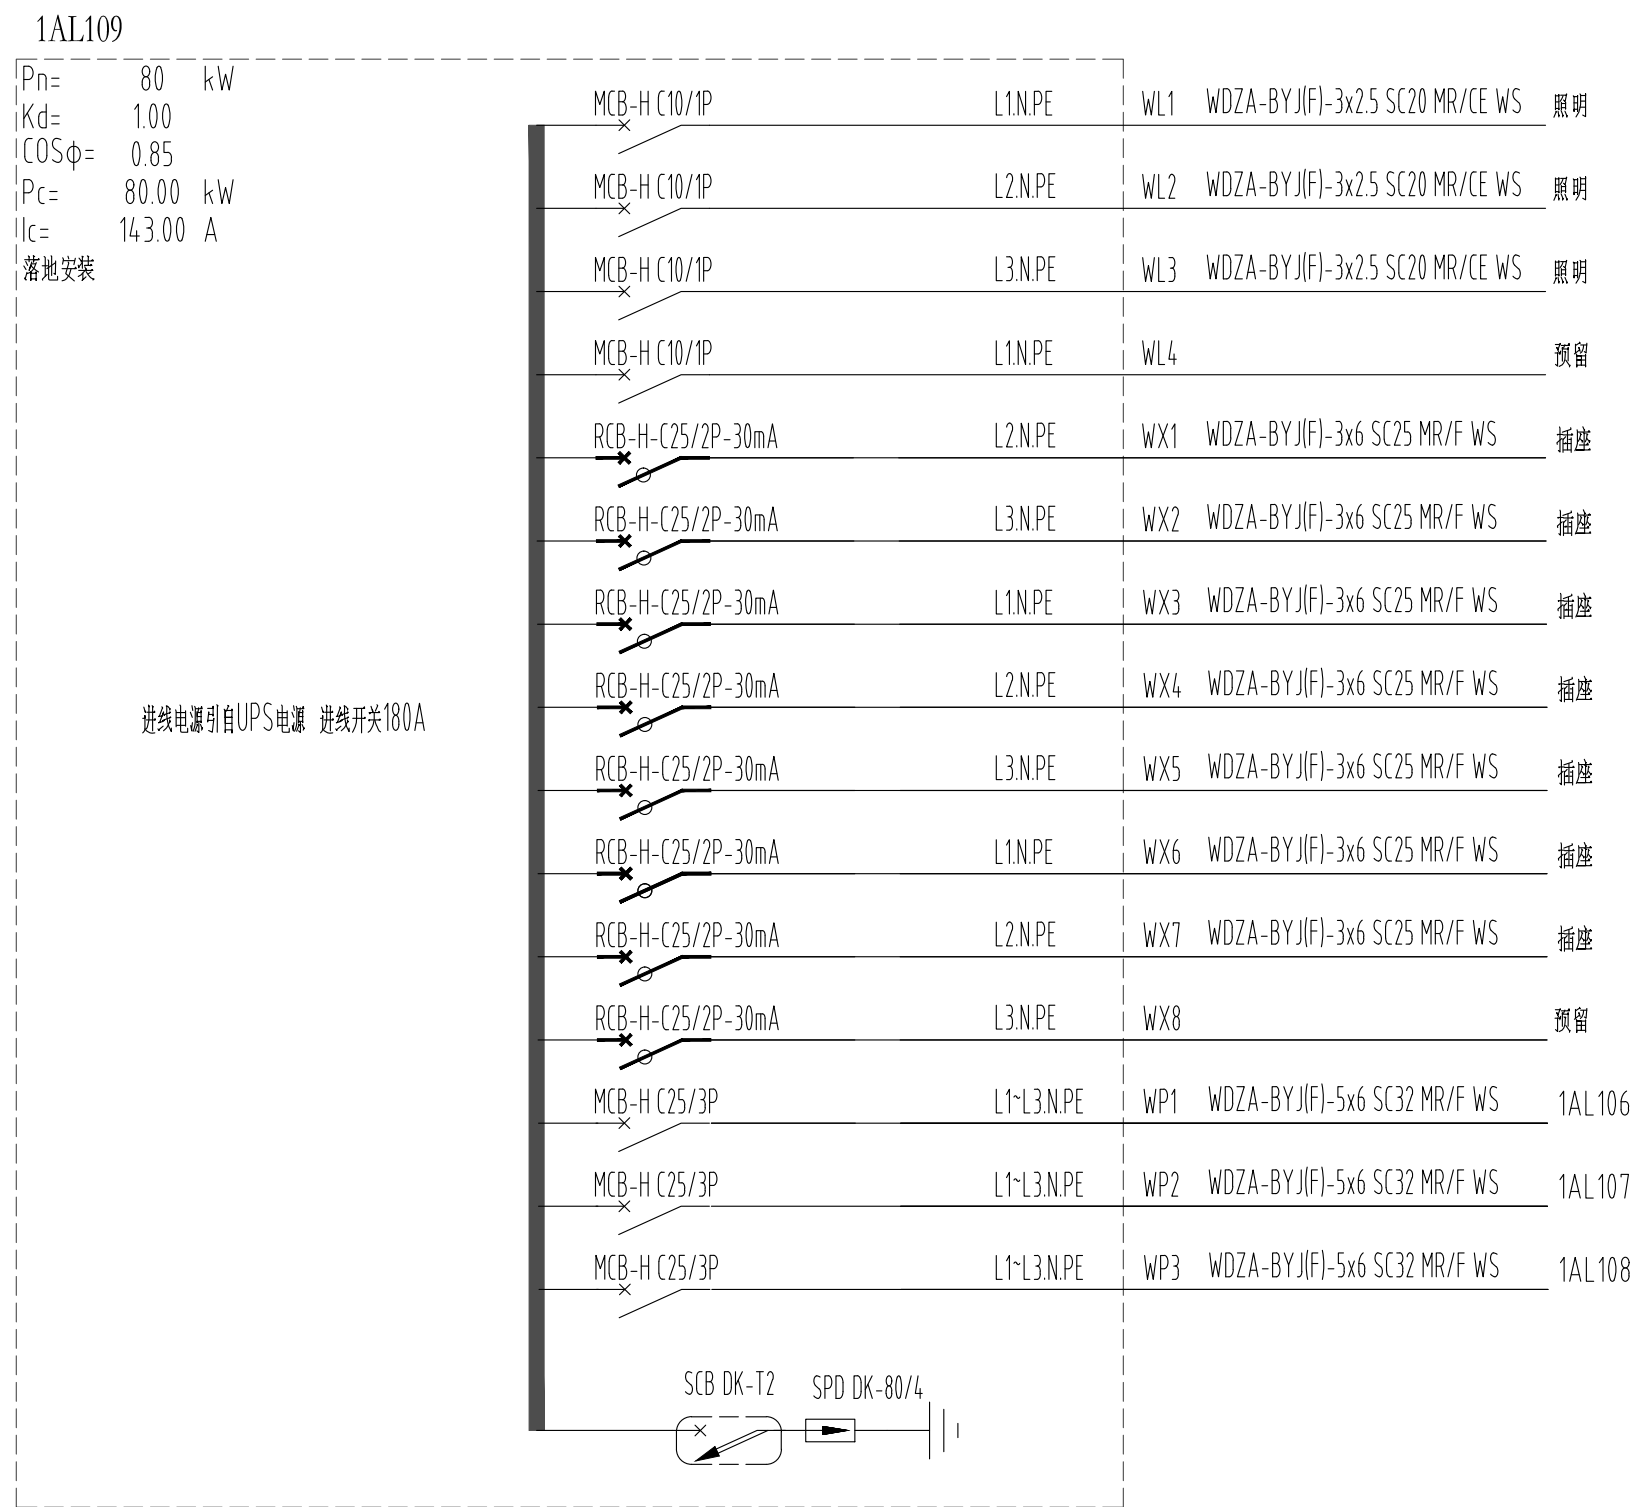


新闻发布厅UPS电源照明用电配电箱

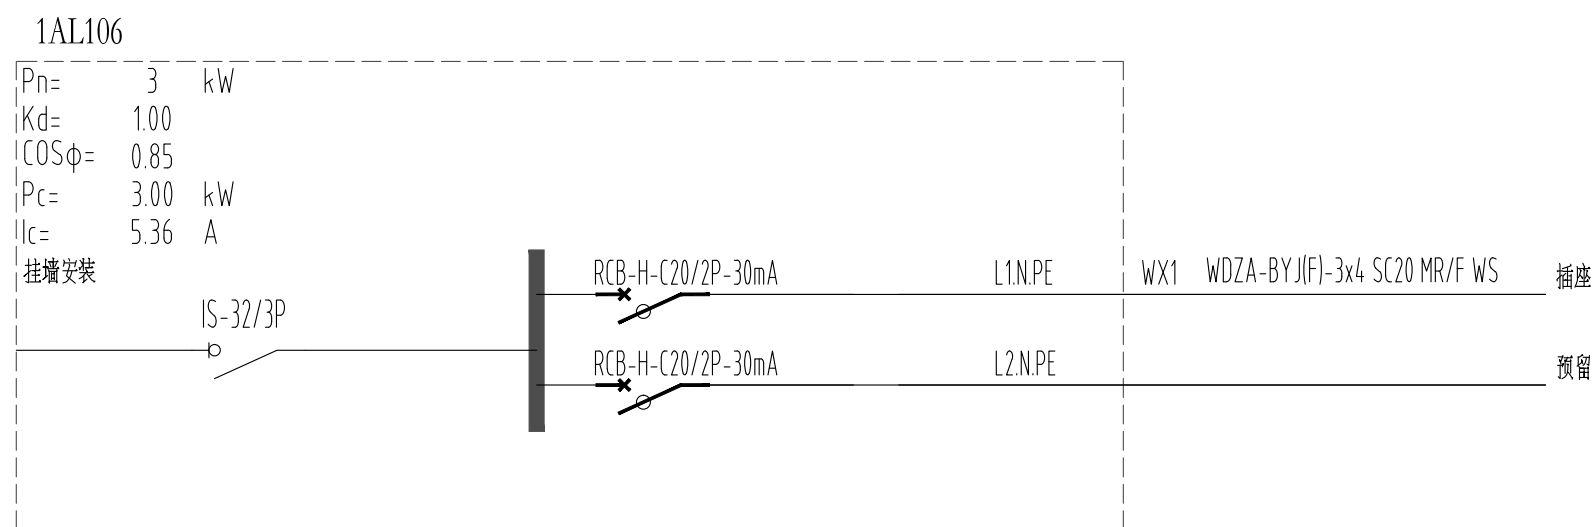


发布会预定办公室UPS电源插座用电配电箱

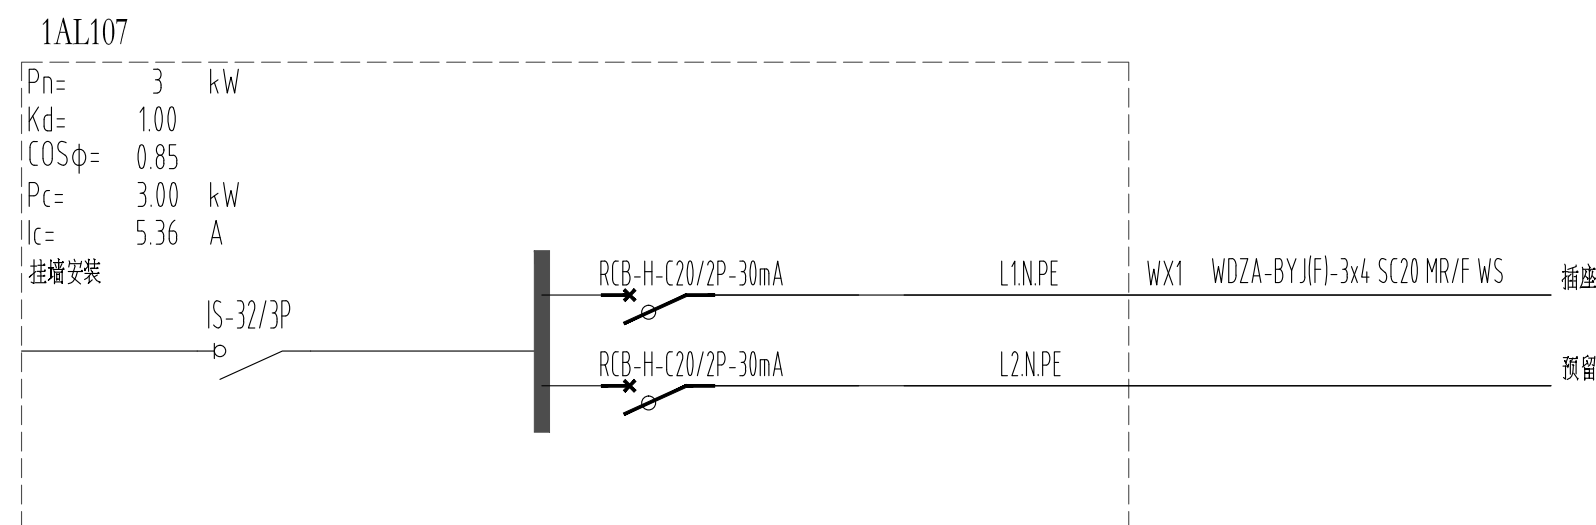


采访间UPS电源插座用电配电箱

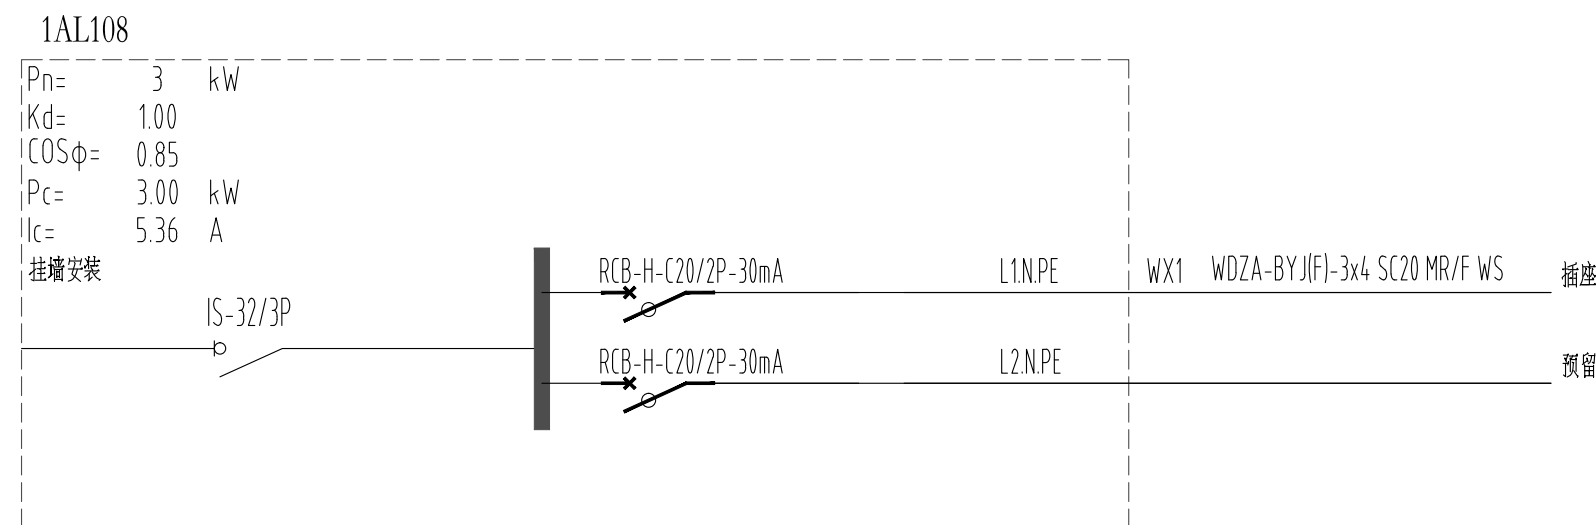

采访间UPS电源插座用电配电箱

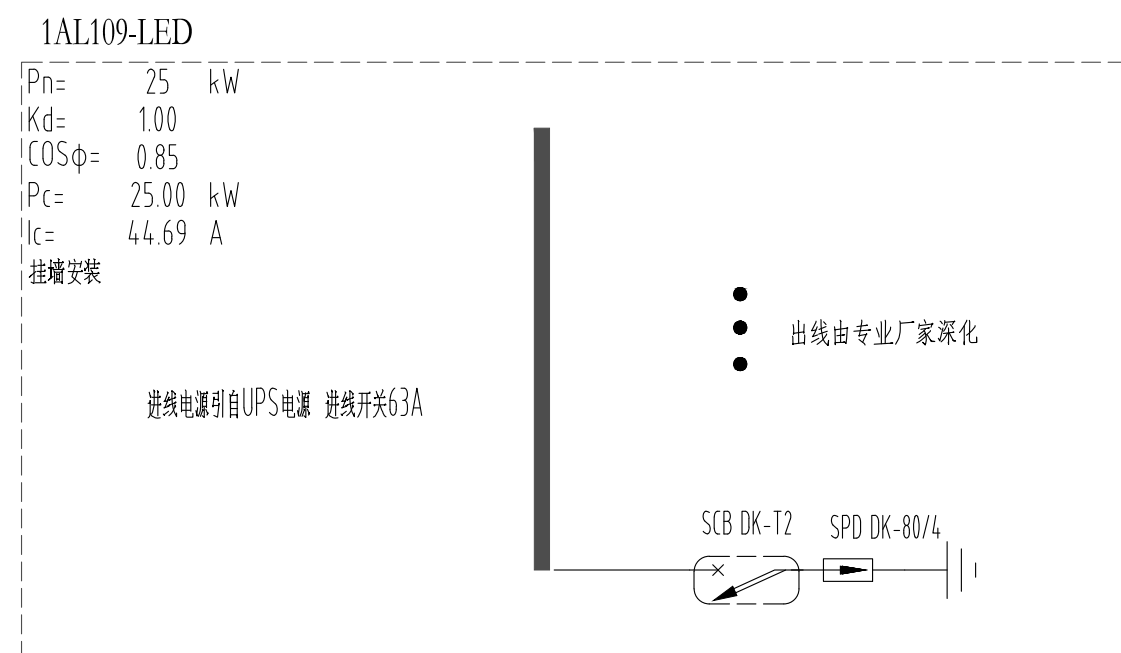

新闻发布厅UPS电源LED配电箱

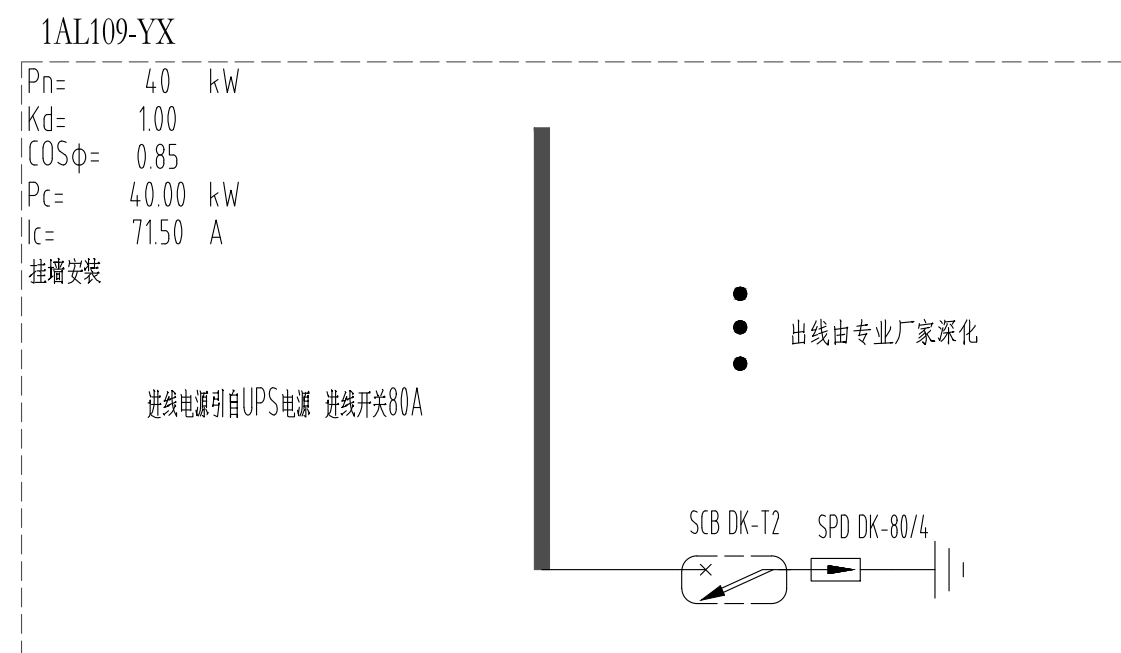

新闻发布厅UPS电源音响配电箱

平面示意: KEY PLAN

[illegible]

注册执业栏		REGISTERED ARCHITECT/ENGINEER
姓 名	NAME	
注册证书号	REGISTRATION CERTIFICATE NO.	
注册印章号	STAMP NO.	
设计号	JOB NO.	
工程名称	PROJECT TITLE	
成都大运会主新闻中心装饰搭建		
子项名称	SUB ITEM	
建设单位		CLIENT
成都博雅文瑞文化传播有限公司		

图 名		DRAWING TITLE	
配电箱系统图二			
单 位	UNIT	图 别	DWG. CATEGORY
比 较	SCALE	图 号	DWG. NO.
日 期	DATE	版 本	VER. NO.
2022.02		A	
制 图	DESIGNED BY	袁仕川	
设 计	DESIGNED BY	袁仕川	袁仕川
校 对	CHECKED BY	鲜 杰	鲜杰
专业负责人	SPECIALIST	方统	方统
DISCIPLINE CHIEF		袁仕川	袁仕川
设计负责人	PROJECT CHIEF		
审 核	APPROVED BY	方 统	方统
审 定	APPROVED BY	陈 立	陈立

四 基准方中

成都基准方中建筑设计股份有限公司
Chengdu JZfz Architectural Design Co., Ltd.

中国 成都市 琉璃路8号华润广场A座7-15楼
电话: +86 (28) 86333800 传真: +86 (28) 86582990
7-15F, Tower A, Cridal Plaza, No.8, Liuli Road, Chengdu
tel. +86(28) 86333800 fax. +86(28) 86582990

工程设计资质证书编号: A151016191

电子文档编号: CAD FILENAME

版 权 说 明

COPYRIGHT DECLARATION

此图版权为成都基准方中建筑设计股份有限公司所有，未经许可不得使用。