




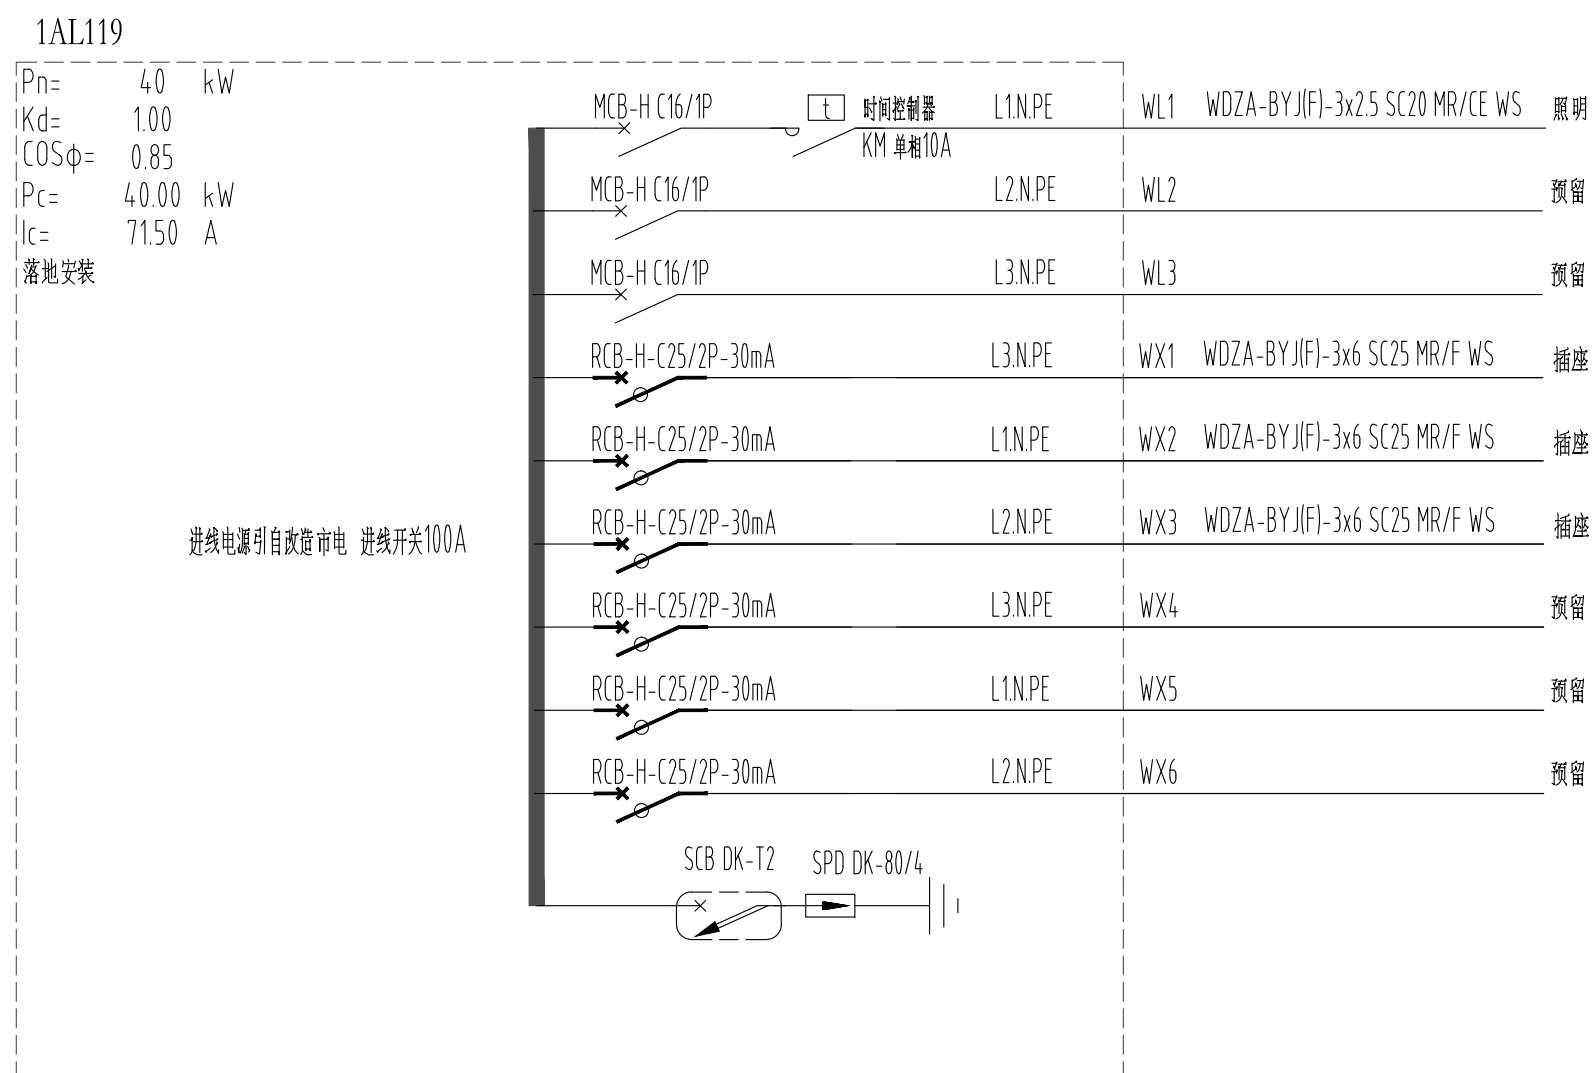

117-119南侧服务欢迎区用电配电箱

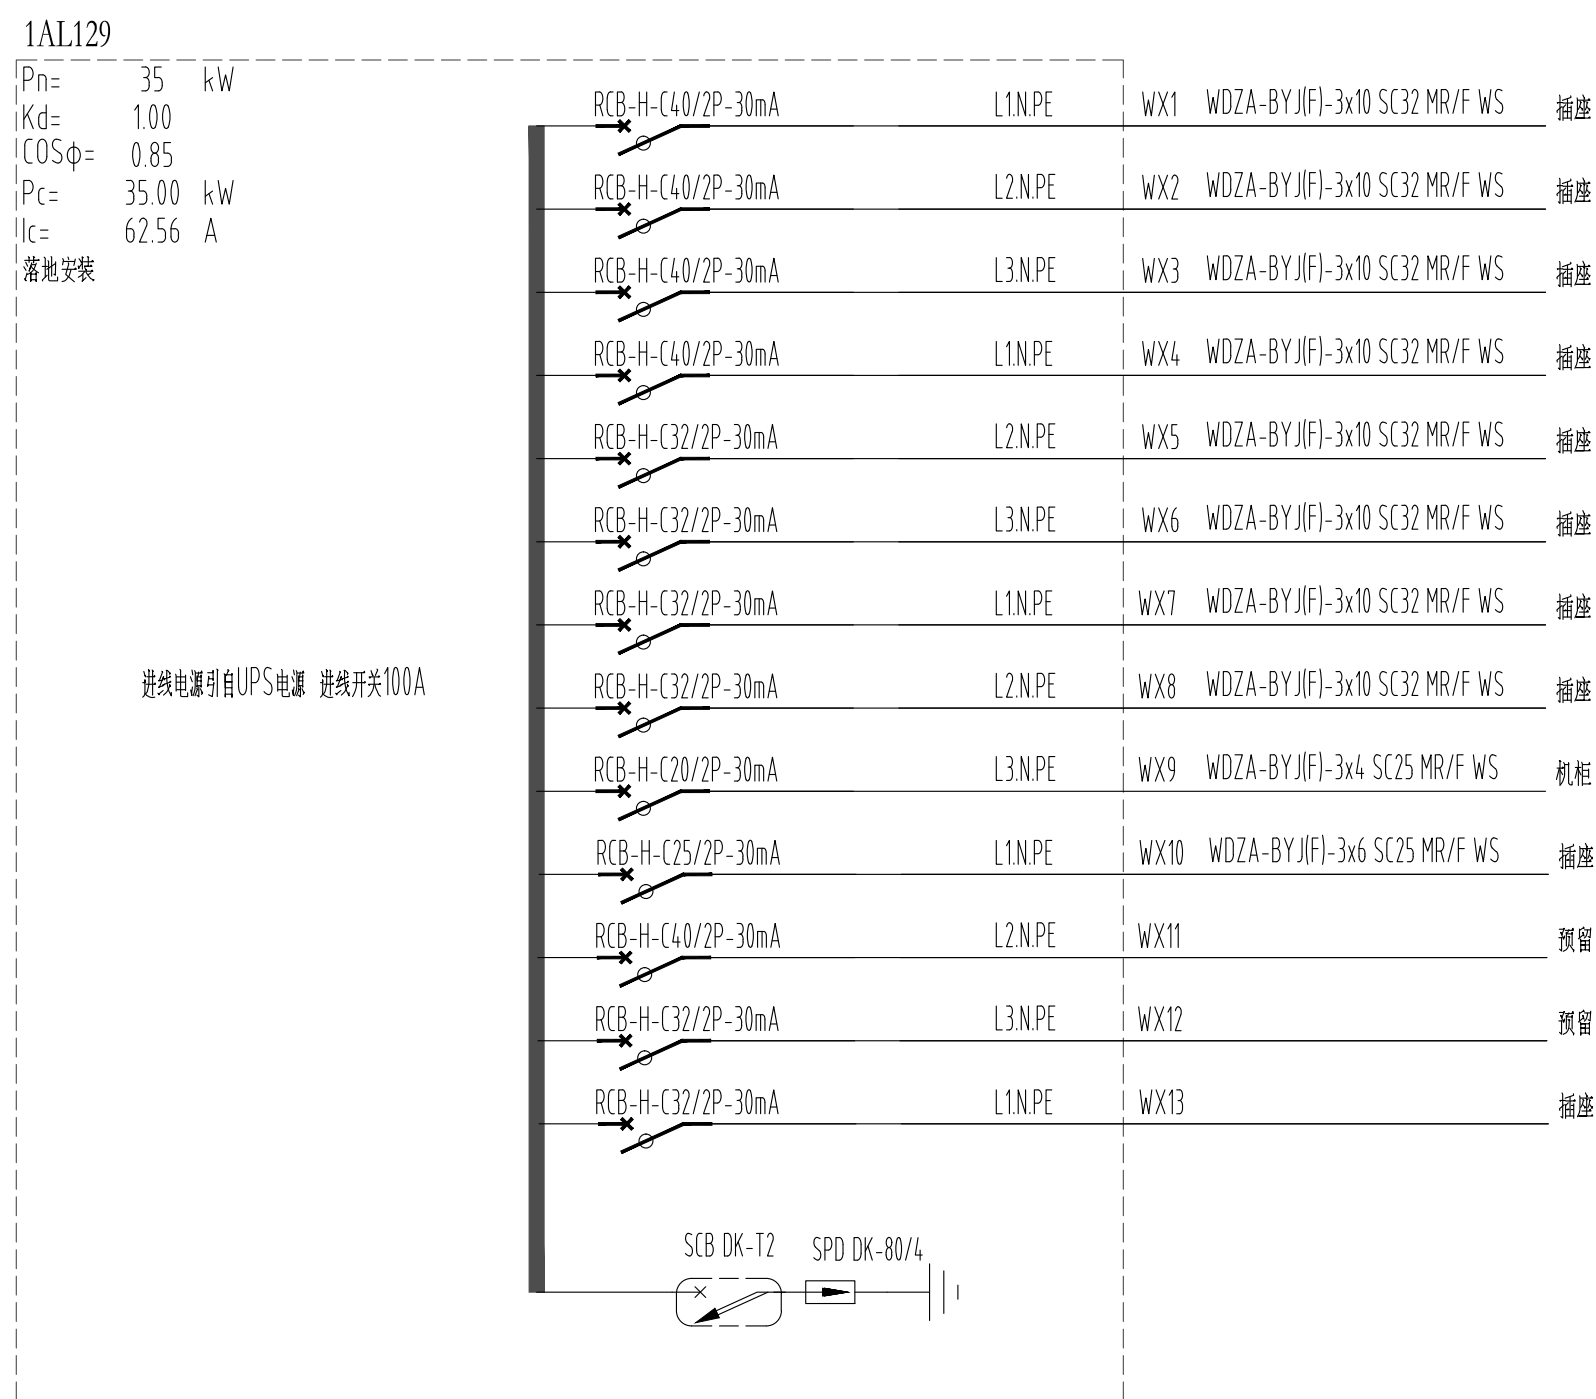

人民日报工作间UPS电源动力插座用电配电箱

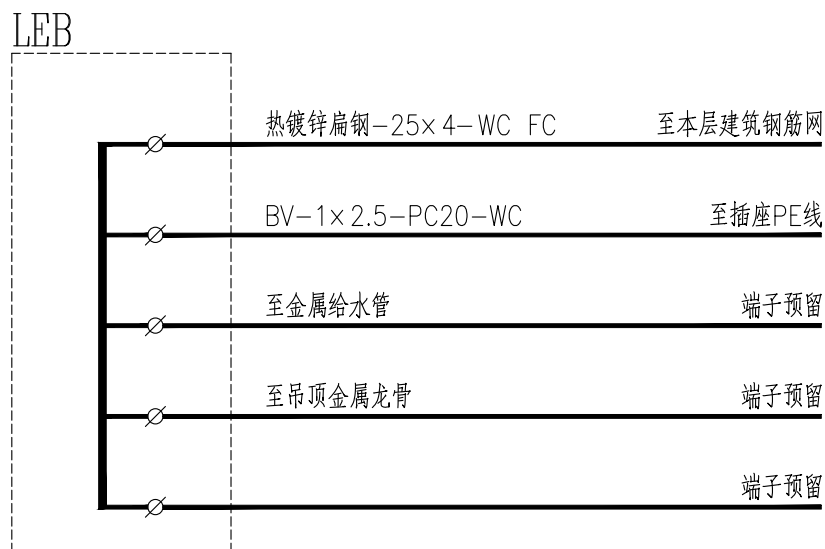


说明: 1、施工参见15D502相关页次。

LEB箱大样图



新华社UPS电源动力插座用电配电箱

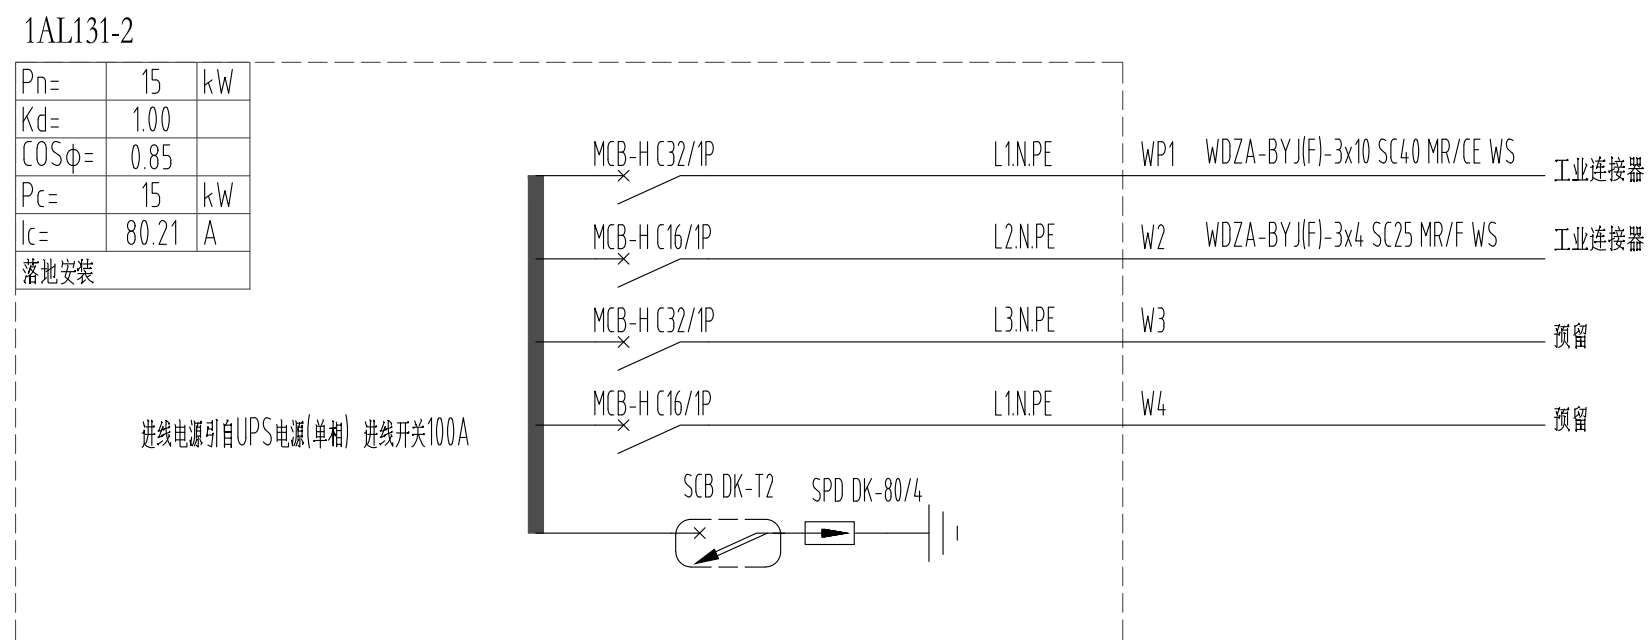

新华社UPS电源机房用电配电箱

[illegible]

注册执业栏		REGISTERED ARCHITECT/ENGINEER
姓 名	NAME	
注册证书号	REGISTRATION CERTIFICATE NO.	
注册印章号码	STAMP NO.	
设计号	JOB NO.	
工程名称	PROJECT TITLE	
成都大运会主新闻中心装饰搭建		
子项名称	SUB ITEM	
建设单位		CLIENT
成都博雅文瑞文化传播有限公司		

图 名		DRAWING TITLE	
配电箱系统图三			
单 位	UNIT	图 号	DWG. CATEGORY
比 例	SCALE	图 号 T03	DWG. NO.
日 期	DATE	版 本	VER. NO.
制 图 DRAWN BY	吴仕川		
设 计 DESIGNED BY	吴仕川		
校 对 CHECKED BY	鲜 杰		
专业负责人 DISCIPLINE CHIEF	方 纯		
审核人 PROJECT CHIEF	吴仕川		
设计总负责人 PROJECT CHIEF			
审 核 AUDIT	方 纯		
审 定 APPROVED BY	陈 立		