




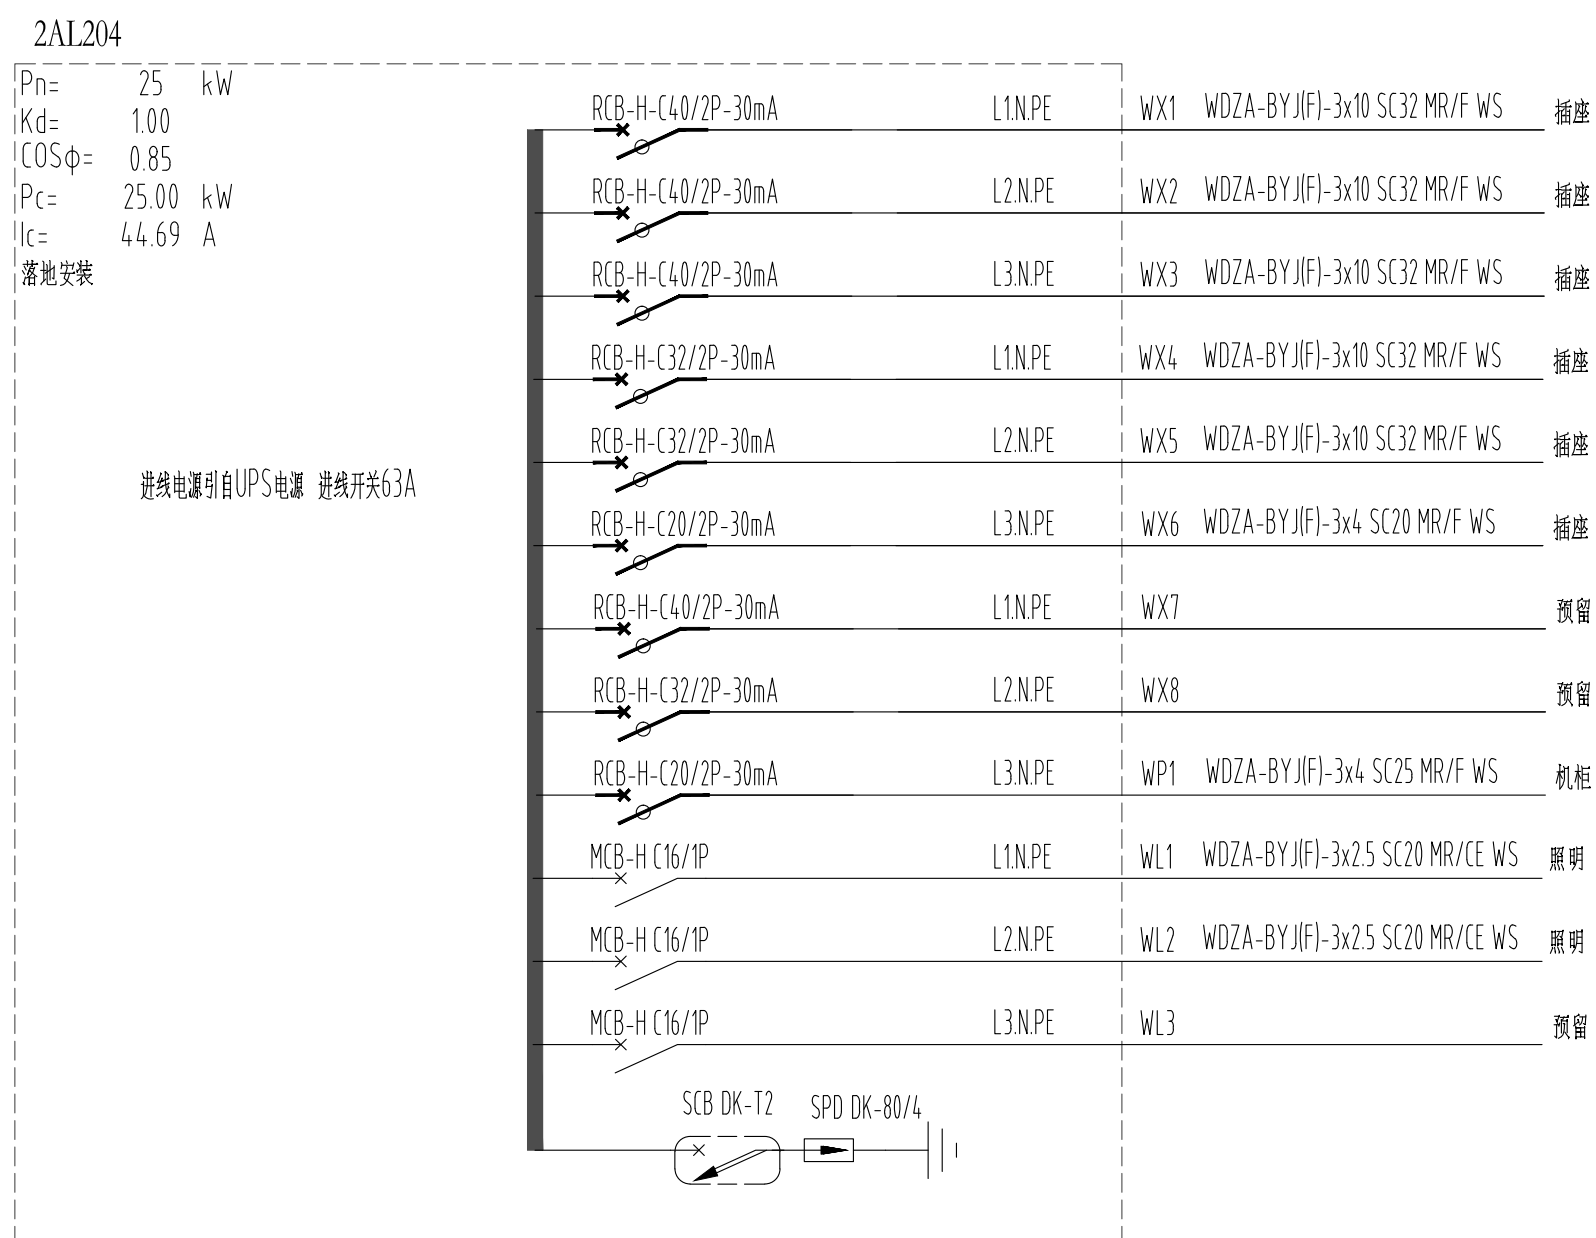


204 办公区UPS电源动力插座用电配电箱

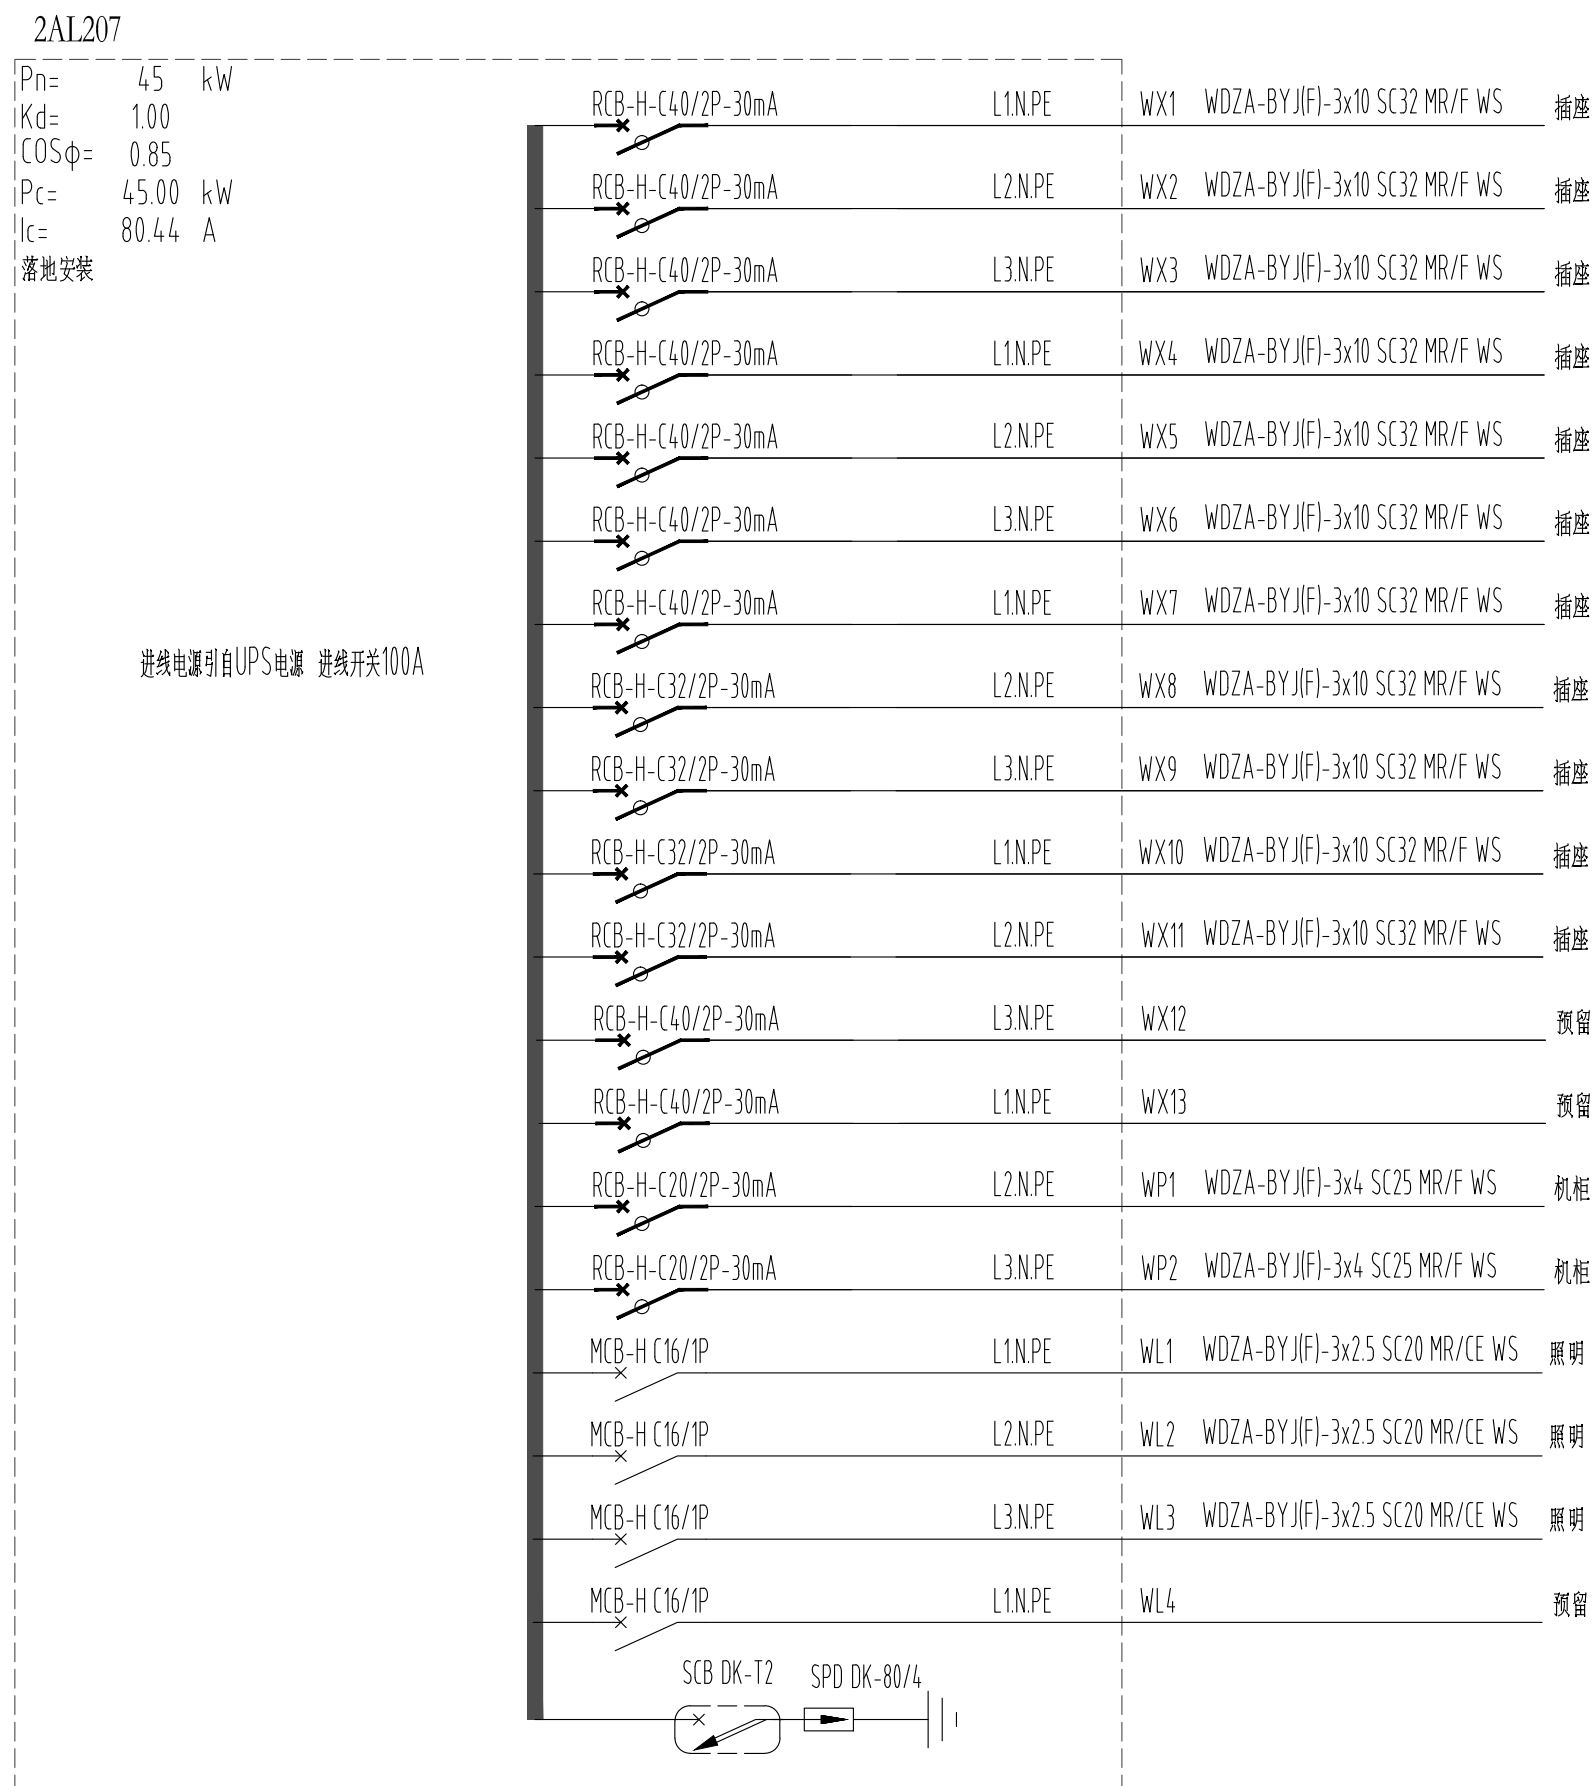


205-210办公区UPS电源动力插座用电配电箱

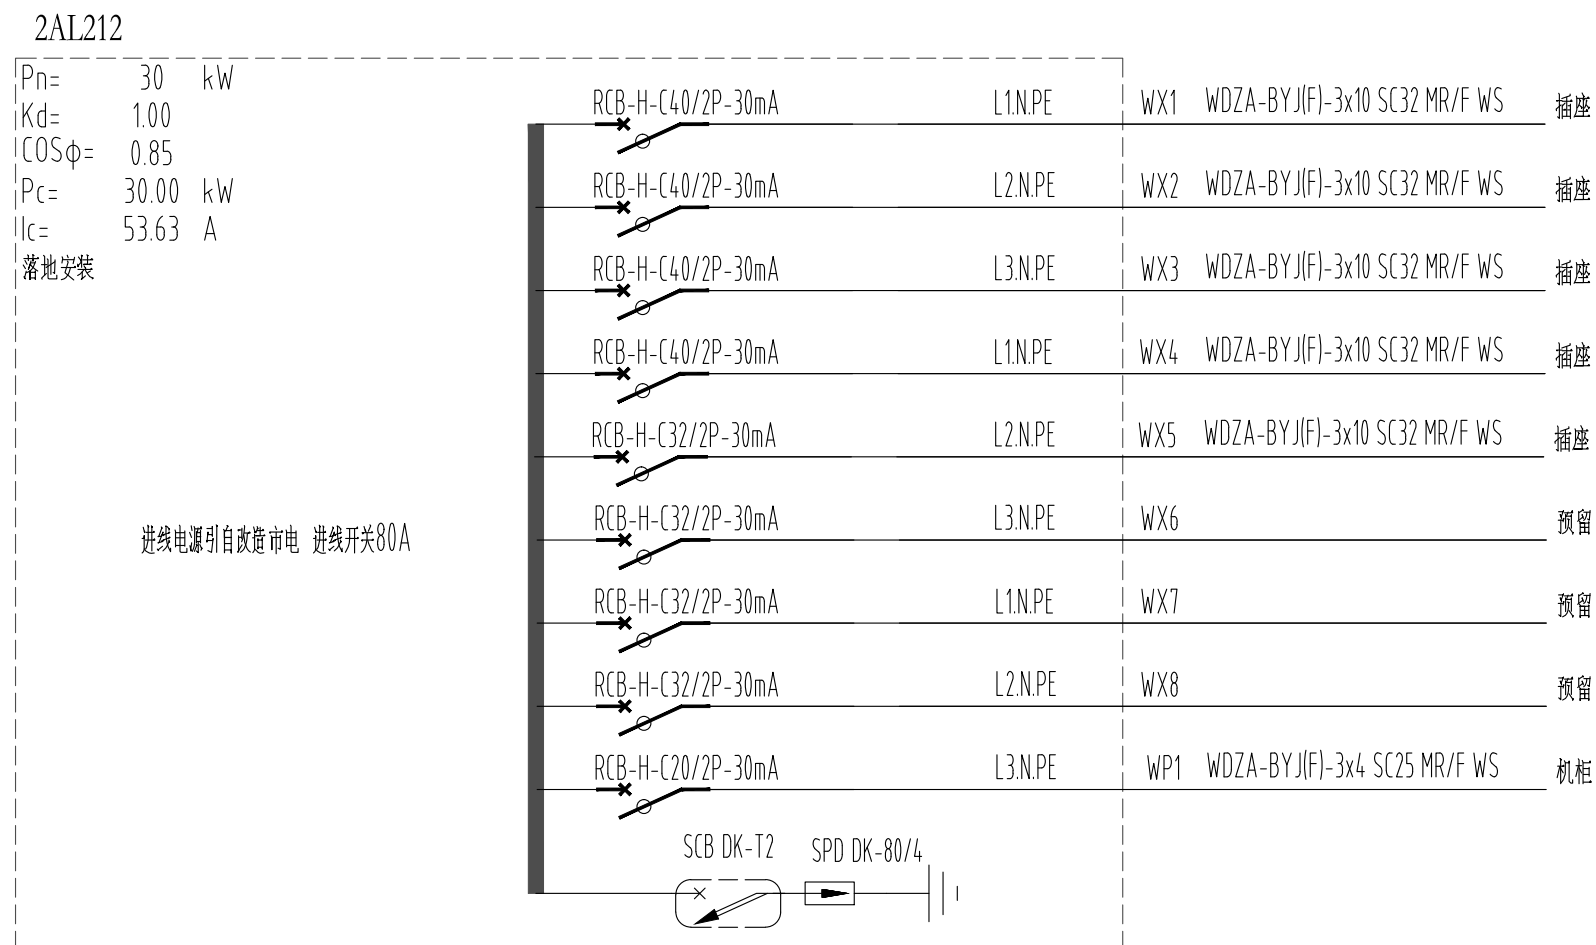


212-215区插座用电配电箱

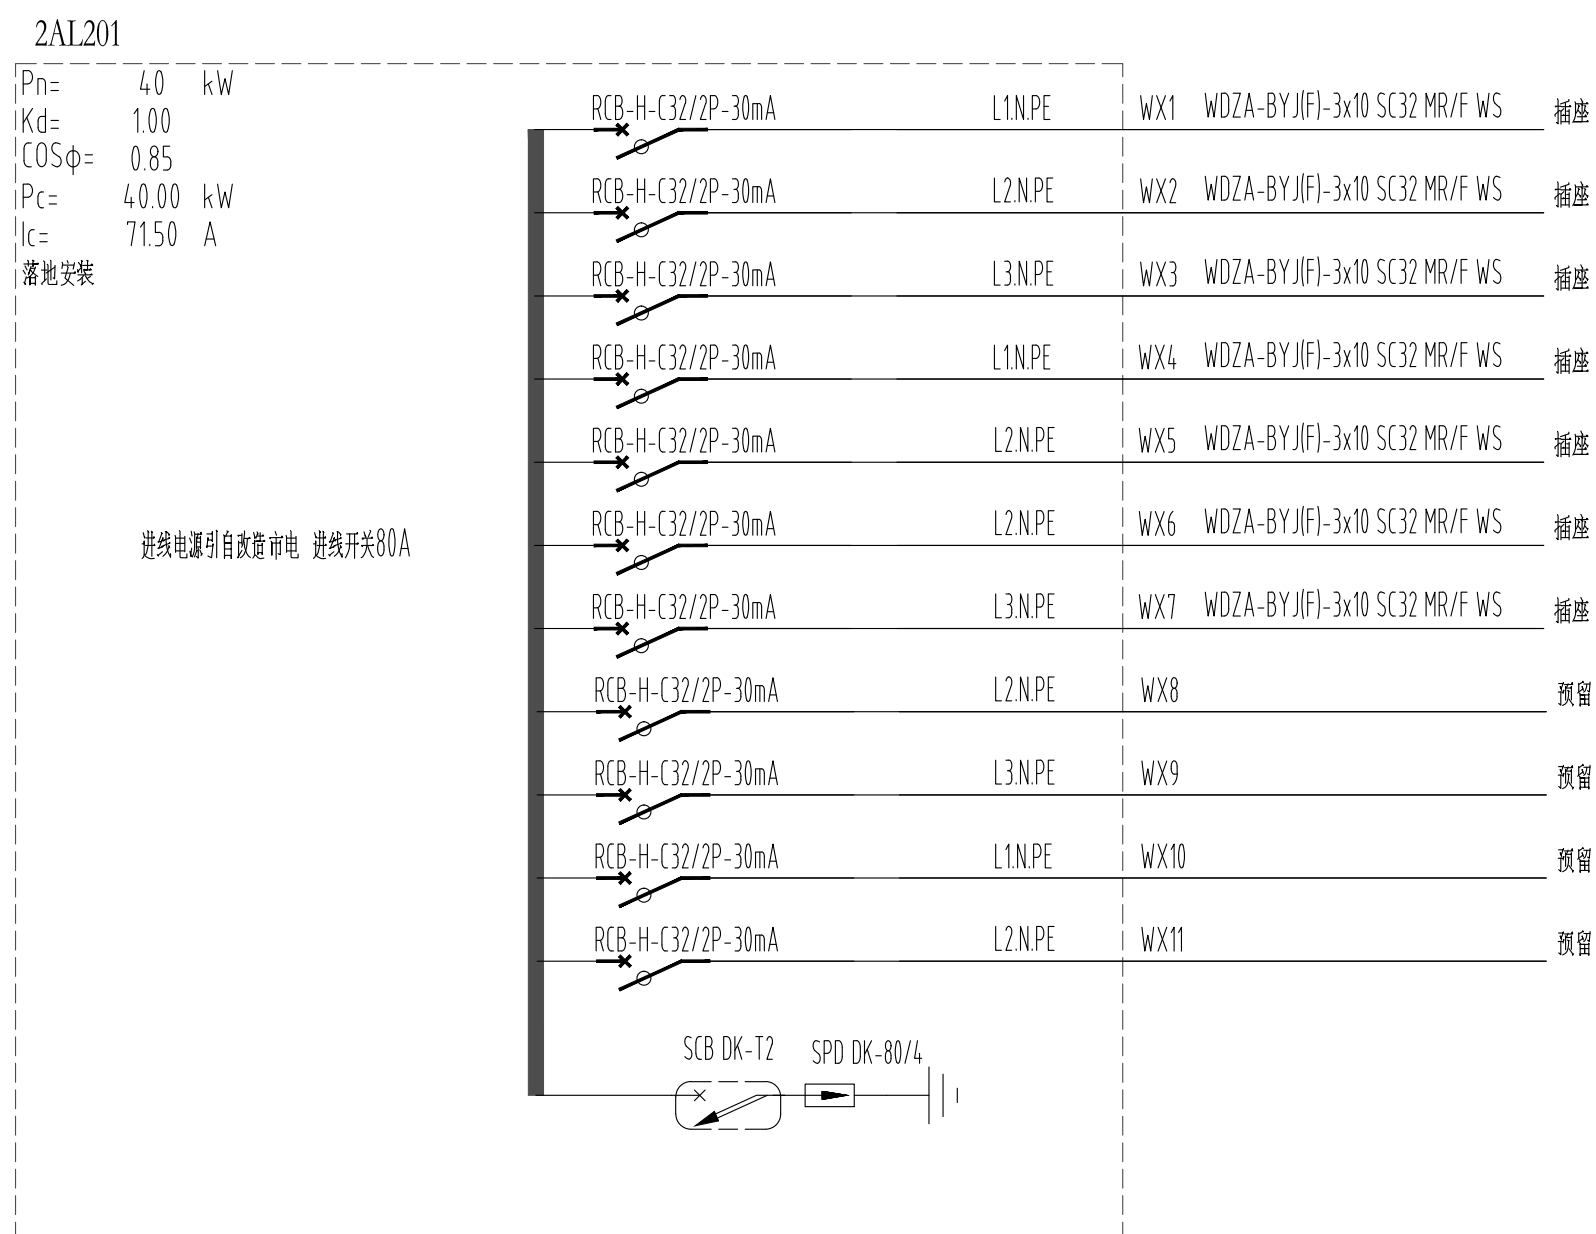

食堂区插座用电配电箱

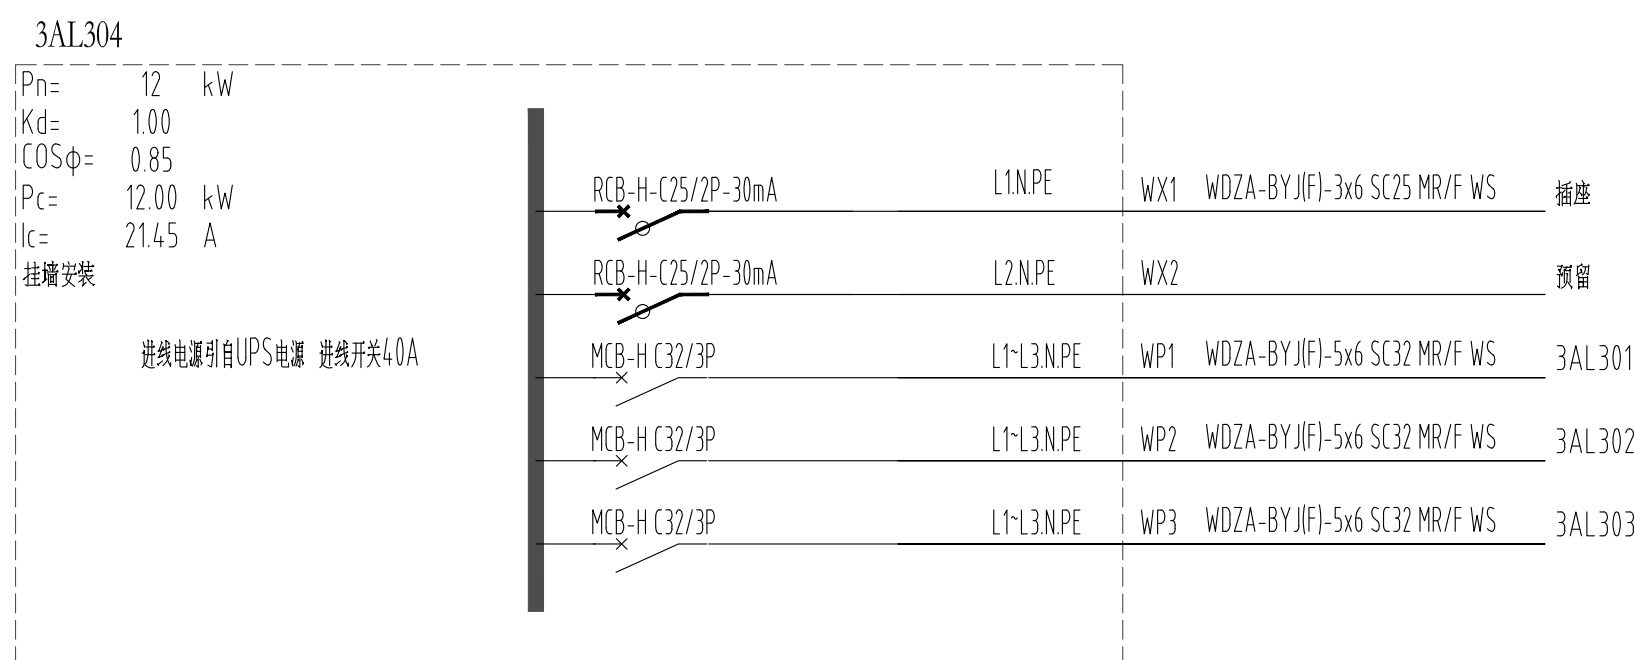

3层采访间UPS电源照明用电配电箱

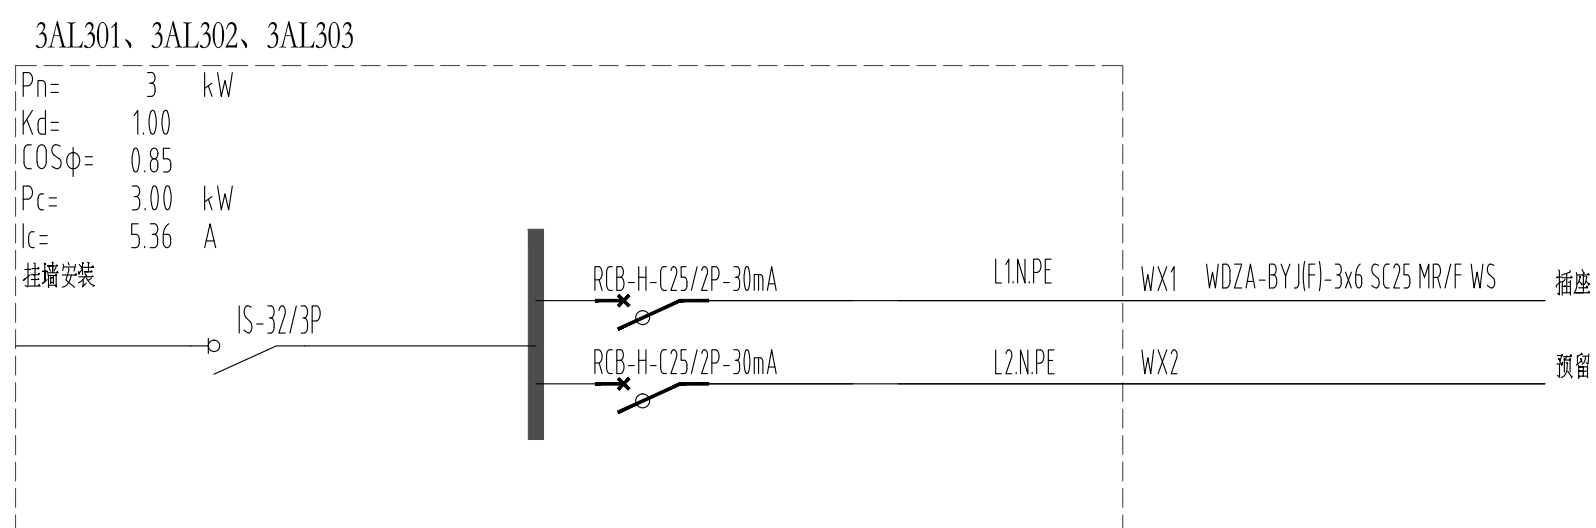

3层采访间UPS电源照明用电配电箱

[illegible]

注册执业栏		REGISTERED ARCHITECT/ENGINEER
姓 名	NAME	
注册证书号码	REGISTRATION CERTIFICATE NO.	
注册印章号码	STAMP NO.	
设计号:	JOB NO.	
工程名称	PROJECT TITLE	
成都大运会主新闻中心装饰搭建		
子项名称	SUB ITEM	

建设单位: 成都博雅文瑞文化传播有限公司

图 名	DRAWING TITLE
-----	---------------

配电箱系统图四

单位:	UNIT	图 题: 电视	DWG. CATEGORY
比例:	SCALE	图号: T04	DWG. NO.
日期: 2022.02	DATE	版本: A	SER. NO.
制图 DRAWN BY:	赵仕川		
设计 DESIGNED BY:	赵仕川		
校对 CHECKED BY:	鲜 杰		
专业负责人 DISCIPLINE CHIEF:	方 纯		
	赵仕川		
设计项目负责人 PROJECT CHIEF:			
审核 AUDIT:	方 纯		
审定 APPROVED BY:	鲜 立		

成都基准方中建筑设计股份有限公司
Chengdu JZfz Architectural Design Co., Ltd.

中国 成都市 琉璃路8号华润广场1座7-15楼
电话: +86 (28) 86333800 传真: +86 (28) 86582990

7-15F, Tower A, Criad Plaza, No.8, Liuli Road, Chengdu, P.R.C.
tel. +86(28) 86333800 fax. +86(28) 86582990

工程设计资质证书编号: A151016191

电子文档编号:

CAD FILENAME

版 权 说 明

COPYRIGHT DECLARATION

此图版权为成都基准方中建筑设计股份有限公司所有，未经许可不得使用。