

[illegible]

注册执业栏		REGISTERED ARCHITECT (ENR068)
姓 名:		NAM
注册证书号码:		REGISTERED NUMBER OF CERTIFICATE NO.
注册印章号码:		CERTIFICAT
设计号:	CD-20212856-F001	DESIGN NO.
工程名称:		PROJECT TITLE
成都大运会议中心装饰搭建		
子项名称:		SUBITEM
建设单位:		CLIENT
成都博雅文瑞文化传播有限公司		
图 表:		DRAWING TABLE


二层天花、灯具布置图			
单位	mm	DWG	DWG CADDWG
比例	1:200	SCALE	比例 室施
日期	2022.02	DATE	图号 C02
		版本	A
设计	设计	校对	审核
DESIGNED BY	李露文		
CHECKED BY	李露文		
专业负责人	李露文		
SPECIAL CHECK			
设计负责人	张敏		
PROJECT CHECK			
审核	张敏		
审批	李敏		

基准方中
成都基准方中建筑设计股份有限公司
Chengdu JZFC Architectural Design Co., Ltd.


中国 成都市 民权路8号华兴广场A座7-14楼
电话: +86(28) 86533000 传真: +86(28) 86582990
7-15F, Tower A, Citrad Plaza, No.8Jialin Road, Chengdu, P.R.C
Tel: +86(28) 86533000 fax: +86(28) 86582990

工程设计资质证书编号: A151016191


版 权 说 明
COPYRIGHT DECLARATION

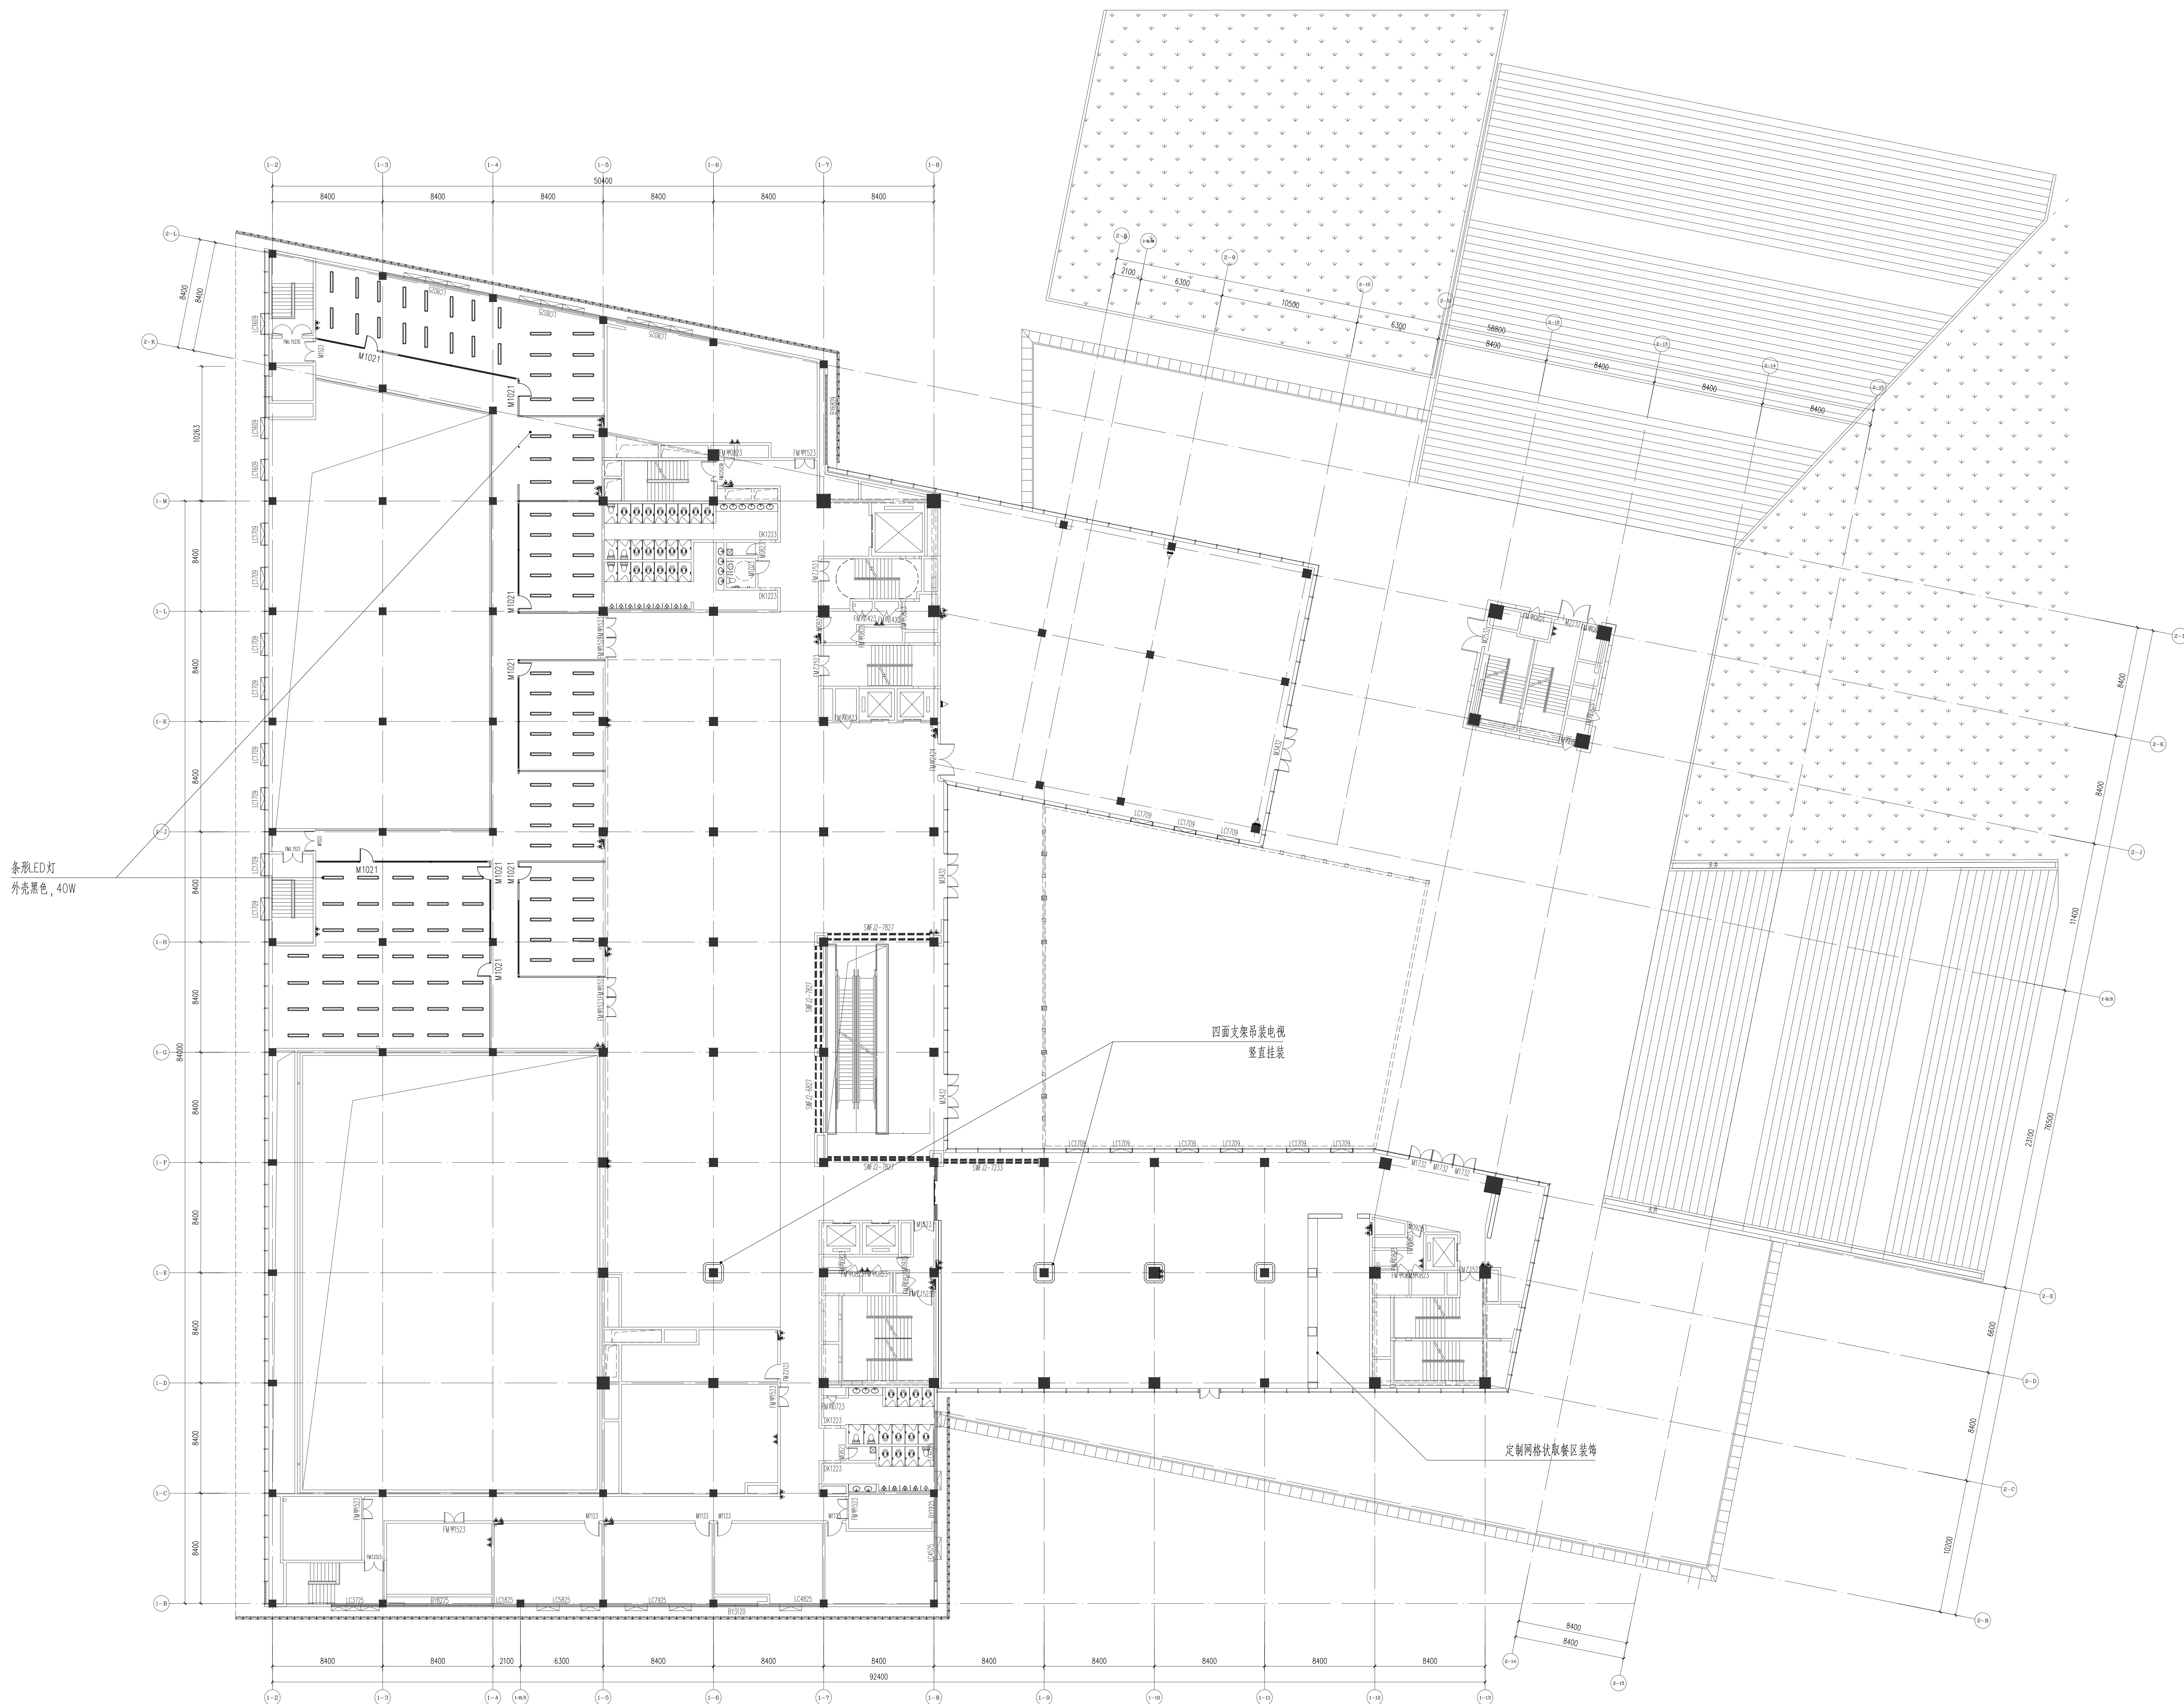


二层天花、灯具布置图 1:200

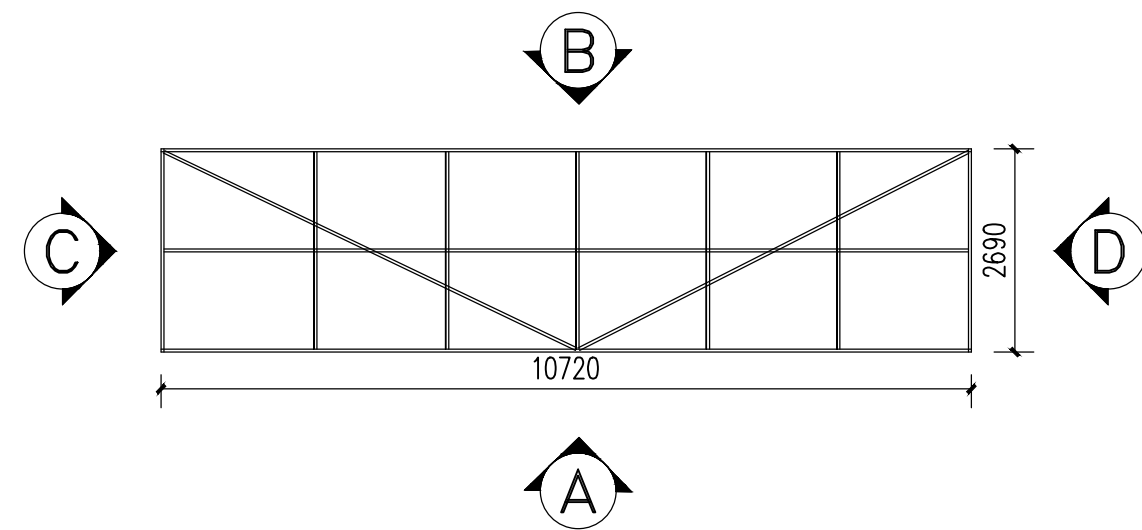

① 隔墙短边平面钢骨架图 1:100

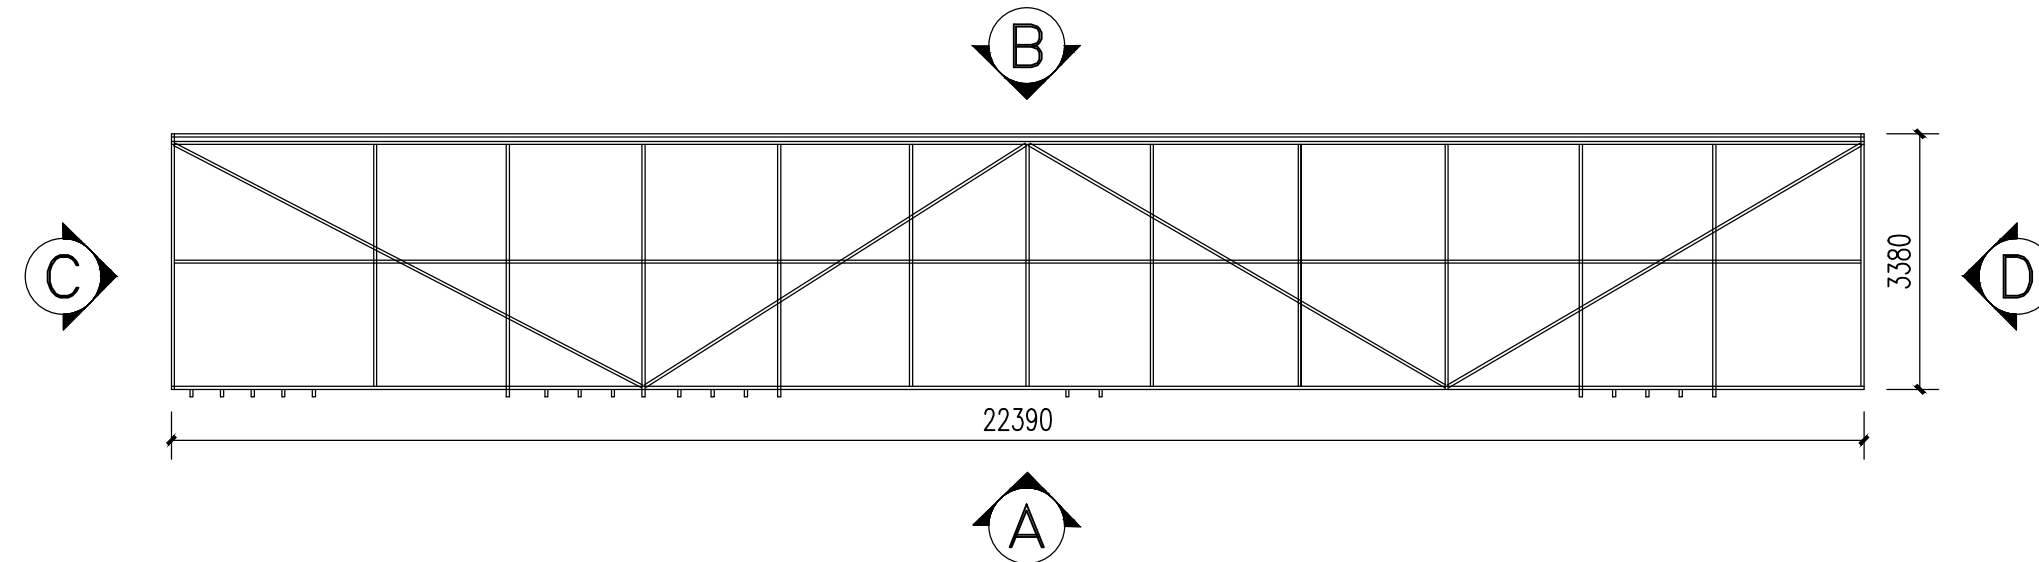


② 隔墙长边平面钢骨架图 1:100

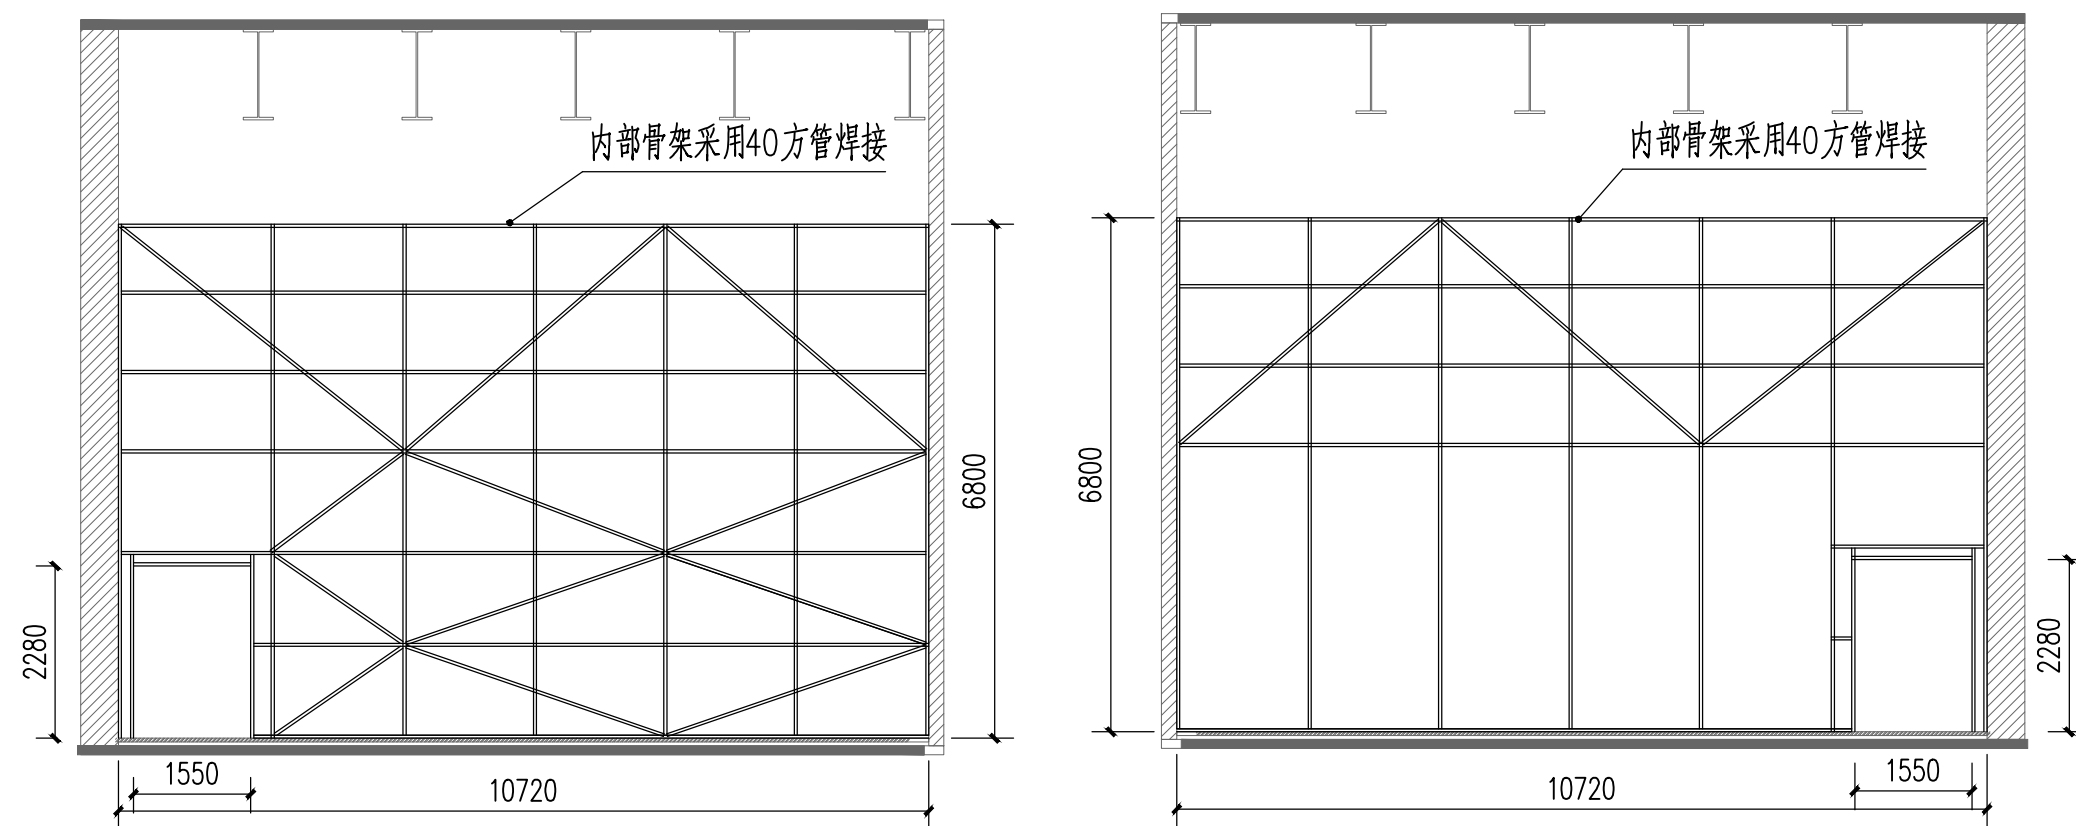


隔墙短边A立面钢骨架图 1:100

隔墙短边B立面钢骨架图 1:100

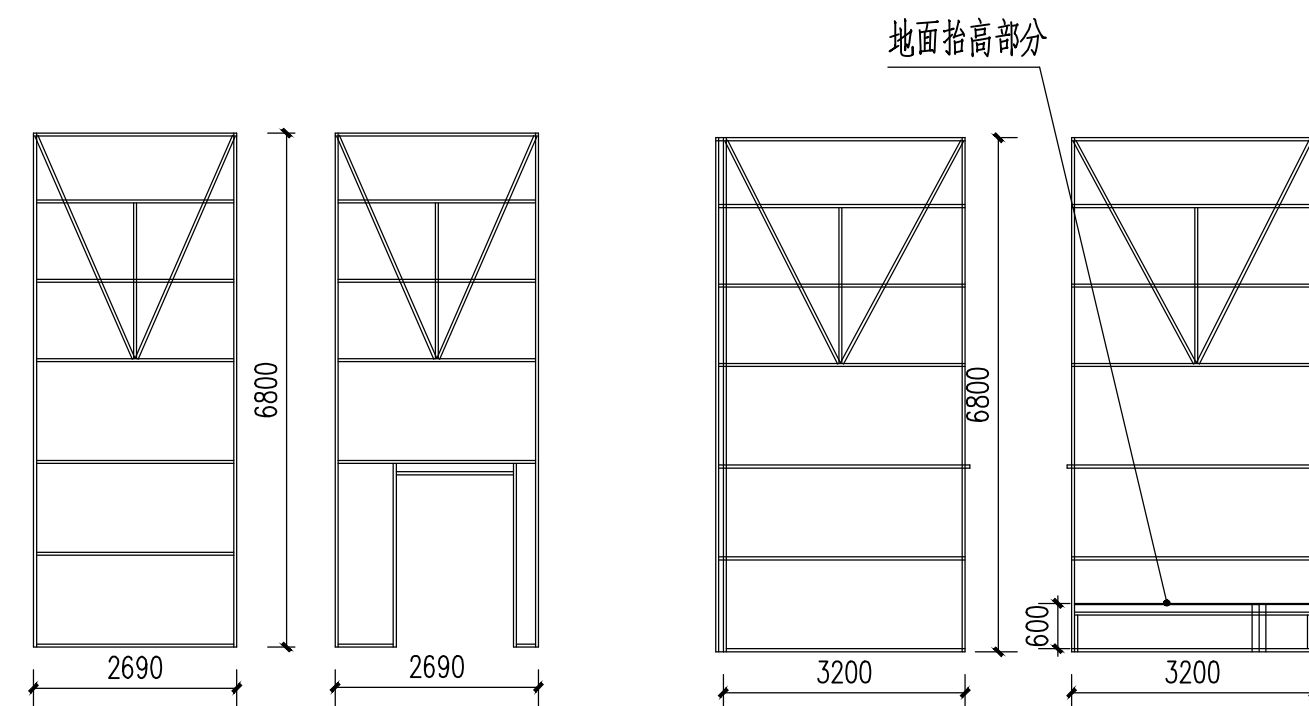

隔墙短边CD立面钢骨架图 1:100

隔墙长边CD立面钢骨架图 1:100

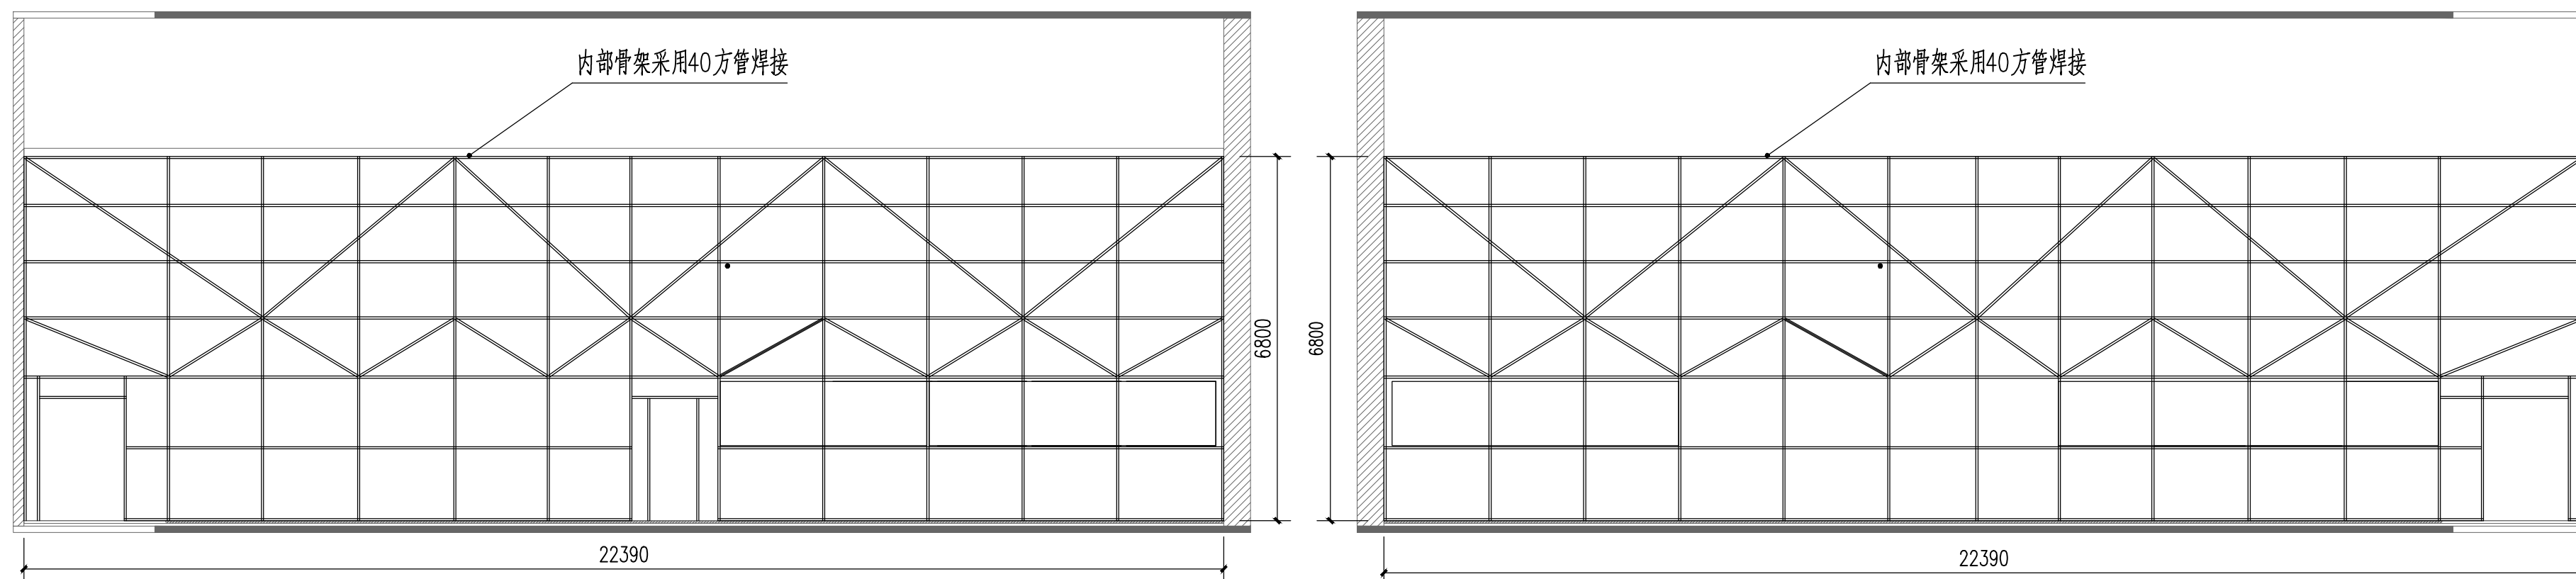


隔墙长边A立面钢骨架图 1:100

隔墙长边B立面钢骨架图 1:100

出图记录		ISSUE NOTES	
版 本 REV.	日 期 DATE	备 注 REMARK	
A	2022.02		
注册执业栏		REGISTERED ARCHITECT/ENGINEER	
姓 名		NAME	
注册证书号码		REGISTRATION CERTIFICATE NO.	
注册印章号码		STAMP NO.	
设计号：CD-20212856-F001		JOB NO.	
工程名称		PROJECT TITLE	
成都大运会主新闻中心装饰搭建			
子项名称		SUB ITEM	
建设单位		CLIENT	
成都博雅文瑞文化传播有限公司			
图 名		DRAWING TITLE	
新闻发布厅隔墙钢骨架排布图			
单 位 mm	UNIT	图 號 室施	DWG. CATEGORY
比 例 1: 100	SCALE	图 号: D01	DWG. NO.
日 期 2022.02	DATE	版 本 A	VER. NO.
制 图 DRAWN BY	方苓		
设 计 DESIGNED BY	方苓		
校 对 CHECKED BY	李霜文		
专业负责人 DISCIPLINE CHIEF	肖子颖		
设计总负责人 PROJECT CHIEF	张峻		
审 核 AUDIT	张峻		
审 定 APPROVED BY	华柯		
园 基准方中 成都基准方中建筑设计股份有限公司 Chengdu JZFY Architectural Design Co., Ltd. 中国 成都市 琉璃路9号华润广场A座7-15楼 电话: +86(28) 86333800 传真: +86(28) 86582990 7-15F, Tower A, Cirlend Plaza, No.8,Liuli Road , Chengdu, P.R.C tel. +86(28) 86333800 fax. +86(28) 86582990 工程资质证书编号: A151016191 CAD FILENAME 电子文档编号: - 版 权 说 明 COPYRIGHT DECLARATION 此图版权为成都基准方中建筑设计股份有限公司所有，未经许可不得使用。			


采暖通风	总图		
电气	给排水		
暖通	结构		
五金	栏杆		

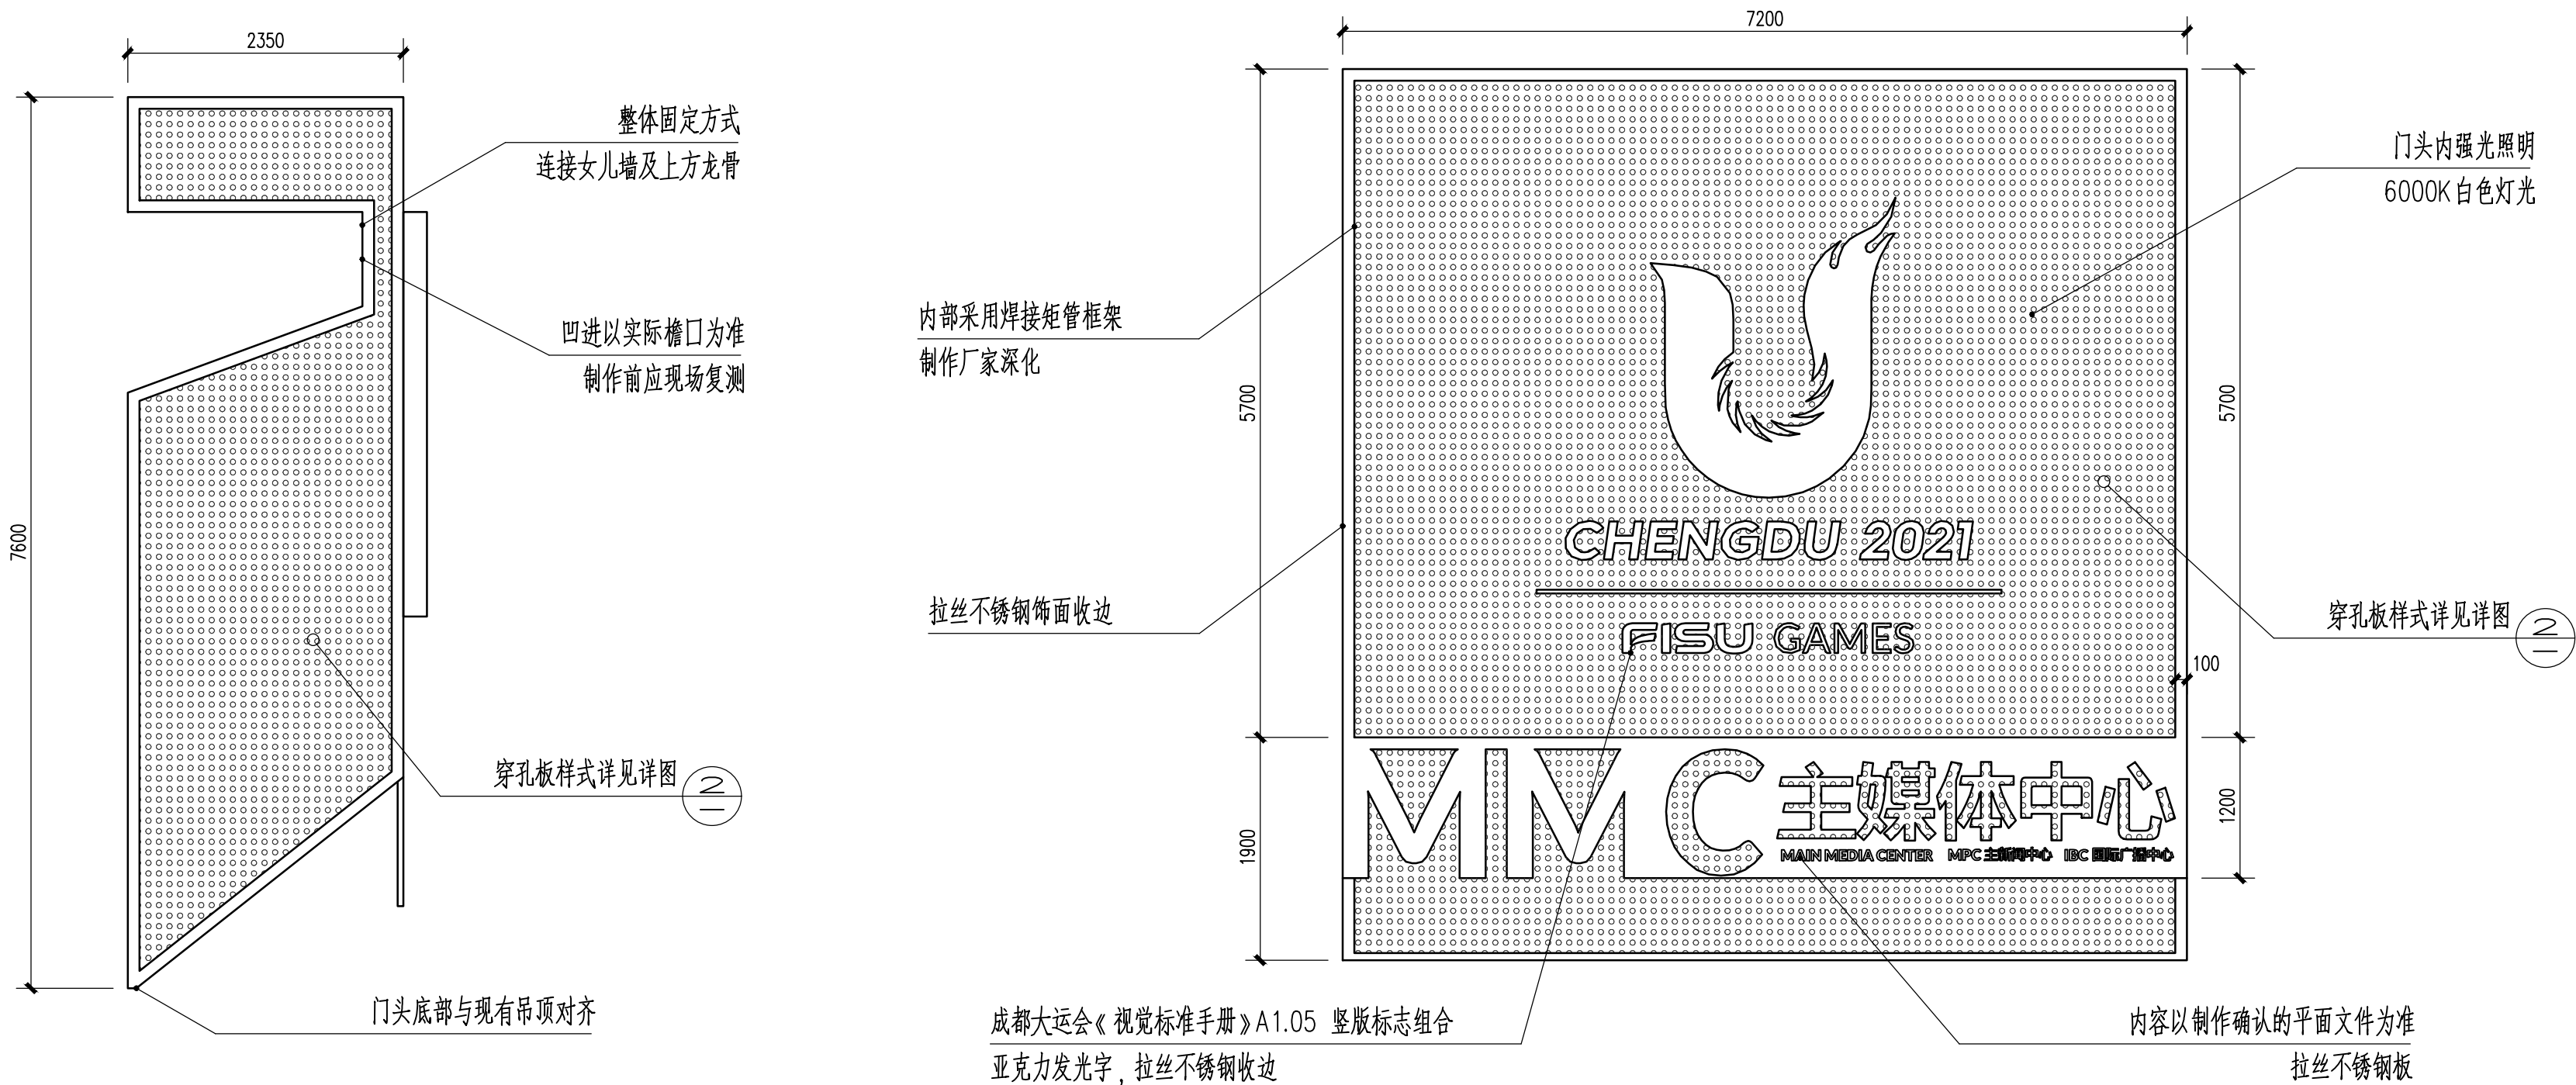


西入口门头侧视图 1:100

西入口门头正视图 1:100

① 西入口门头大样图 1:100

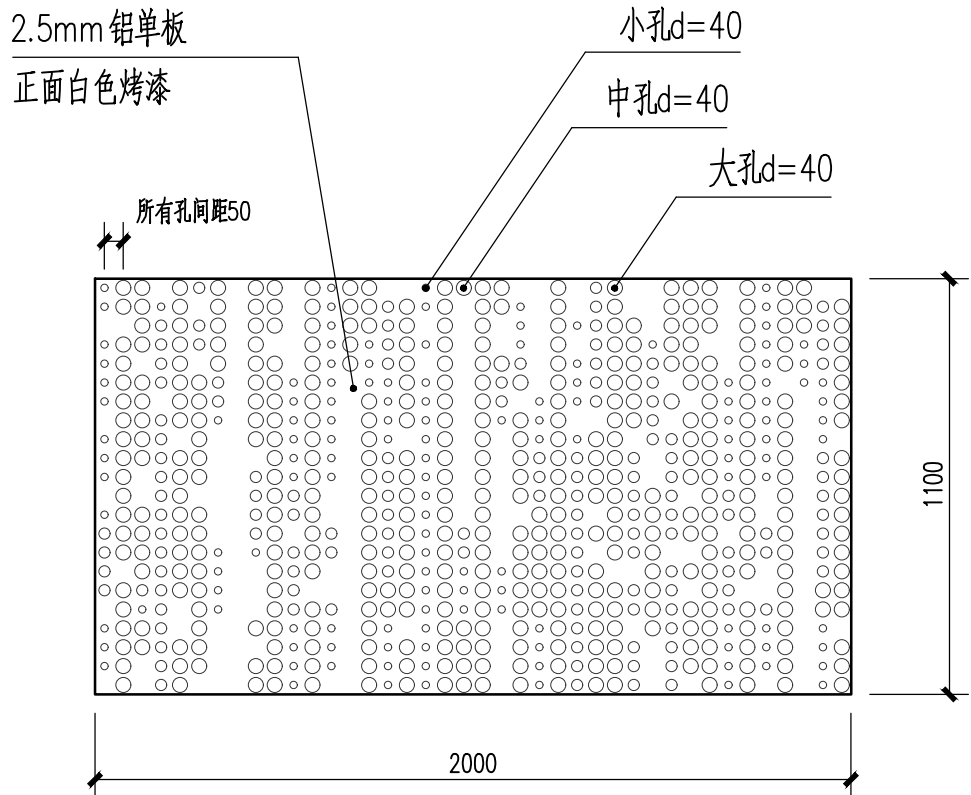


② 西入口门头穿孔板样式图 1:20

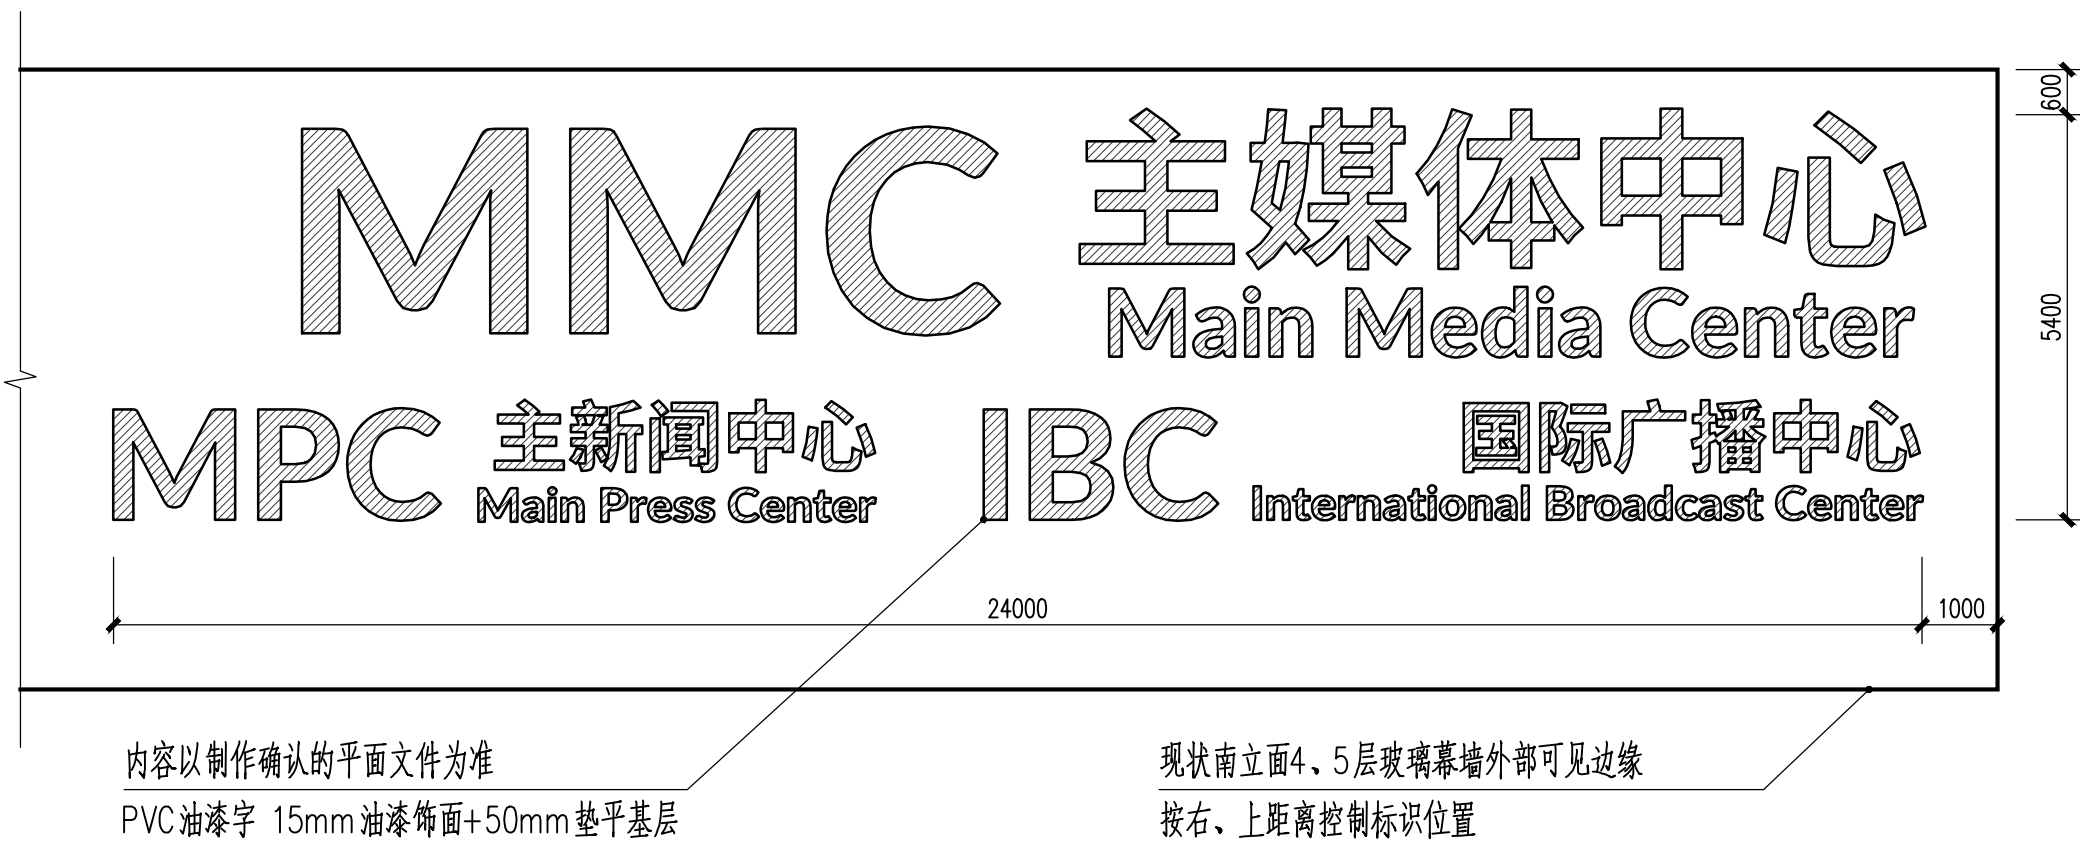


③ 南立面标识立面图 1:100

出图记录		ISSUE NOTES
版 本	日 期	备 注
REV.	DATE	REMARK
A	2022.02	
注册执业栏		REGISTERED ARCHITECT/ENGINEER
姓 名		NAME
注册证书号码		REGISTRATION CERTIFICATE NO.
注册印章号码		STAMP NO.
设计号: CD-20212856-F001		JOB NO.
工程名称		PROJECT TITLE
成都大运会主新闻中心装饰搭建		
子项名称		SUB ITEM
建设单位		CLIENT
成都博雅文瑞文化传播有限公司		
图 名		DRAWING TITLE
西入口门头、南立面标识大样图		
单 位	mm	UNIT
图 别	室 施	DWG. CATEGORY
比 例	—	SCALE
图 号	D02	DWG. NO.
日 期	2022.02	DATE
版 本	A	VER. NO.
制 图	张 丽	
设 计	肖子颖	
校 对	李 珊 文	
专业负责人	肖子颖	
DISCIPLINE CHIEF		
设计总负责人	张 峻	
PROJECT CHIEF		
审 核	张 峻	
AUDIT		
审 定	华 柯	
APPROVED BY		
国 基准方中		
成都基准方中建筑设计股份有限公司		
Chengdu JZfZ Architectural Design Co., Ltd.		
中国 成都市 琉璃路8号华润广场A座7-15楼		
电话: +86(28) 86333800 传真: +86(28) 86582990		
7-15F, Tower A, Grand Plaza, No.8, Liuli Road, Chengdu, P.R.C		
tel. +86(28) 86333800 fax. +86(28) 86582990		
工程设计资质证书编号: A151016191		
电子文档编号: —		
CAD FILENAME		
版 权 说 明		
COPYRIGHT DECLARATION		
此图版权为成都基准方中建筑设计股份有限		
公司所有, 未经许可不得使用。		


采暖通风					
总图					

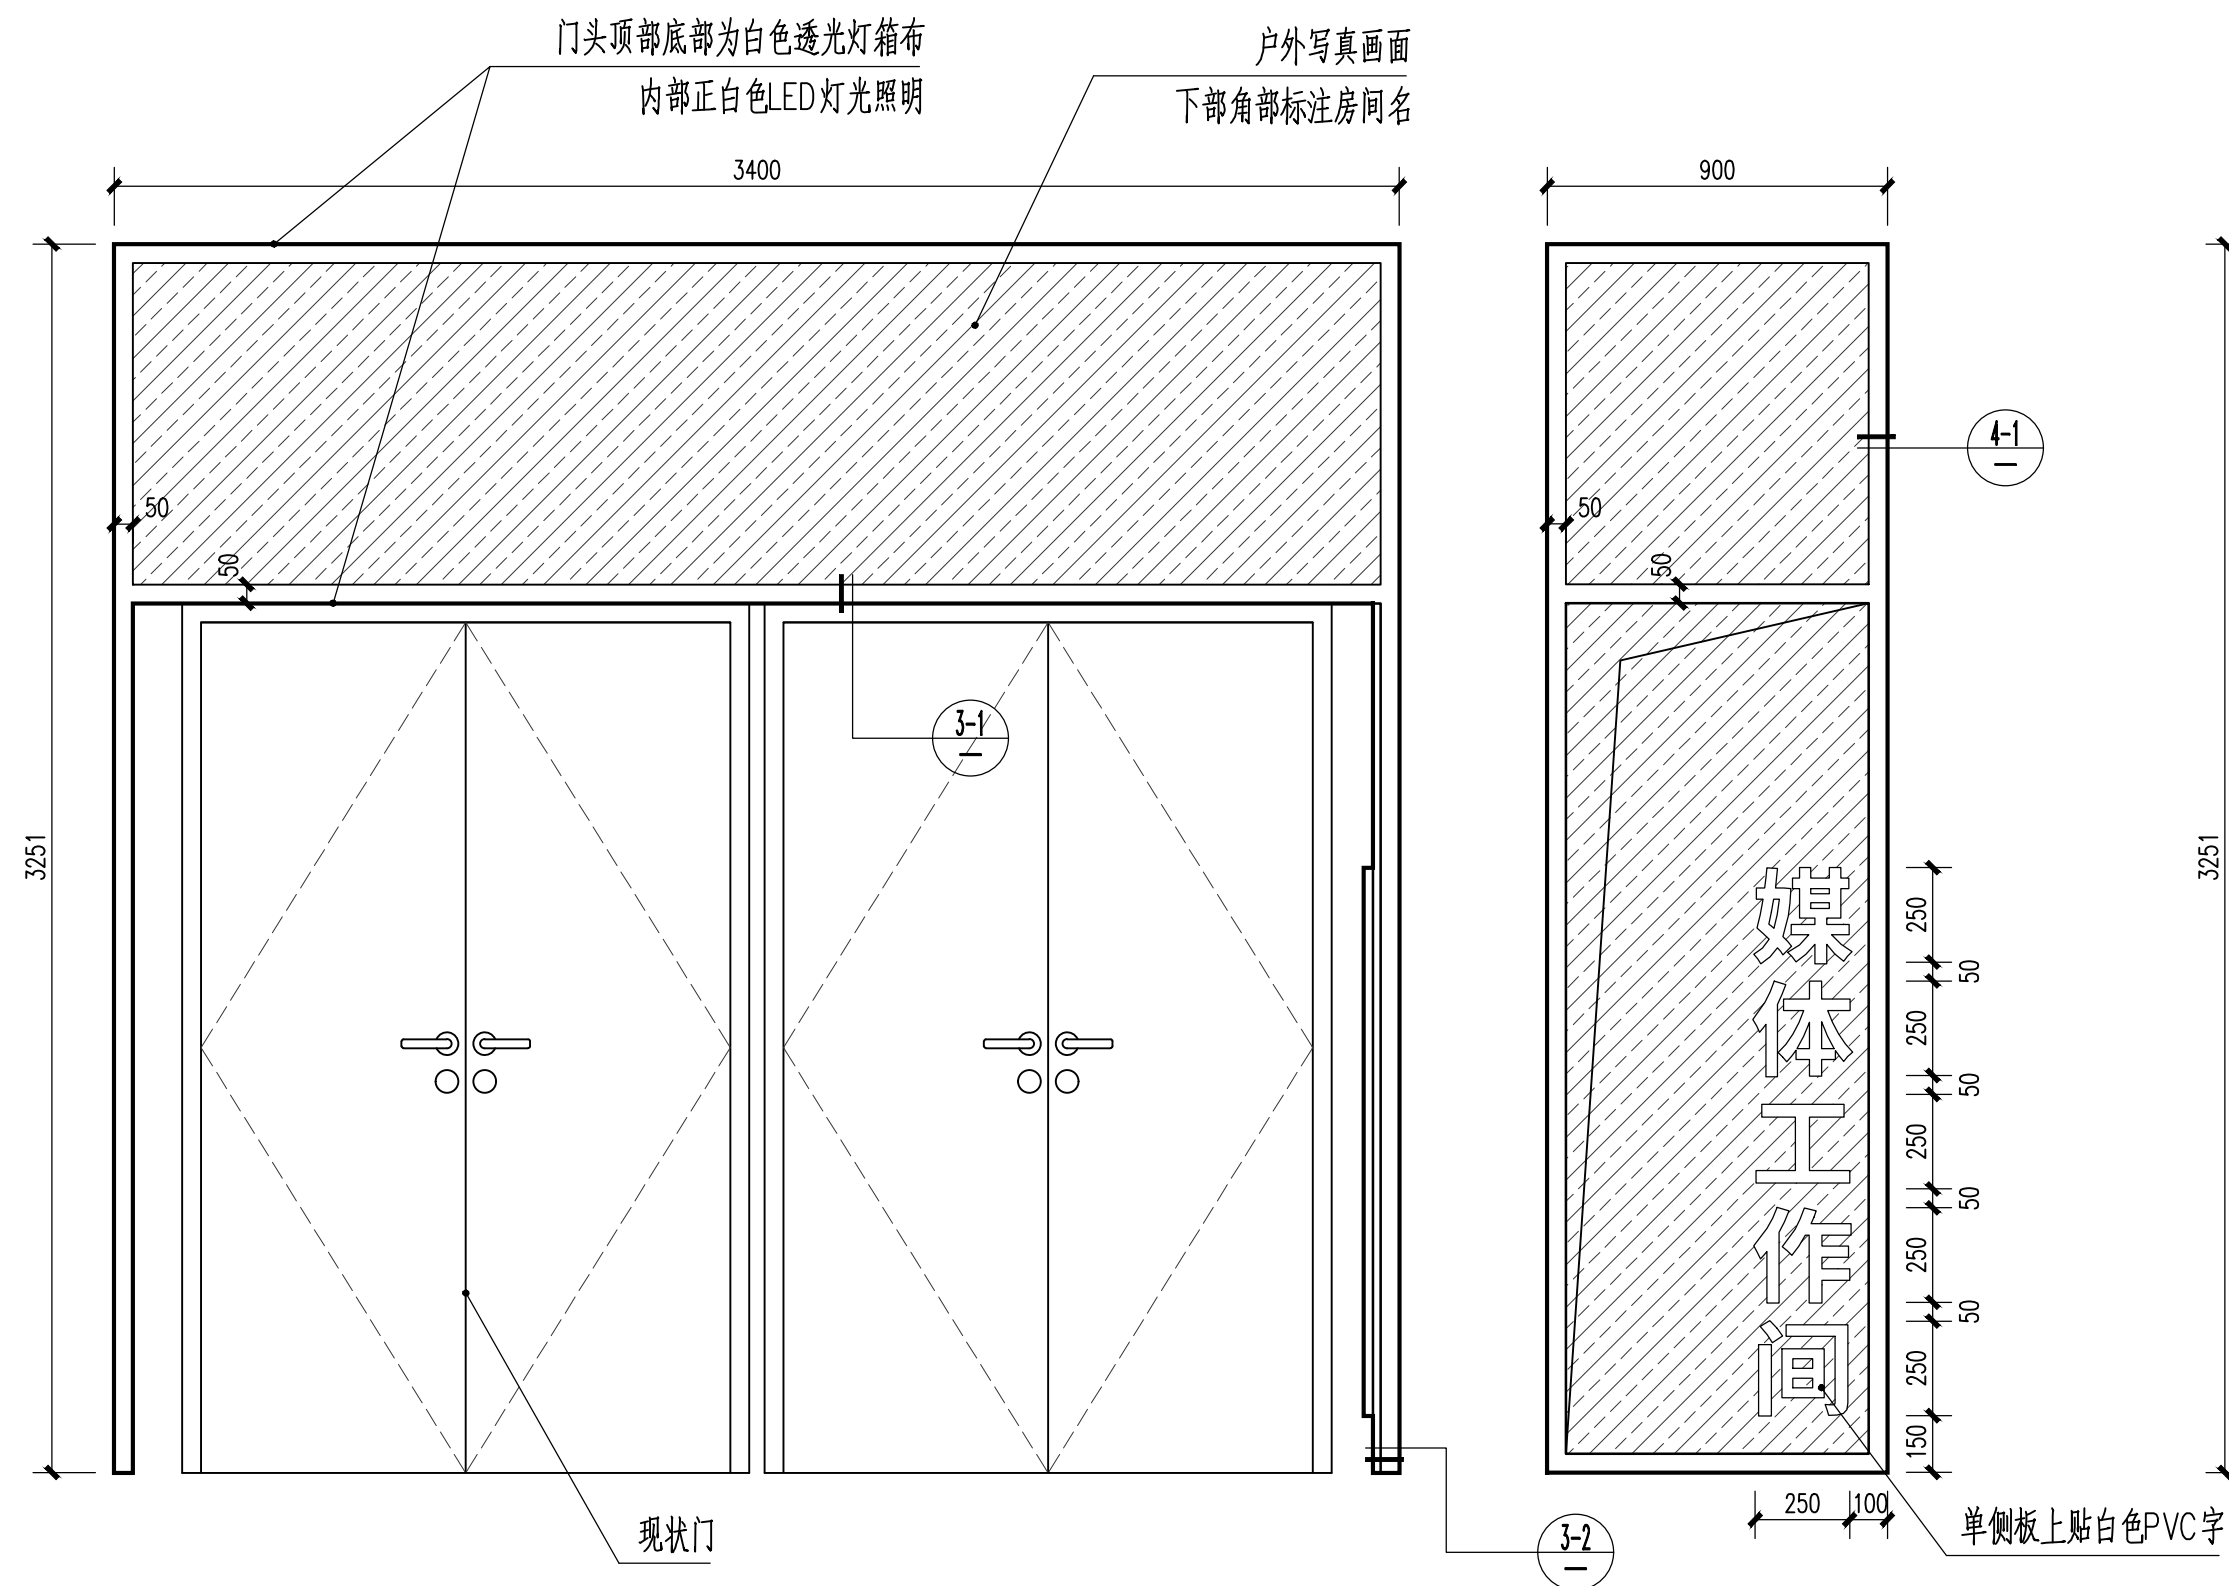


① 门框(大)正、侧立面图 1:20

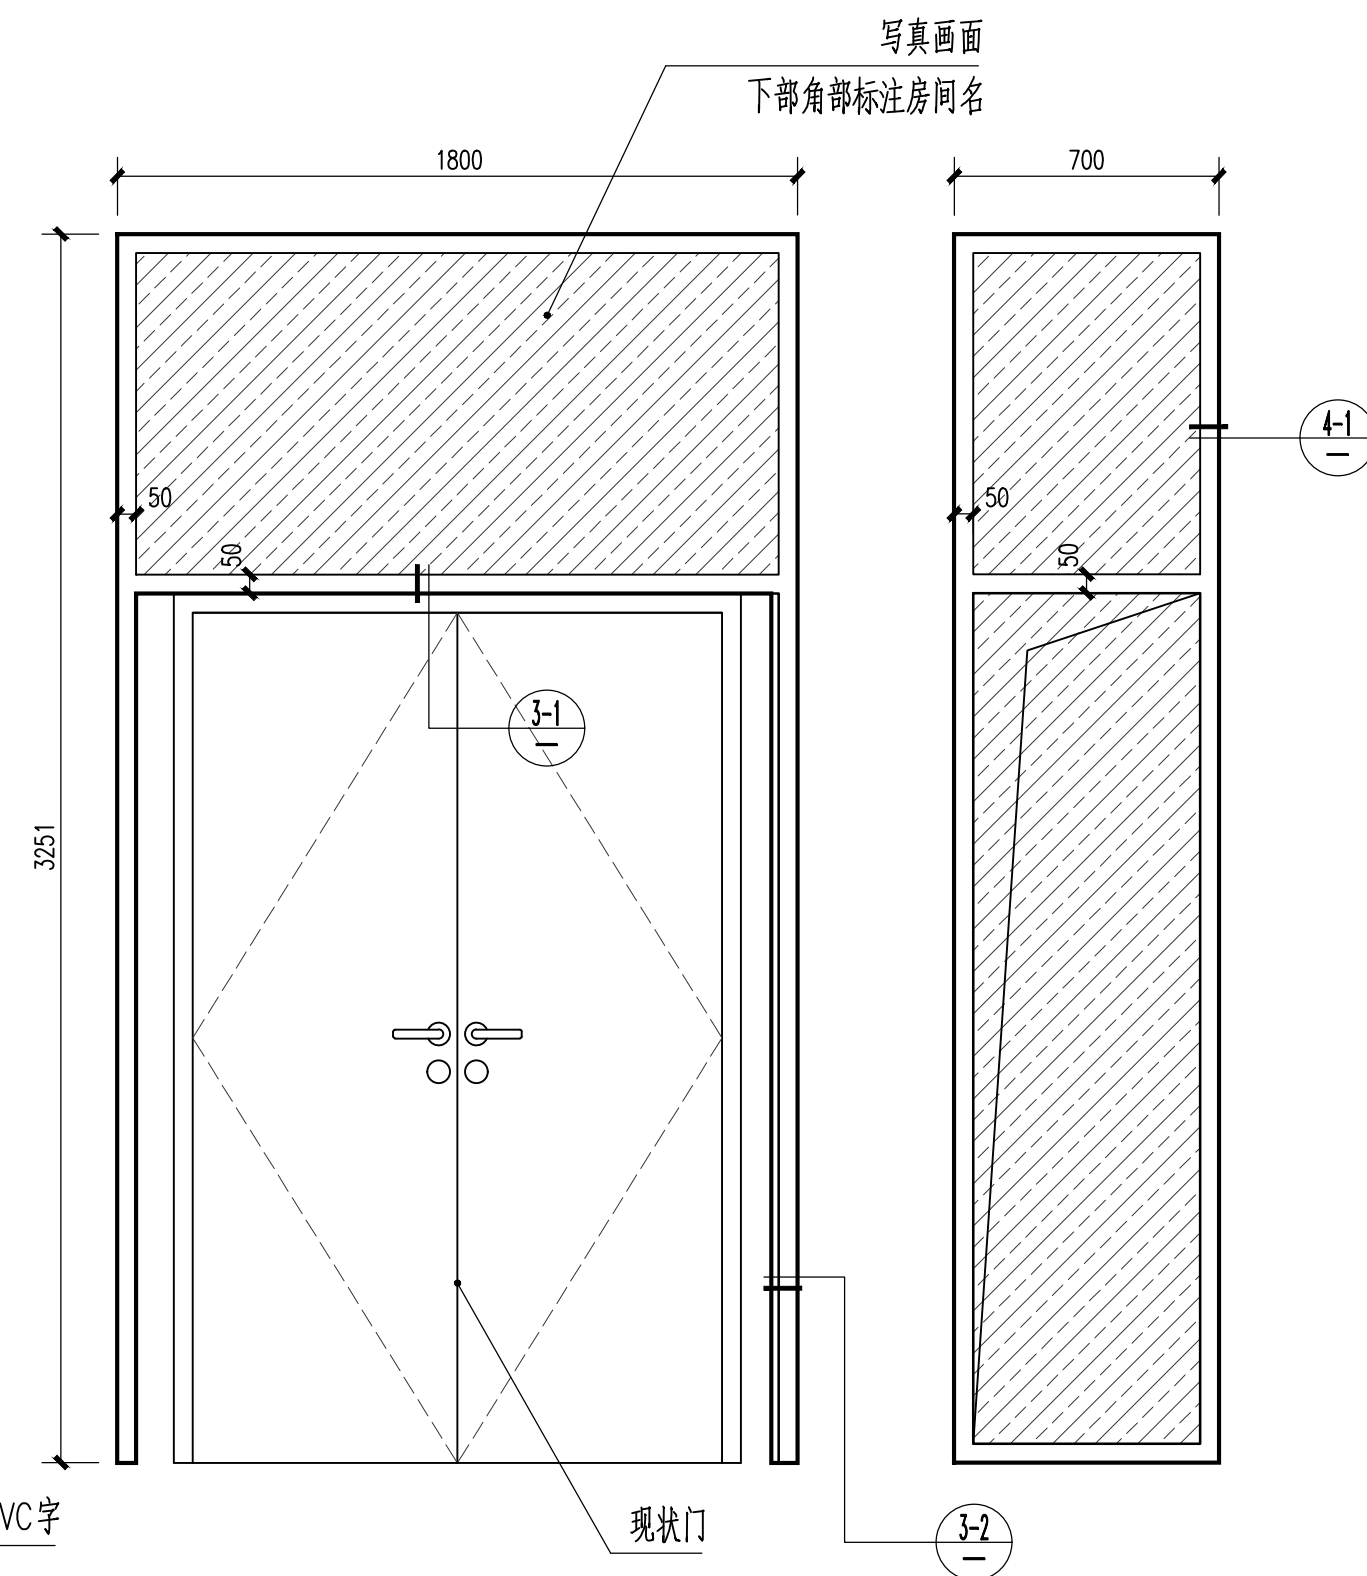

② 门框(小)正、侧立面图 1:20

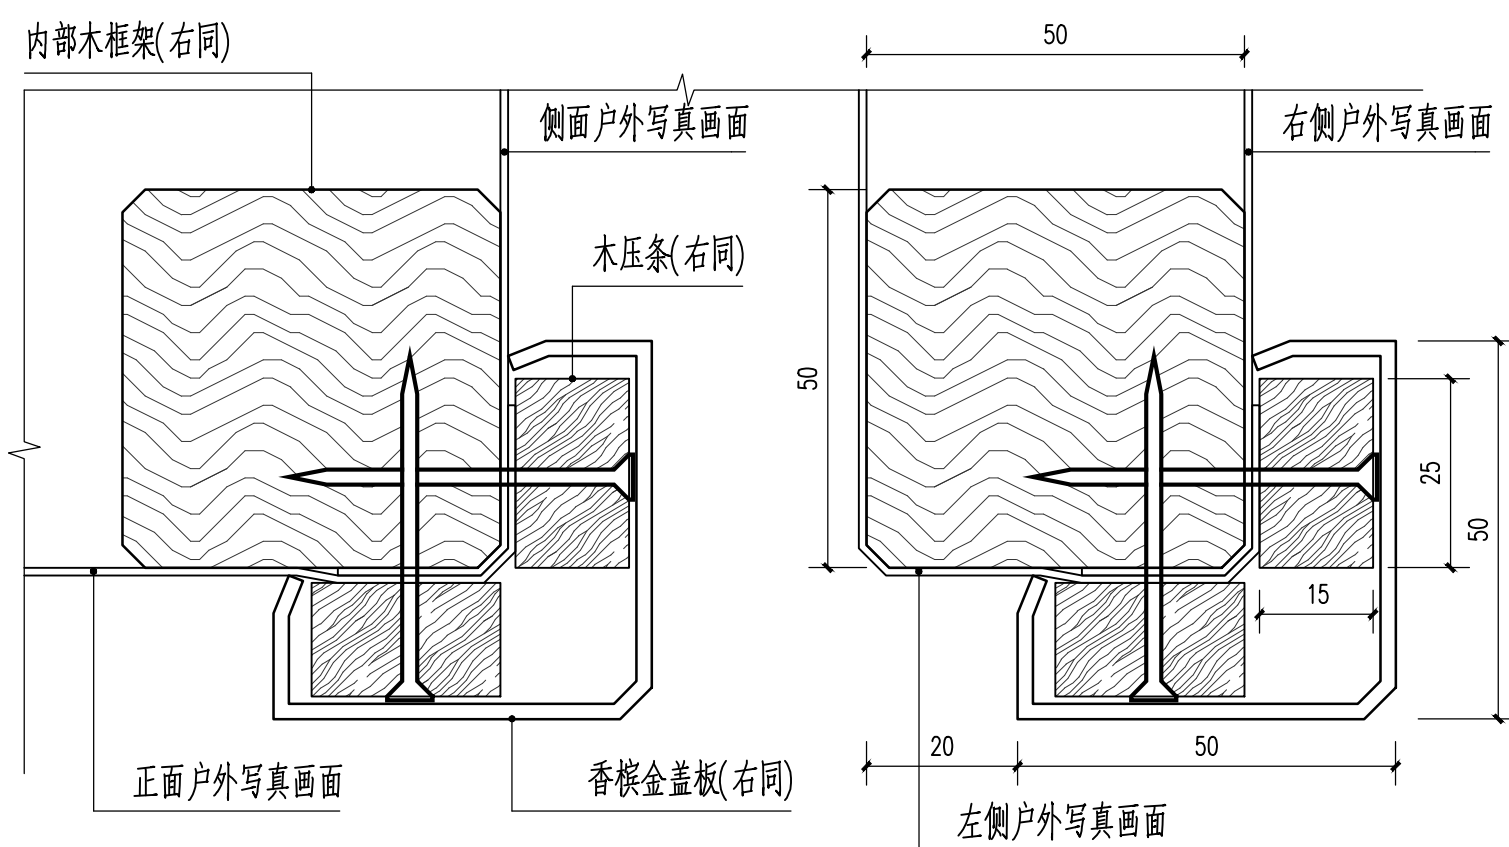

③-1 门框边框(角部)大样图 1:1 ③-2 门框边框(端部)大样图 1:1

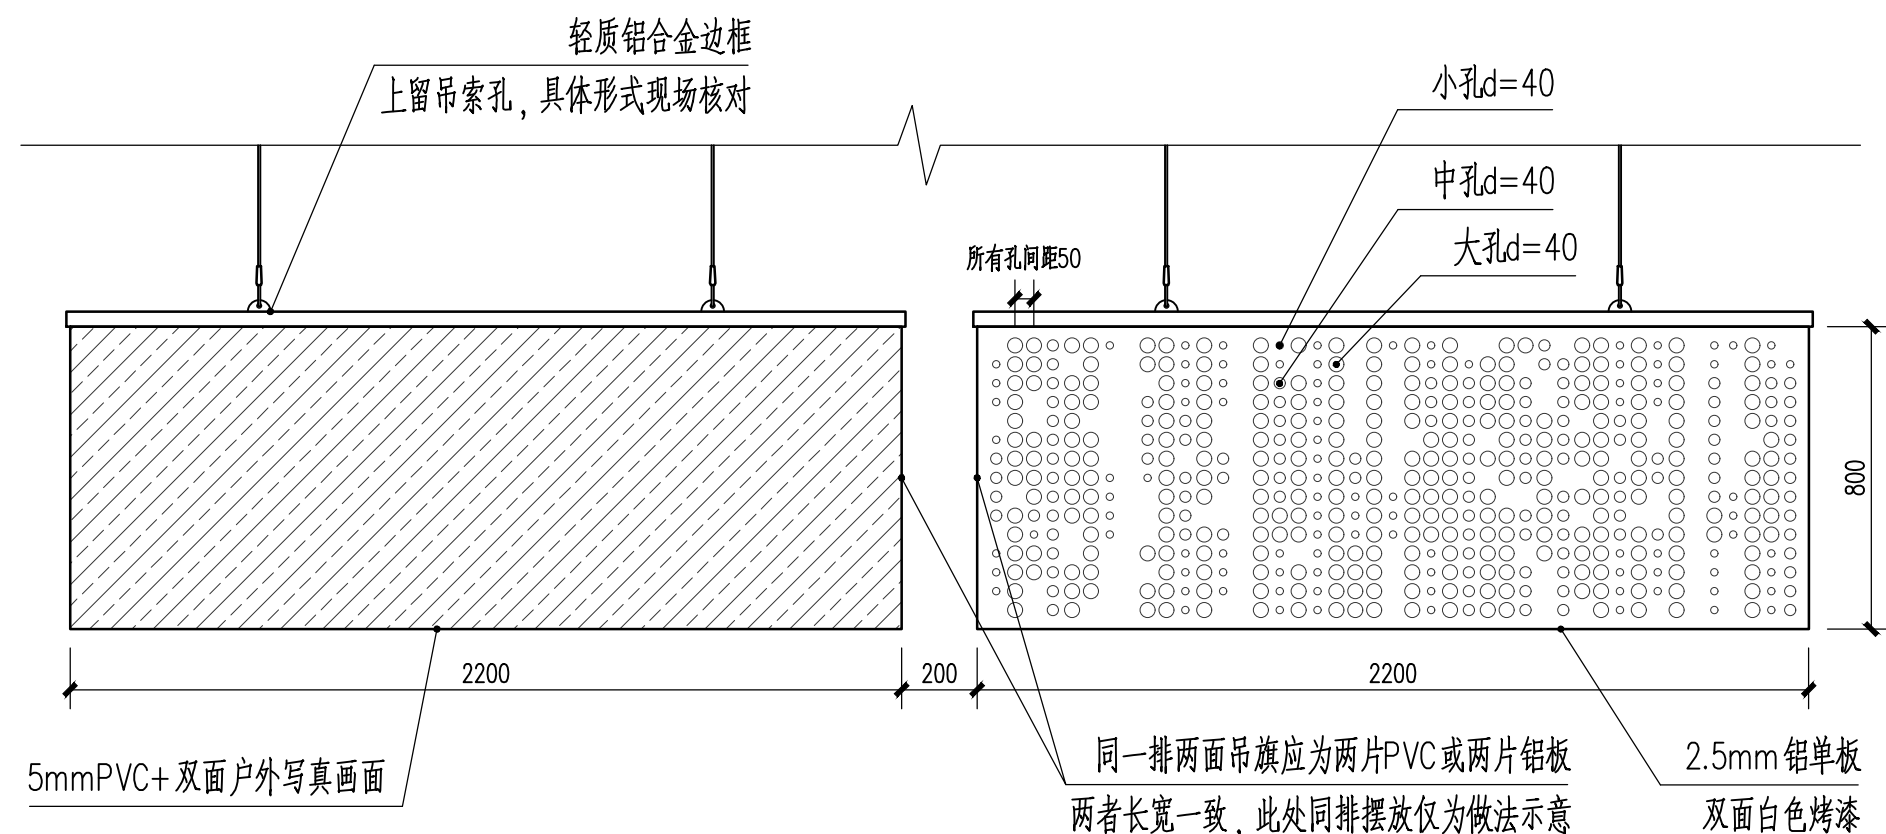


④ 吊旗大样图 1:20

出图记录						ISSUE NOTES	
版 本 REV.		日 期 DATE		备 注 REMARK			
A		2022.02					
注册执业栏						REGISTERED ARCHITECT/ENGINEER	
姓 名						NAME	
注册证书号码						REGISTRATION CERTIFICATE NO.	
注册印章号码						STAMP NO.	
设计号：CD-20212856-F001						JOB NO.	
工程名称						PROJECT TITLE	
成都大运会主新闻中心装饰搭建							
子项名称						SUB ITEM	
建设单位						CLIENT	
成都博雅文瑞文化传播有限公司							
图 名						DRAWING TITLE	
西入口通道与发布厅外侧通道 门框大样图、吊旗大样图							
单 位 mm		UNIT		图 號 室施		DWG. CATEGORY	
比 例 —		SCALE		图 号 D03		DWG. NO.	
日 期 2022.02		DATE		版 本 A		VER. NO.	
制 图 DRAWN BY		雷鑫鹏					
设 计 DESIGNED BY		肖子颖					
校 对 CHECKED BY		李耀文					
专业负责人 DISCIPLINE CHIEF		肖子颖					
设计总负责人 PROJECT CHIEF		张峻					
审 核 AUDIT		张峻					
审 定 APPROVED BY		华轲					
国 基准方中 成都基准方中建筑设计股份有限公司 Chengdu JZFF Architectural Design Co., Ltd. 中国 成都市 琉璃场8号华润广场A座7-14楼 电话：+86(28) 86333800 传真：+86(28) 86582990 7-15F, Tower A, Criland Plaza, No.8Jinli Road , Chengdu, P.R.C tel. +86(28) 86333800 fax. +86(28) 86582990 工程设计资质证书编号： A151016191 电子文档编号： - CAD FILENAME 版 权 说 明 COPYRIGHT DECLARATION 此图版权为成都基准方中建筑设计股份有限公司所有，未经许可不得使用。							




①落地发光字M大样图 1:10

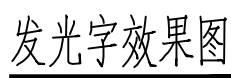


②落地发光字P大样图 1:10


版 本 REV.		日 期 DATE	备 注 REMARK	
A		2022.02		

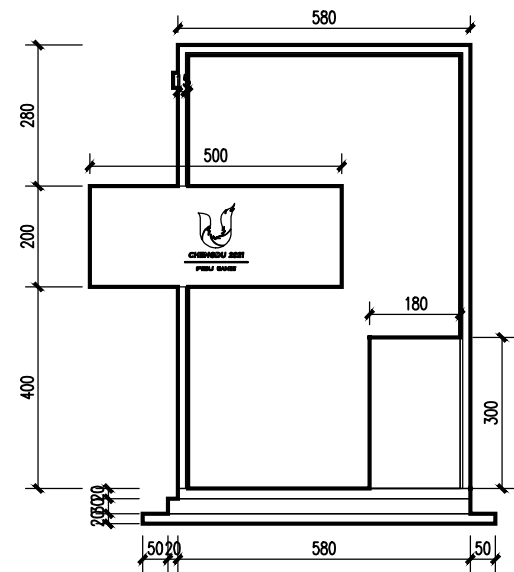


A花箱 前视图 1:15

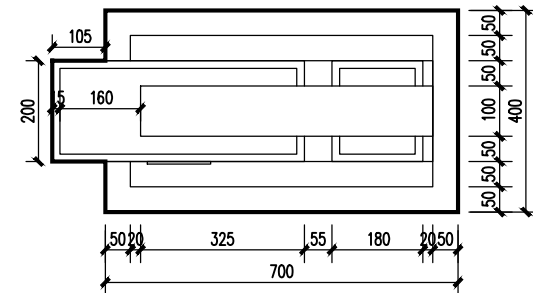

A花箱 顶视图 1:15

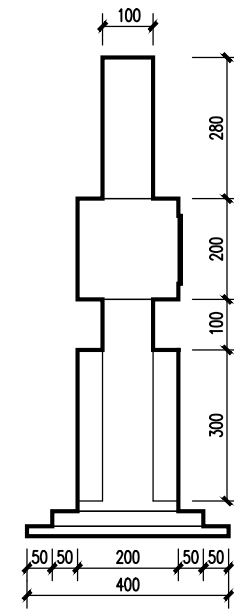

A花箱 侧视图 1:15

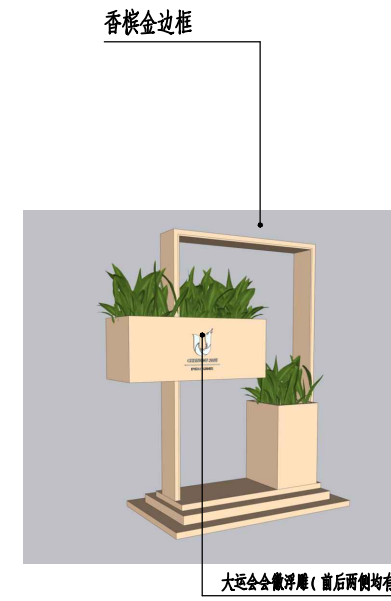


A花箱(餐厅)透视图




A花箱(综合服务区、报告厅入口)透视图


① A花箱大样图 1:15

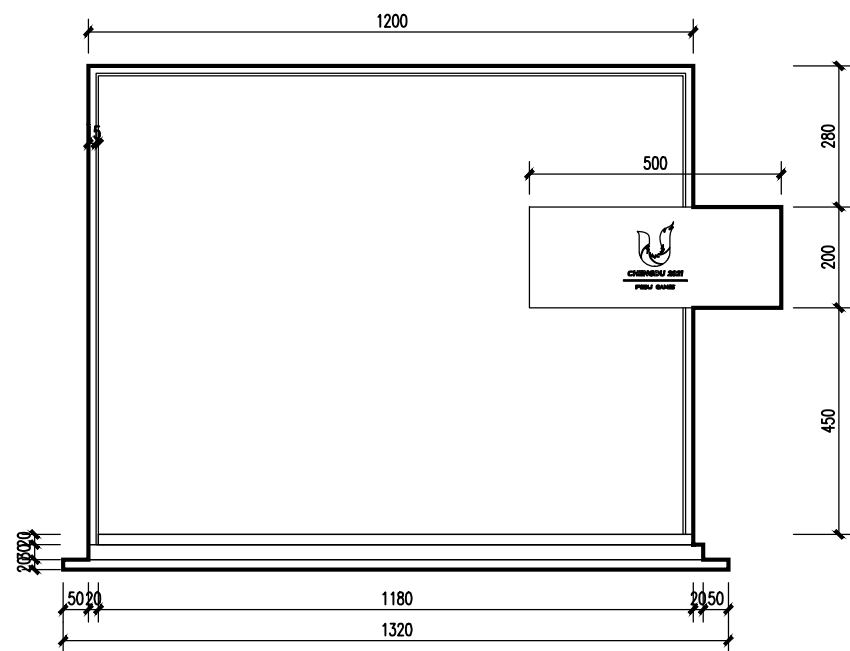


B花箱 前视图 1:15

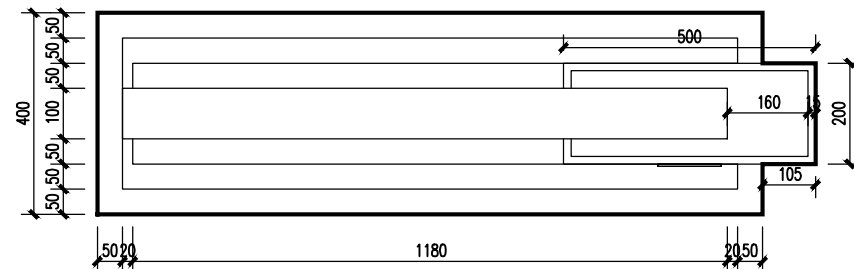

B花箱 顶视图 1:15

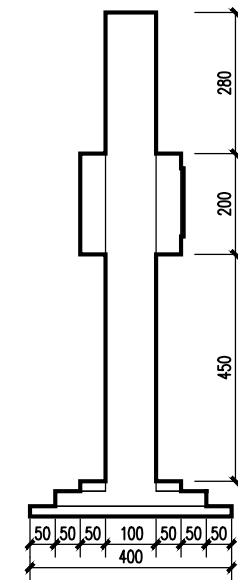

B花箱 侧视图 1:15

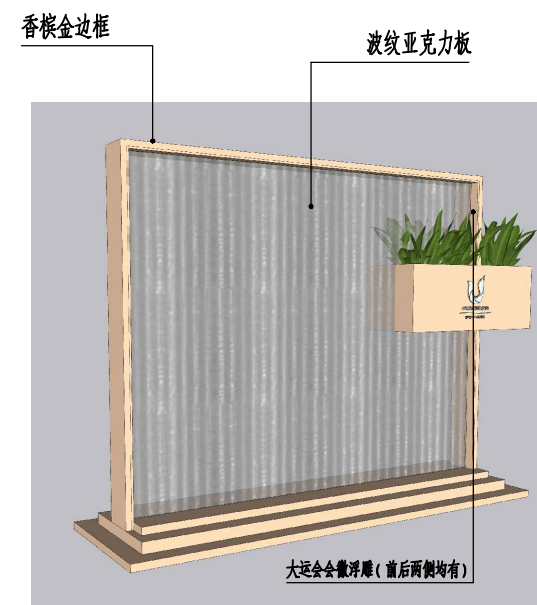


B花箱(餐厅)透视图




B花箱(综合服务区、报告厅入口)透视图


② B花箱大样图 1:15

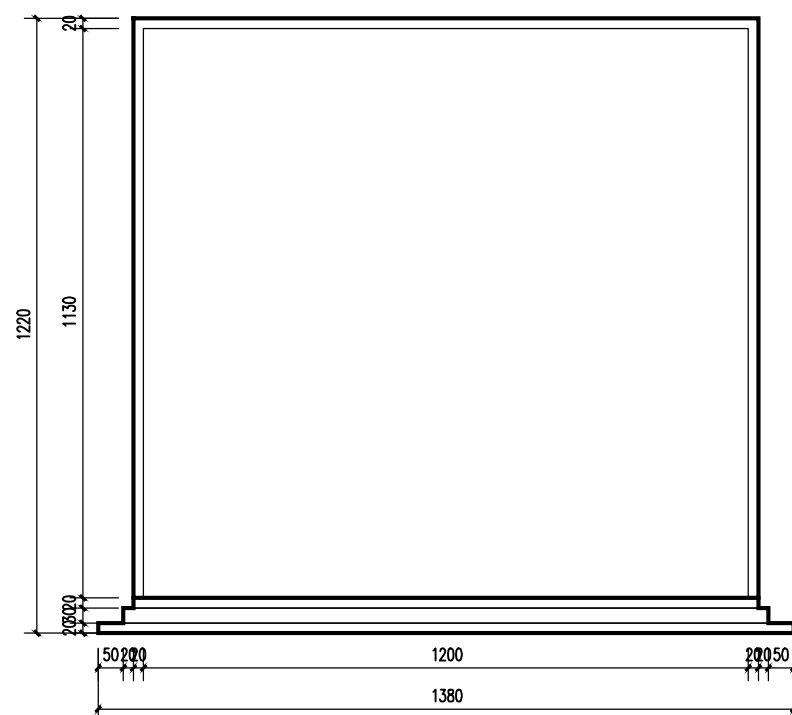


隔断 前视图 1:15

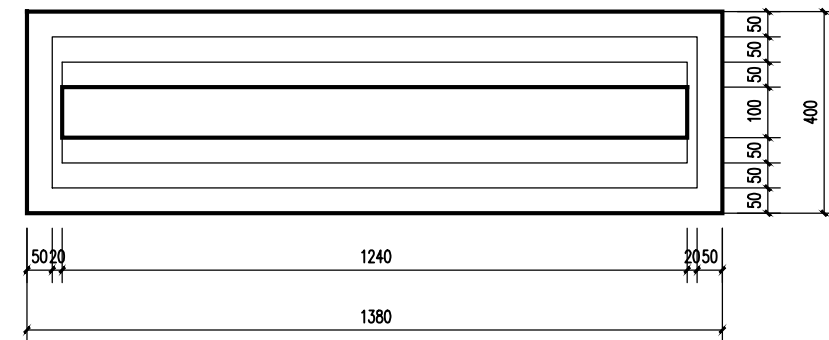

隔断 顶视图 1:15

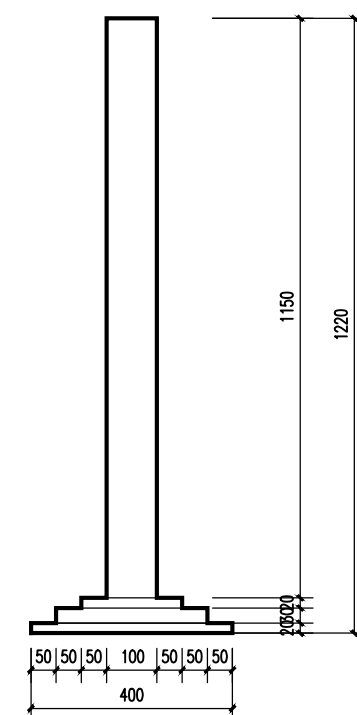


隔断 侧视图 1:15

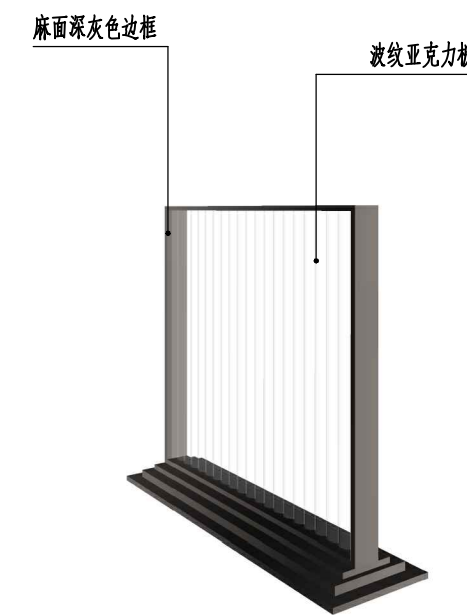

隔断透视图

③ 隔断大样图 1:15

出图记录						ISSUE NOTES	
版 本 REV.		日 期 DATE		备 注 REMARK			
A		2022.02					
注册执业栏 REGISTERED ARCHITECT/ENGINEER							
姓 名							NAME
注册证书号码							REGISTRATION CERTIFICATE NO.
注册印章号码							STAMP NO.
设计号：CD-20212856-F001							JOB NO.
工程名称							PROJECT TITLE
成都大运会主新闻中心装饰搭建							
子项名称							SUB ITEM
建设单位							CLIENT
成都博雅文瑞文化传播有限公司							
图 名							DRAWING TITLE
花箱及隔断大样图							
单 位 mm		UNIT		图 别 室施		DWG. CATEGORY	
比 例 1 : 15		SCALE		图 号 D05		DWG. NO.	
日 期 2022.02		DATE		版 本 A		VER. NO.	
制 图 DRAWN BY		雷鑫鹏					
设 计 DESIGNED BY		张峻					
校 对 CHECKED BY		李瀛文					
专业负责人 DISCIPLINE CHIEF		肖子顺					
设计总负责人 PROJECT CHIEF		张峻					
审 核 AUDIT		张峻					
审 定 APPROVED BY		华轲					
园 基准方中 成都基准方中建筑设计股份有限公司 Chengdu JZfz Architectural Design Co., Ltd. 中国·成都市·琉璃路9号华润广场A座7-15楼 电话：+86(28) 86333800 传真：+86(28) 86582990 7-15F, Tower A, Criland Plaza, No.8,LiuLu Road , Chengdu, P.R.C tel. +86(28) 86333800 fax. +86(28) 86582990 工程设计资质证书编号： A151016191 电子文档编号： -							
版 权 说 明 COPYRIGHT DECLARATION 此图版权为成都基准方中建筑设计股份有限公司所有，未经许可不得使用。							

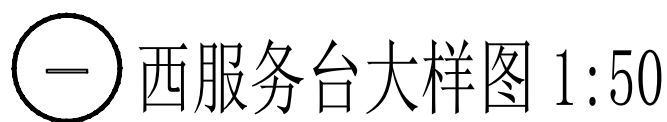

出图记录			ISSUE NOTES		
版 本 REV.	日 期 DATE	备 注 REMARK			
A	2022.02				
注册执业栏			REGISTERED ARCHITECT/ENGINEER		
姓 名			NAME		
注册证书号码			REGISTRATION CERTIFICATE NO.		
注册印章号码			STAMP NO.		
设计号: CD-20212856-F001			JOB NO.		
工程名称			PROJECT TITLE		
成都大运会主新闻中心装饰搭建					
子项名称			SUB ITEM		
建设单位			CLIENT		
成都博雅文瑞文化传播有限公司					
图 名			DRAWING TITLE		
西服务台大样图					
单 位	mm	UNIT	图 号	室施	DWG. CATEGORY
比 例	1:50	SCALE	图 号	D06	DWG. NO.
日 期	2022.02	DATE	版 本	A	VER. NO.
制 图	雷鑫鹏				
DESIGNED BY					
设 计	肖子颖				
DESIGNED BY					
校 对	李霜文				
CHECKED BY					
专业负责人	肖子颖				
DISCIPLINE CHIEF					
设计总负责人	张竣				
PROJECT CHIEF					
审 核	张竣				
AUDIT					
审 定	华轲				
APPROVED BY					
图 基准方中 成都基准方中建筑设计股份有限公司 Chengdu JZFF Architectural Design Co., Ltd. 中国·成都市·琉璃路9号华润广场A座7-15楼 电话: +86(28) 86333800 传真: +86(28) 86582990 7-15F, Tower A, Orland Plaza, No.9, Liuli Road, Chengdu, P.R.C tel. +86(28) 86333800 fax. +86(28) 86582990					
工程设计资质证书编号: A151016191					
电子文档编号: -					
版 权 说 明					
COPYRIGHT DECLARATION					
此图版权为成都基准方中建筑设计股份有限公司所有, 未经许可不得使用。					

白色pvc板A，共23个

宽1600，高1050，12厚，间隔200

白色pvc板,贴画面,共18个
宽1120,高900,8厚,间隔280

无色半透明亚克力板，共23个
宽3400，高500，8厚，间隔200

白色pvc板C，共17个
宽2440，高270，12厚，间隔250



南服务台效果图

木色免漆板

大运会KV喷绘布


白色漆面

深灰色亚克力灯箱
长2900，高690，宽1290


蓉宝立体吉祥物

白色书架，亚克力背板，共21列，3排
高2300，左右间隔210，上下间隔590


蓝色亚克力灯箱
，高600，宽1080

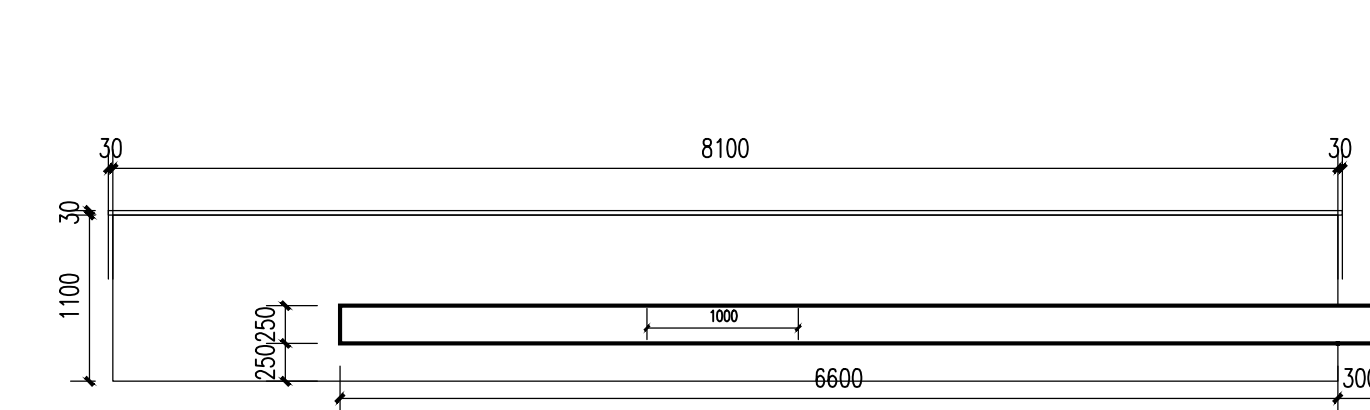


南欢迎台 前视图 1:50

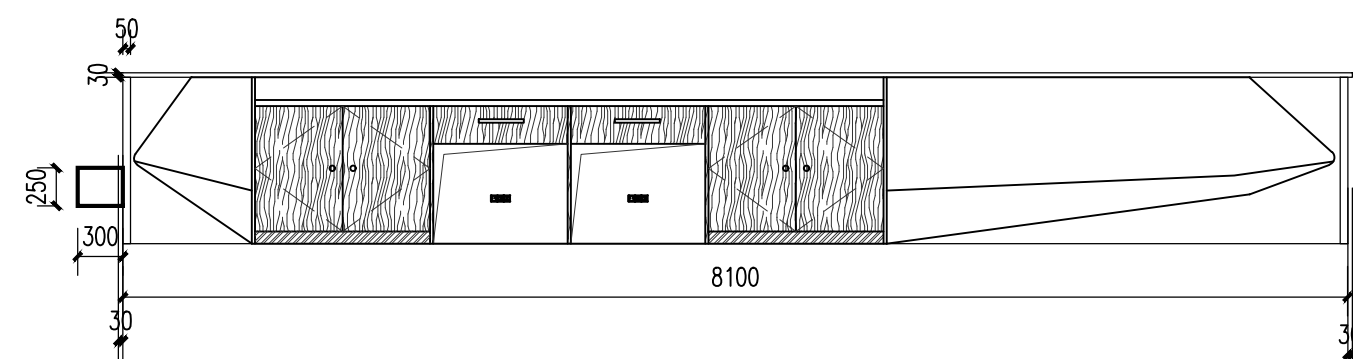

南欢迎台 后视图 1:50

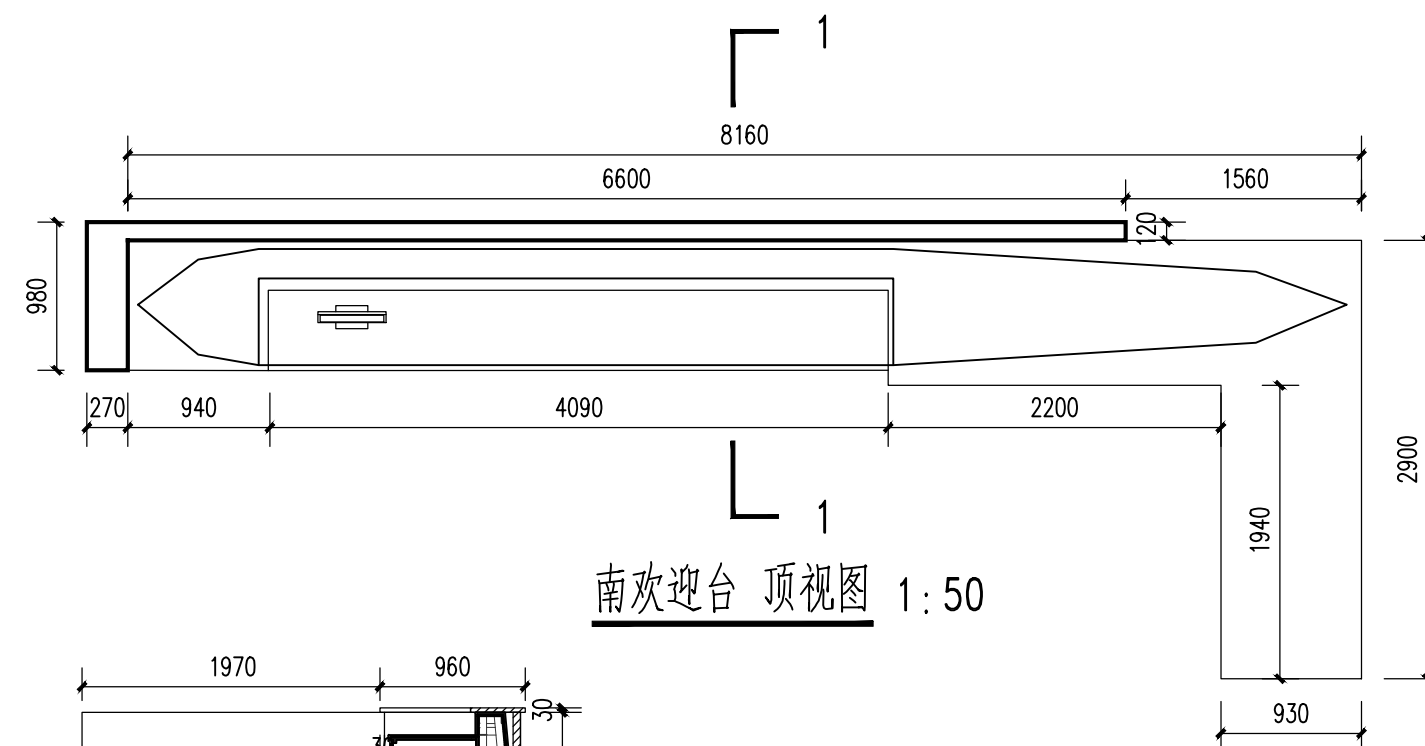


南欢迎台 顶视图 1:50

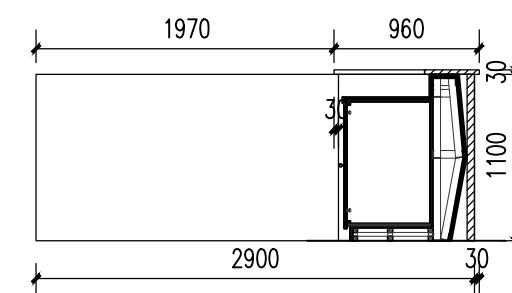


南欢迎台 1-1 剖视图 1:50

① 南服务台大样图 1:50


[illegible]

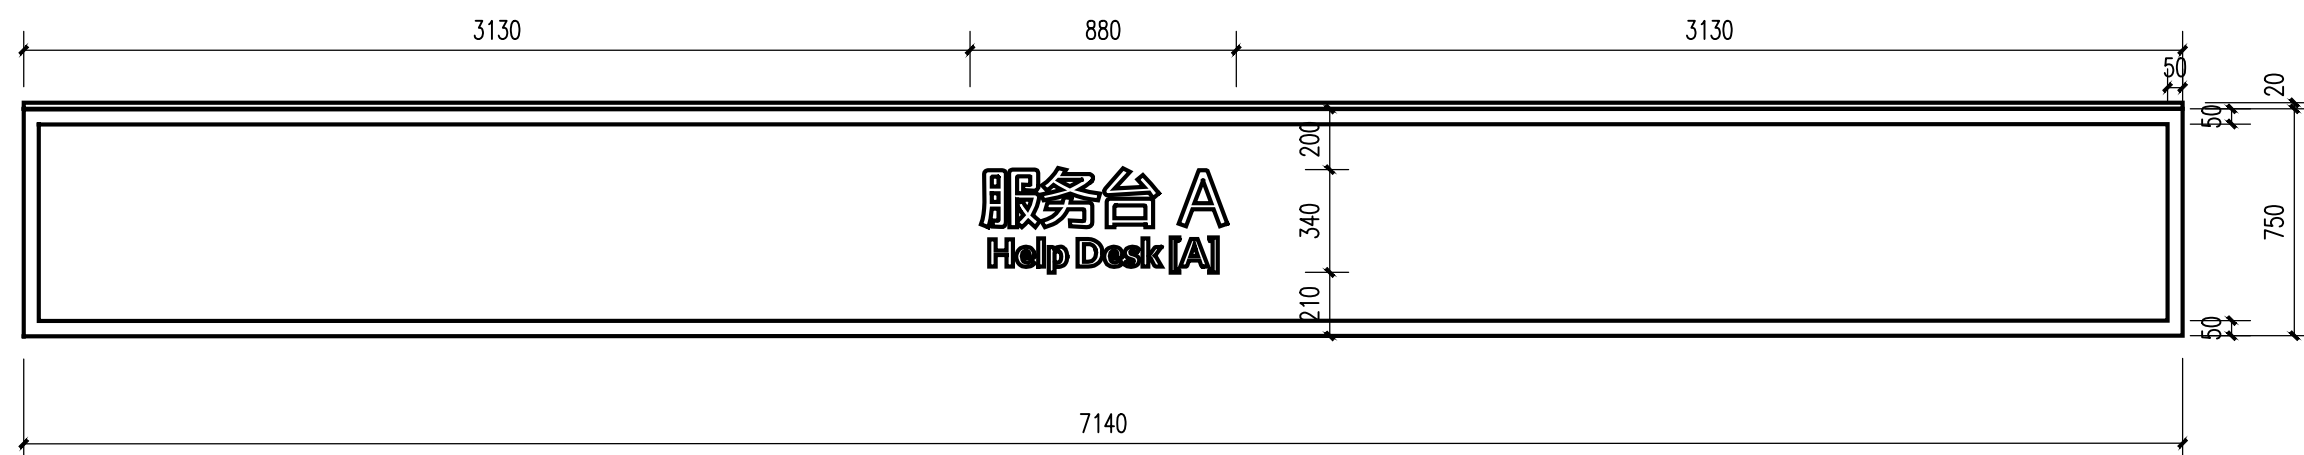


服务台A 前视图 1:25

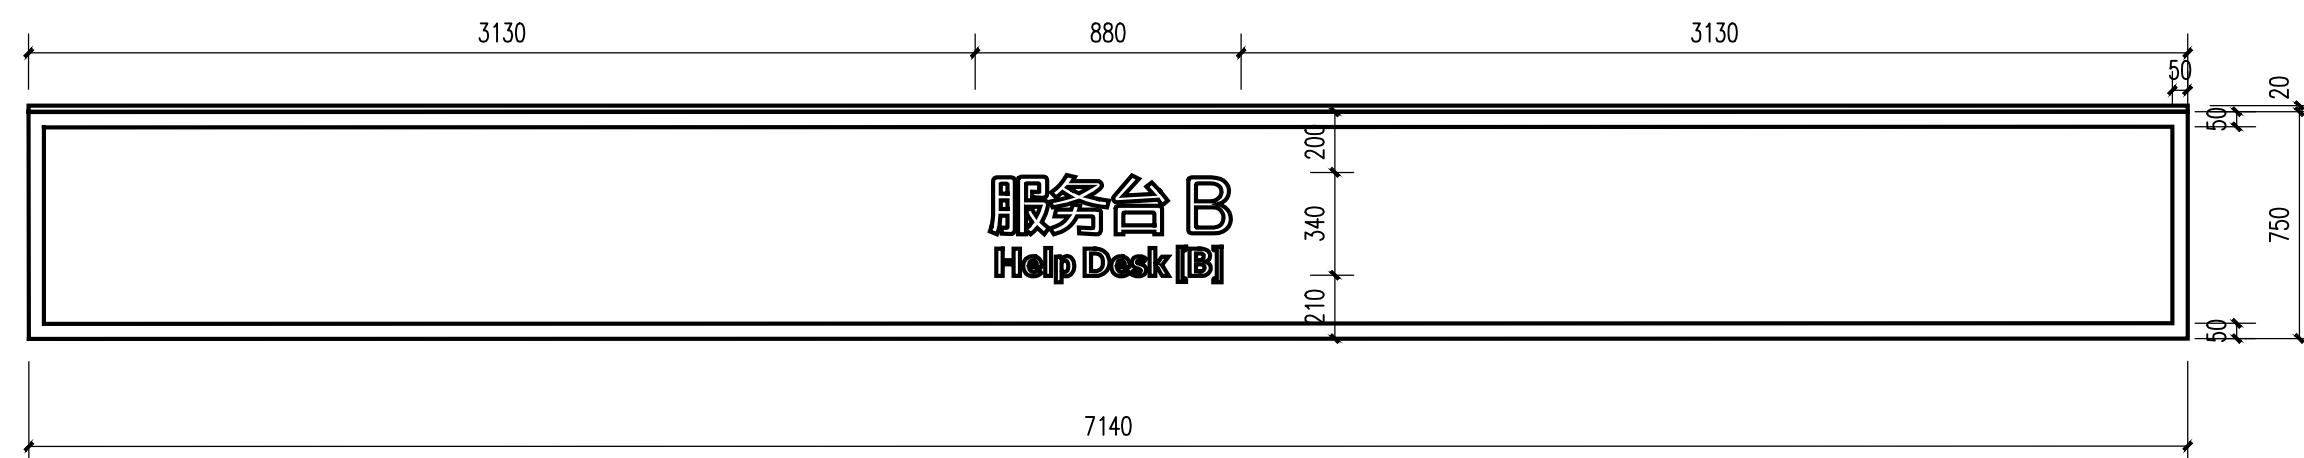


服务台B 前视图 1:25

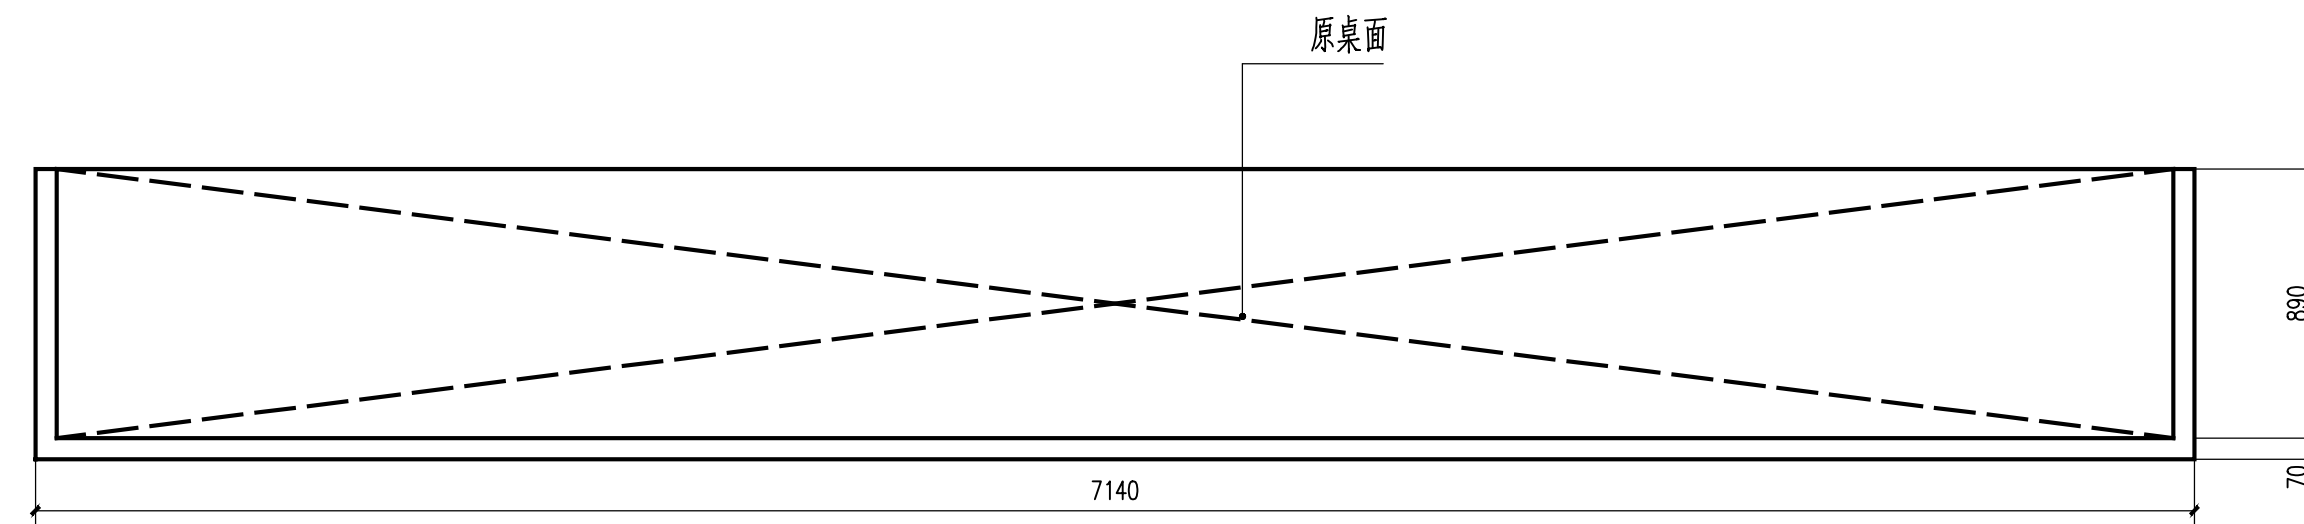


服务台AB 顶视图 1:25

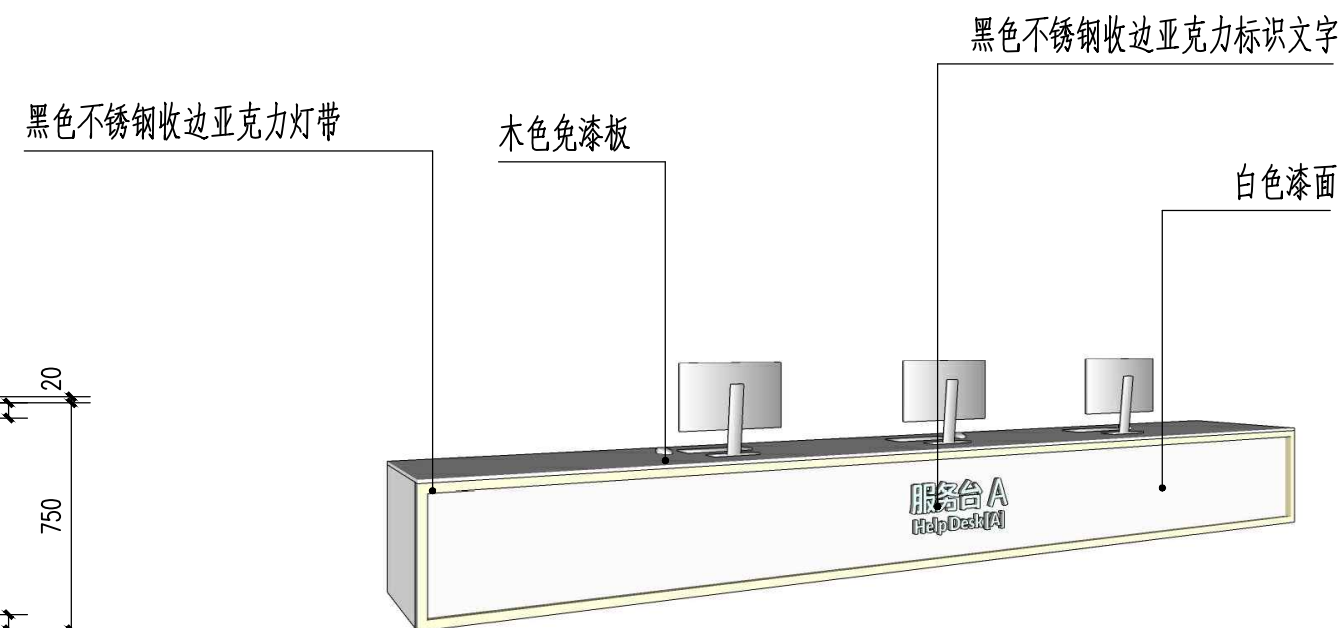

服务台A 效果图

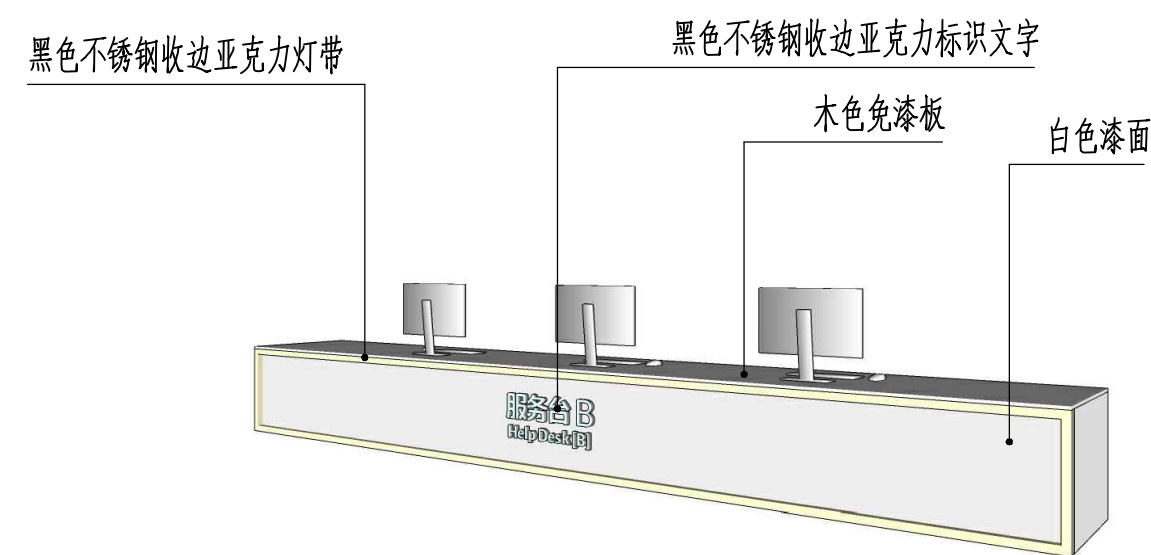









服务台B 效果图

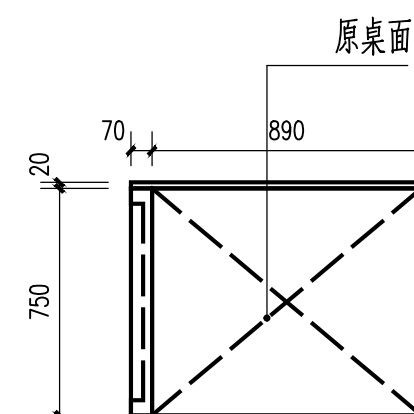


服务台AB 侧视图 1:25



出图记录			ISSUE NOTES		
版 本 REV.	日 期 DATE	备 注 REMARK			
A	2022.02				
注册执业栏					
REGISTERED ARCHITECT/ENGINEER					
姓 名					NAME
注册证书号码					REGISTRATION CERTIFICATE NO.
注册印章号码					STAMP NO.
设计号: CD-20212856-F001					JOB NO.
工程名称					PROJECT TITLE
成都大运会主新闻中心装饰搭建					
子项名称					SUB ITEM
建设单位					CLIENT
成都博雅文瑞文化传播有限公司					
图 名					DRAWING TITLE
服务台A、B大样图					
单 位	mm	UNIT	图 别	室 施	DWG. CATEGORY
比 例	1:25	SCALE	图 号	D08	DWG. NO.
日 期	2022.02	DATE	版 本	A	VER. NO.
制 图	雷鑫鹏				
DRAWN BY					
设 计	肖子颖				
DESIGNED BY					
校 对	李瀛文				
CHECKED BY					
专业负责人	肖子颖				
DISCIPLINE CHIEF					
设计总负责人	张峻				
PROJECT CHIEF					
审 核	张峻				
AUDIT					
审 定	华轲				
APPROVED BY					
成都基准方中建筑设计股份有限公司					
Chengdu JZfZ Architectural Design Co., Ltd.					
中国 成都市 琉璃路8号华润广场A座7-15楼					
电话: +86(28) 86333800 传真: +86(28) 86582990					
7-15F, Tower A, Criland Plaza, No.8, Liuli Road, Chengdu, P.R.C					
tel. +86(28) 86333800 fax. +86(28) 86582990					
工程投资资质证书编号: A151016191					
电子文档编号: -					
CAD FILENAME					
版 权 说 明					
COPYRIGHT DECLARATION					
此图版权为成都基准方中建筑设计股份有限公司所有, 未经许可不得使用。					

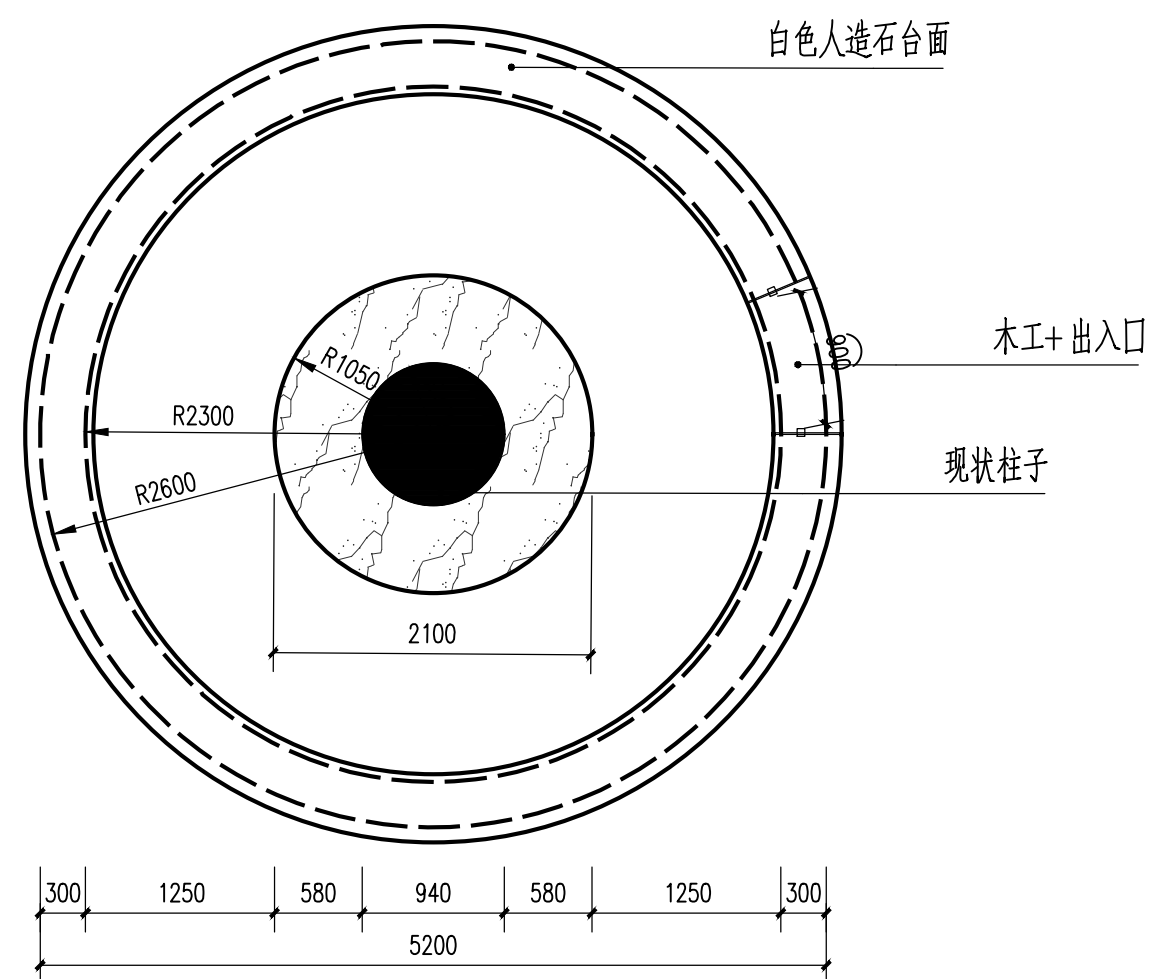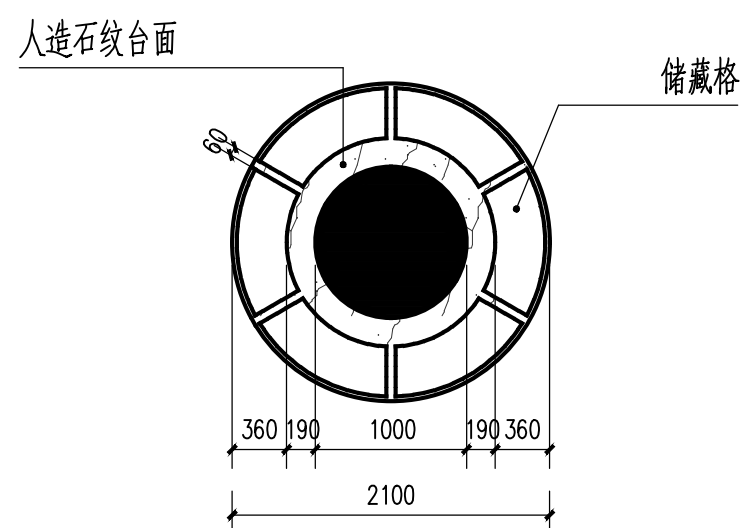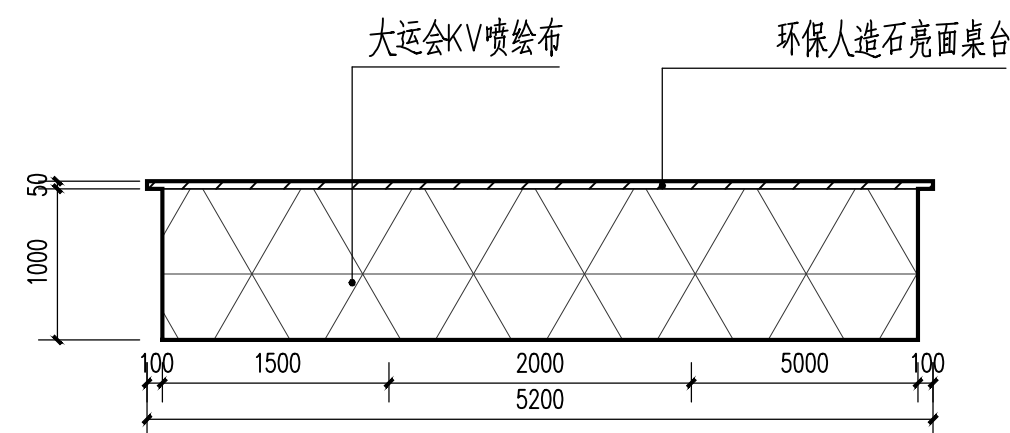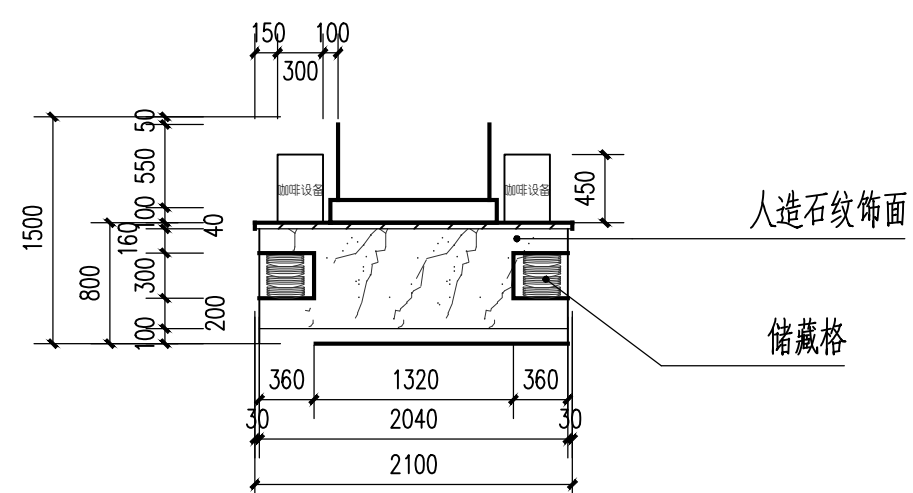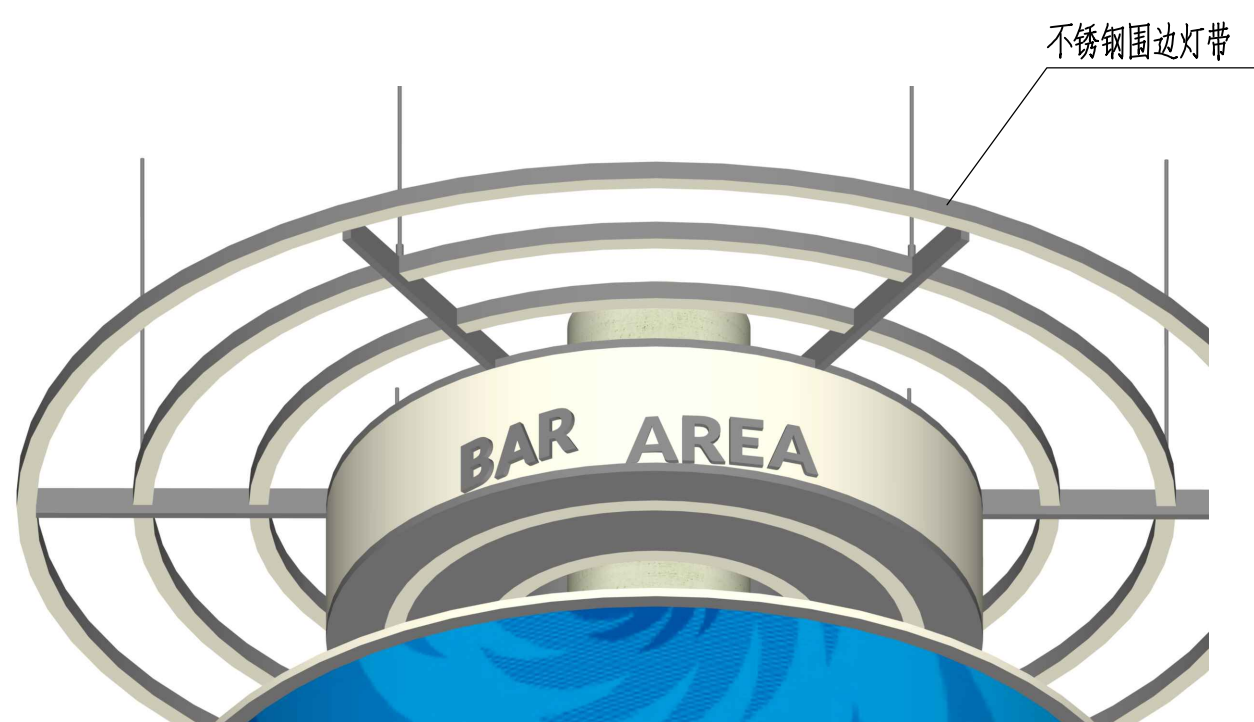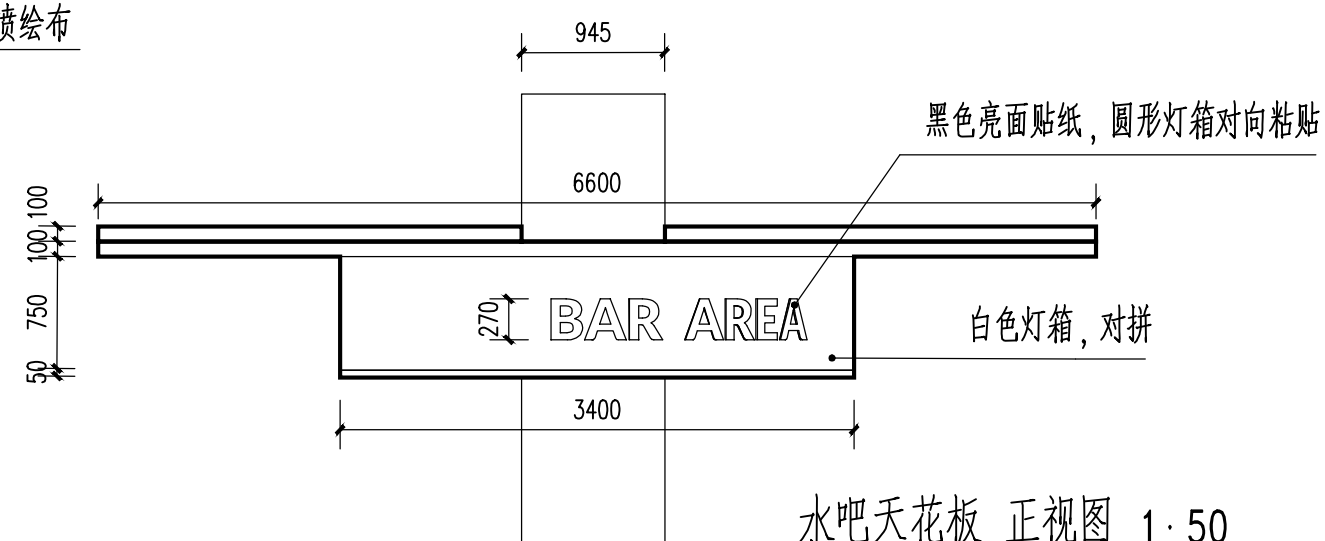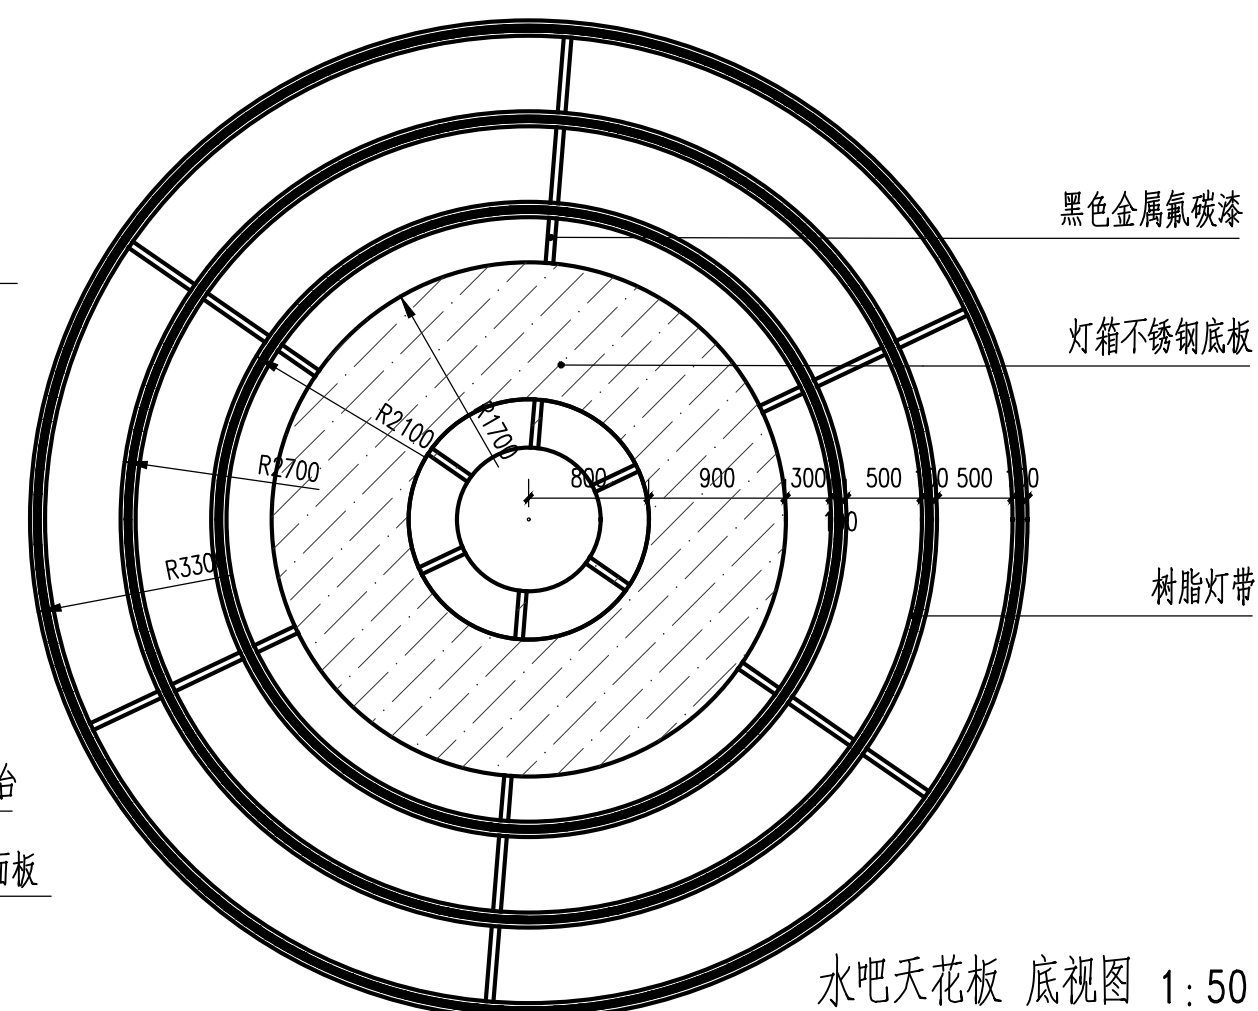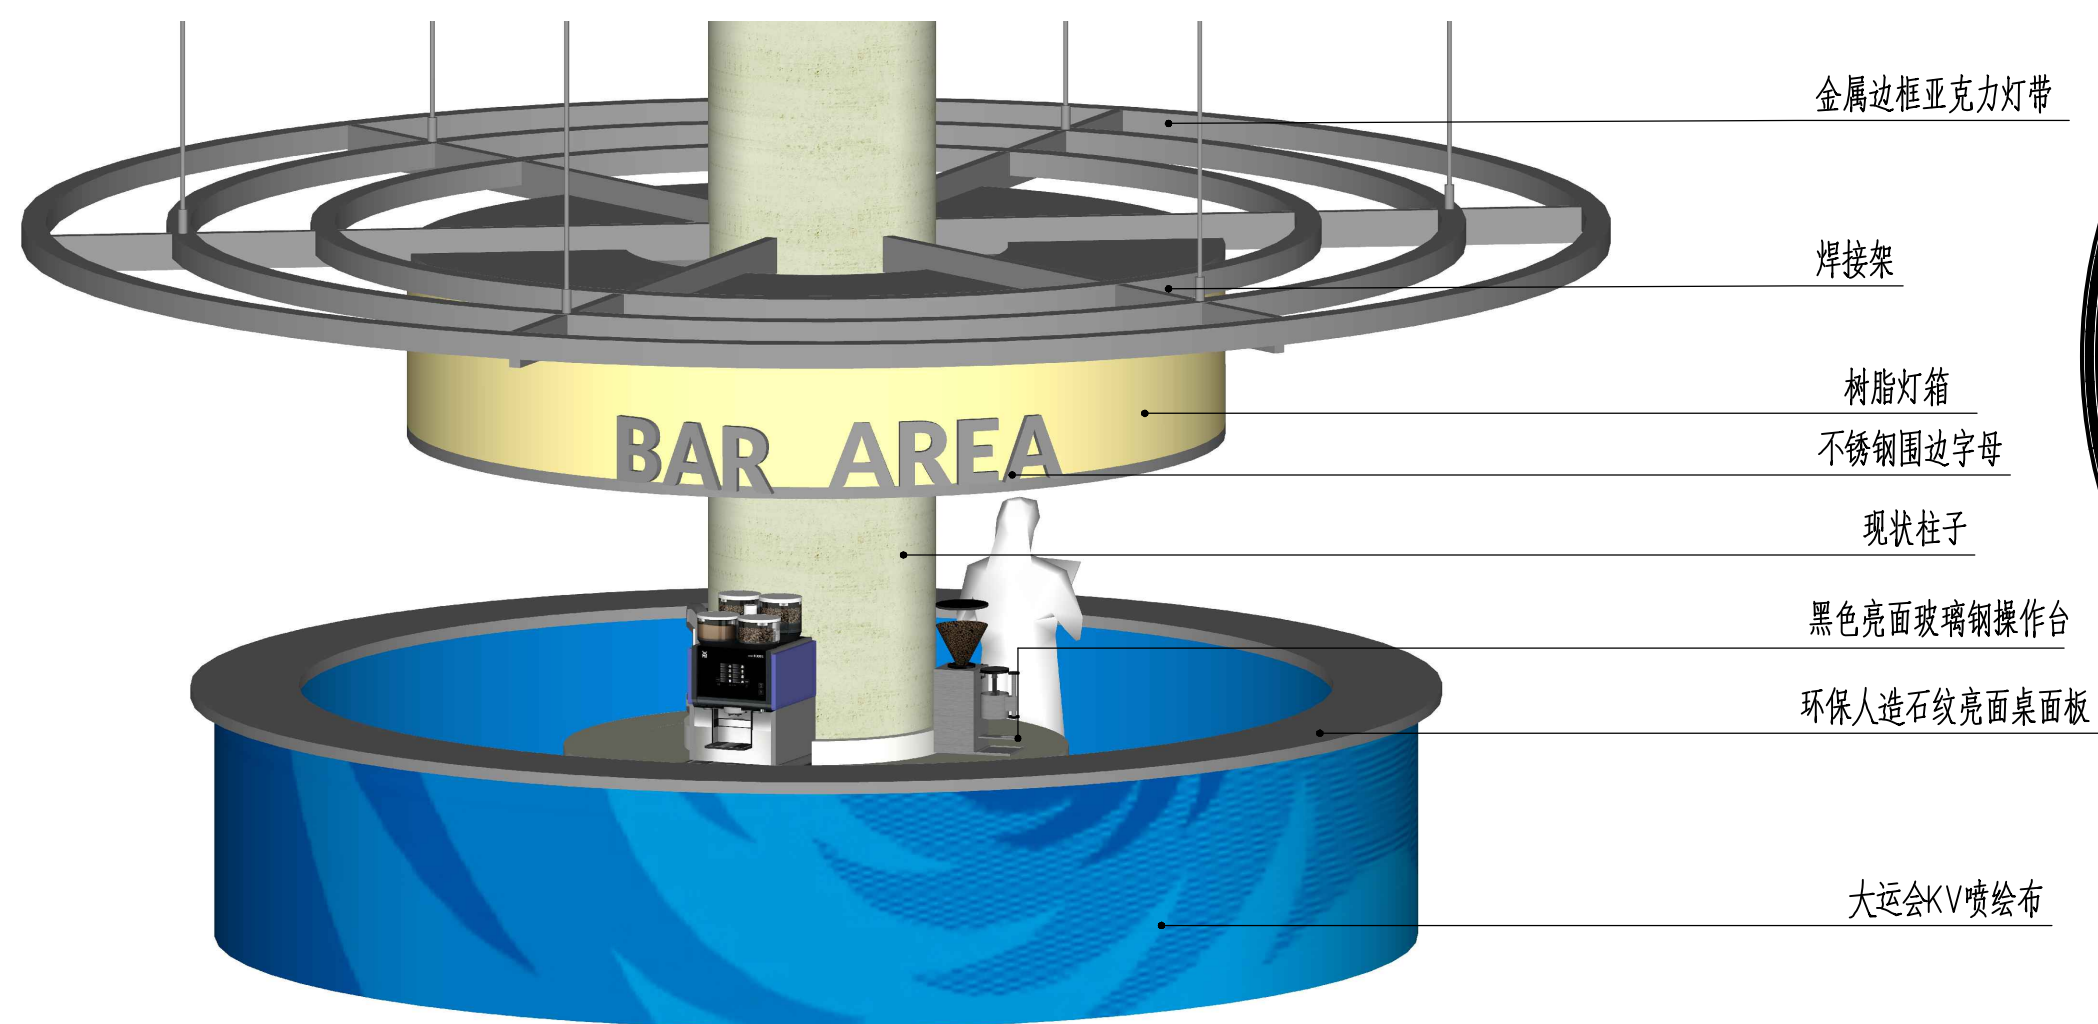


出图记录			ISSUE NOTES		
版 本 REV.	日 期 DATE	备 注 REMARK			
A	2022.02				
注册执业栏					
REGISTERED ARCHITECT/ENGINEER					
姓 名					NAME
注册证书号码					REGISTRATION CERTIFICATE NO.
注册印章号码					STAMP NO.
设计号: CD-20212856-F001					JOB NO.
工程名称					PROJECT TITLE
成都大运会主新闻中心装饰搭建					
子项名称					SUB ITEM
建设单位					CLIENT
成都博雅文瑞文化传播有限公司					
图 名					DRAWING TITLE
水吧大样图					
单 位	mm	UNIT	图 号	室 施	DWG. CATEGORY
比 例	1:50	SCALE	图 号	D09	DWG. NO.
日 期	2022.02	DATE	版 本	A	VER. NO.
制 图	罗 匀				
DESIGNED BY	肖子颖				
校 对	李 瀛 文				
CHECKED BY	肖子颖				
专业负责人					
DISCIPLINE CHIEF					
设计总负责人	张 峻				
PROJECT CHIEF					
审 核	张 峻				
AUDIT					
审 定	华 轲				
APPROVED BY					
成都基准方中建筑设计股份有限公司					
Chengdu JZfZ Architectural Design Co., Ltd.					
中国 成都市 琉璃路8号华润广场A座7-15楼					
电话: +86(28) 86333800 传真: +86(28) 86582990					
7-15F, Tower A, Criland Plaza, No.8, Liuli Road, Chengdu, P.R.C					
tel. +86(28) 86333800 fax. +86(28) 86582990					
工程投资资质证书编号: A151016191					
电子文档编号: -					CAD FILENAME
版 权 说 明					
COPYRIGHT DECLARATION					
此图版权为成都基准方中建筑设计股份有限公司所有, 未经许可不得使用。					

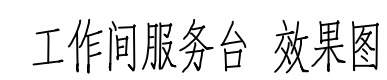

① MPC服务台大样图 1:50


[illegible]

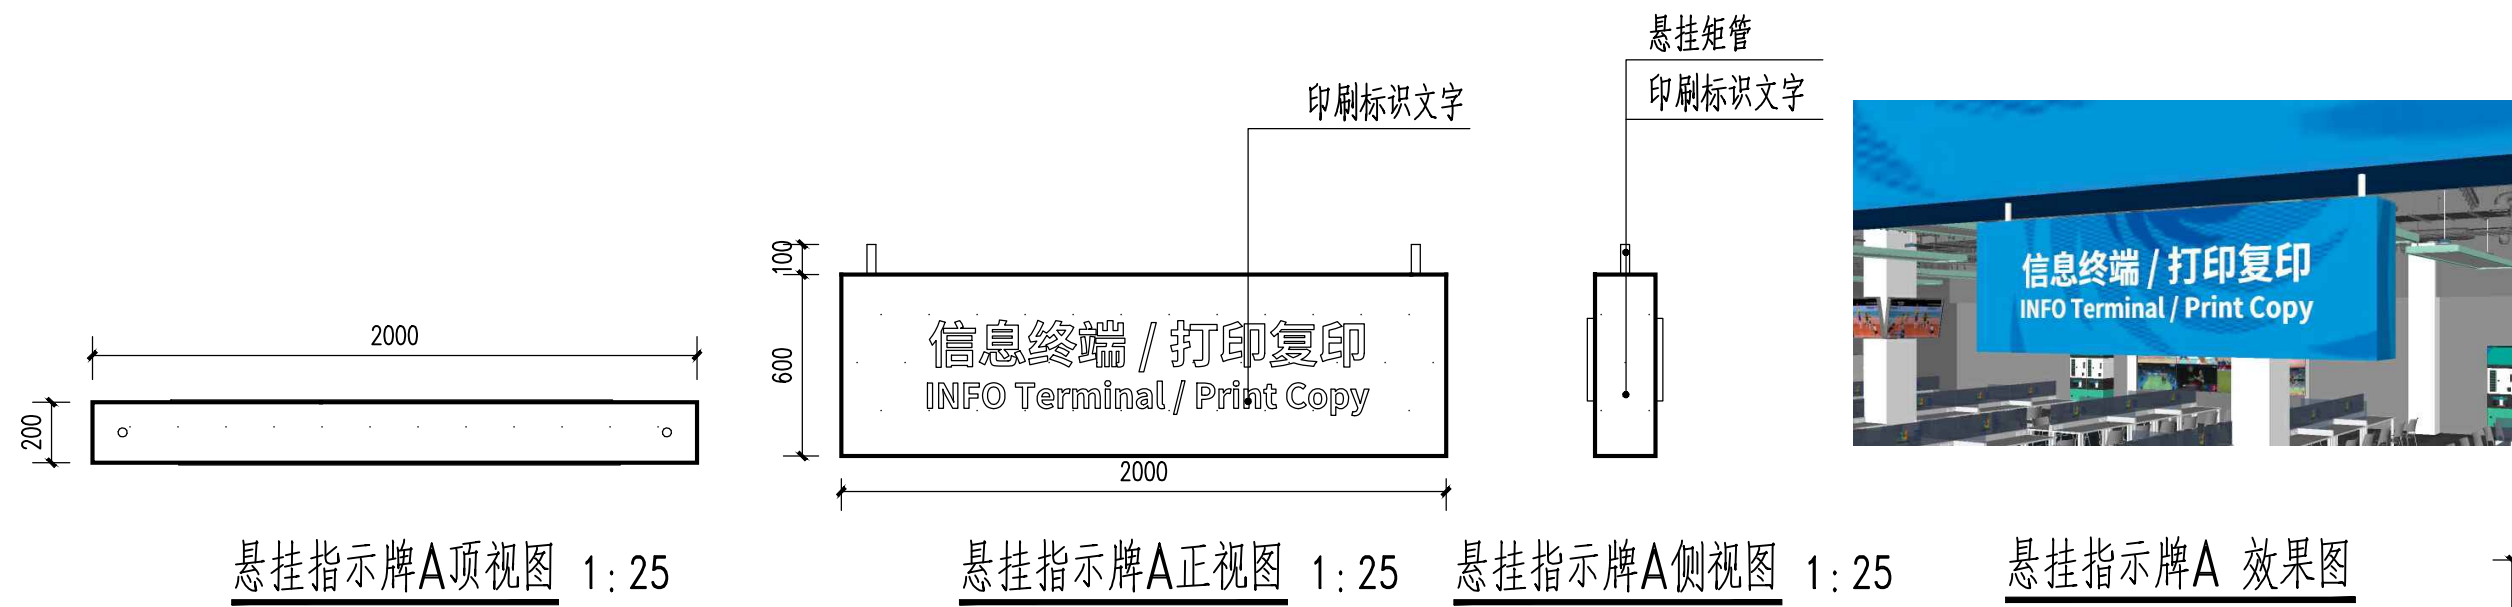

悬挂指示牌A正视图 1:25

悬挂指示牌A 效果图

① 悬挂指示牌A大样图 1:25

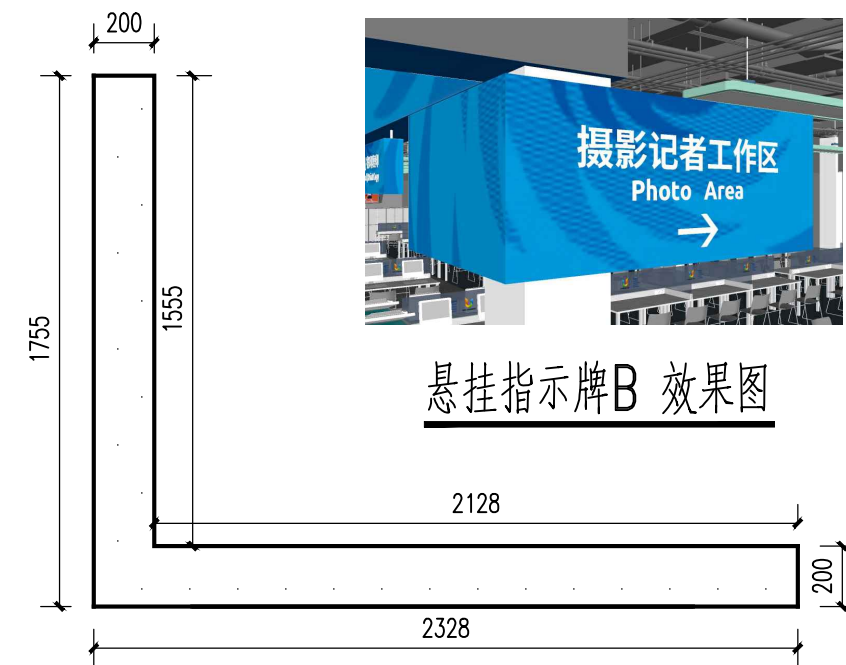


悬挂指示牌B 效果图


悬挂指示牌

悬挂指示牌B侧视图 1:25


② 悬挂指示牌B大样图 1:25

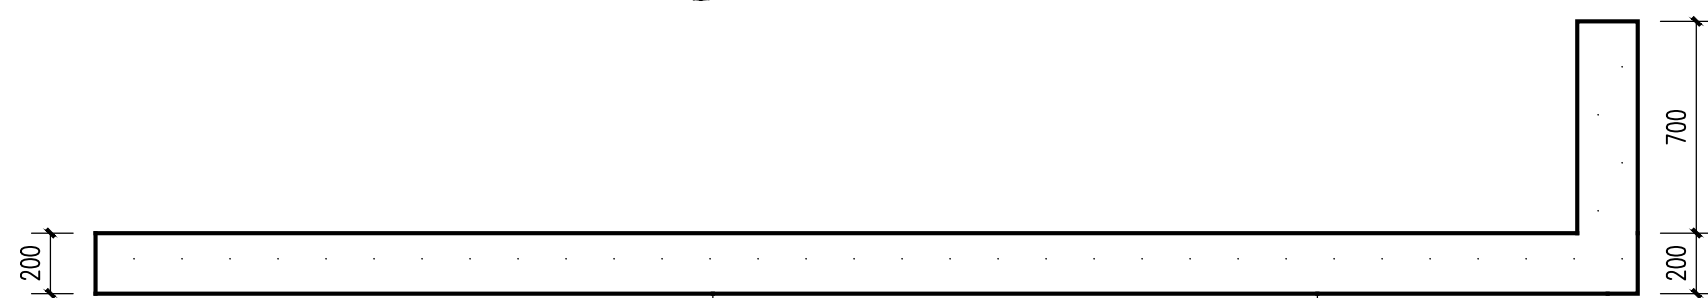

指示牌围挡顶视图 1:25

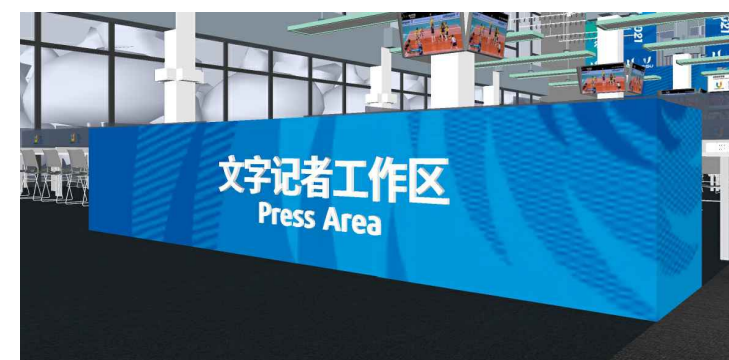

指示牌围挡 效果图

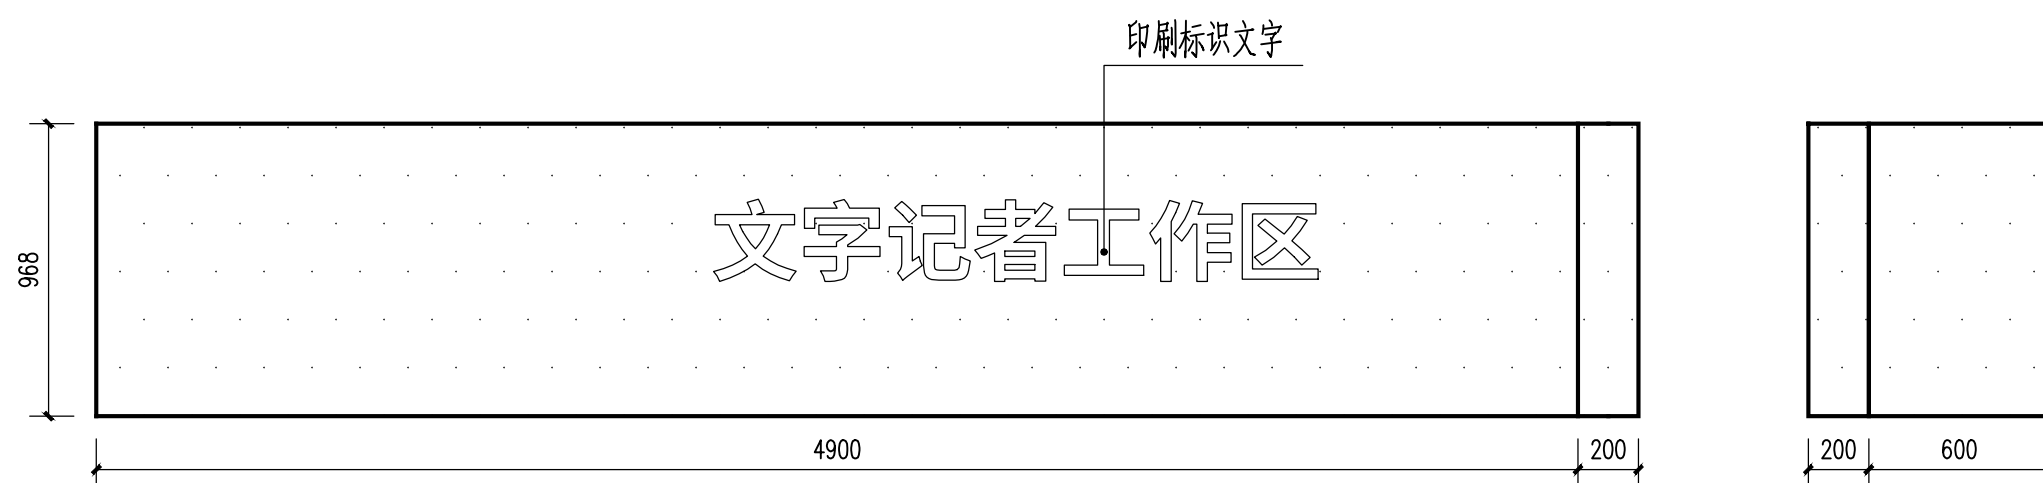

指示牌围挡正视图 1:25


指示牌围挡侧视图 1:25

③ 指示牌围挡大样图 1:25




④ 吊旗大样图 1:25

出图记录		ISSUE NOTES
版本 REV.	日期 DATE	备注 REMARK
A	2022.02	
注册执业栏 REGISTERED ARCHITECT/ENGINEER		
姓 名		NAME
注册证书号码		REGISTRATION CERTIFICATE NO.
注册印章号码		STAMP NO.
设计号: CD-20212856-F001		JOB NO.
工程名称		PROJECT TITLE
成都大运会主新闻中心装饰搭建		
子项名称		SUB ITEM
建设单位		CLIENT
成都博雅文瑞文化传播有限公司		
图 名		DRAWING TITLE
媒体工作间指示及吊旗大样图		
单位 mm	UNIT	图 别 室 施 DWG. CATEGORY
比例 1:25	SCALE	图 号: D11 DWG. NO.
日期 2022.02	DATE	版本 A VER. NO.
制 图 DRAWN BY	张丽	
设 计 DESIGNED BY	肖子颖	
校 对 CHECKED BY	李耀文	
专业负责人 DISCIPLINE CHIEF	肖子颖	
设计总负责人 PROJECT CHIEF	张竣	
审 核 AUDIT	张竣	
审 定 APPROVED BY	华轲	
国 基准方中 成都基准方中建筑设计股份有限公司 Chengdu JZFC Architectural Design Co., Ltd. 中国 成都市 琉璃场8号华润广场A座7-15楼 电话: +86(28) 86333800 传真: +86(28) 86582990 7-15F, Tower A, Criad Plaza, No.8Jiuli Road, Chengdu, P.R.C tel. +86(28) 86333800 fax. +86(28) 86582990 工程设计资质证书编号: A151016191 电子文档编号: - CAD FILENAME 版 权 说 明 COPYRIGHT DECLARATION 此图版权为成都基准方中建筑设计股份有限公司所有, 未经许可不得使用。		

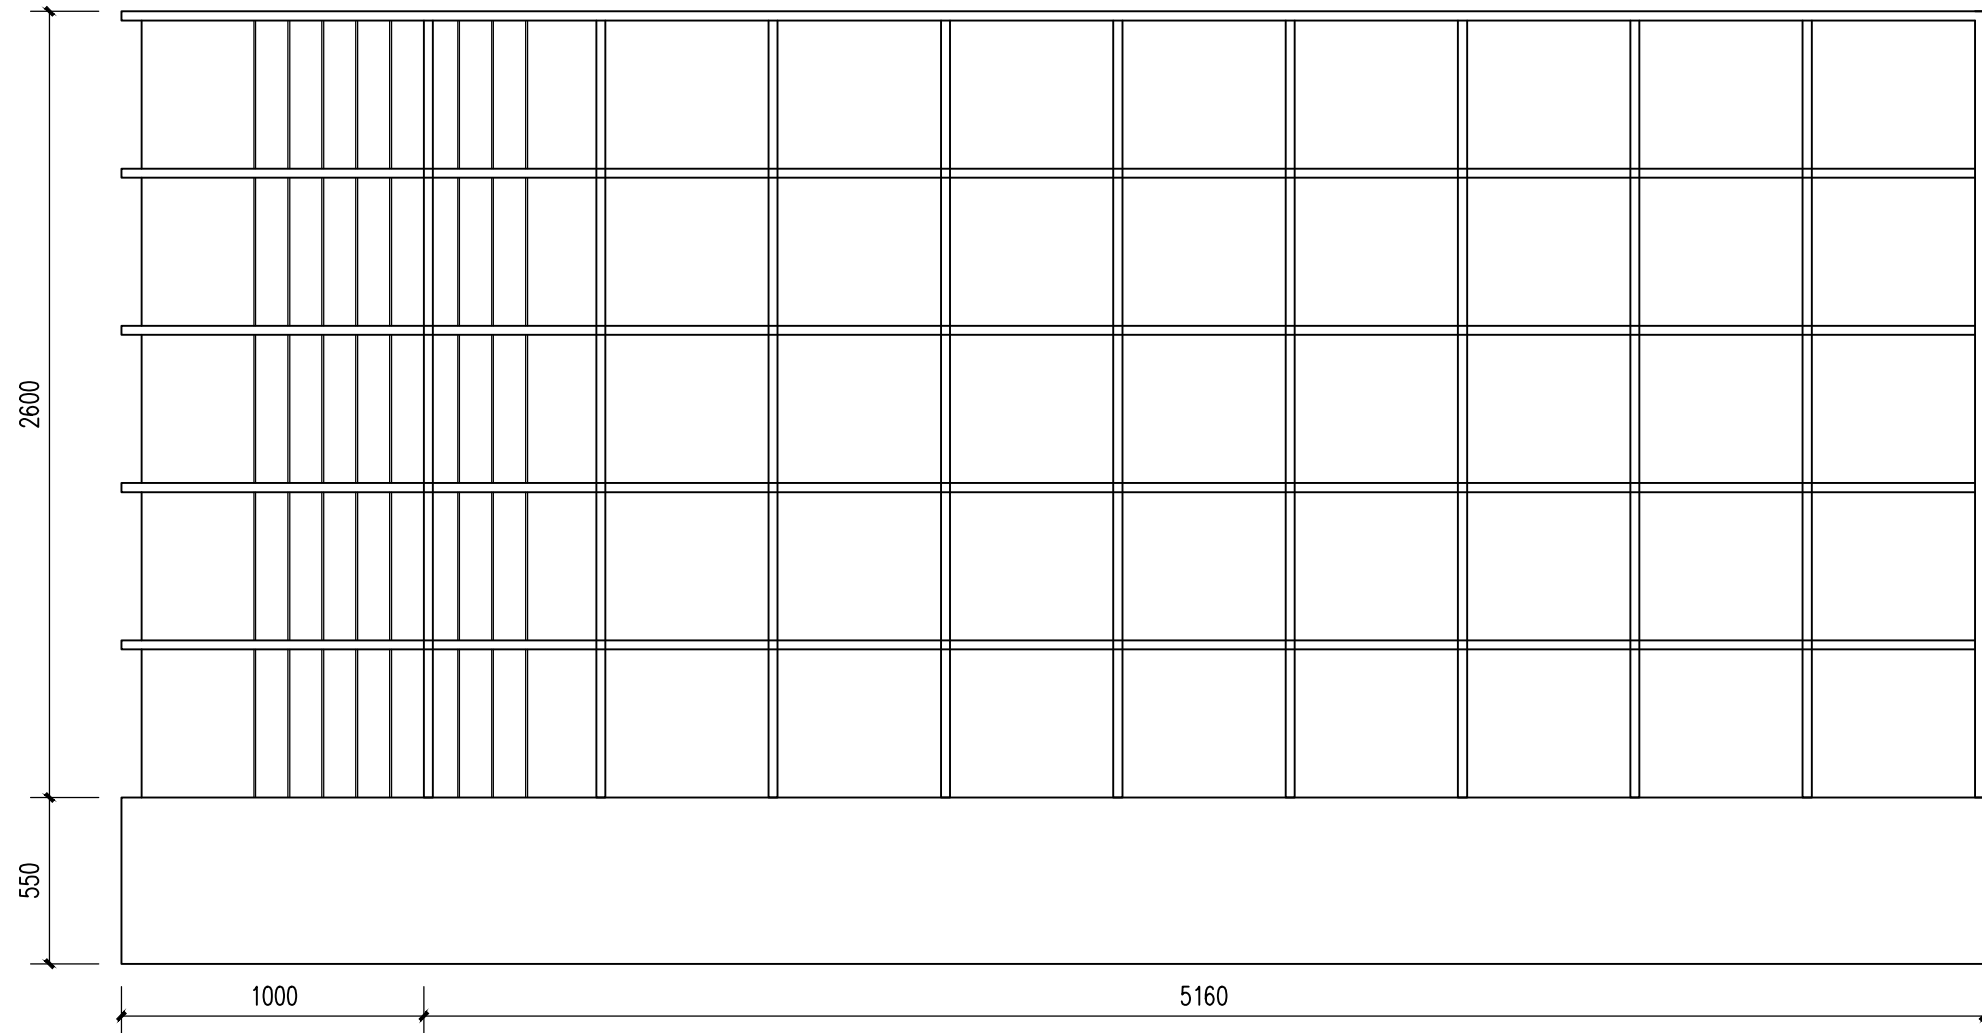


书架 B 立面视图 1:25

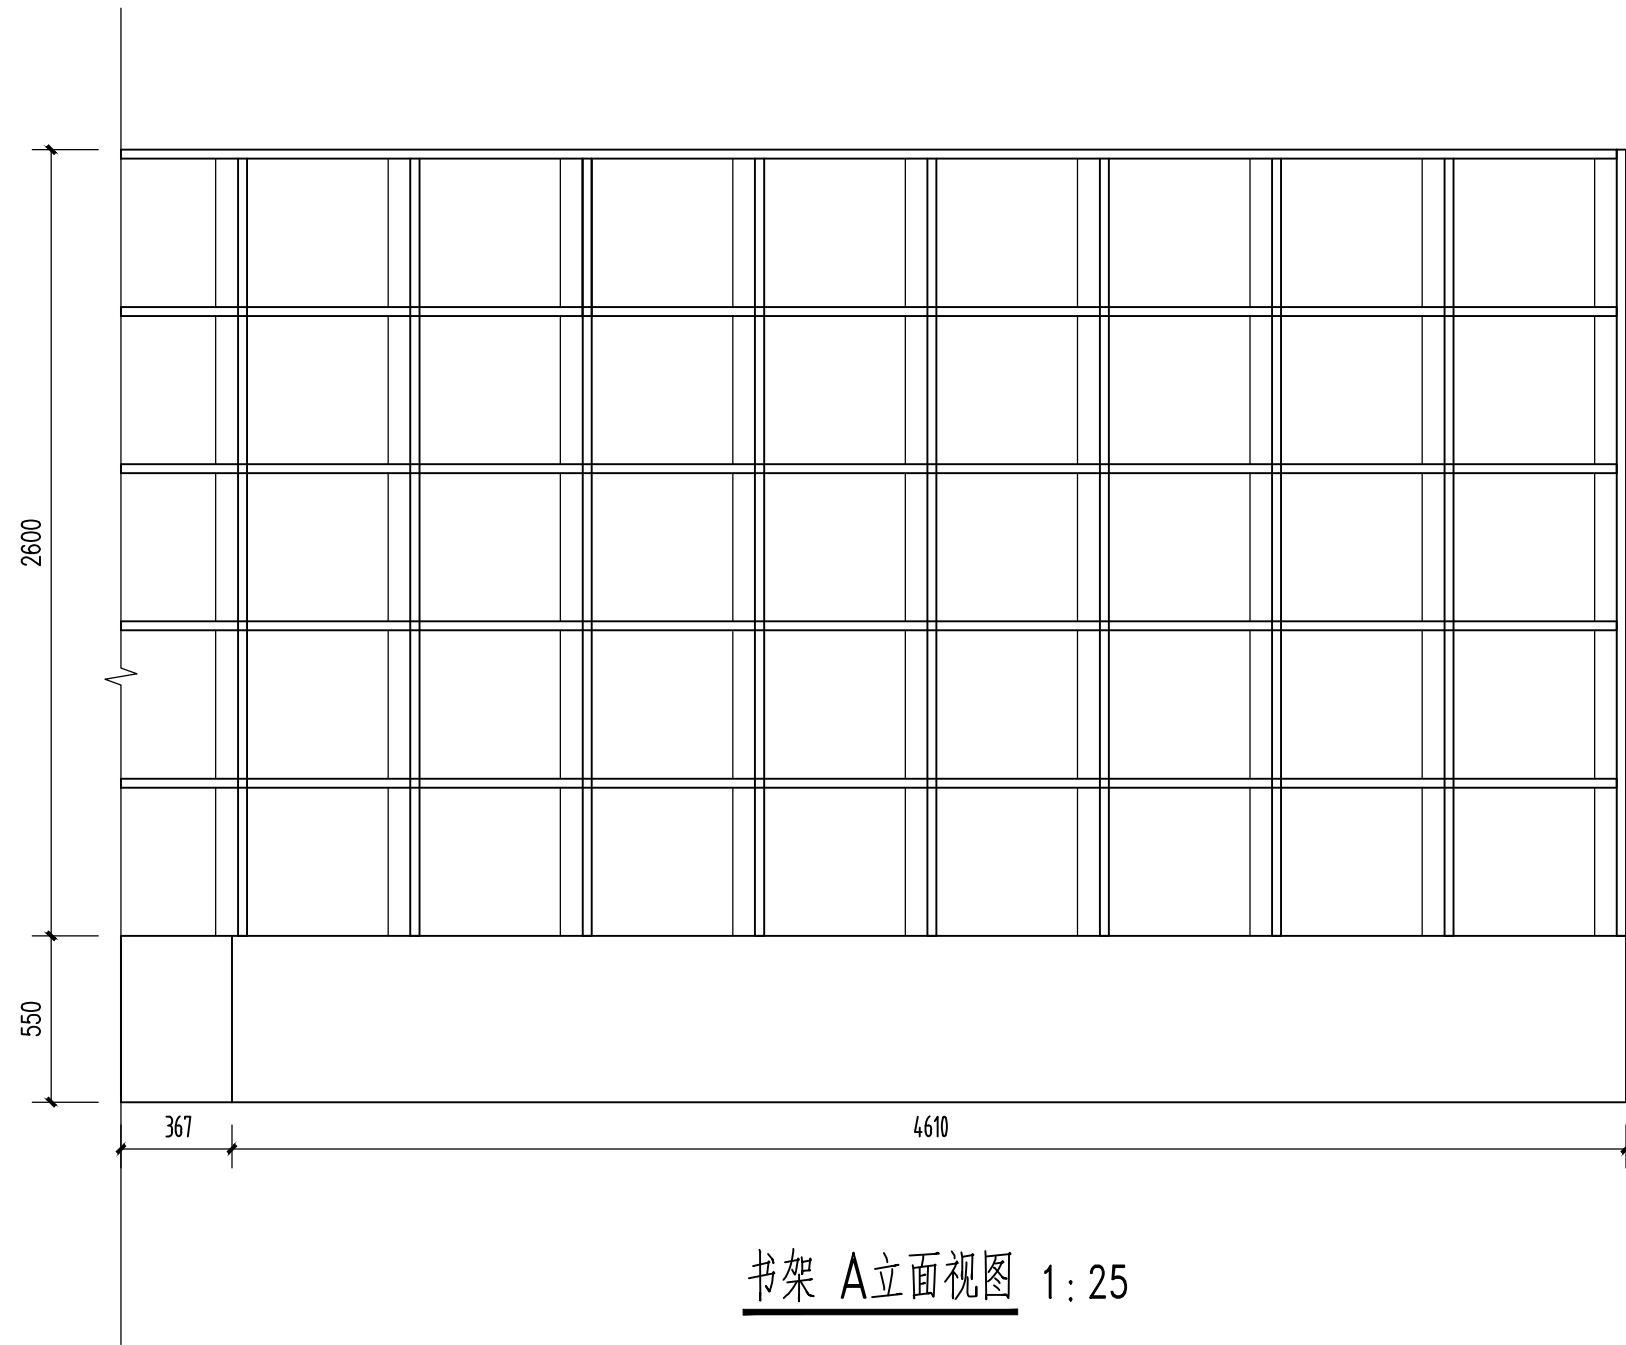


书架 A立面视图 1:25

① 媒体工作间书架大样图 1:25


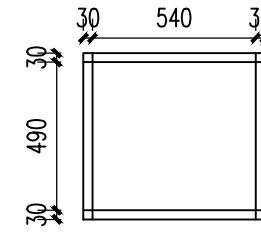


书架标准格子详图 1:25


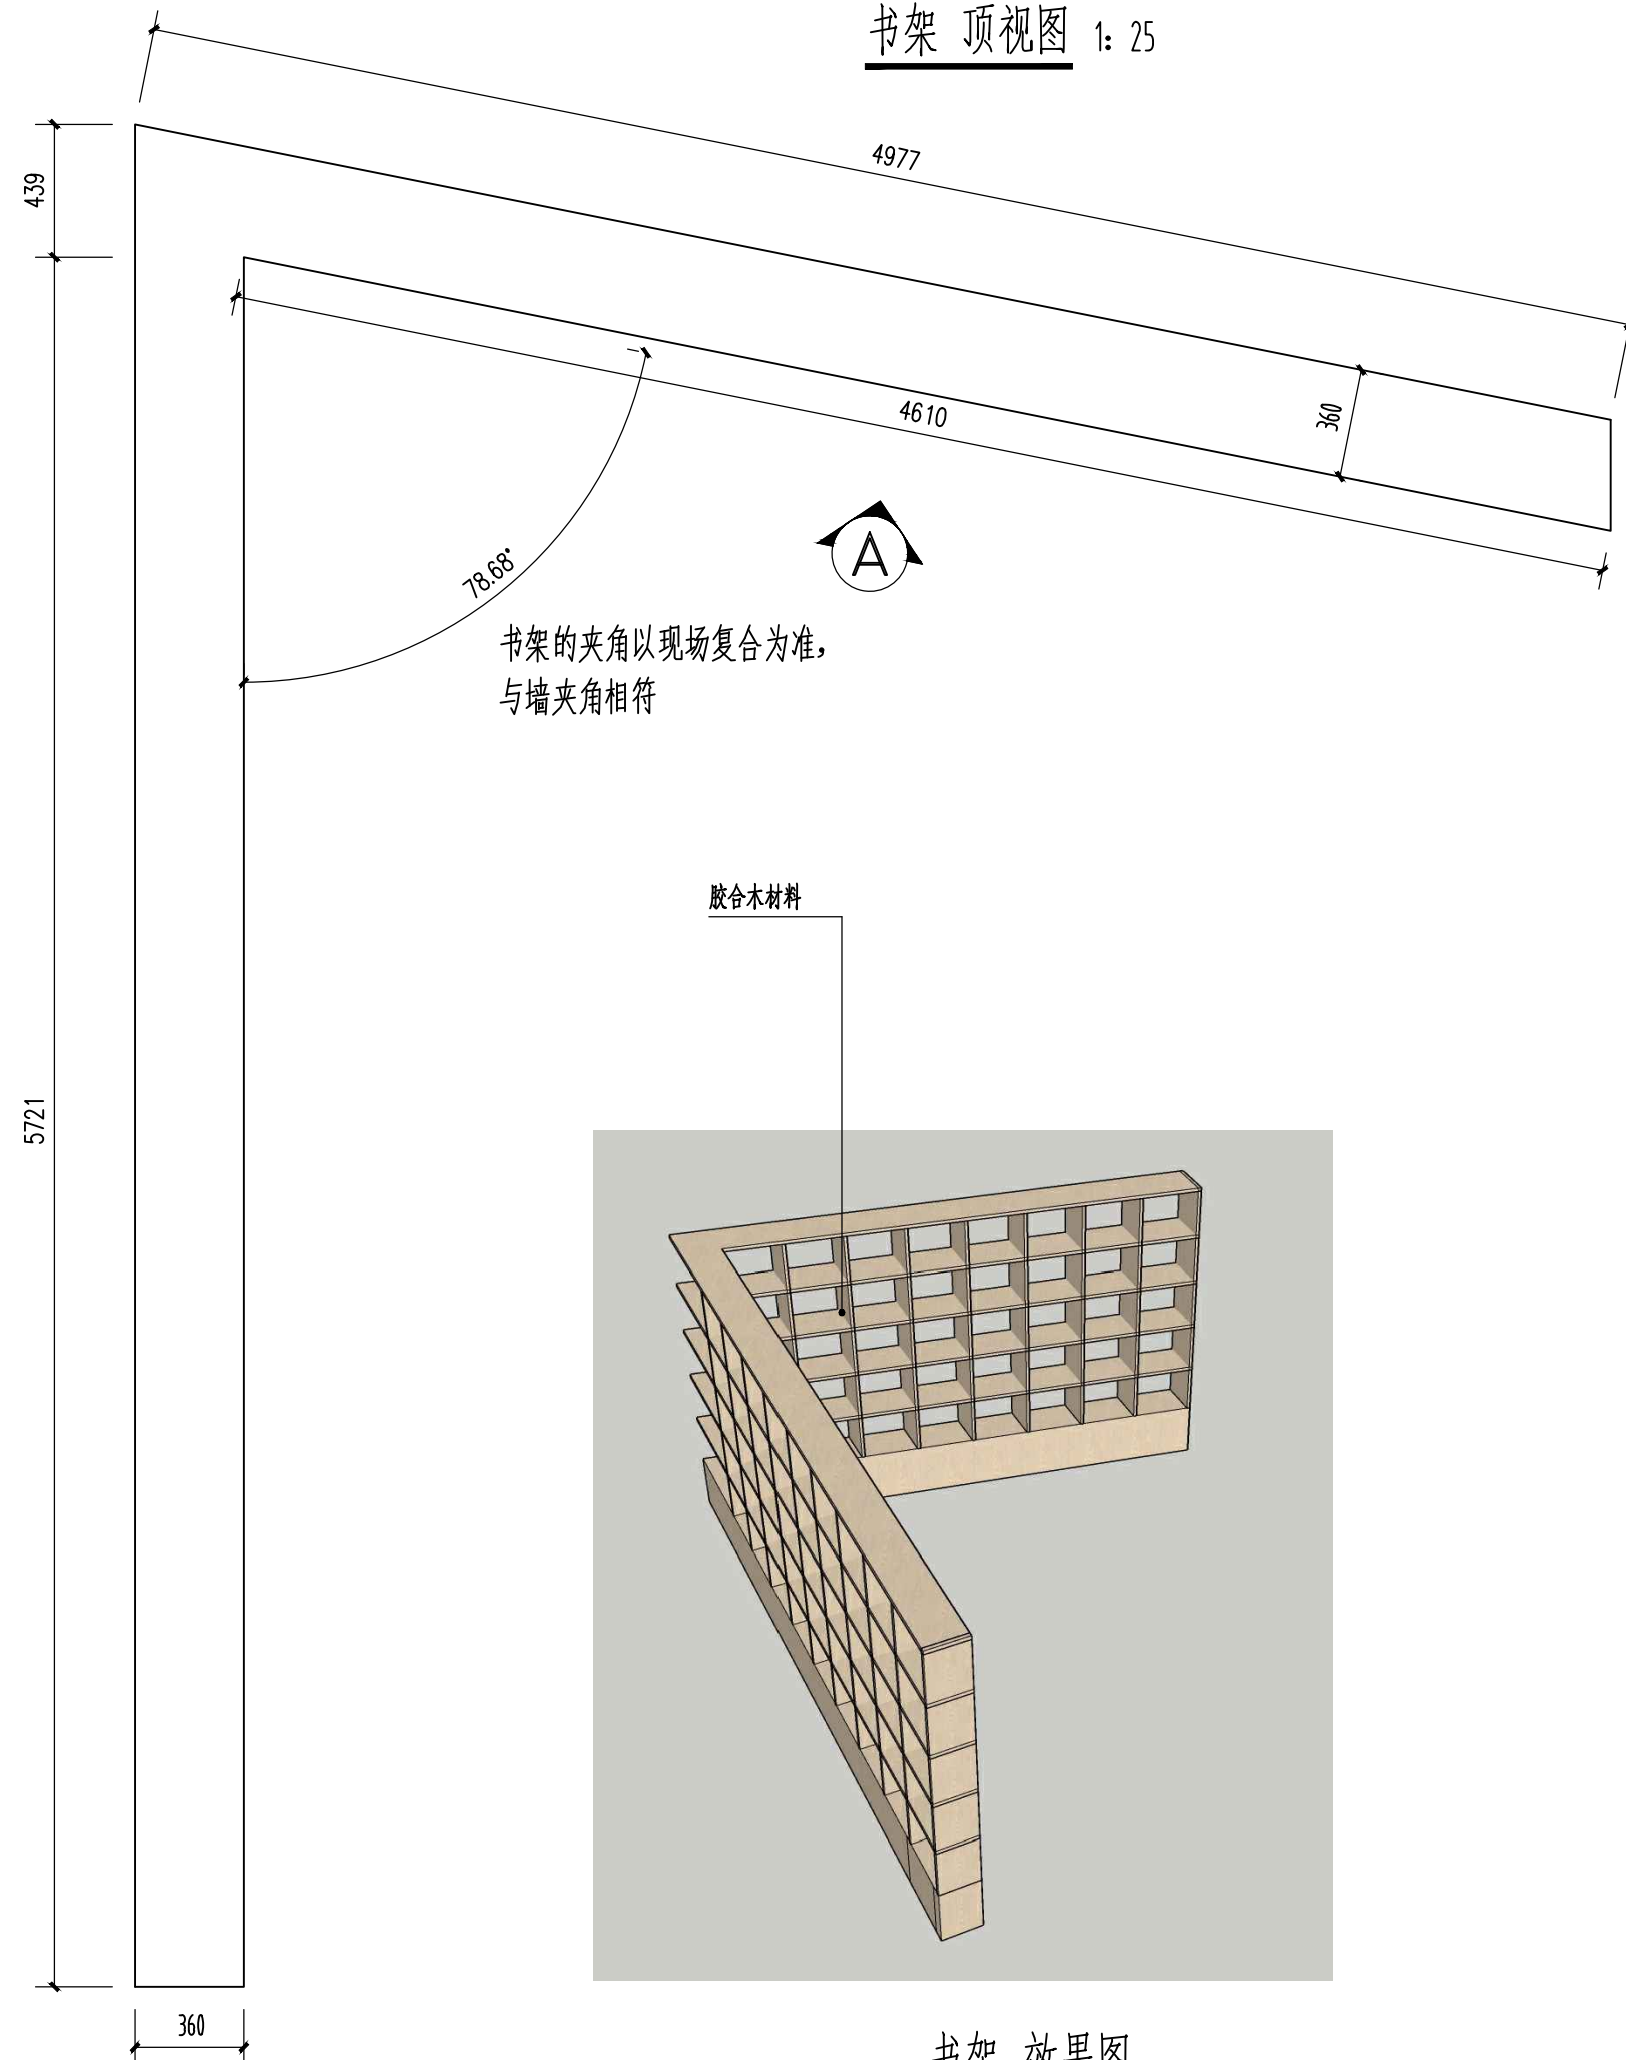


书架效果图


出图记录		ISSUE NOTES	
版 本 REV.	日 期 DATE	备 注 REMARK	
A	2022.02		
注册执业栏		REGISTERED ARCHITECT/ENGINEER	
姓 名		NAME	
注册证书号码		REGISTRATION CERTIFICATE NO.	
注册印章号码		STAMP NO.	
设计号: CD-20212856-F001		JOB NO.	
工程名称		PROJECT TITLE	
成都大运会主新闻中心装饰搭建			
子项名称		SUB ITEM	
建设单位		CLIENT	
成都博雅文瑞文化传播有限公司			
图 名		DRAWING TITLE	
媒体工作间书架大样图			
单 位: mm	UNIT	图 别	DWG. CATEGORY
比 例: 1:25	SCALE	图 号: D12	DWG. NO.
日 期: 2022.02	DATE	版 本: A	VER. NO.
制 图 DRAWN BY	张丽		
设 计 DESIGNED BY	肖子颖		
校 对 CHECKED BY	李翔文		
专业负责人 DISCIPLINE CHIEF	肖子颖		
设计总负责人 PROJECT CHIEF	张峻		
审 核 AUDIT	张峻		
审 定 APPROVED BY	华轲		
图 基 准 方 中 成都基准方中建筑设计股份有限公司 Chengdu JZFC Architectural Design Co., Ltd. 中国 成都市 琉璃路8号华润广场A座7-15楼 电话: +86(28) 86333800 传真: +86(28) 86582990 7-15F, Tower A, Ciland Plaza, No.8,Liuli Road , Chengdu, P.R.C tel. +86(28) 86333800 fax. +86(28) 86582990 工程设计资质证书编号: A151016191 电子文档编号: - CAD FILENAME 版 权 说 明 COPYRIGHT DECLARATION 此图版权为成都基准方中建筑设计股份有限公司所有, 未经许可不得使用。			

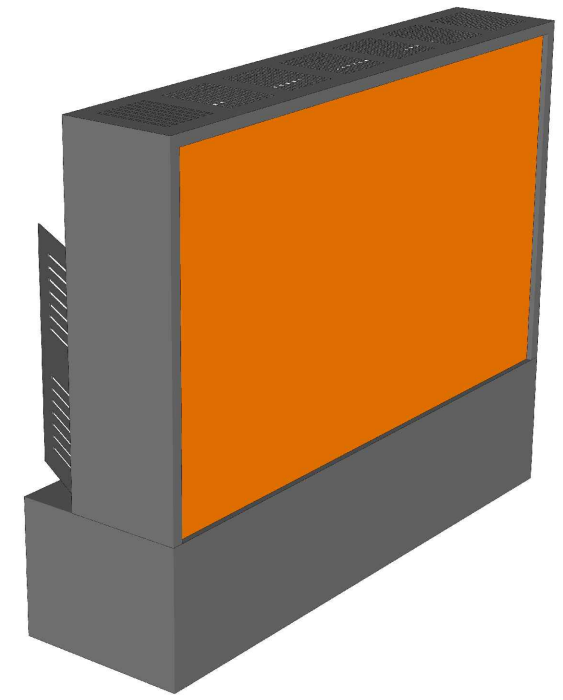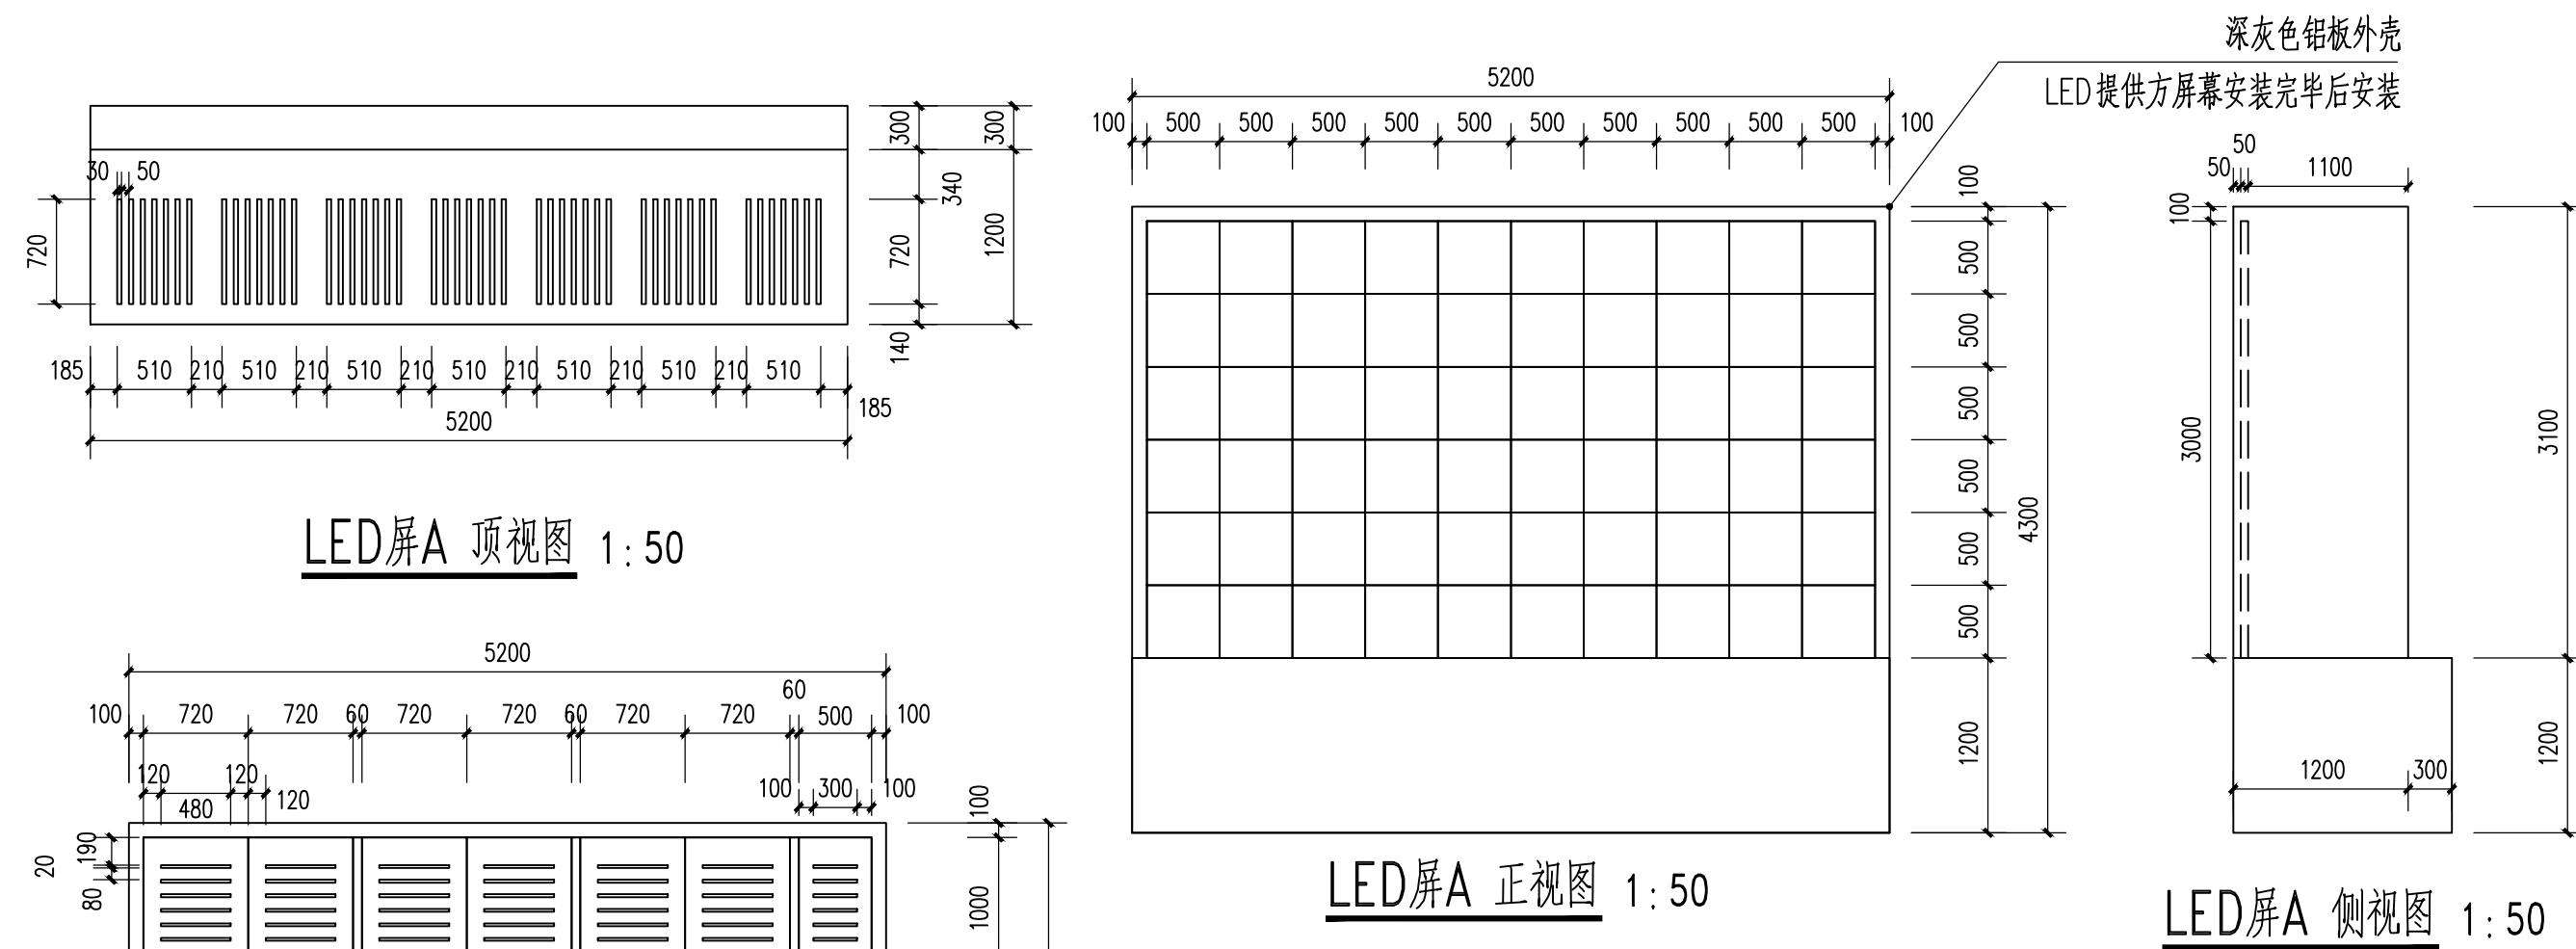



LED屏A 效果图

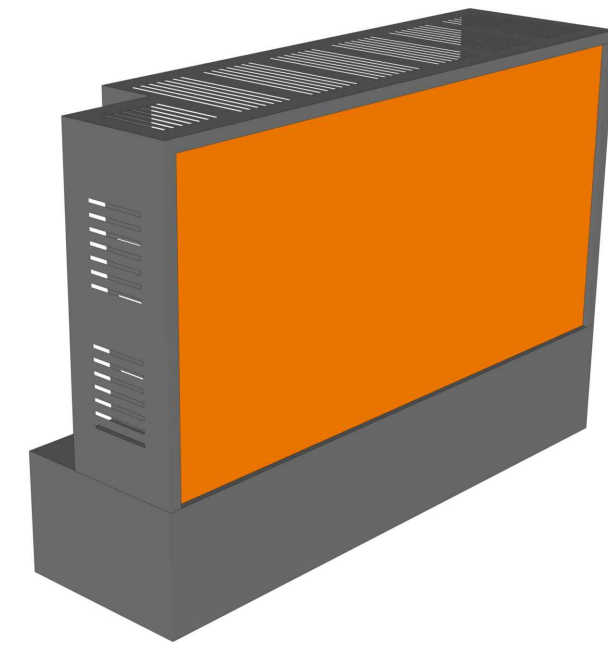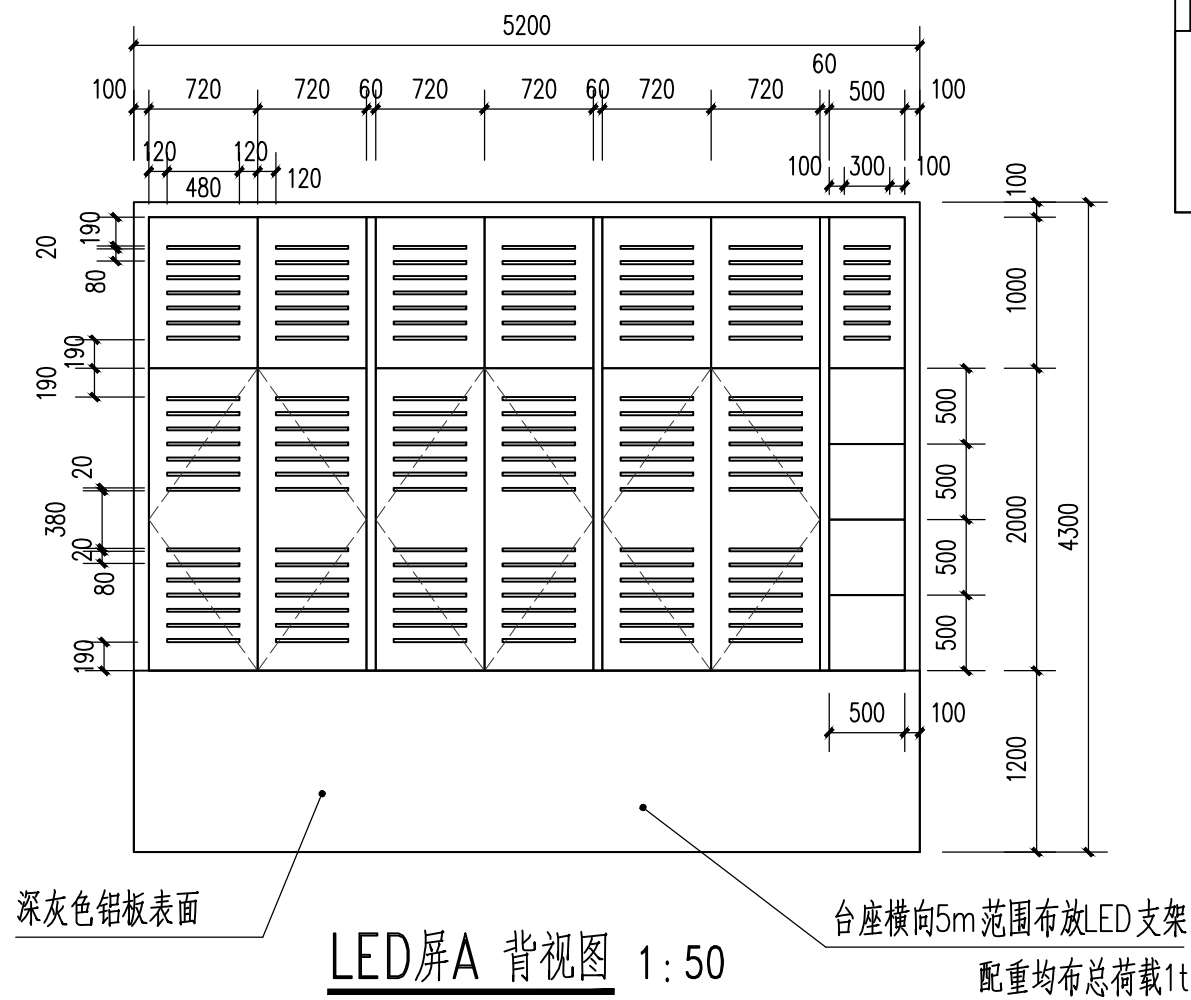


LED屏B 效果图

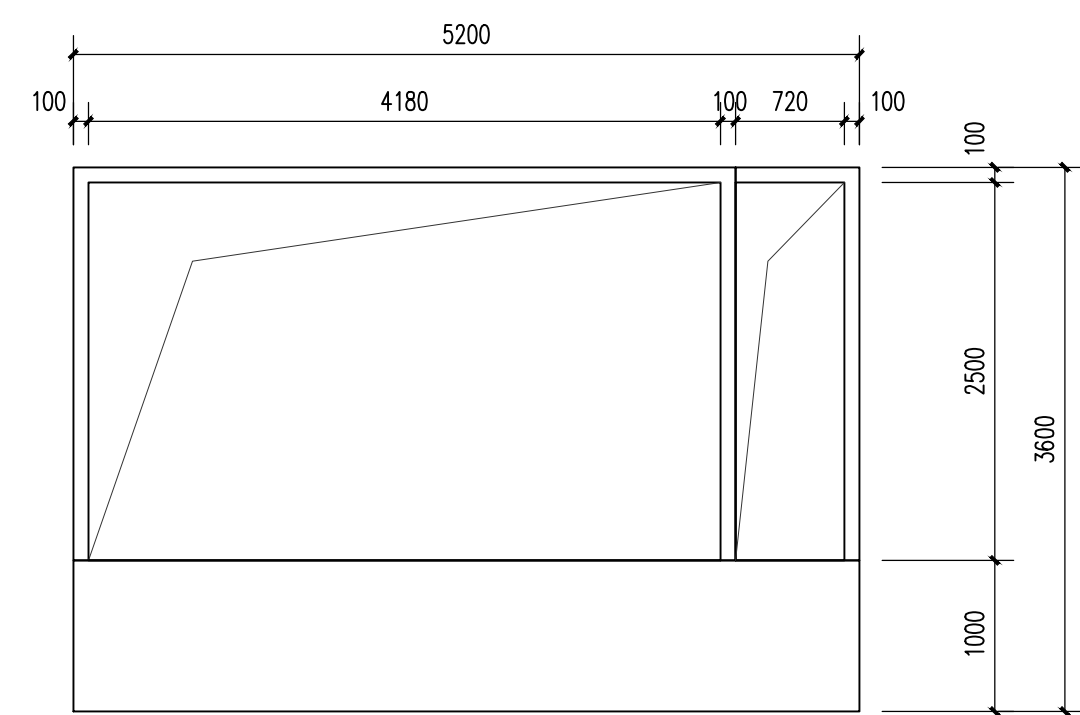

LED屏B 背视图 1:50

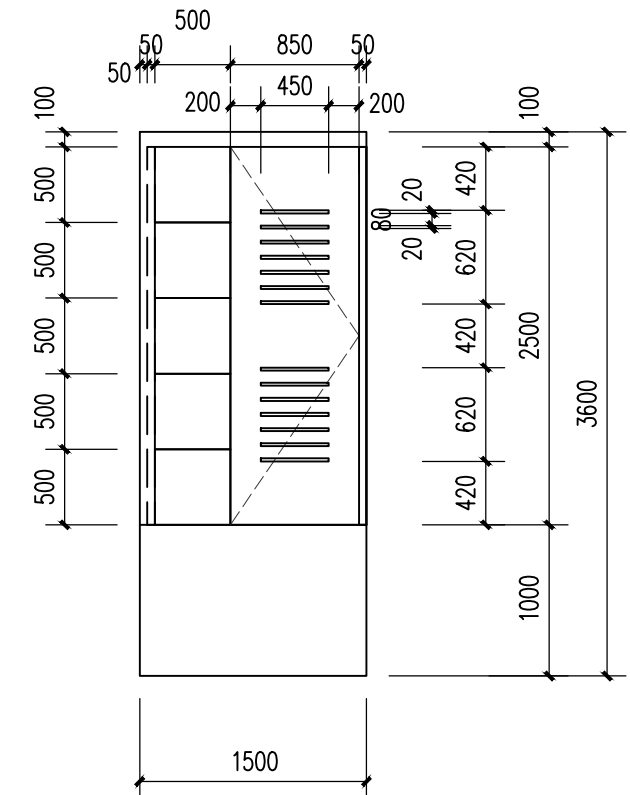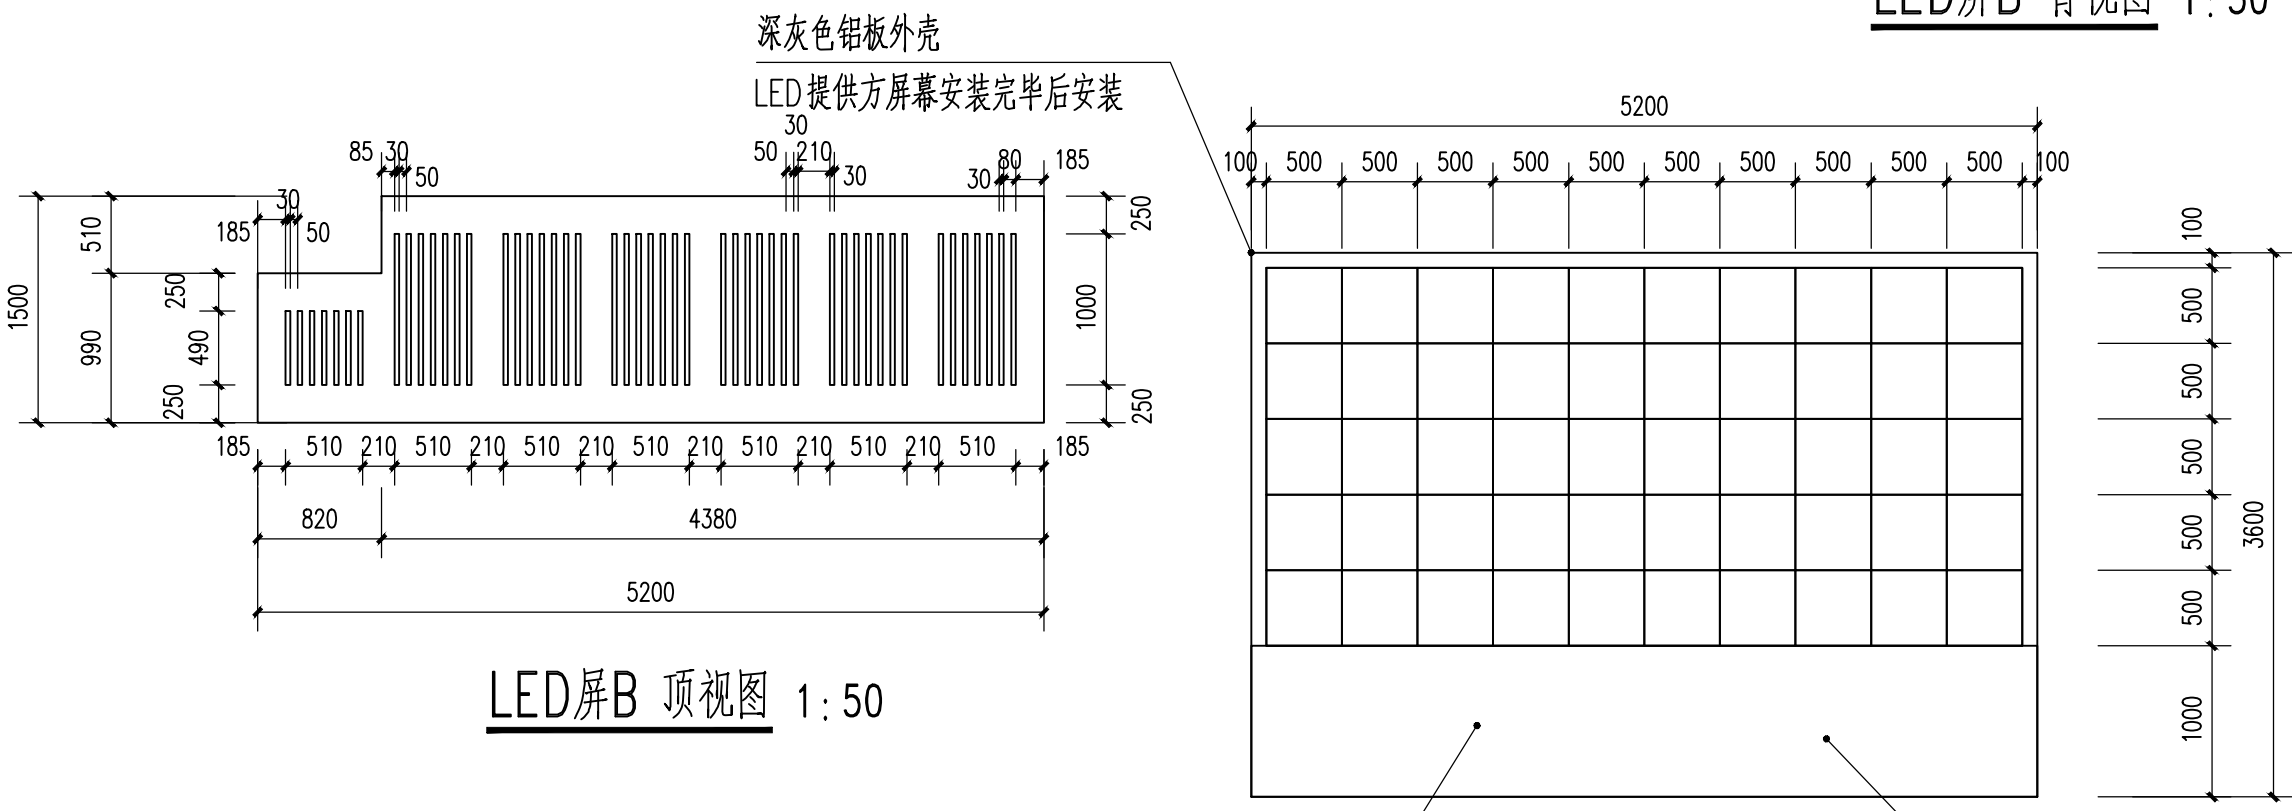


LED屏B 右侧视图 1:50

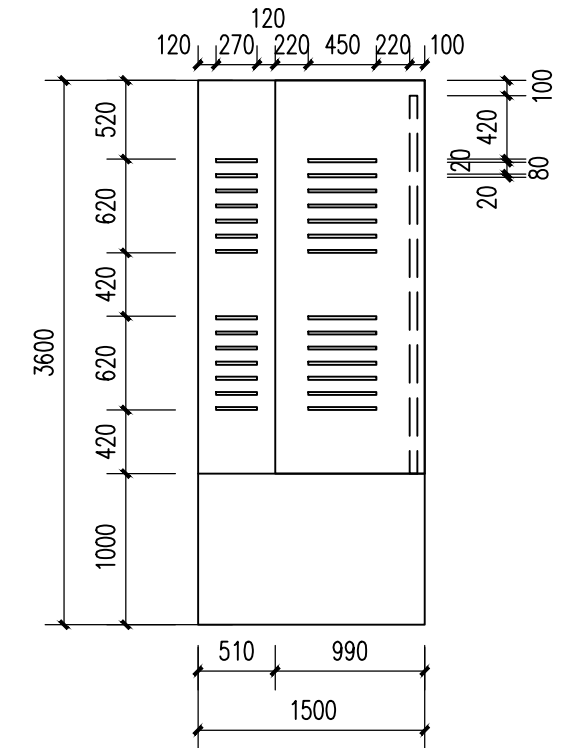


LED屏B 左侧视图 1:50


出图记录			ISSUE NOTES		
版 本 REV.	日 期 DATE	备 注 REMARK			
A	2022.02				
注册执业栏					
REGISTERED ARCHITECT/ENGINEER					
姓 名					
NAME					
注册证书号码					
REGISTRATION CERTIFICATE NO.					
注册印章号码					
STAMP NO.					
设计号: CD-20212856-F001					
JOB NO.					
工程名称					
PROJECT TITLE					
成都大运会主新闻中心装饰搭建					
子项名称					
SUB ITEM					
建设单位					
CLIENT					
成都博雅文瑞文化传播有限公司					
图 名					
DRAWING TITLE					
媒体工作间LED屏大样图					
单 位	mm	UNIT	图 别	室 施	DWG. CATEGORY
比 例	1:50	SCALE	图 号	D13	DWG. NO.
日 期	2022.02	DATE	版 本	A	VER. NO.
制 图	雷鑫鹏				
DRAWN BY					
设 计	李灏文				
DESIGNED BY					
校 对	李灏文				
CHECKED BY					
专业负责人	肖子颖				
DISCIPLINE CHIEF					
设计总负责人	张峻				
PROJECT CHIEF					
审 核	张峻				
AUDIT					
审 定	华轲				
APPROVED BY					
中 方 基 准					
成都基准方中建筑设计股份有限公司					
Chengdu JZJZ Architectural Design Co., Ltd.					
中国 成都市 琉璃路8号华润广场A座7-15楼					
电话: +86(28) 86333800 传真: +86(28) 86582990					
7-15F, Tower A, Criland Plaza, No.8,Liuli Road , Chengdu, P.R.C					
tel. +86(28) 86333800 fax. +86(28) 86582990					
工程设计资质证书编号: A151016191					
CAD 文件编号: -					
版 权 说 明					
COPYRIGHT DECLARATION					
此图版权为成都基准方中建筑设计股份有限公司所有, 未经许可不得使用。					

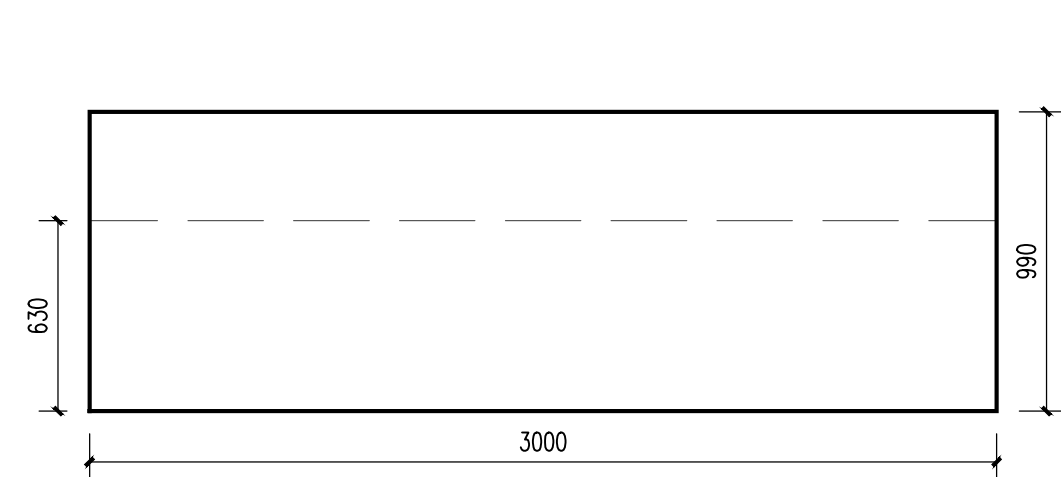


餐厅服务台 正视图 1: 25

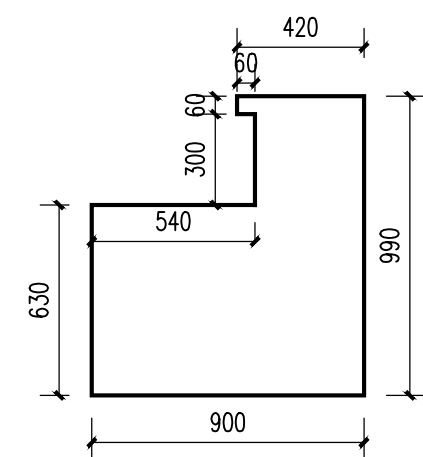


餐厅服务台 侧视图 1: 25

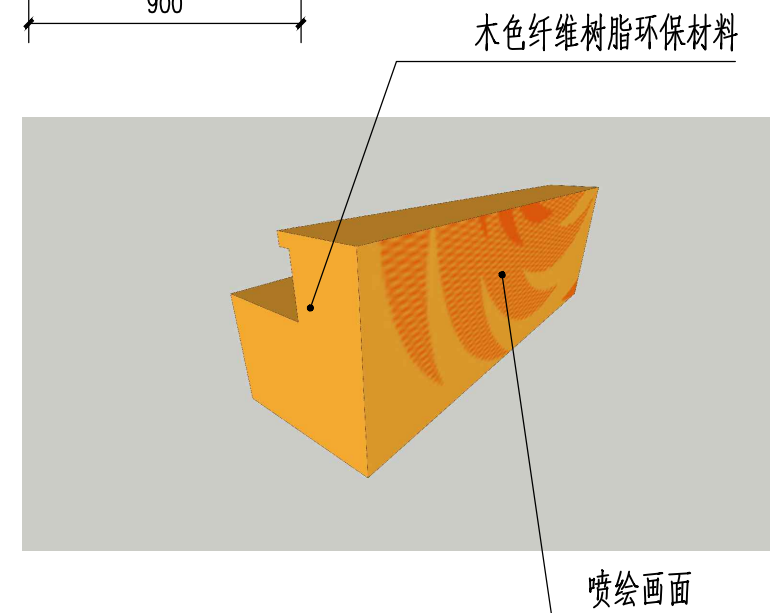


餐厅服务台 效果图

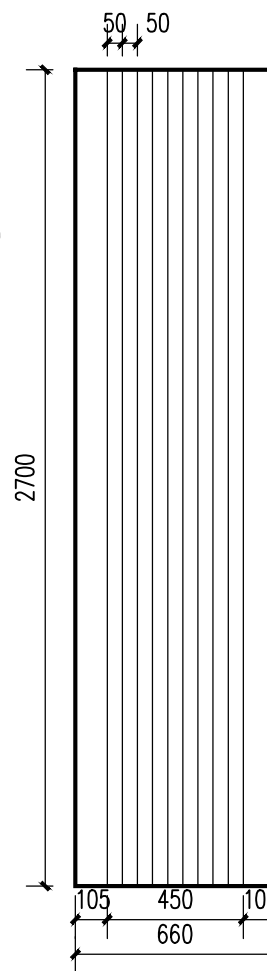


餐厅柱饰面 正视图 1:25

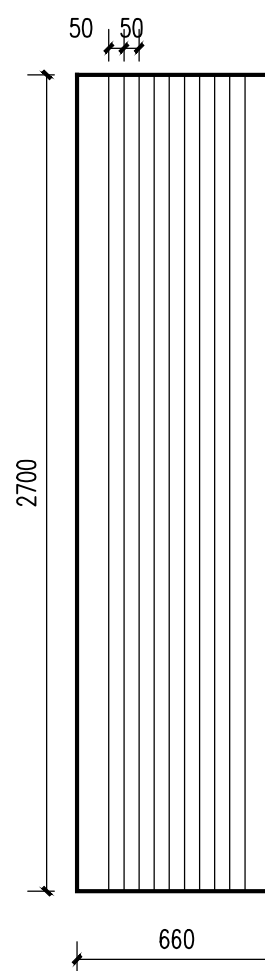

餐厅柱饰面 侧视图 1:25

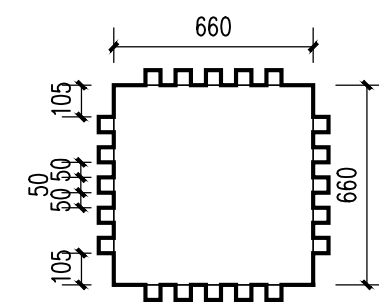


餐厅柱饰面 顶视图 1: 25

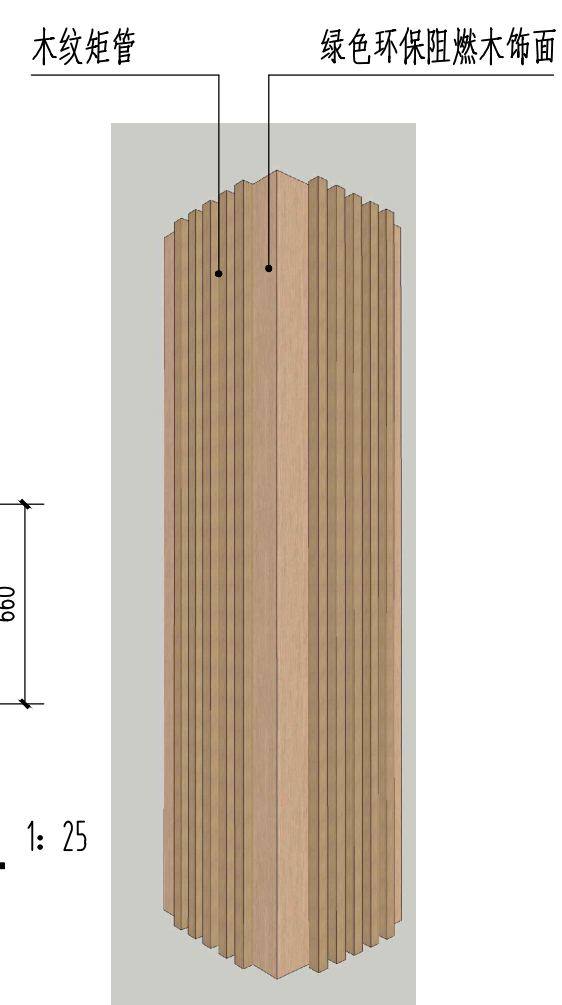

餐厅柱饰面 效果图

① 餐厅服务台大样图 1:25

② 餐厅柱饰面大样图 1:25

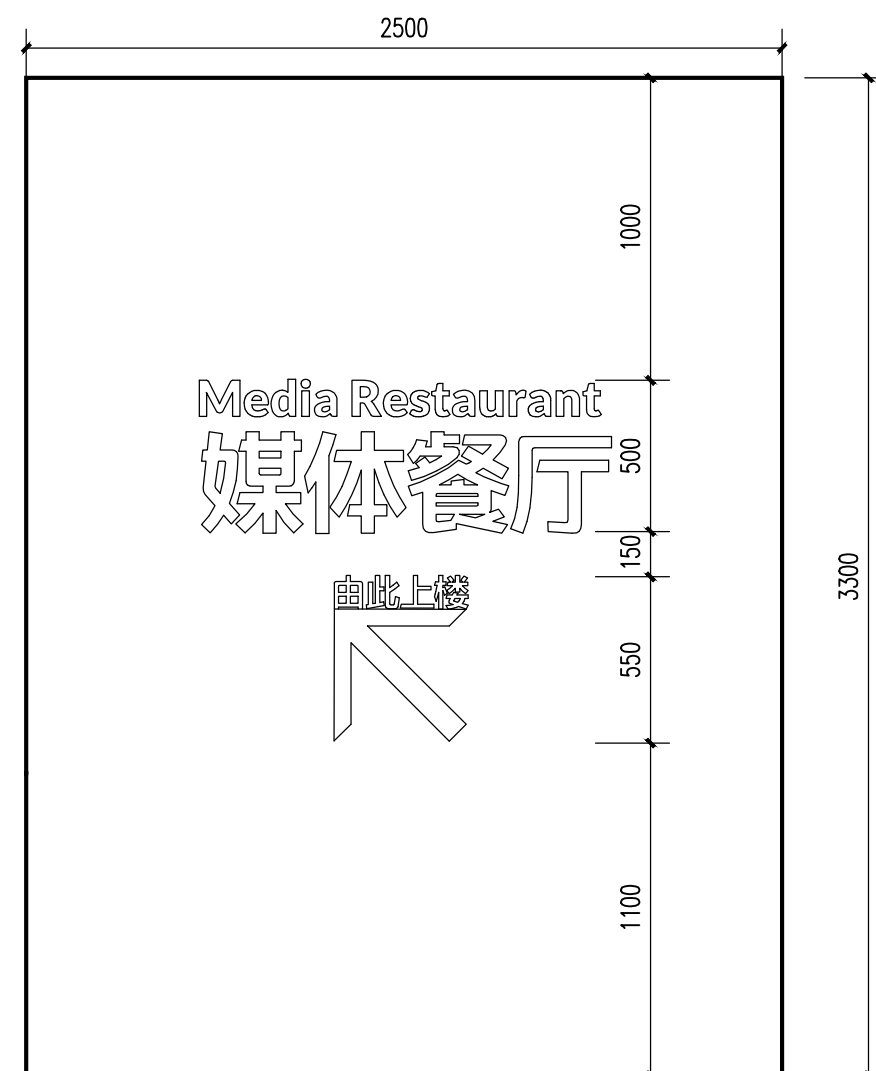


餐厅指示A 正视图 1:25

③ 餐厅指示A大样图 1:25



餐厅导视A 效果图

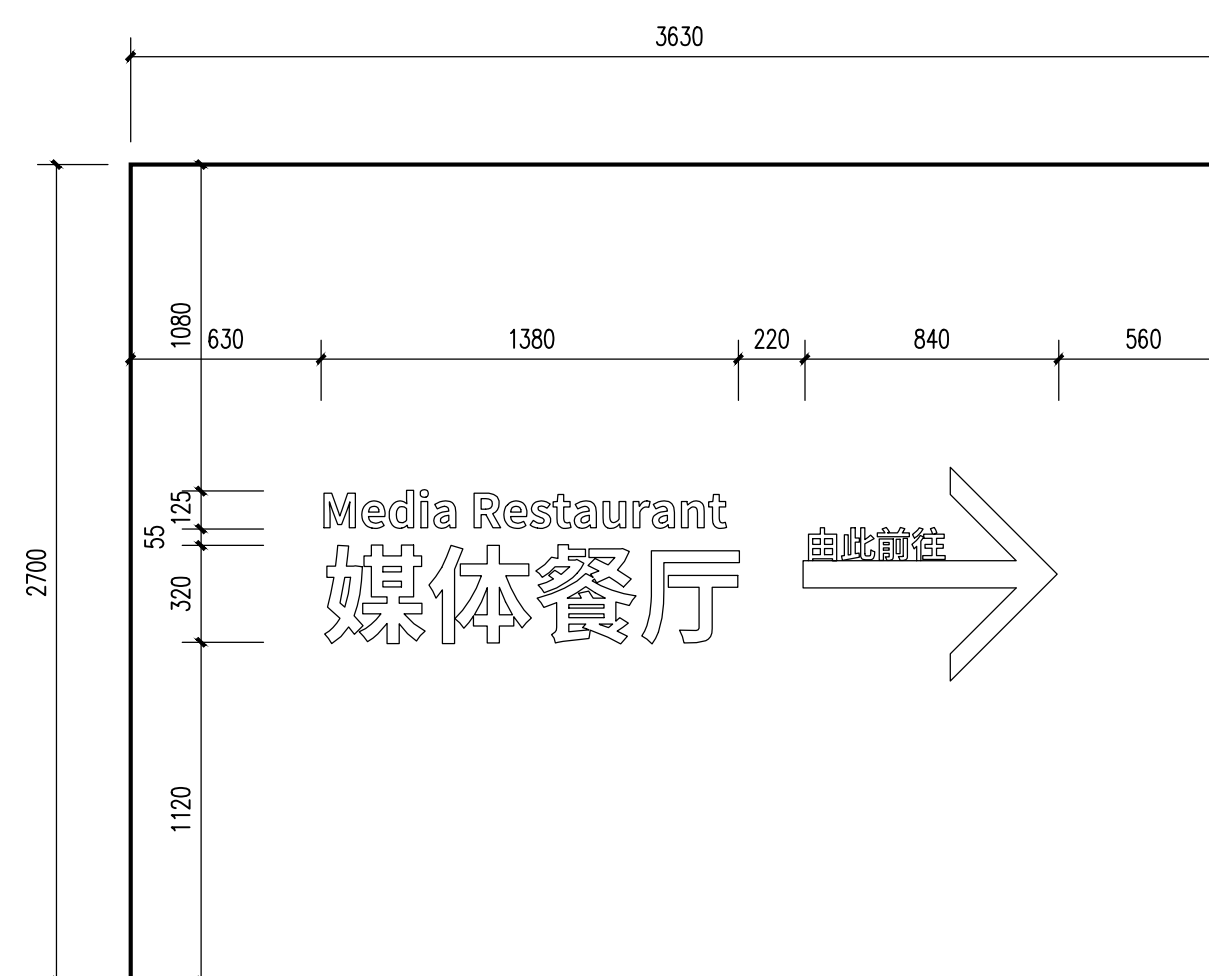



餐厅指示B 正视图 1:25

④ 餐厅指示B大样图 1:25




餐厅导视B 效果图

出图记录			ISSUE NOTES		
版本 REV.	日期 DATE	备注 REMARK			
A	2022.02				
注册执业栏					
REGISTERED ARCHITECT/ENGINEER					
姓 名					
NAME					
注册证书号码					
REGISTRATION CERTIFICATE NO.					
注册印章号码					
STAMP NO.					
设计号					
JOB NO.					
工程名称					
PROJECT TITLE					
成都大运会主新闻中心装饰搭建					
子项名称					
SUB ITEM					
建设单位					
CLIENT					
成都博雅文瑞文化传播有限公司					
图 名					
DRAWING TITLE					
餐厅服务台、柱饰面及指示大样图					
单 位	mm	UNIT	图 别	室 施	DWG. CATEGORY
比 例	1:25	SCALE	图 号	D 14	DWG. NO.
日 期	2022.02	DATE	版 本	A	VER. NO.
制 图	DRAWN BY		雷鑫鹏		
设 计	DESIGNED BY		雷鑫鹏		
校 对	CHECKED BY		李翔文		
专业负责人	DISCIPLINE CHIEF		肖子颖		
设计总负责人	PROJECT CHIEF		张竣		
审 核	AUDIT		张竣		
审 定	APPROVED BY		华轲		
图 基 准 方 中					
成都基准方中建筑设计股份有限公司					
Chengdu JZFY Architectural Design Co., Ltd.					
中国 成都市 琉璃路8号华润广场A座7-15楼					
电话: +86 (28) 86333800 传真: +86 (28) 86582990					
7-15F, Tower A, Criland Plaza, No.8Jiuli Road, Chengdu, P.R.C					
tel. +86(28) 86333800 fax. +86(28) 86582990					
工程设计资质证书编号: A151016191					
电子文档编号: -					
CAD 图框					
版 权 说 明					
COPYRIGHT DECLARATION					
此图版权为成都基准方中建筑设计股份有限公司所有, 未经许可不得使用。					

 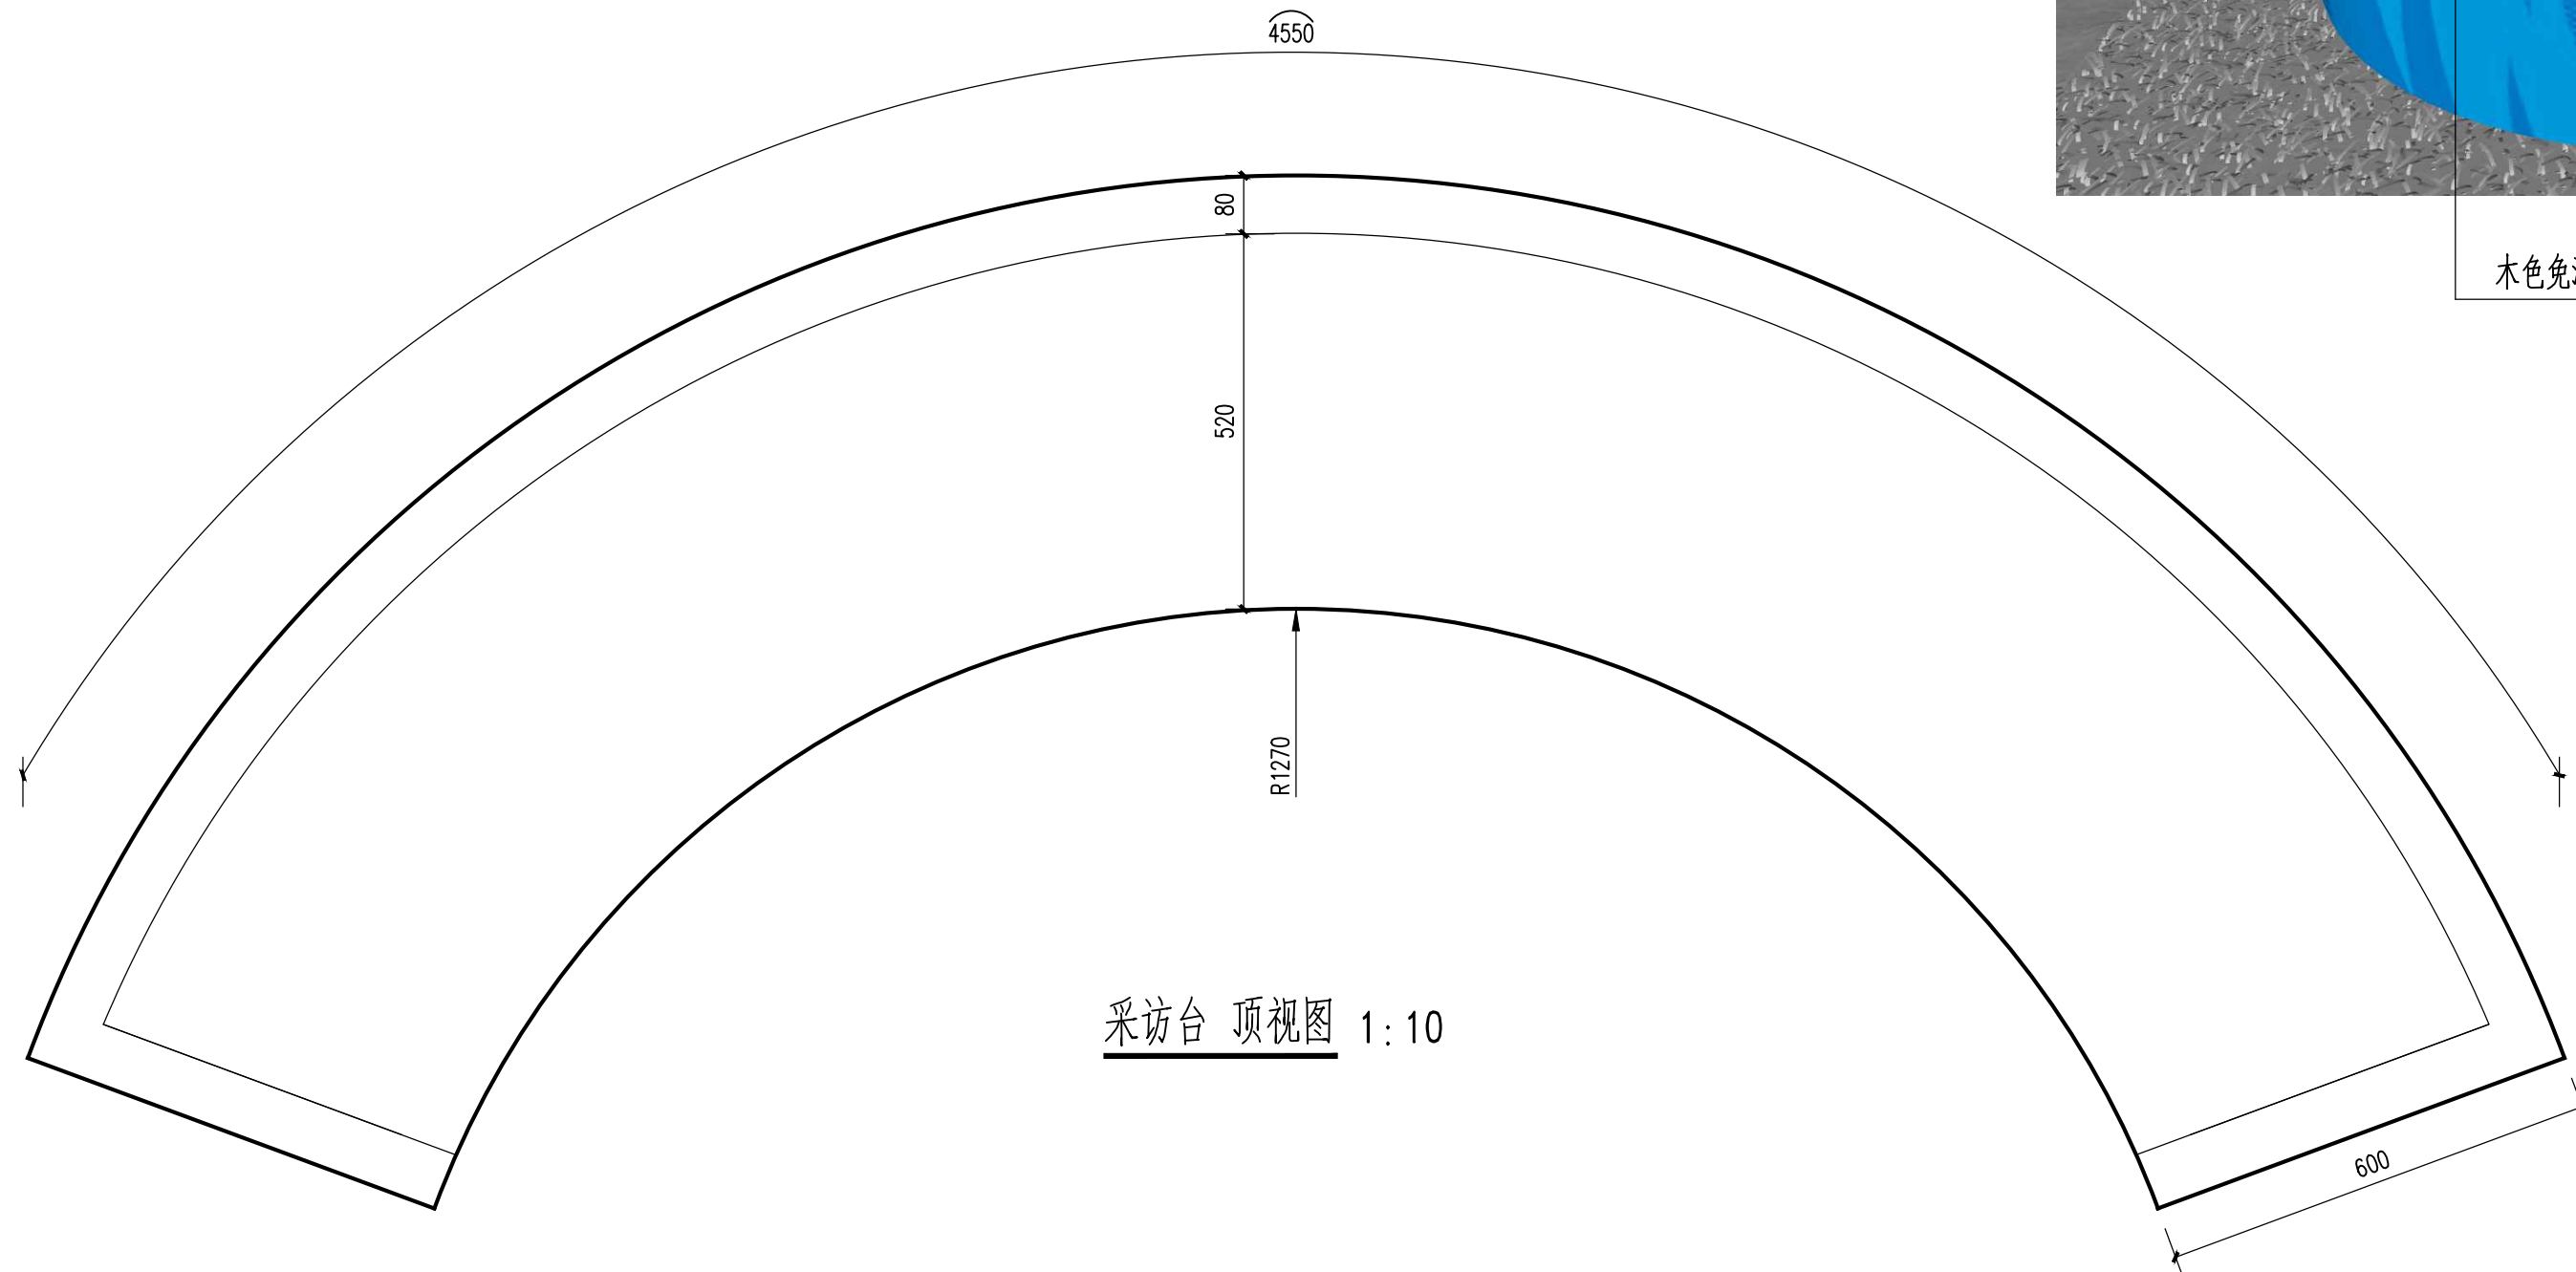

采访台 正面展开图 1:10

① 直播/采访间采访台大样图 1:10

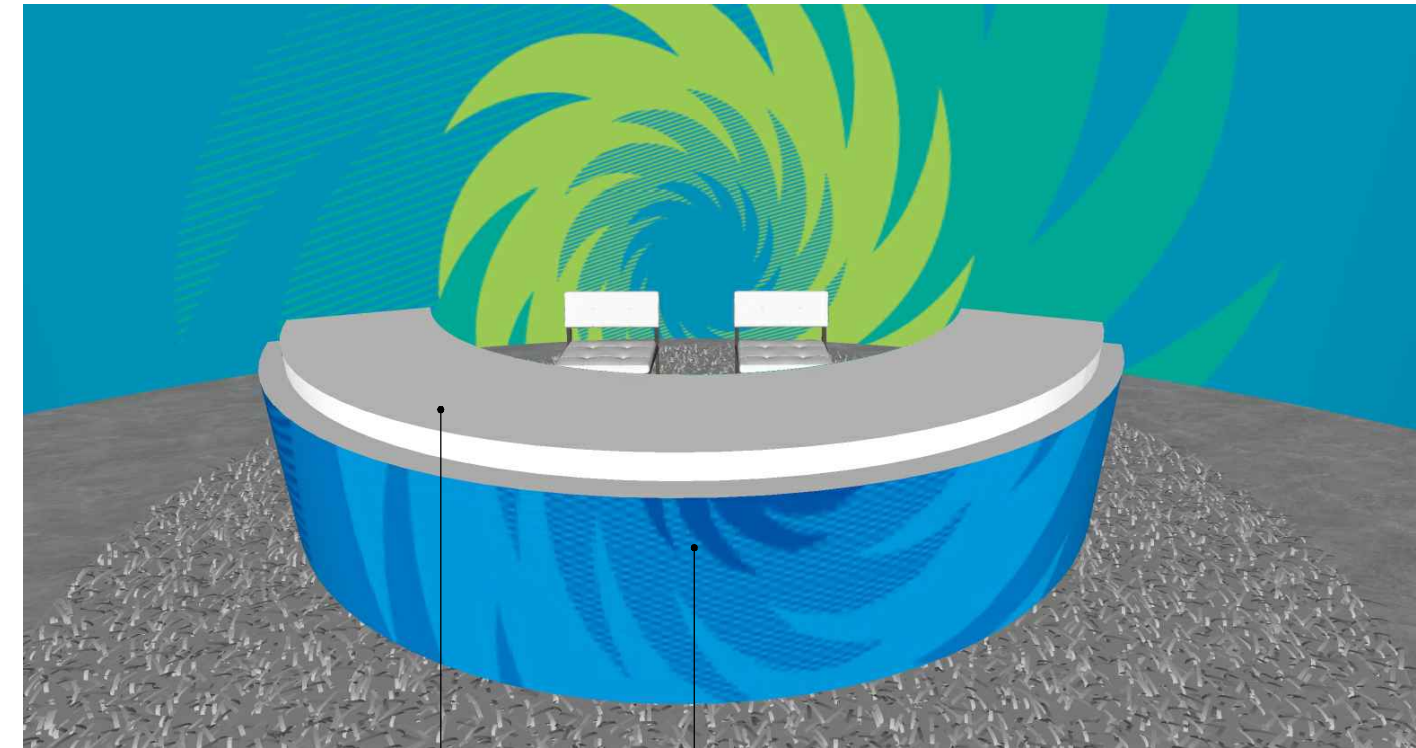

木色免漆板

大运会KV喷绘布

采访台 效果图


[illegible]

注册执业栏		REGISTERED ARCHITECT/ENGINEER	
姓 名		NAME	
注册证书号码		REGISTRATION CERTIFICATE NO.	
注册印章号码		STAMP NO.	
设计号: CD-2012856-F001		JOB NO.	
工程名称		PROJECT TITLE	
成都大运会主新闻中心装饰搭建			
子项名称		SUB ITEM	
弧形采访台 透视图			
建设单位:		CLIENT	
成都博雅文瑞文化传播有限公司			


图名		DRAWING	
直播/采访间采访台大样图			
单位	mm	UNIT	DWG. CATEGORY
比例	1:10	SCALE	DWG. NO.
日期	2022.02	DATE	VER. NO.
		图 号	室 施
		图 号	D15
		版 本	A

制 DRAWN BY	雷鑫鹏	
设 DESIGNED BY	雷鑫鹏	
校 CHECKED BY	李滢文	
专业负责人 DISCIPLINE CHIEF	肖子颖	
设计总负责人 PROJECT CHIEF	张峻	
审 AUDIT	张峻	
审 APPROVED BY	华轲	



中 方 基 准	
成都基准方中建筑设计股份有限公司	
Chengdu JZFC Architectural Design Co., Ltd.	
中国 成都市 琉璃路9号华润广场A座7-15楼	
电话: +86 (28) 86333800	传真: +86 (28) 86582990
7-15F, Tower A, Oriental Plaza, No.9Ruli Road., Chengdu, P.R.C	
tel. +86(28) 86333800	fax. +86(28) 86582990
工程投资资质证书编号: A151016191	
电子文档编号: -	
版 权 说 明	
COPYRIGHT DECLARATION	
此图版权为成都基准方中建筑设计股份有限公司所有, 未经许可不得使用。	

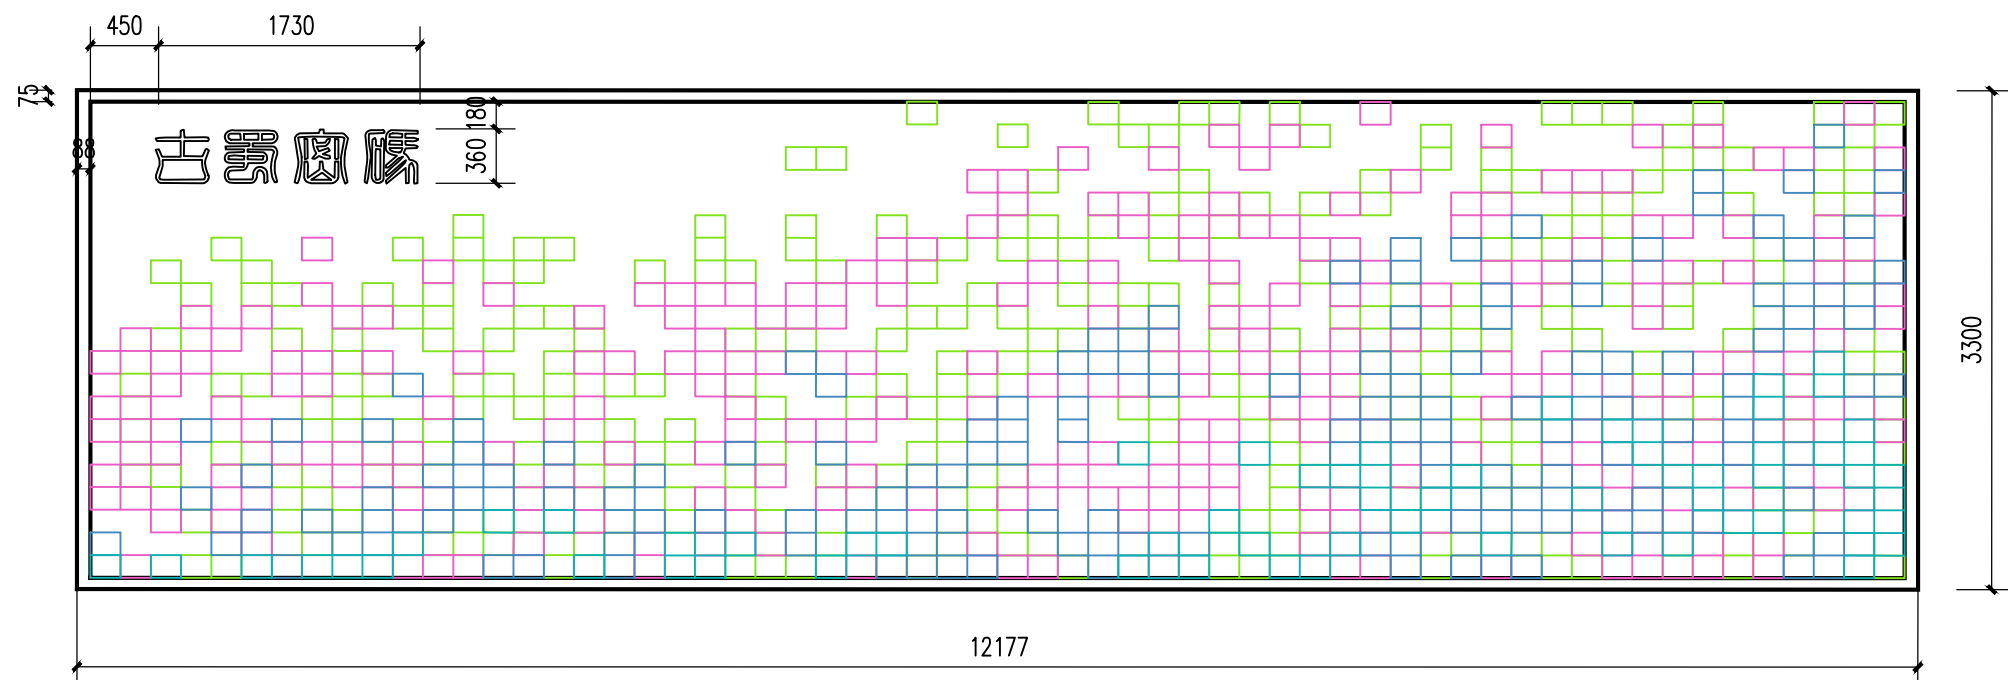

古蜀密码 正视图 1:50

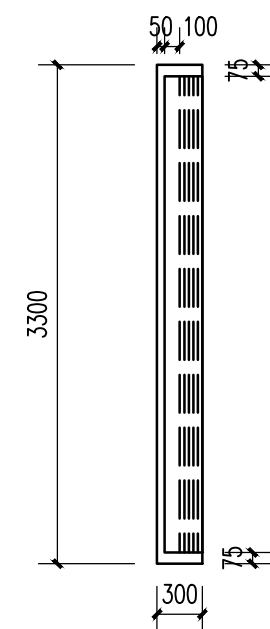

古蜀密码 侧视图 1:50

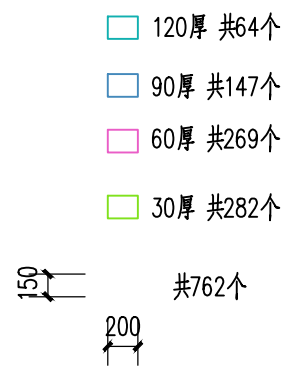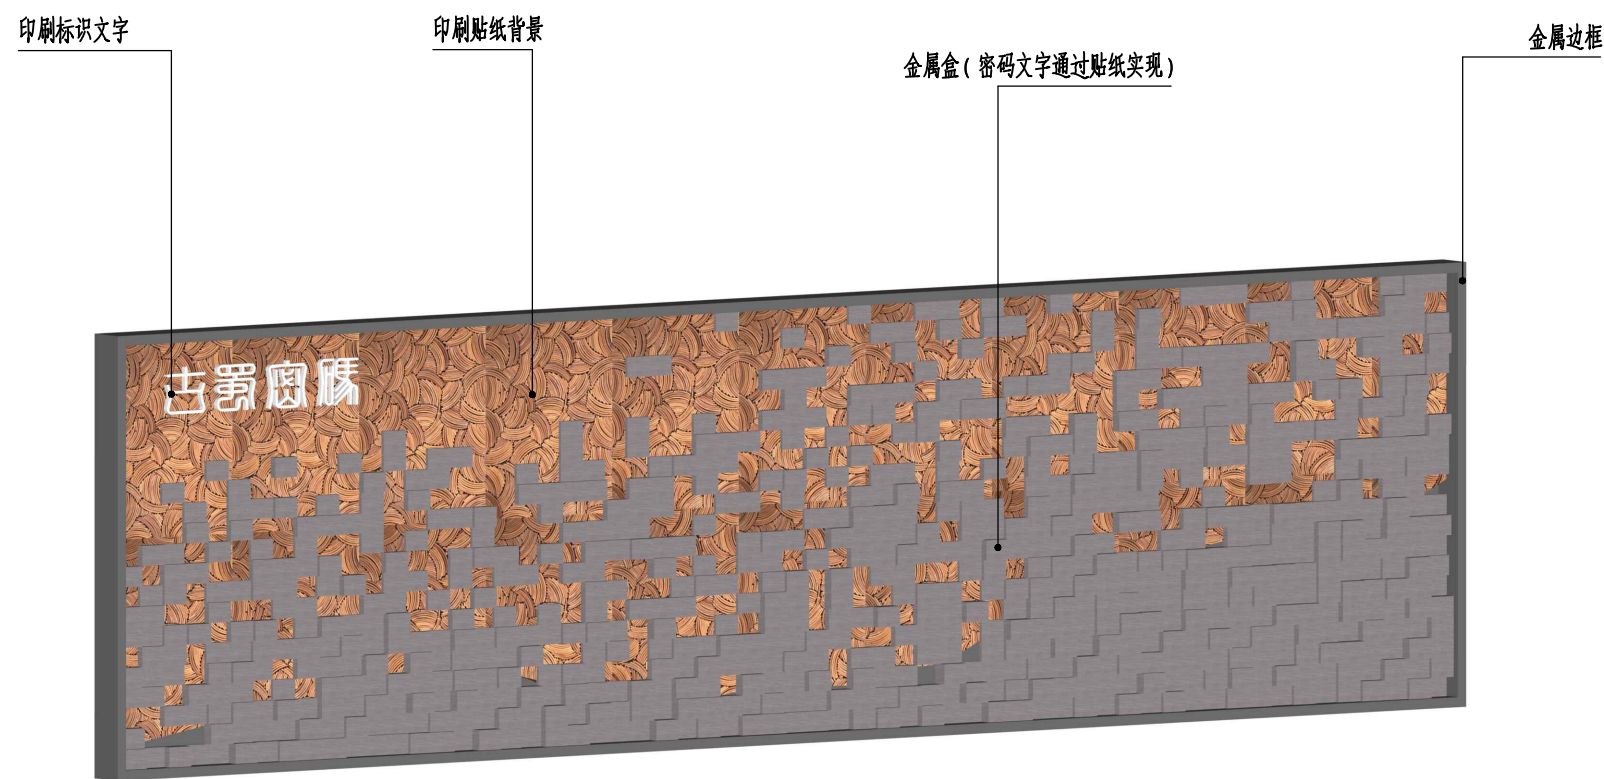


古蜀密码标准块详图 1:50

古蜀密码 效果图

① 古蜀密码大样图 1:50

出图记录			ISSUE NOTES	
版本 REV.	日期 DATE	备注 REMARK		
A	2022.02			
注册执业栏 REGISTERED ARCHITECT/ENGINEER				
姓 名				NAME
注册证书号码				REGISTRATION CERTIFICATE NO.
注册印章号码				STAMP NO.
设计号: CD-20212856-F001				JOB NO.
工程名称				PROJECT TITLE
成都大运会主新闻中心装饰搭建				
子项名称				SUB ITEM
建设单位				CLIENT
成都博雅文瑞文化传播有限公司				
图名				DRAWING TITLE
古蜀密码大样图				
单位: mm	UNIT	图 号	室 施	DWG. CATEGORY
比例: 1:50	SCALE	图 号	D16	DWG. NO.
日期: 2022.02	DATE	版 本	A	VER. NO.
制 图 DRAWN BY	雷鑫腾			
设 计 DESIGNED BY	罗 匀			
校 对 CHECKED BY	李 翊 文			
专业负责人 DISCIPLINE CHIEF	肖子颖			
设计总负责人 PROJECT CHIEF	张 竣			
审 核 AUDIT	张 竣			
审 定 APPROVED BY	华 柯			
图 基准方中				
成都基准方中建筑设计股份有限公司 Chengdu JZFC Architectural Design Co., Ltd.				
中国 成都市 琉璃路8号华润广场A座7-15楼 电话: +86(28) 86333800 传真: +86(28) 86582990 7-15F, Tower A, Grand Plaza, No.8, Liuli Road, Chengdu, P.R.C tel: +86(28) 86333800 fax: +86(28) 86582990				
工程设计资质证书编号: A151016191				
电子文档编号: --				CAO FILENAME
版 权 说 明 COPYRIGHT DECLARATION				
此图版权为成都基准方中建筑设计股份有限公司所有, 未经许可不得使用。				


合 格 栏	建 筑	电 气	采 暖 通 风	
	结 构	给 排 水	总 图	

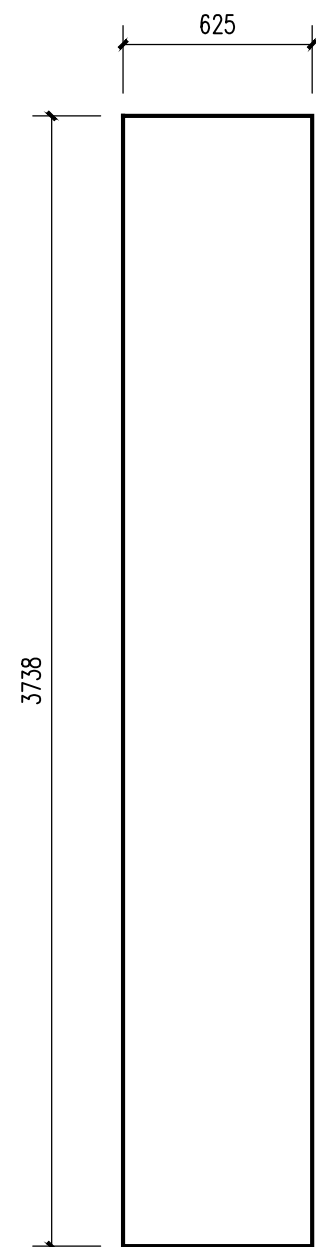

大运友谊墙侧视图 1:25




大运友谊墙效果图

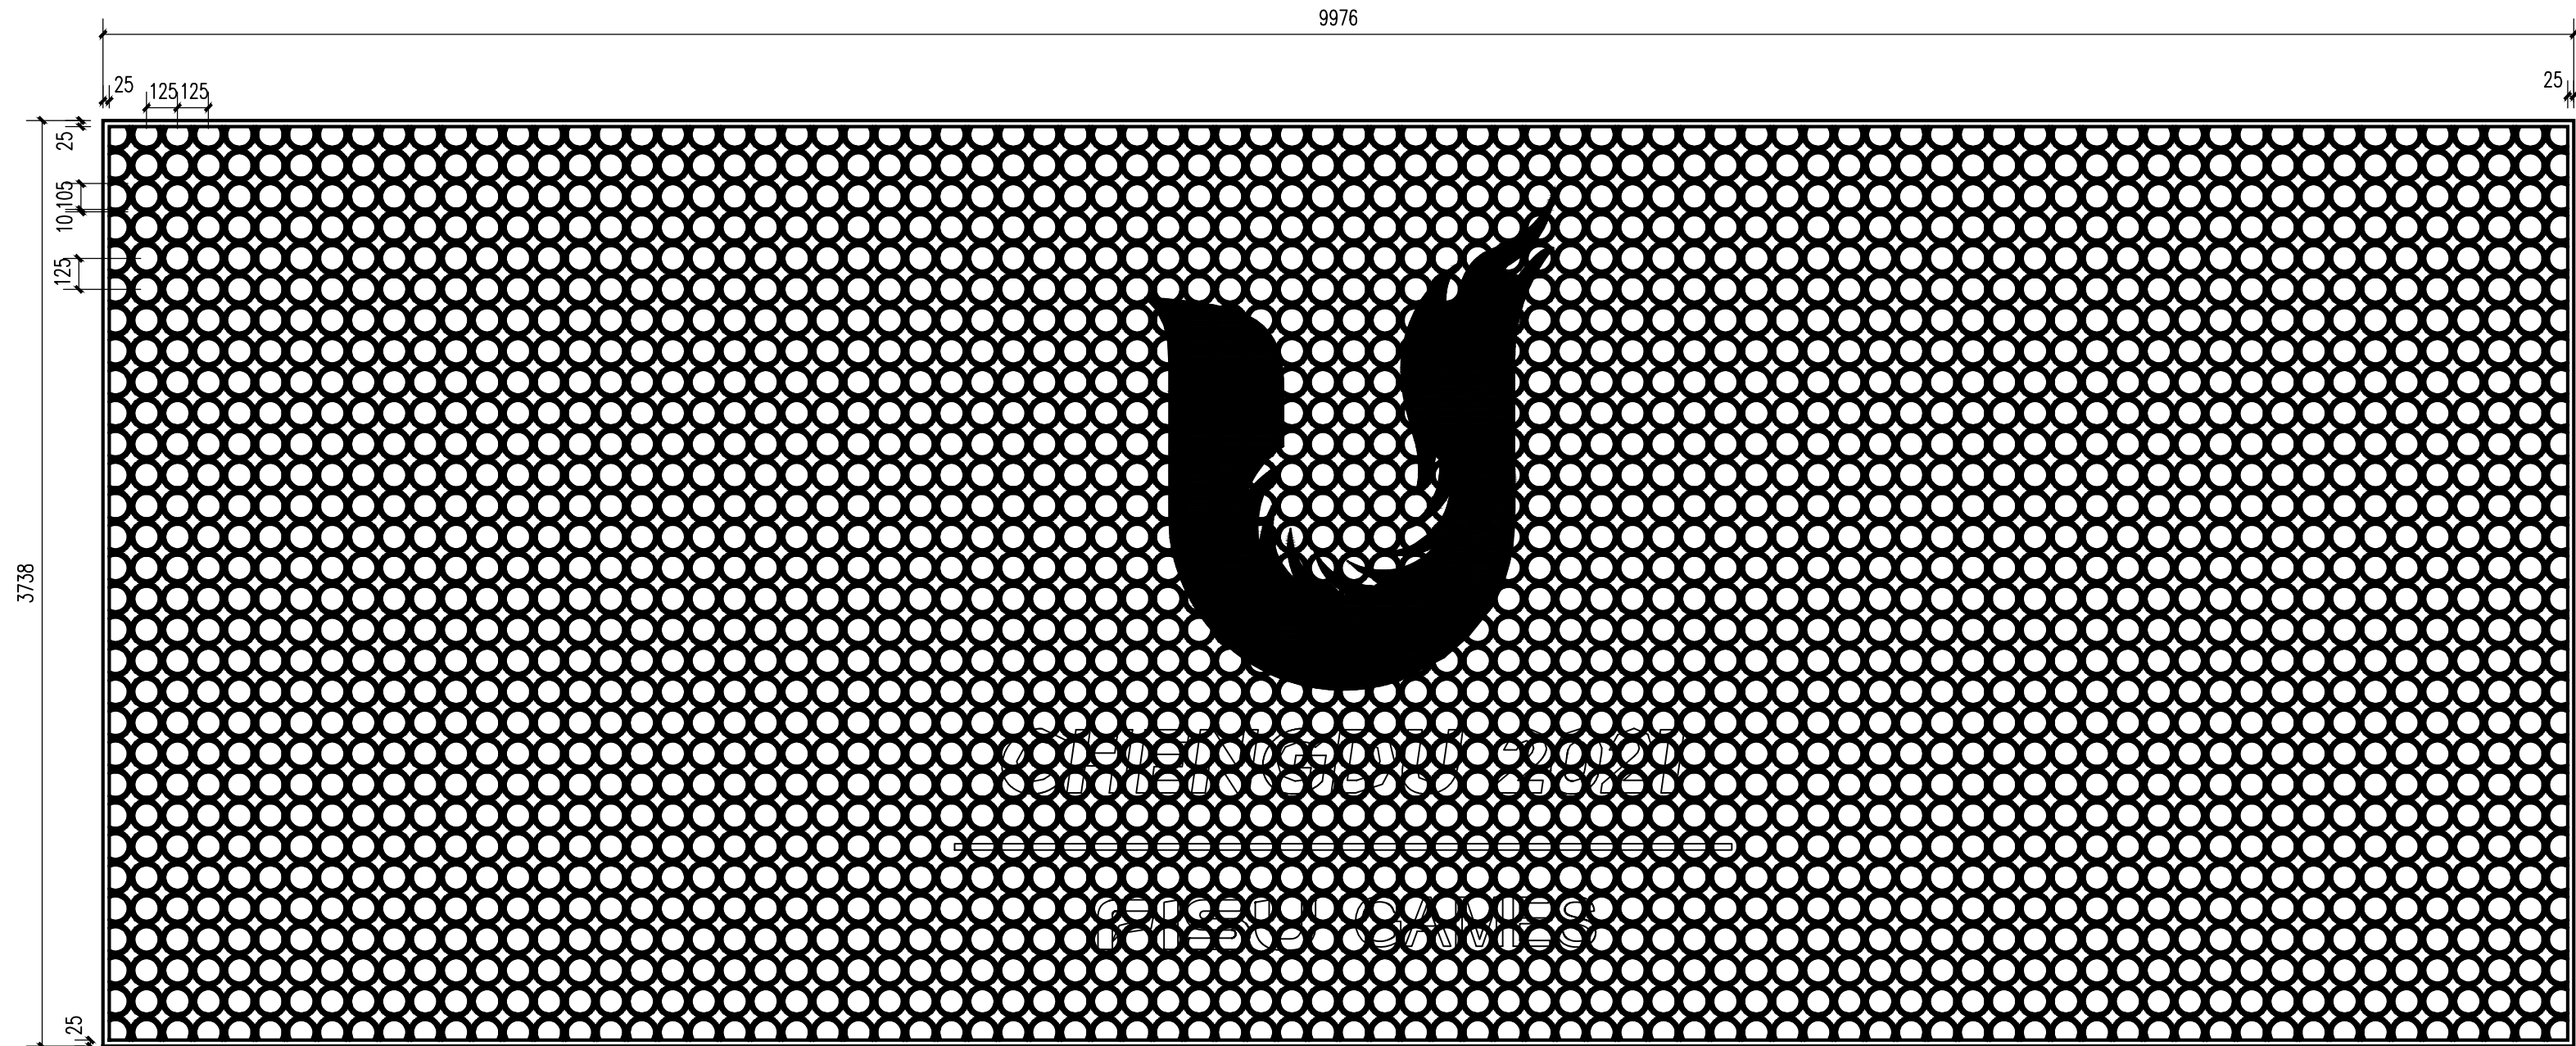


大运友谊墙正视图 1:25

① 大运友谊墙大样图 1:25


出图记录			ISSUE NOTES		
版本 REV.	日期 DATE	备注 REMARK			
A	2022.02				
注册执业栏 REGISTERED ARCHITECT/ENGINEER					
姓 名					NAME
注册证书号码					REGISTRATION CERTIFICATE NO.
注册印章号码					STAMP NO.
设计号: CD-20212856-F001					JOB NO.
工程名称					PROJECT TITLE
成都大运会主新闻中心装饰搭建					
子项名称					SUB ITEM
建设单位					CLIENT
成都博雅文瑞文化传播有限公司					
图 名 DRAWING TITLE					
大运会友谊墙大样图					
单 位	mm	UNIT	图 别	室 施	DWG. CATEGORY
比 例	1:25	SCALE	图 号	D17	DWG. NO.
日 期	2022.02	DATE	版 本	A	VER. NO.
制 图 DRAWN BY	雷鑫鹏				
设 计 DESIGNED BY	罗 匀				
校 对 CHECKED BY	李 翔 文				
专业负责人 DISCIPLINE CHIEF	肖子颖				
设计总负责人 PROJECT CHIEF	张 峻				
审 核 AUDIT	张 峻				
审 定 APPROVED BY	华 柯				
图 基 准 方 中					
成都基准方中建筑设计股份有限公司 Chengdu JZFC Architectural Design Co., Ltd.					
中国 成都市 琉璃路8号华润广场A座7-15楼 电话: +86(28) 86333800 传真: +86(28) 86582990 7-15F, Tower A, Crand Plaza, No.8Jinli Road , Chengdu, P.R.C tel. +86(28) 86333800 fax. +86(28) 86582990					
工程设计资质证书编号: A151016191					
电子文档编号: -					CAD FILENAME
版 权 说 明 COPYRIGHT DECLARATION					
此图版权为成都基准方中建筑设计股份有限公司所有, 未经许可不得使用。					

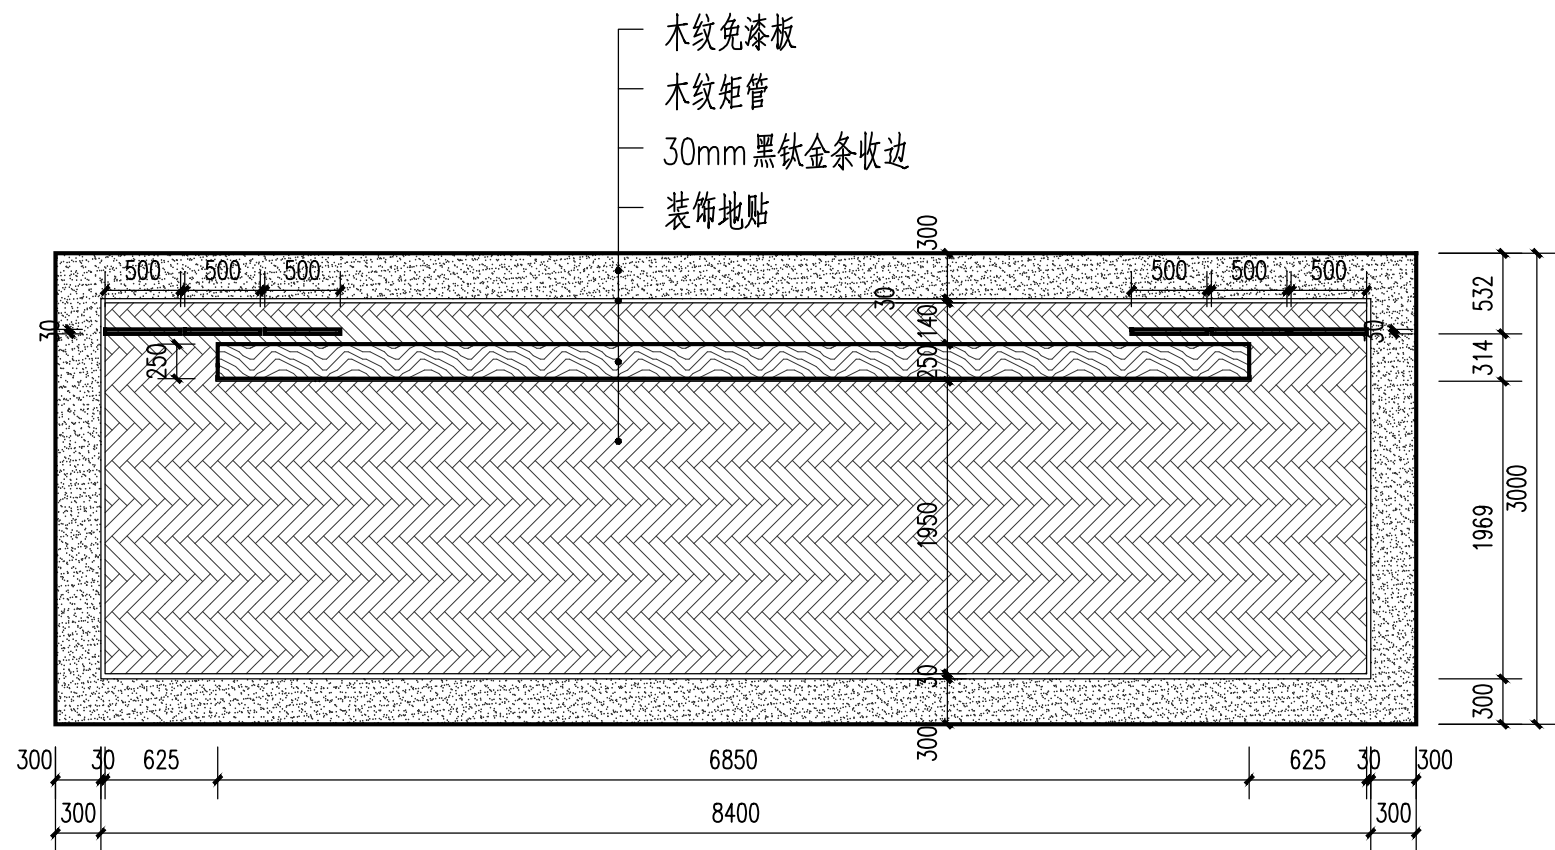


川剧表演舞台顶视图 1:50

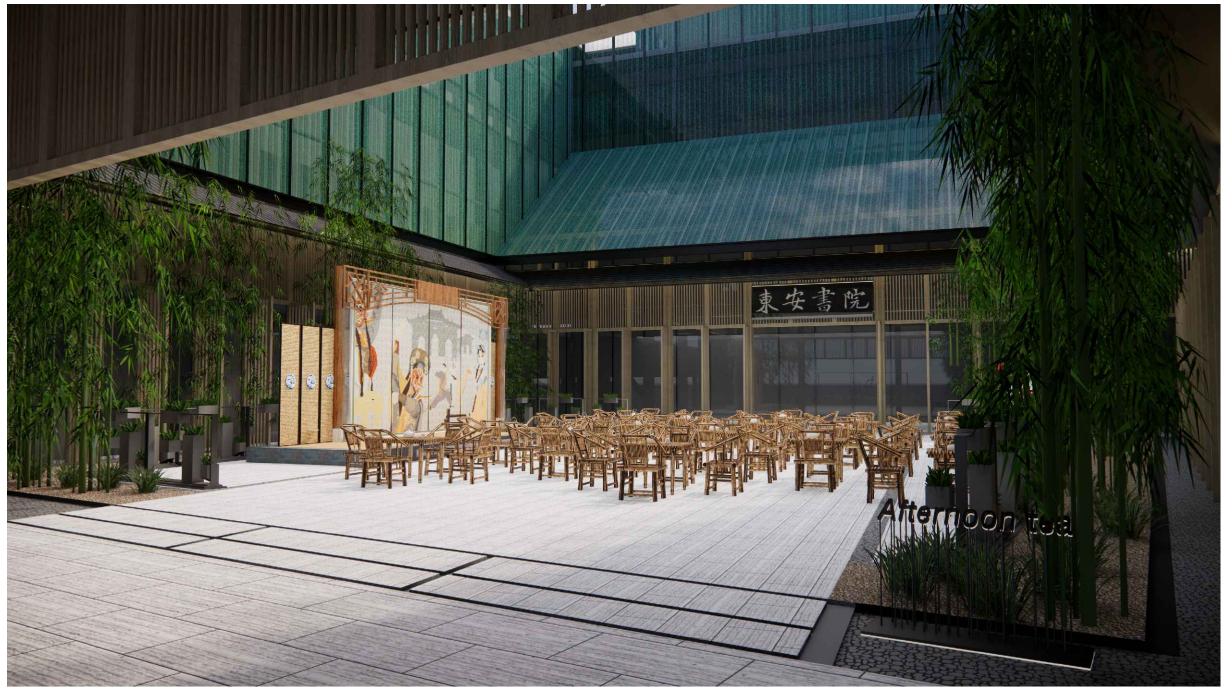


川剧表演舞台效果图

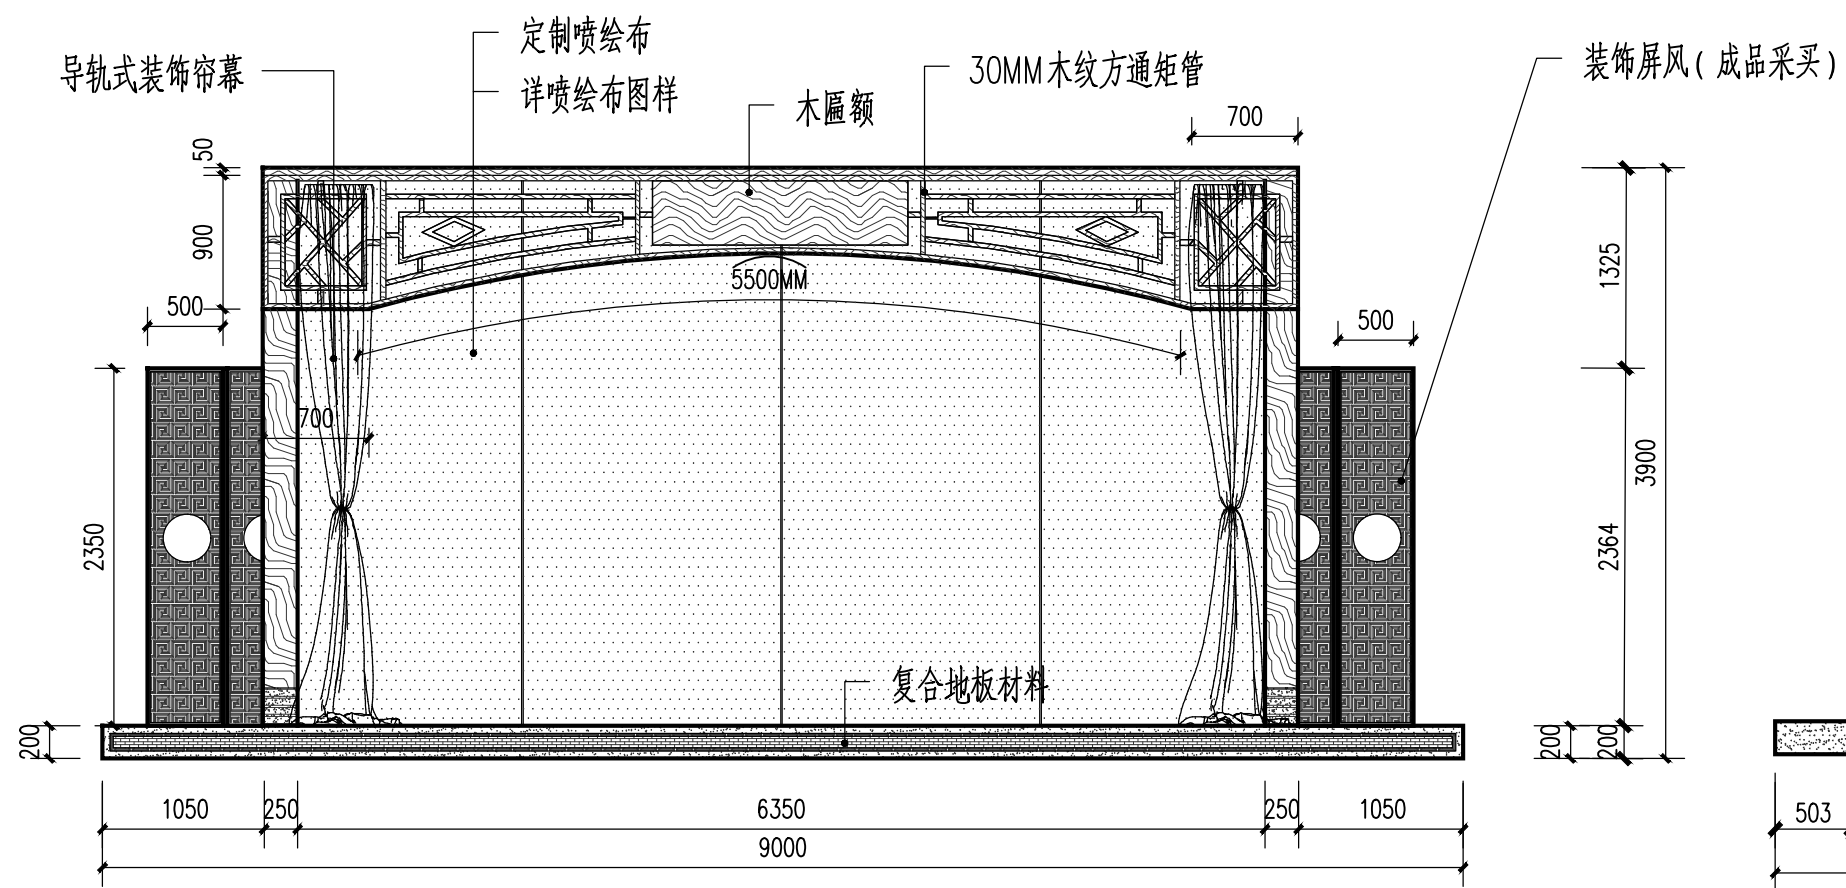

川剧表演舞台正视图 1:50

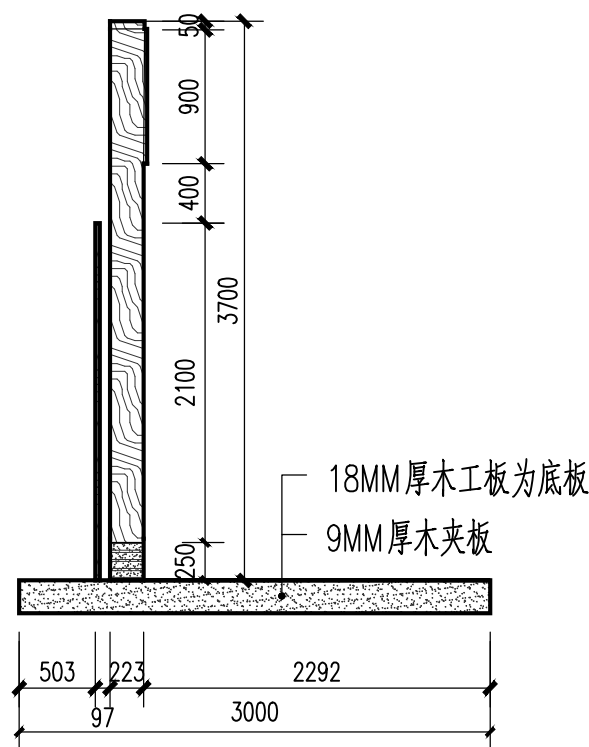


川剧表演舞台侧视图 1:50

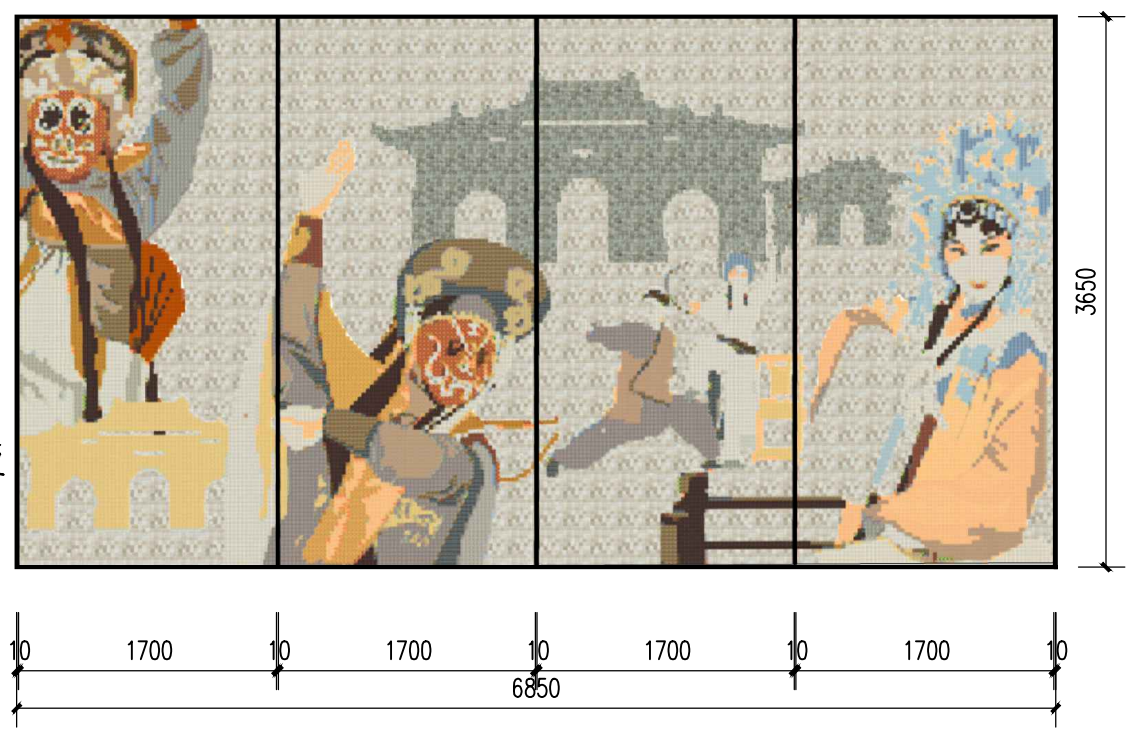


川剧表演舞台背景板正视图 1:50

① 川剧表演舞台大样图 1:50


出图记录			ISSUE NOTES	
版 本 REV.	日 期 DATE	备 注 REMARK		
A	2022.02			
注册执业栏				
		REGISTERED ARCHITECT/ENGINEER		
姓 名		NAME		
注册证书号码		REGISTRATION CERTIFICATE NO.		
注册印章号码		STAMP NO.		
设计号: CD-20212856-F001		JOB NO.		
工程名称		PROJECT TITLE		
成都大运会主新闻中心装饰搭建				
子项名称		SUB ITEM		
建设单位		CLIENT		
成都博雅文瑞文化传播有限公司				
图 名		DRAWING TITLE		
川剧表演舞台大样图				
单 位	mm	UNIT	图 别	室 施
			DWG. CATEGORY	
比 例	1:50	SCALE	图 号	D18
			DWG. NO.	
日 期	2022.02	DATE	版 本	A
			VER. NO.	
制 图	罗 匀			
DRAWN BY				
设 计	罗 匀			
DESIGNED BY				
校 对	李 灏 文			
CHECKED BY				
专业负责人	肖子颖			
DISCIPLINE CHIEF				
设计总负责人	张 竣			
PROJECT CHIEF				
审 核	张 竣			
AUDIT				
审 定	华 轲			
APPROVED BY				
园 基 准 方 中				
成都基准方中建筑设计股份有限公司				
Chengdu JZFY Architectural Design Co., Ltd.				
中国 成都市 琉璃路8号华润广场A座7-15楼				
电话: +86(28) 86333800 传真: +86(28) 86582990				
7-15F, Tower A, Cifand Plaza, No.8,Liuli Road , Chengdu, P.R.C				
tel. +86(28) 86333800 fax. +86(28) 86582990				
工程设计资质证书编号: A151016191				
电子文档编号: --				
CAD FILENAME				
版 权 说 明				
COPYRIGHT DECLARATION				
此图版权为成都基准方中建筑设计股份有限公司所有, 未经许可不得使用。				

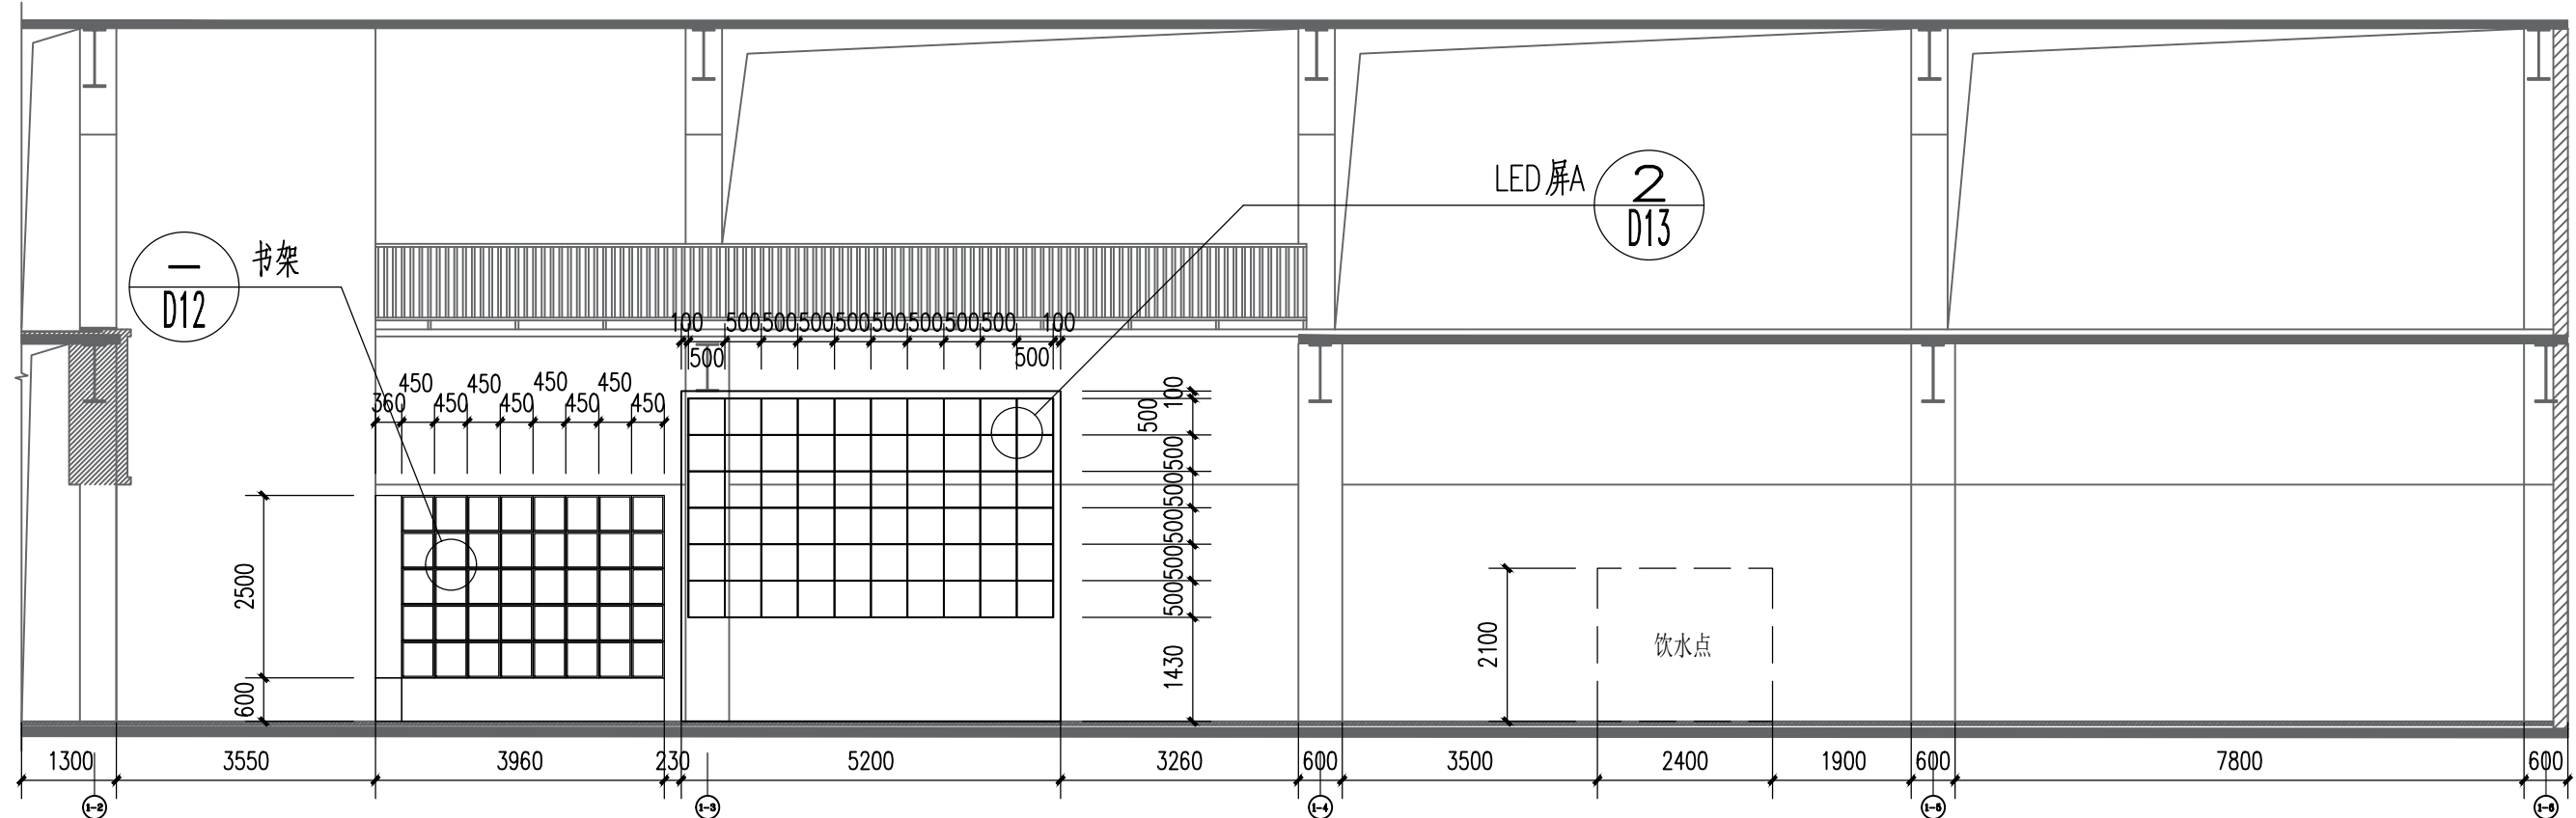


媒体工作间 A立面图 1:100

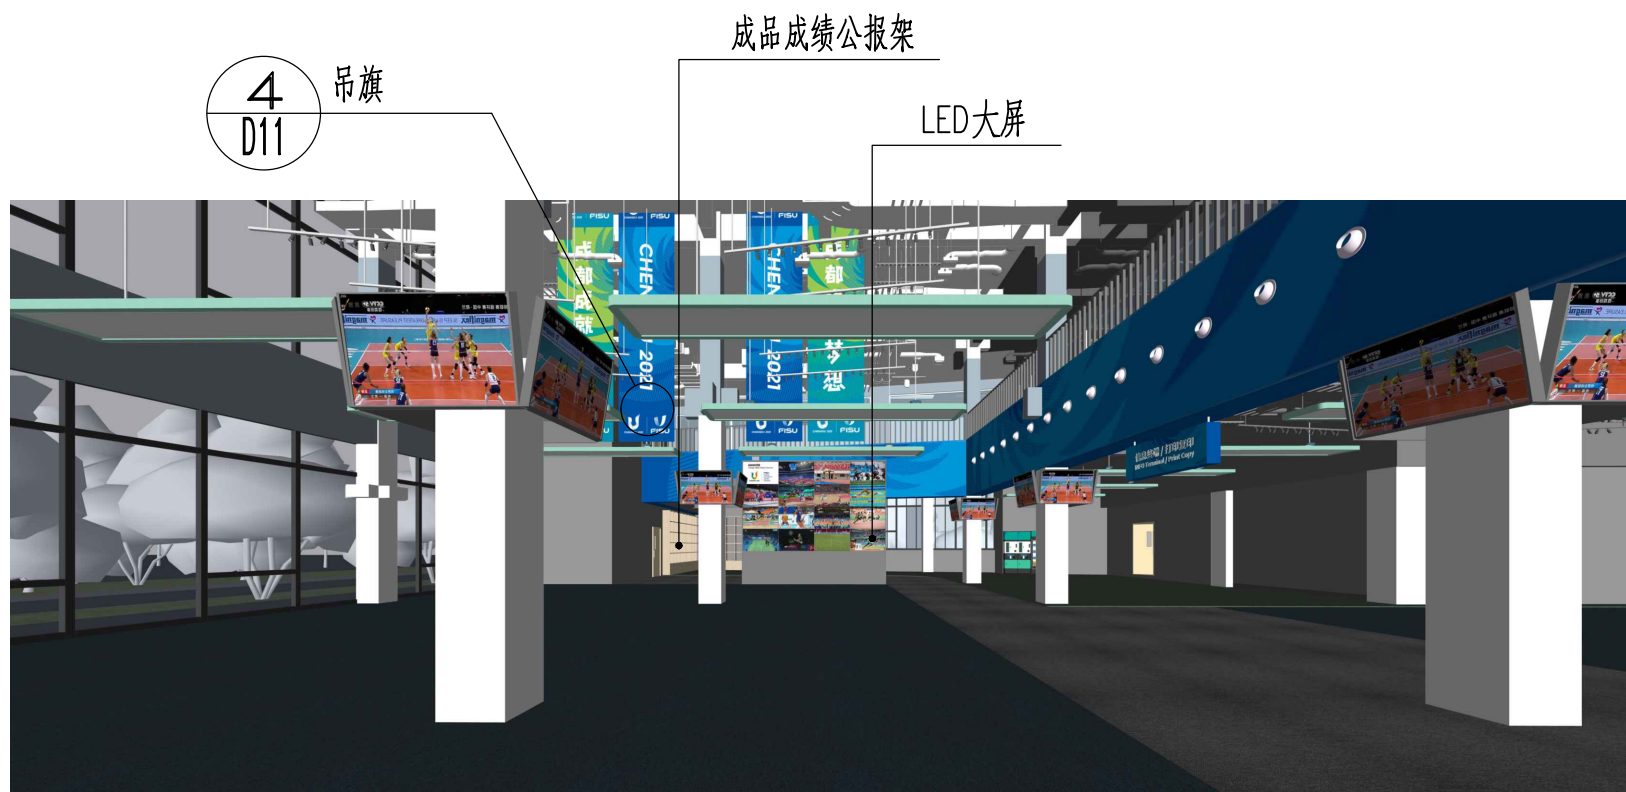

媒体工作间 A立面效果图


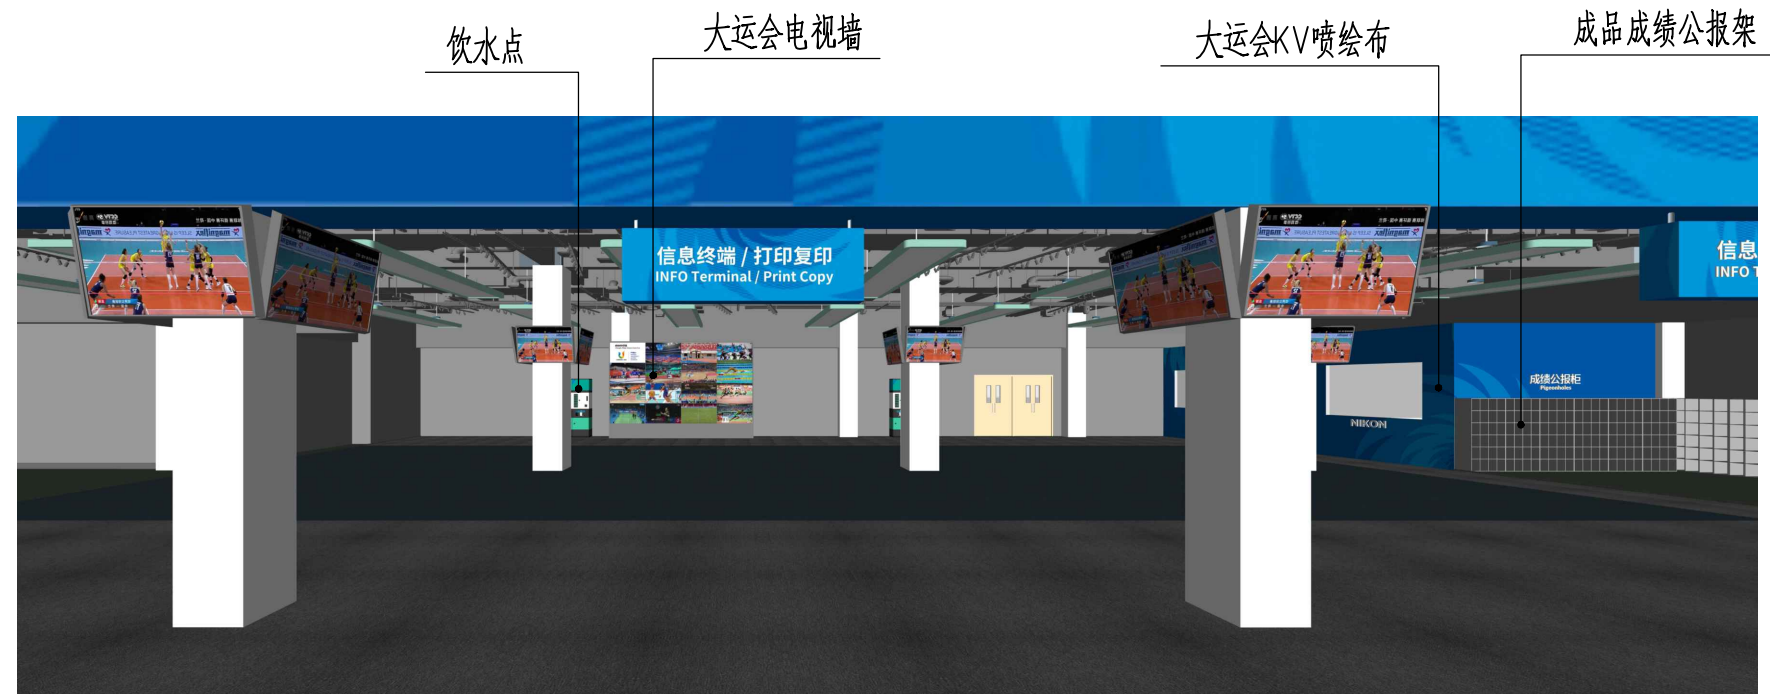


媒体工作间 B立面效果图

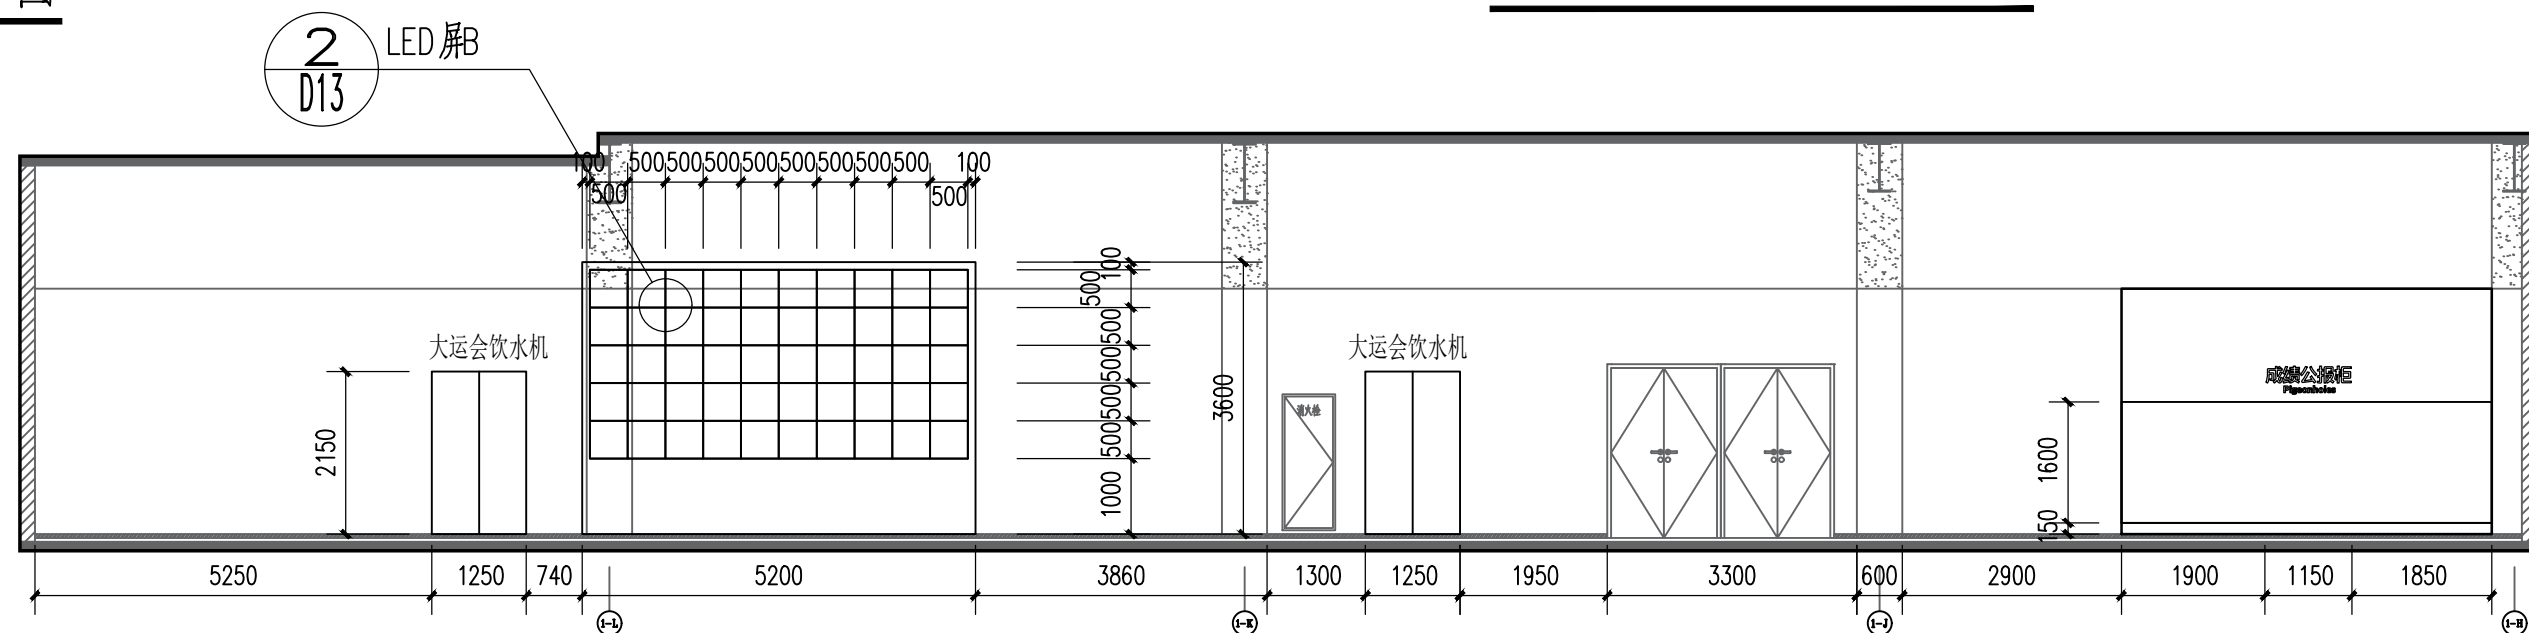


媒体工作间 B立面图 1:100


[illegible]

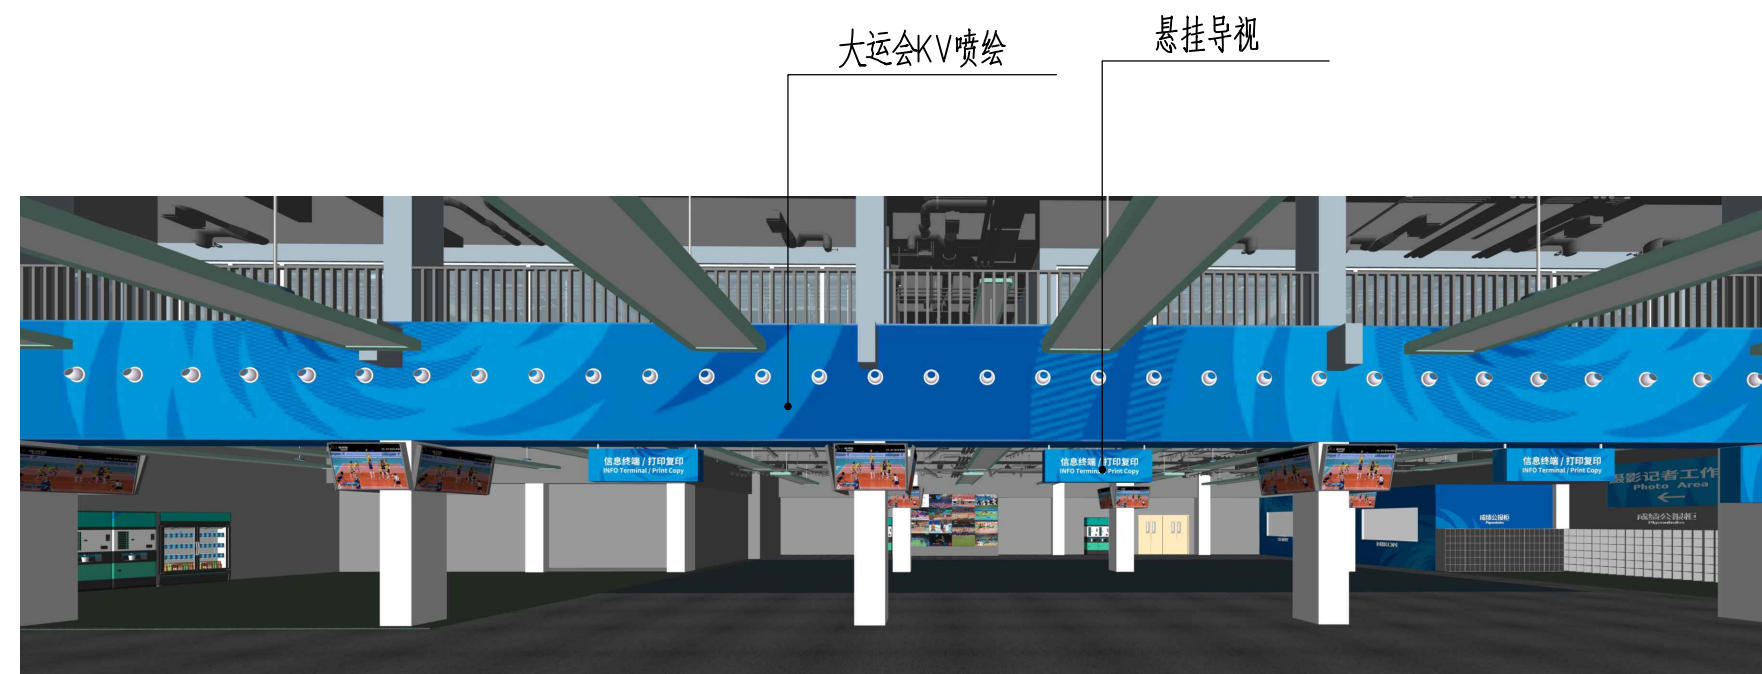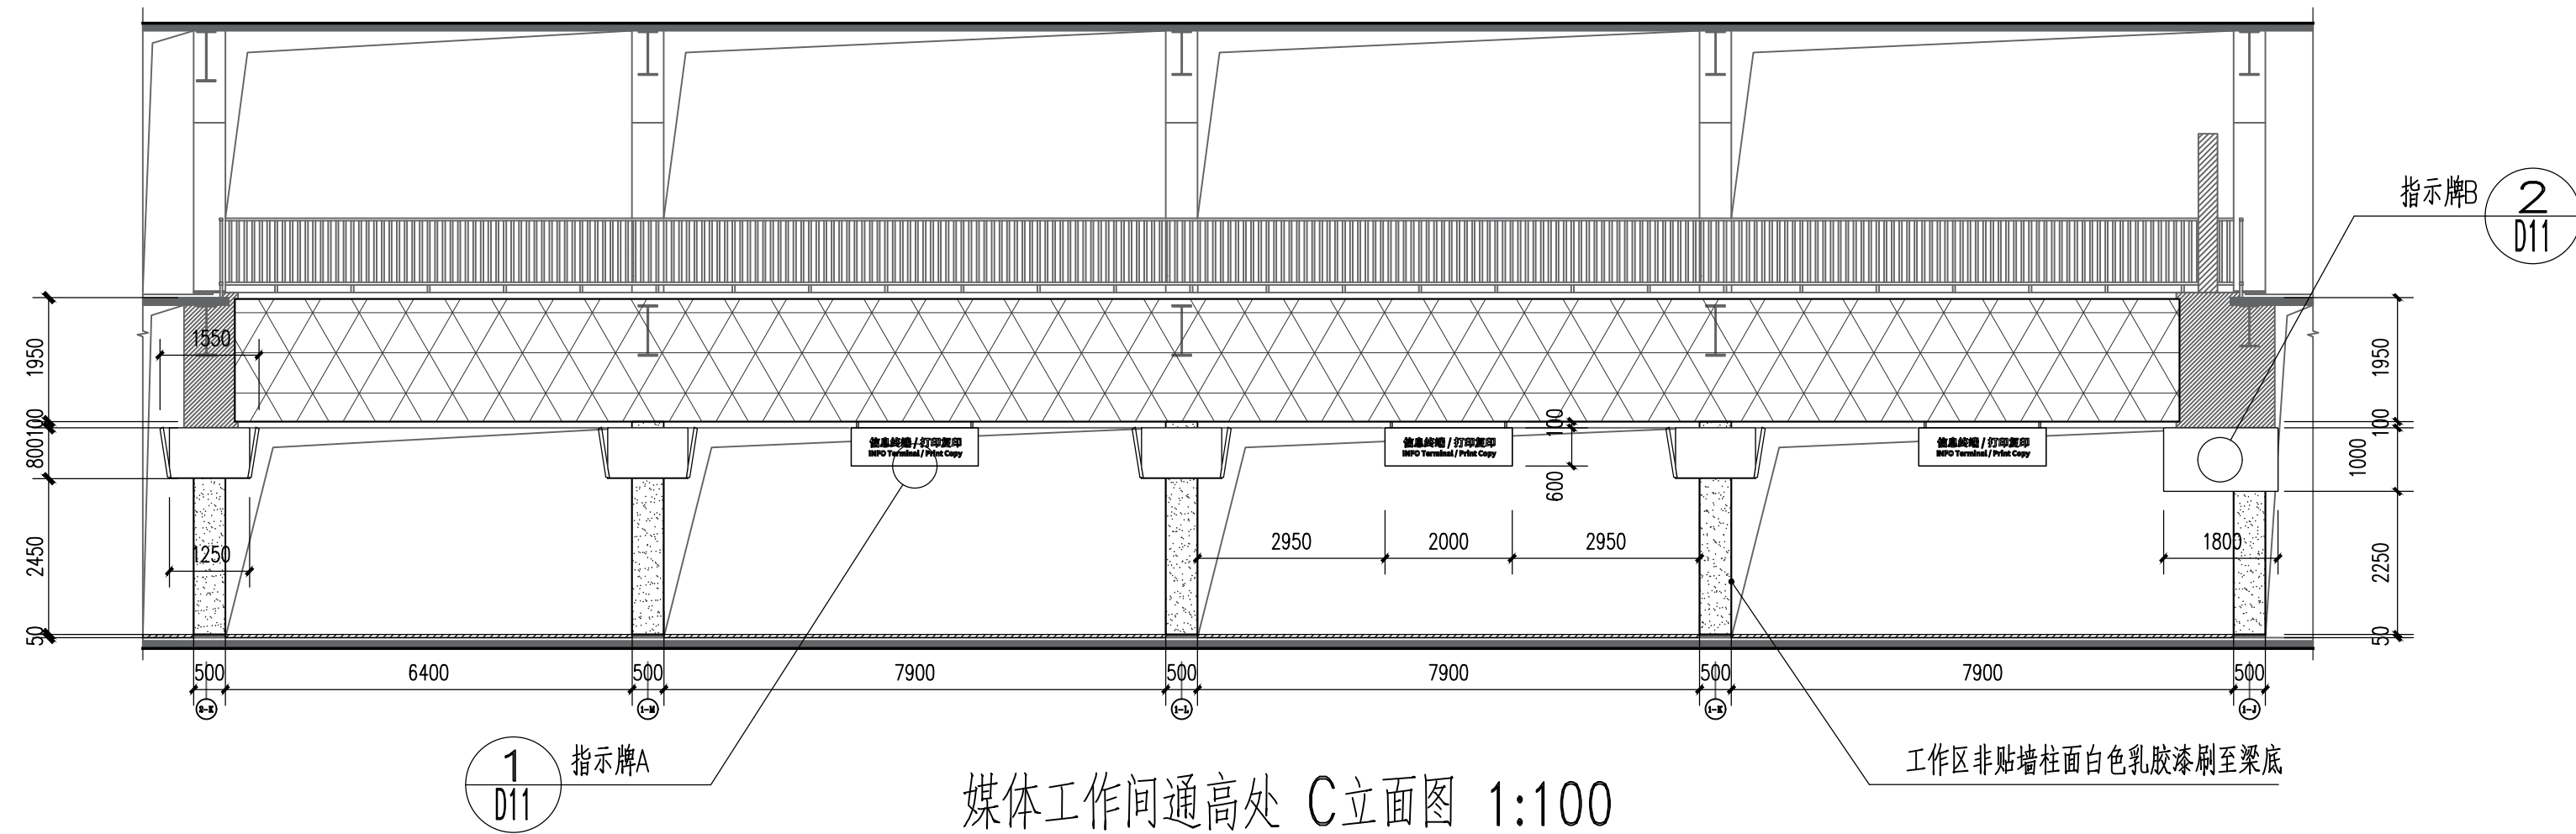

媒体工作间通高处 C 立面效果图

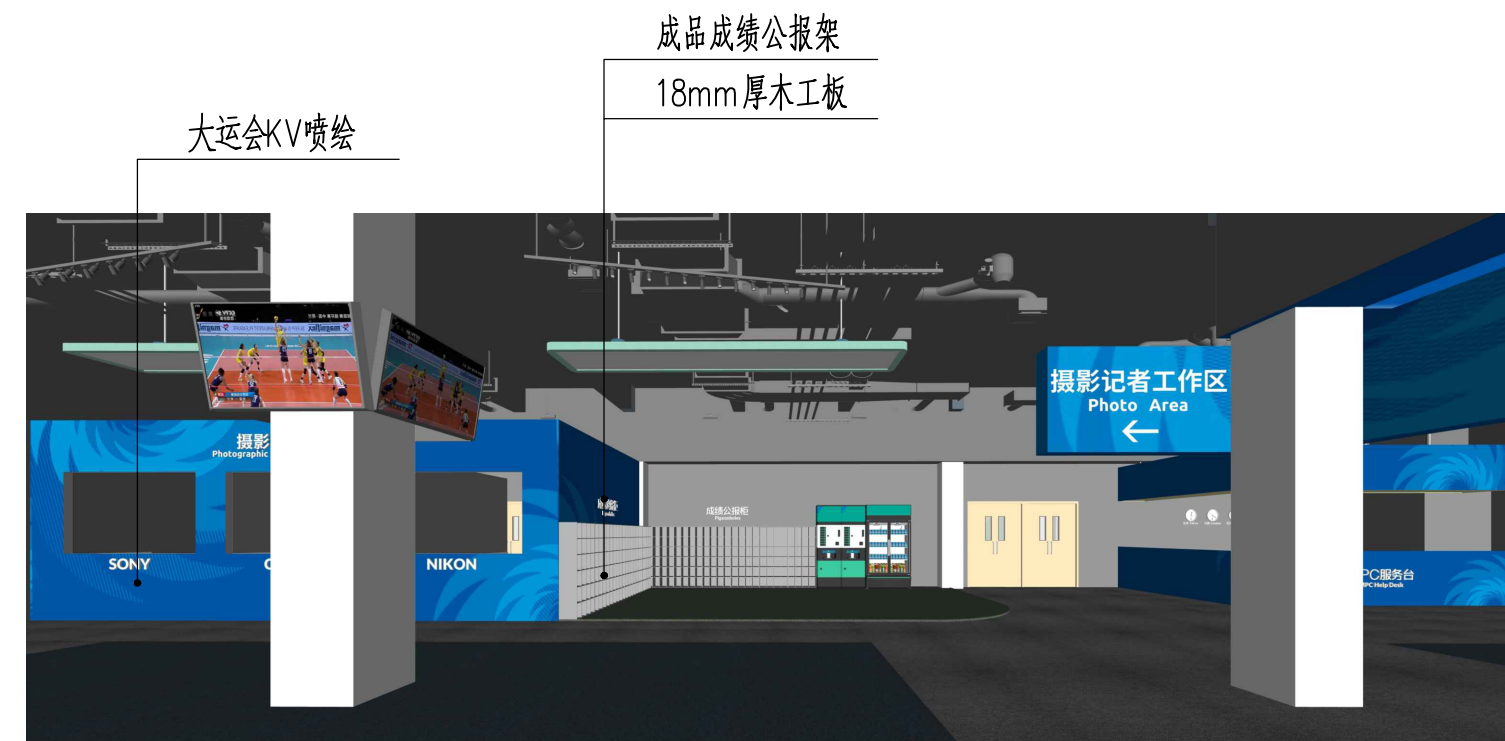


媒体工作间 D立面效果图

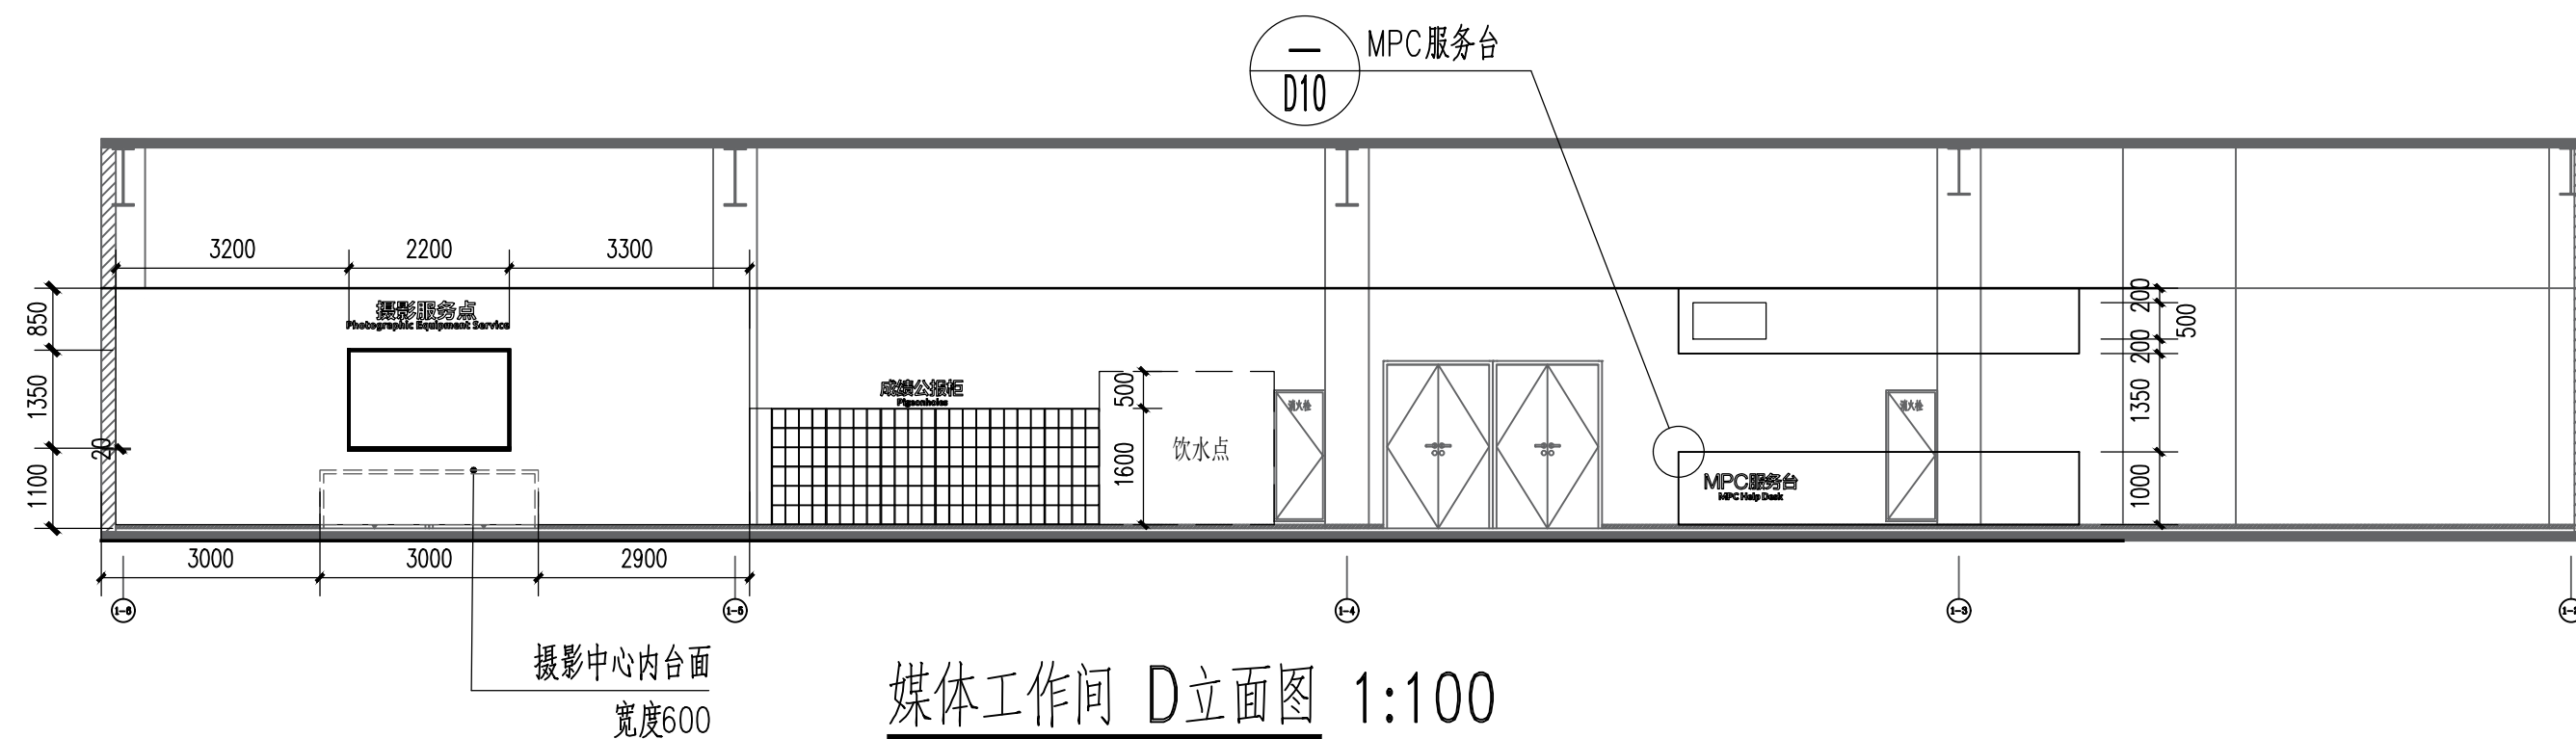


媒体工作间 D立面图 1:100


[illegible]

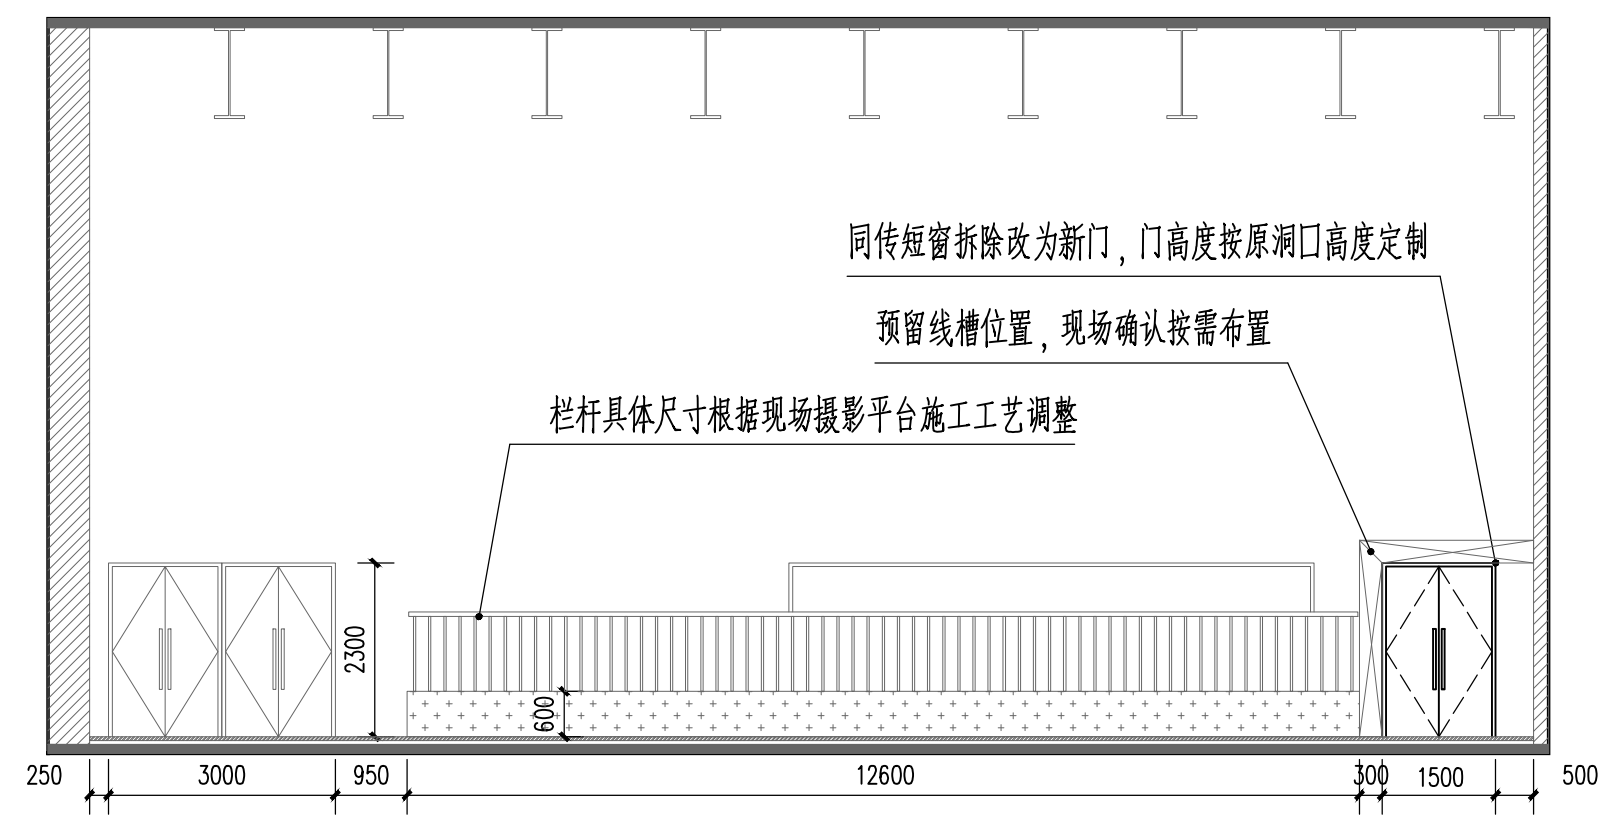




发布厅1 A立面图 1:100

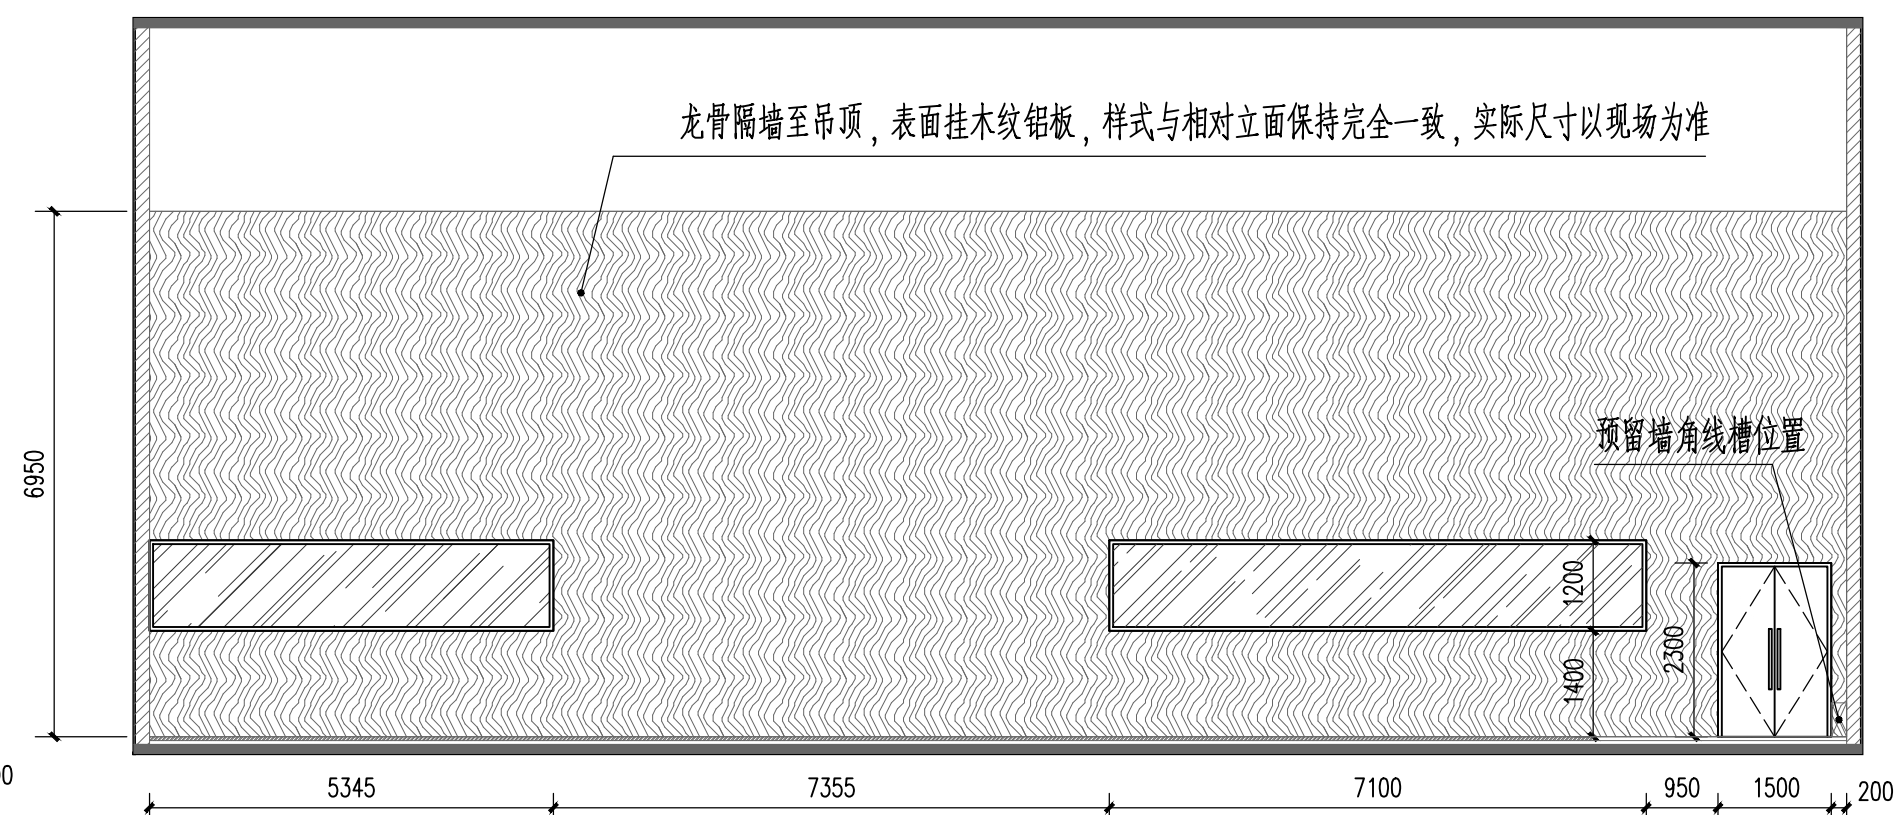

发布厅1 B立面图 1:100

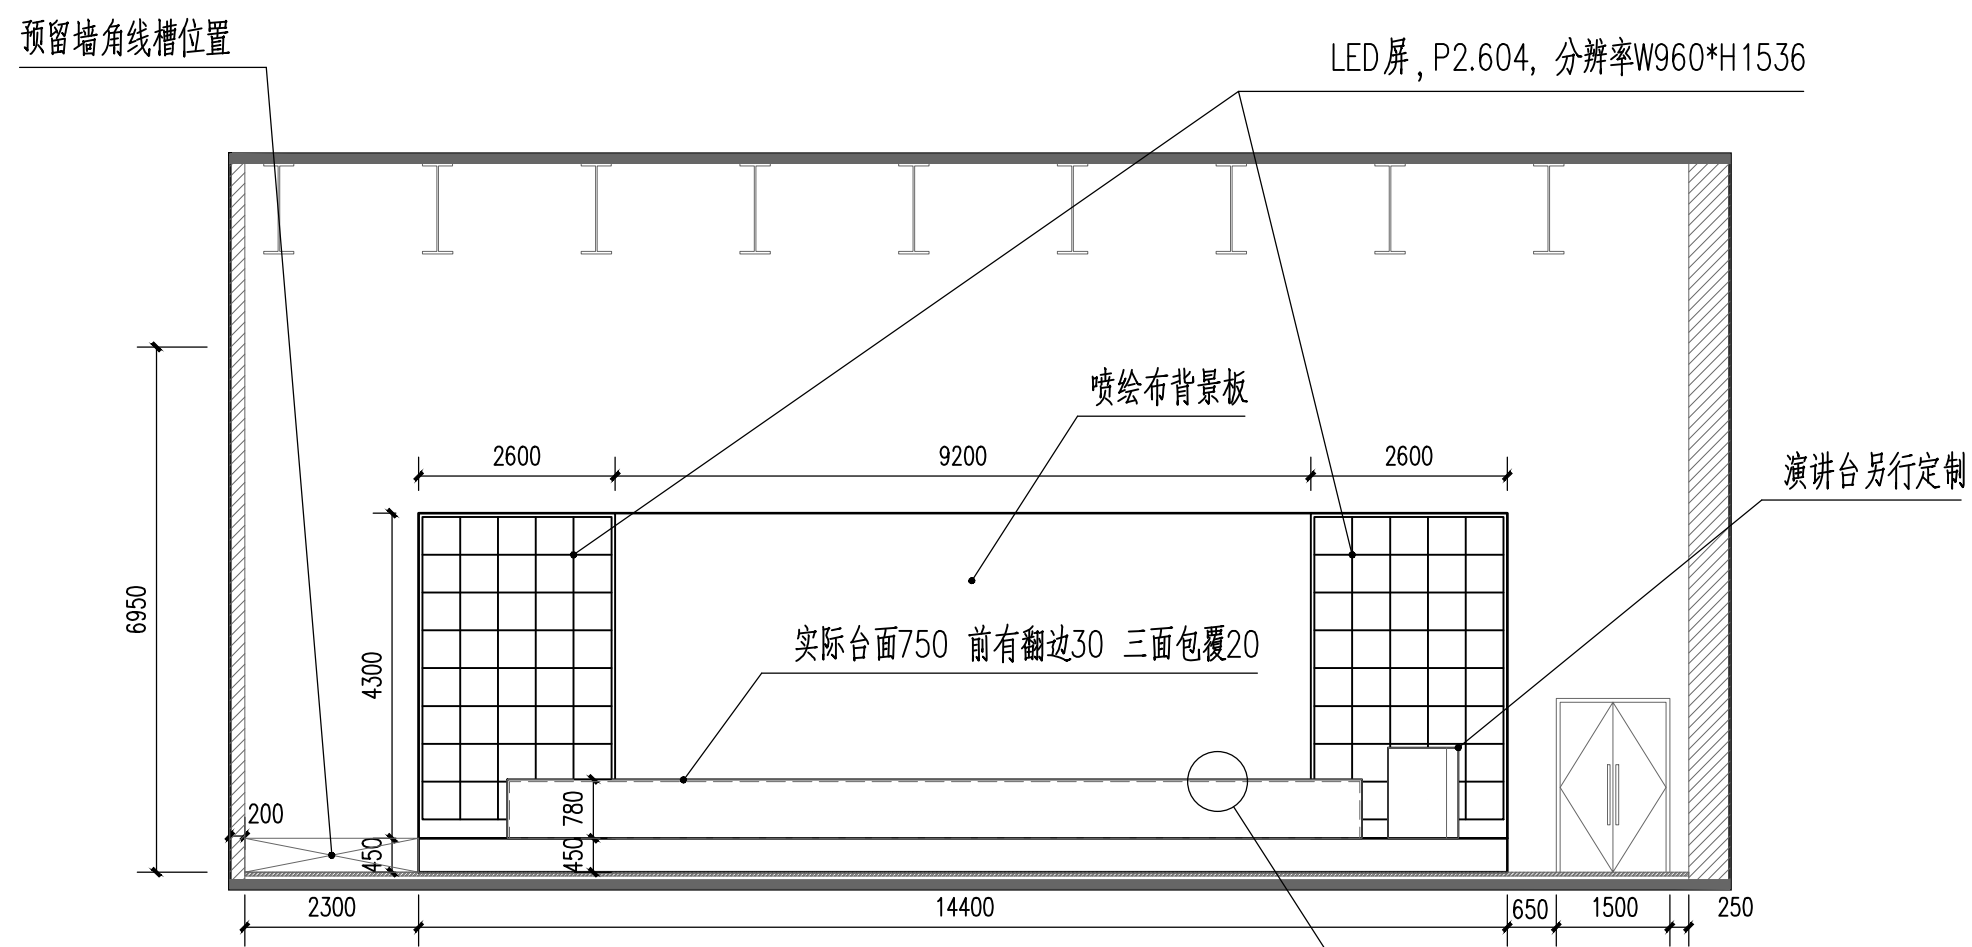


发布厅1 C立面图 1:100

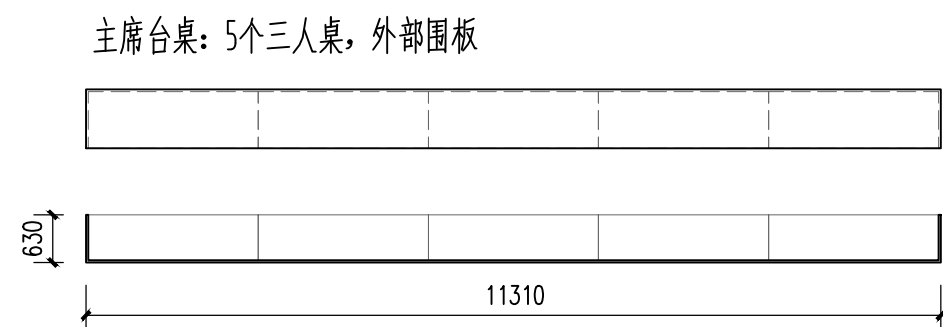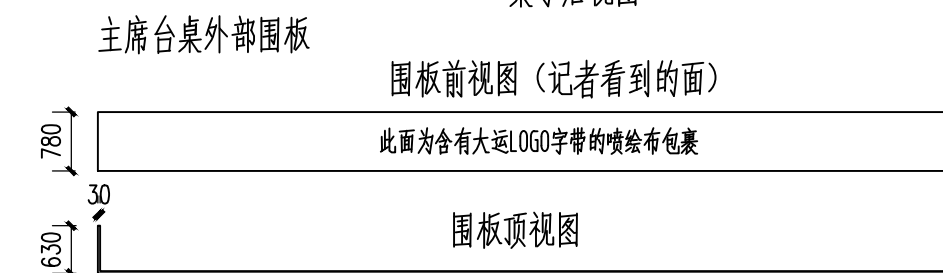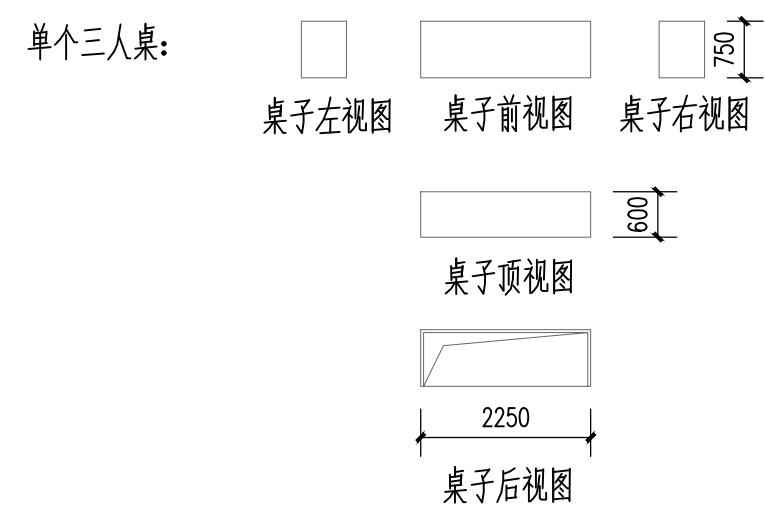


① 发布厅1主席台桌子详图 1:100


出图记录						ISSUE NOTES	
版 本 REV.		日 期 DATE		备 注 REMARK			
A		2022.02					
注册执业栏						REGISTERED ARCHITECT/ENGINEER	
姓 名						NAME	
注册证书号码						REGISTRATION CERTIFICATE NO.	
注册印章号码						STAMP NO.	
设计号：CD-20212856-F001						JOB NO.	
工程名称						PROJECT TITLE	
成都大运会主新闻中心装饰搭建							
子项名称						SUB ITEM	
建设单位						CLIENT	
成都博雅文瑞文化传播有限公司							
图 名						DRAWING TITLE	
新闻发布厅1立面图							
单 位 mm		UNIT		图 别 室施		DWG. CATEGORY	
比 例 1:100		SCALE		图 号 E03		DWG. NO.	
日 期 2022.02		DATE		版 本 A		VER. NO.	
制 图 DRAWN BY		李晚洁					
设 计 DESIGNED BY		陈星杭					
校 对 CHECKED BY		李瀛文					
专业负责人 DISCIPLINE CHIEF		肖子顺					
设计总负责人 PROJECT CHIEF		张峻					
审 核 AUDIT		张峻					
审 定 APPROVED BY		华轲					
国 基准方中 成都基准方中建筑设计股份有限公司 Chengdu JZfz Architectural Design Co., Ltd. 中国·成都市·琉璃路8号华润广场A座7-15楼 电话：+86(28) 86333800 传真：+86(28) 86582990 7-15F, Tower A, Crystal Plaza, No.8,Liuli Road , Chengdu, P.R.C tel. +86(28) 86333800 fax. +86(28) 86582990 工程设计资质证书编号：A151016191 电子文档编号：- CAD FILENAME 版 权 说 明 COPYRIGHT DECLARATION 此图版权为成都基准方中建筑设计股份有限公司所有，未经许可不得使用。							

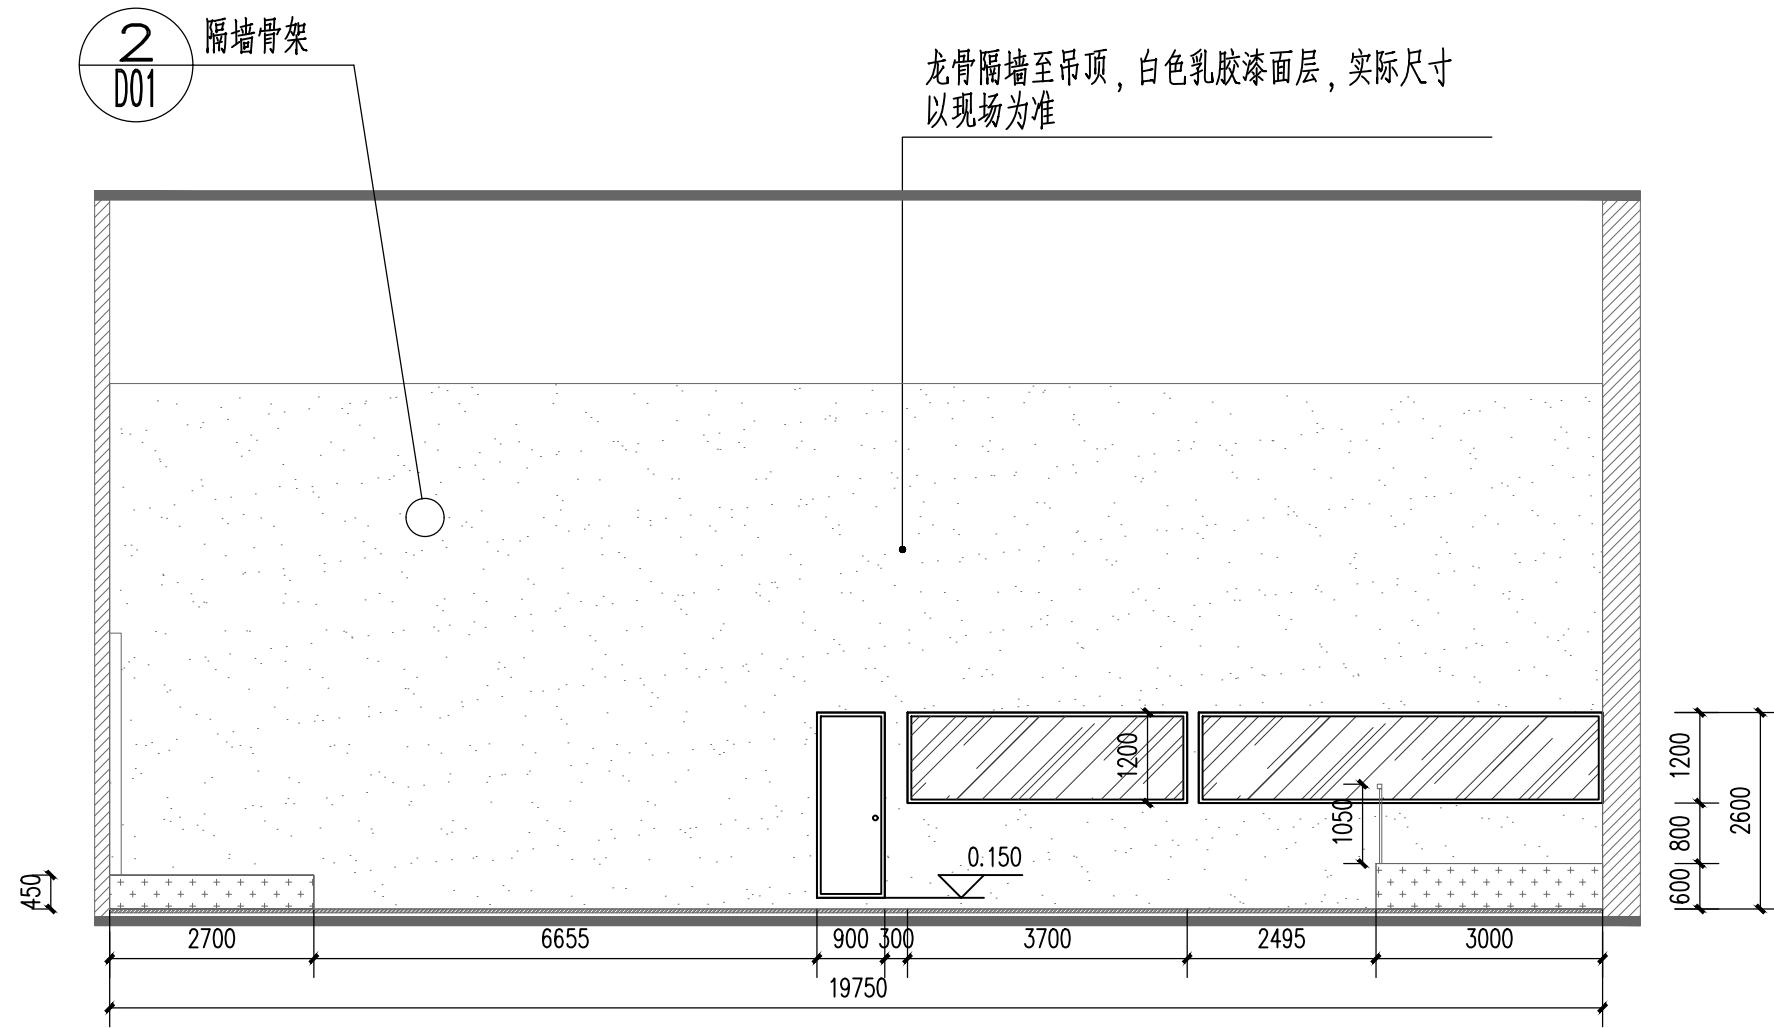

发布厅2 A立面图 1:100

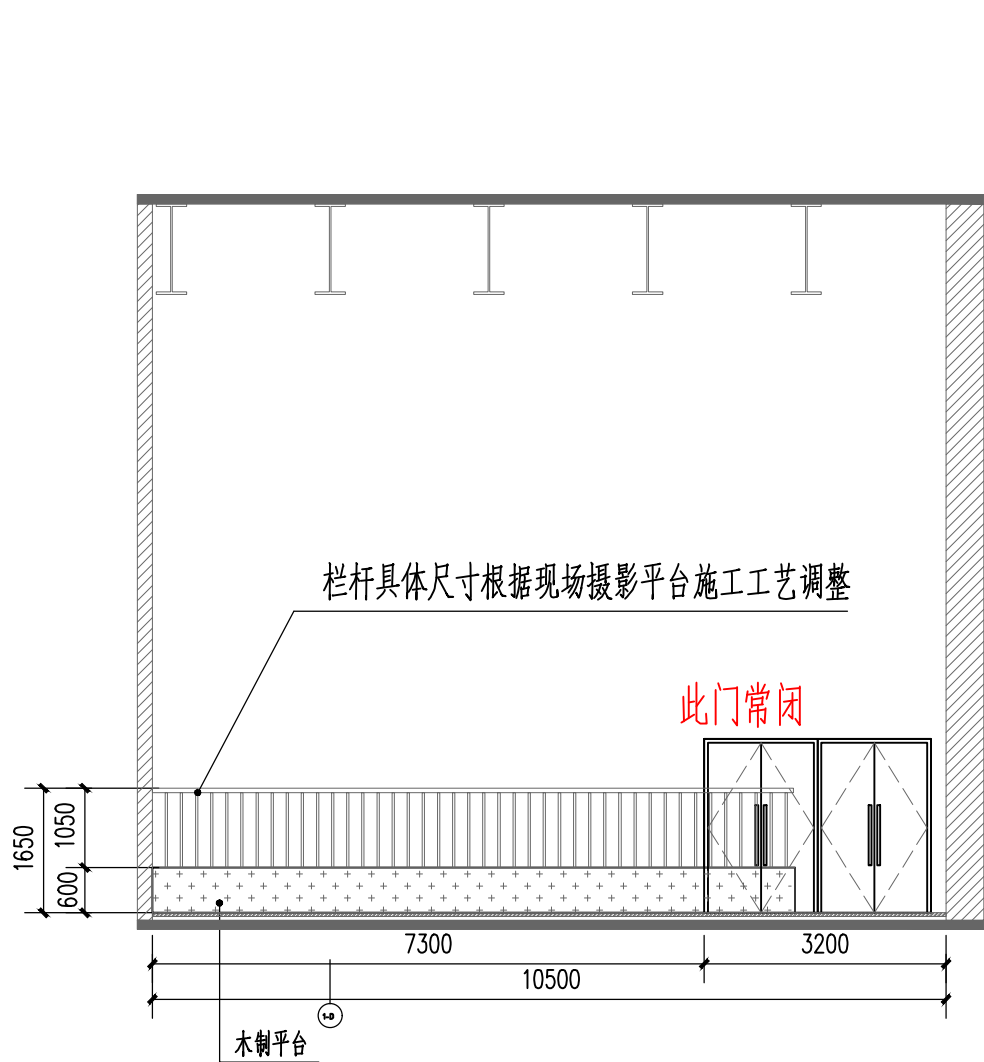


发布厅2 B立面图 1:100

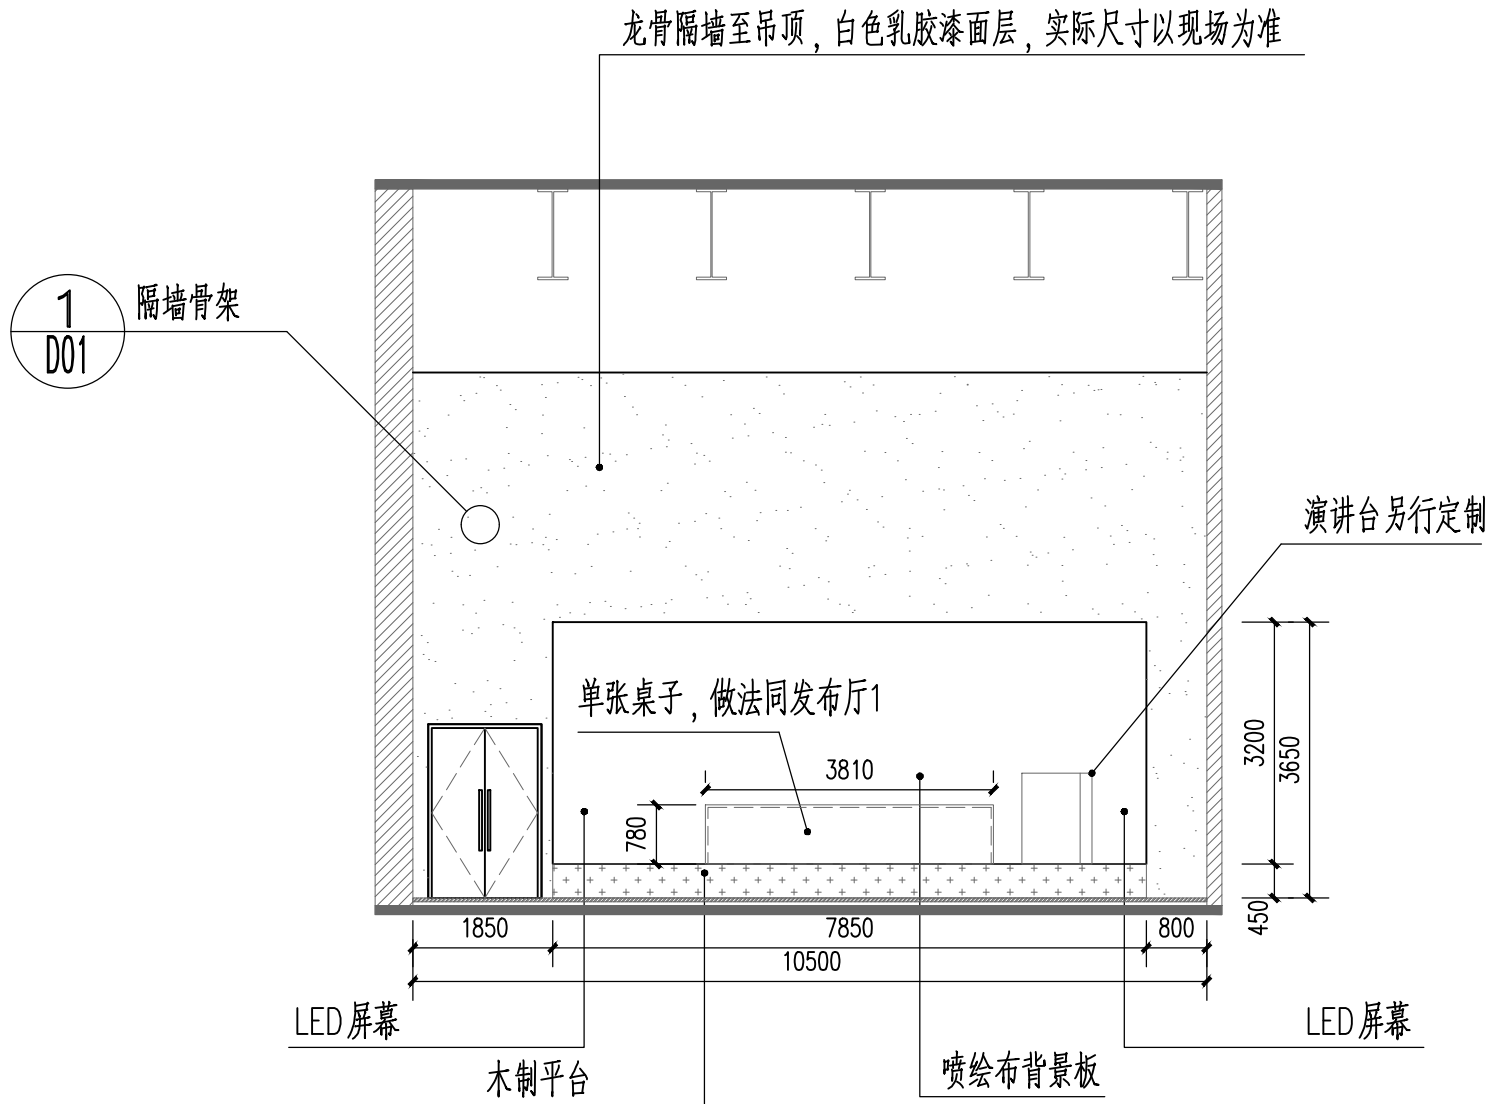

发布厅2 C立面图 1:100

出图记录		ISSUE NOTES
版 本	日 期	备 注
REV.	DATE	REMARK
A	2022.02	
注册执业栏		REGISTERED ARCHITECT/ENGINEER
姓 名		NAME
注册证书号码		REGISTRATION CERTIFICATE NO.
注册印章号码		STAMP NO.
设计号: CD-20212856-F001		JOB NO.
工程名称		PROJECT TITLE
成都大运会主新闻中心装饰搭建		
子项名称		SUB ITEM
建设单位		CLIENT
成都博雅文瑞文化传播有限公司		
图 名		DRAWING TITLE
新闻发布厅2 立面图		
单 位	mm	UNIT
图 别	室 施	DWG. CATEGORY
比 例	1: 100	SCALE
图 号	E04	DWG. NO.
日 期	2022.02	DATE
版 本	A	VER. NO.
制 图	张 丽	
设 计	赵佳欣	
校 对	李 璐 文	
专业负责人	肖子颖	
DISCIPLINE CHIEF		
设计总负责人	张 峻	
PROJECT CHIEF		
审 核	张 峻	
AUDIT		
审 定	华 柯	
APPROVED BY		
基准方中		
成都基准方中建筑设计股份有限公司		
Chengdu JZFZ Architectural Design Co., Ltd.		
中国 成都市 琉璃路8号华润广场A座7-15楼		
电话: +86 (28) 86333800 传真: +86 (28) 86582990		
7-15F, Tower A, Cifang Plaza, No.8, Liuli Road, Chengdu, P.R.C		
tel. +86(28) 86333800 fax. +86(28) 86582990		
工程设计资质证书编号: A151016191		
电子文档编号: -		CAD FILENAME
版 权 说 明		
COPYRIGHT DECLARATION		
此图版权为成都基准方中建筑设计股份有限 公司所有, 未经许可不得使用。		


采暖通风					
总图					

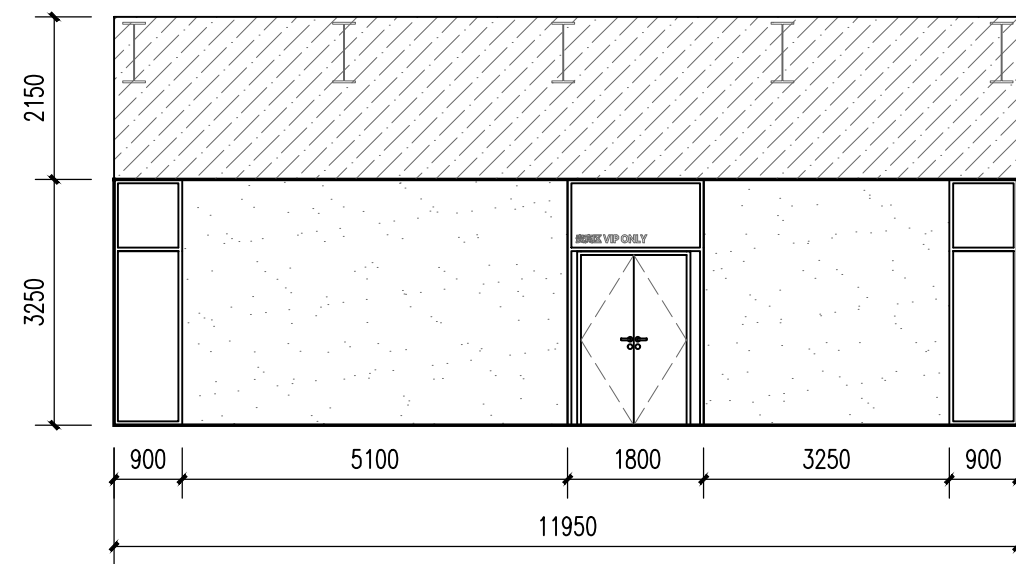

西入口区域 E立面图 1:100




西入口区域 E立面效果图

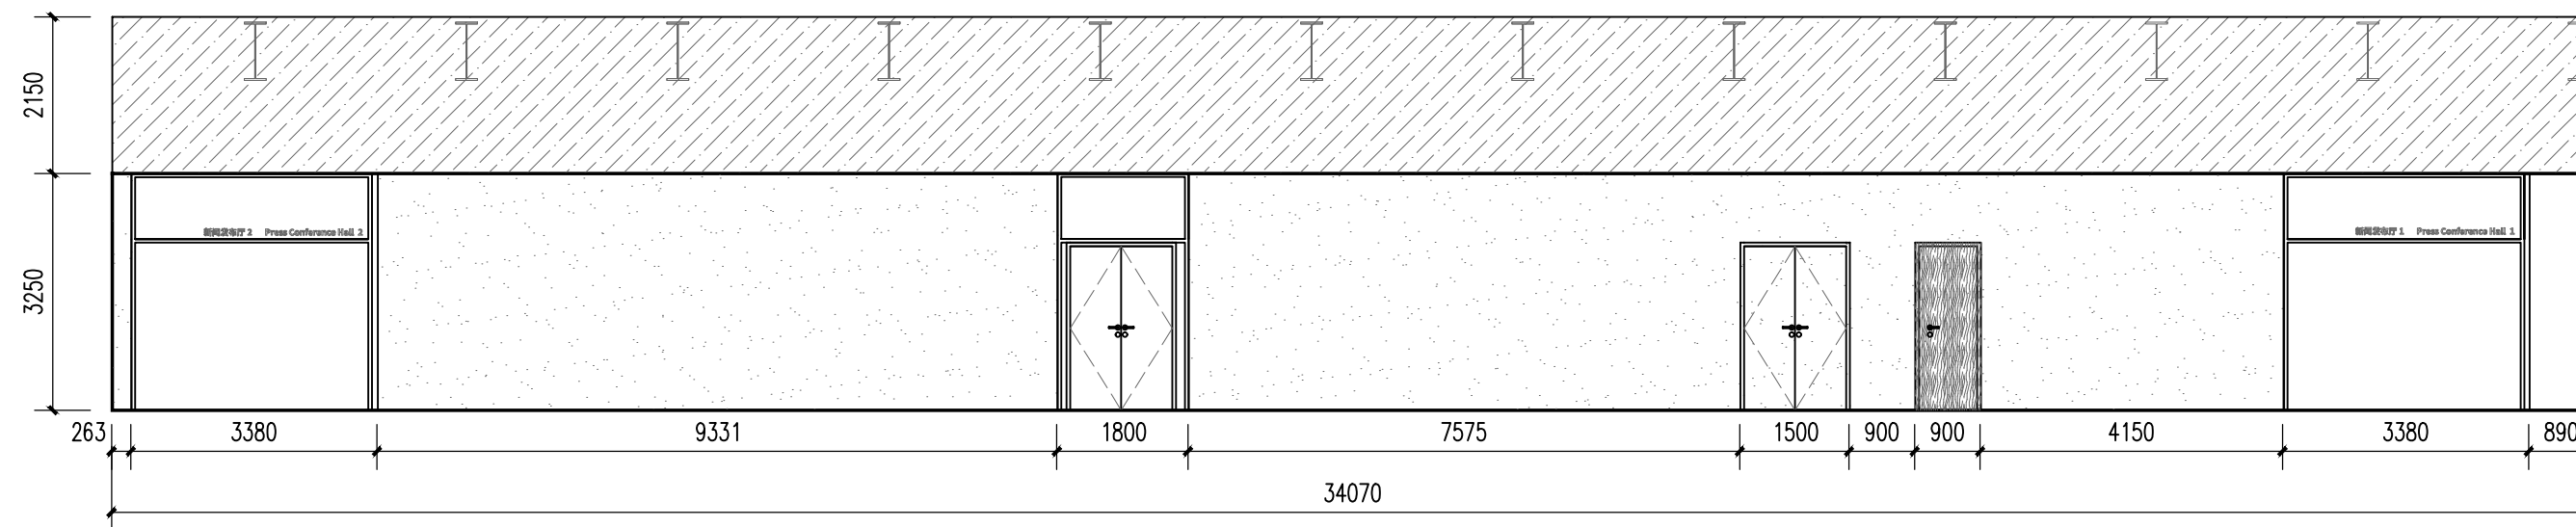


西入口区域 F立面图 1:100



西入口区域 F立面效果图

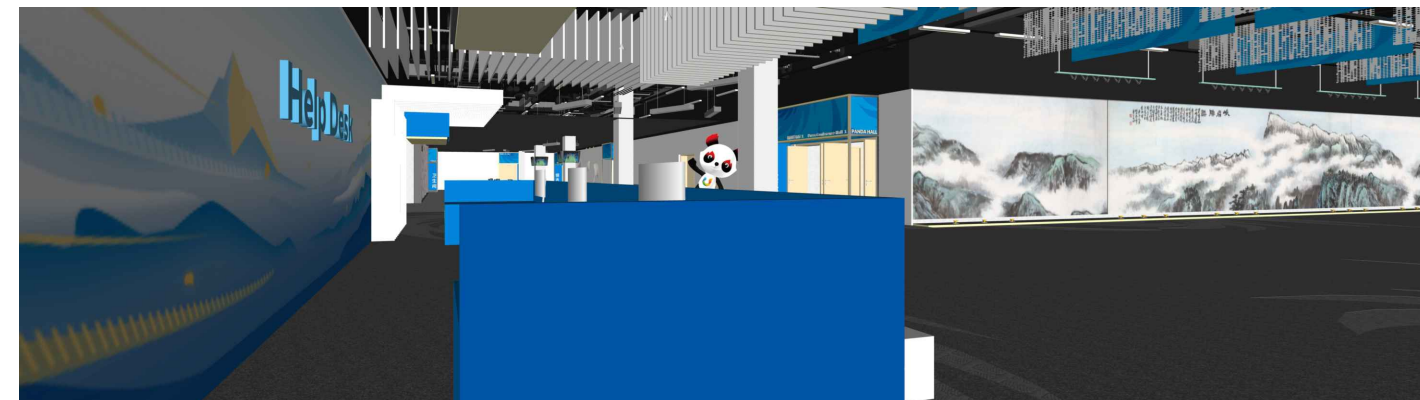


西入口区域 G立面效果图

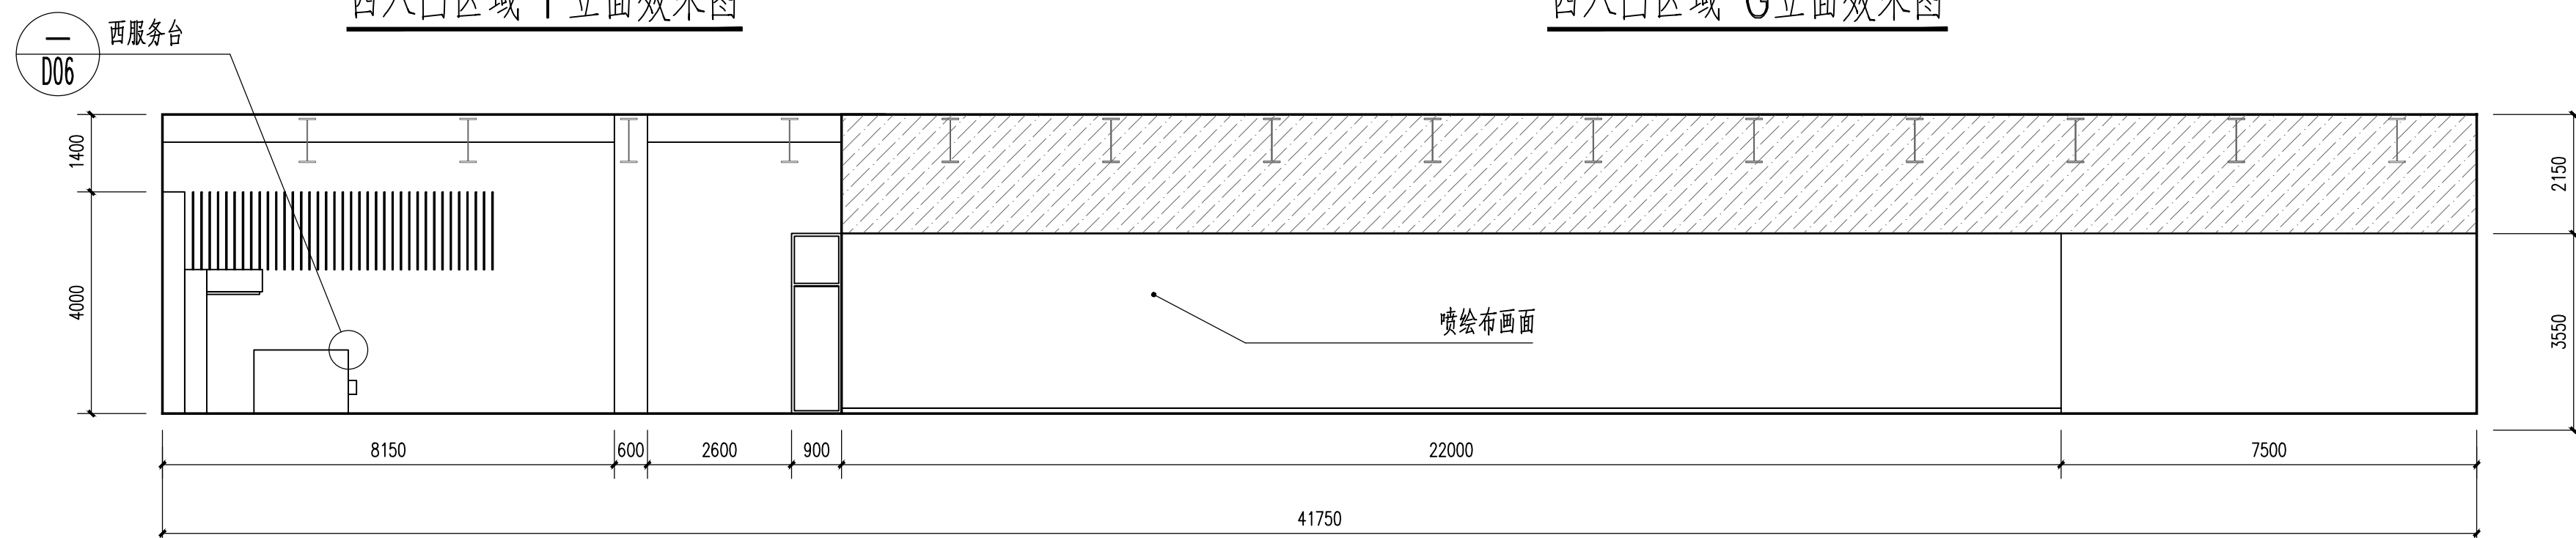

西入口区域 G立面图 1:100

出图记录						ISSUE NOTES	
版 本 REV.		日 期 DATE		备 注 REMARK			
A		2022.02					
注册执业栏						REGISTERED ARCHITECT/ENGINEER	
姓 名						NAME	
注册证书号码						REGISTRATION CERTIFICATE NO.	
注册印章号码						STAMP NO.	
设计号：CD-20212856-F001						JOB NO.	
工程名称						PROJECT TITLE	
成都大运会主新闻中心装饰搭建							
子项名称						SUB ITEM	
建设单位						CLIENT	
成都博雅文瑞文化传播有限公司							
图 名						DRAWING TITLE	
西入口区域立面图（二）							
单 位 mm		UNIT		图 號 室施		DWG. CATEGORY	
比 例 1:100		SCALE		图 号 E06		DWG. NO.	
日 期 2022.02		DATE		版 本 A		VER. NO.	
制 图 DRAWN BY		方苓					
设 计 DESIGNED BY		肖子颖					
校 对 CHECKED BY		李霜文					
专业负责人 DISCIPLINE CHIEF		肖子颖					
设计总负责人 PROJECT CHIEF		张竣					
审 核 AUDIT		张竣					
审 定 APPROVED BY		华轲					
园 基准方中 成都基准方中建筑设计股份有限公司 Chengdu JZJZ Architectural Design Co., Ltd. 中国·成都市·琉璃路9号华润广场A座7-15楼 电话：+86(28) 86333800 传真：+86(28) 86582990 7-15F, Tower A, Orland Plaza, No.8,JinLi Road , Chengdu, P.R.C tel. +86(28) 86333800 fax. +86(28) 86582990 工程设计资质证书编号： A151016191 电子文档编号： - CAD FILENAME 版 权 说 明 COPYRIGHT DECLARATION 此图版权为成都基准方中建筑设计股份有限公司所有，未经许可不得使用。							

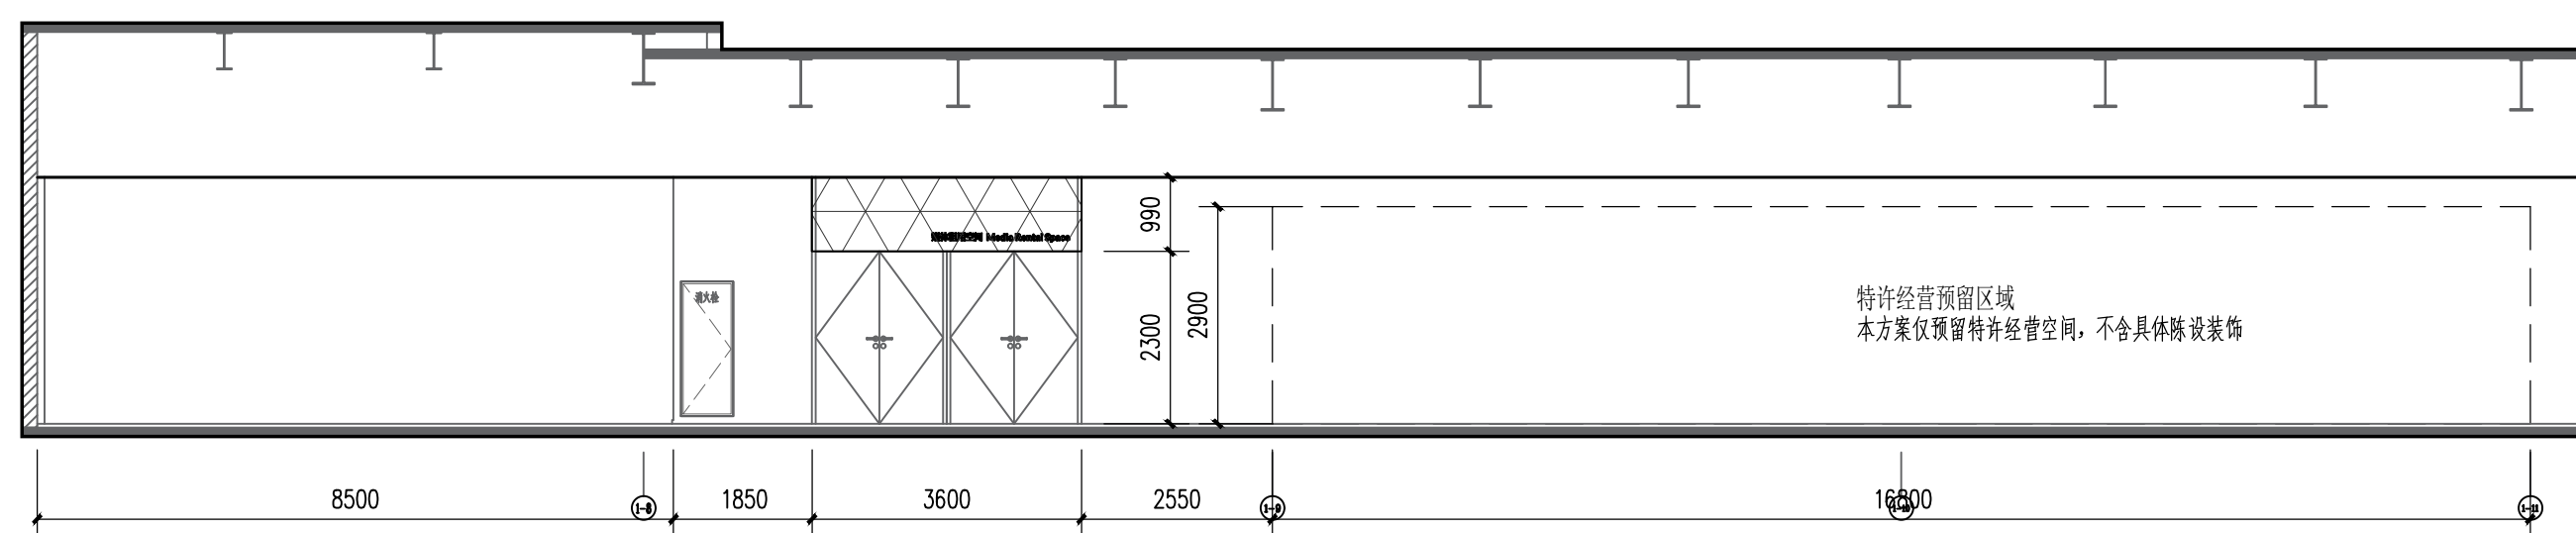


综合服务区 A立面图 1:100




特许经营区域示意

本方案仅预留特许经营空间，不含具体陈设装饰，此图仅为示意

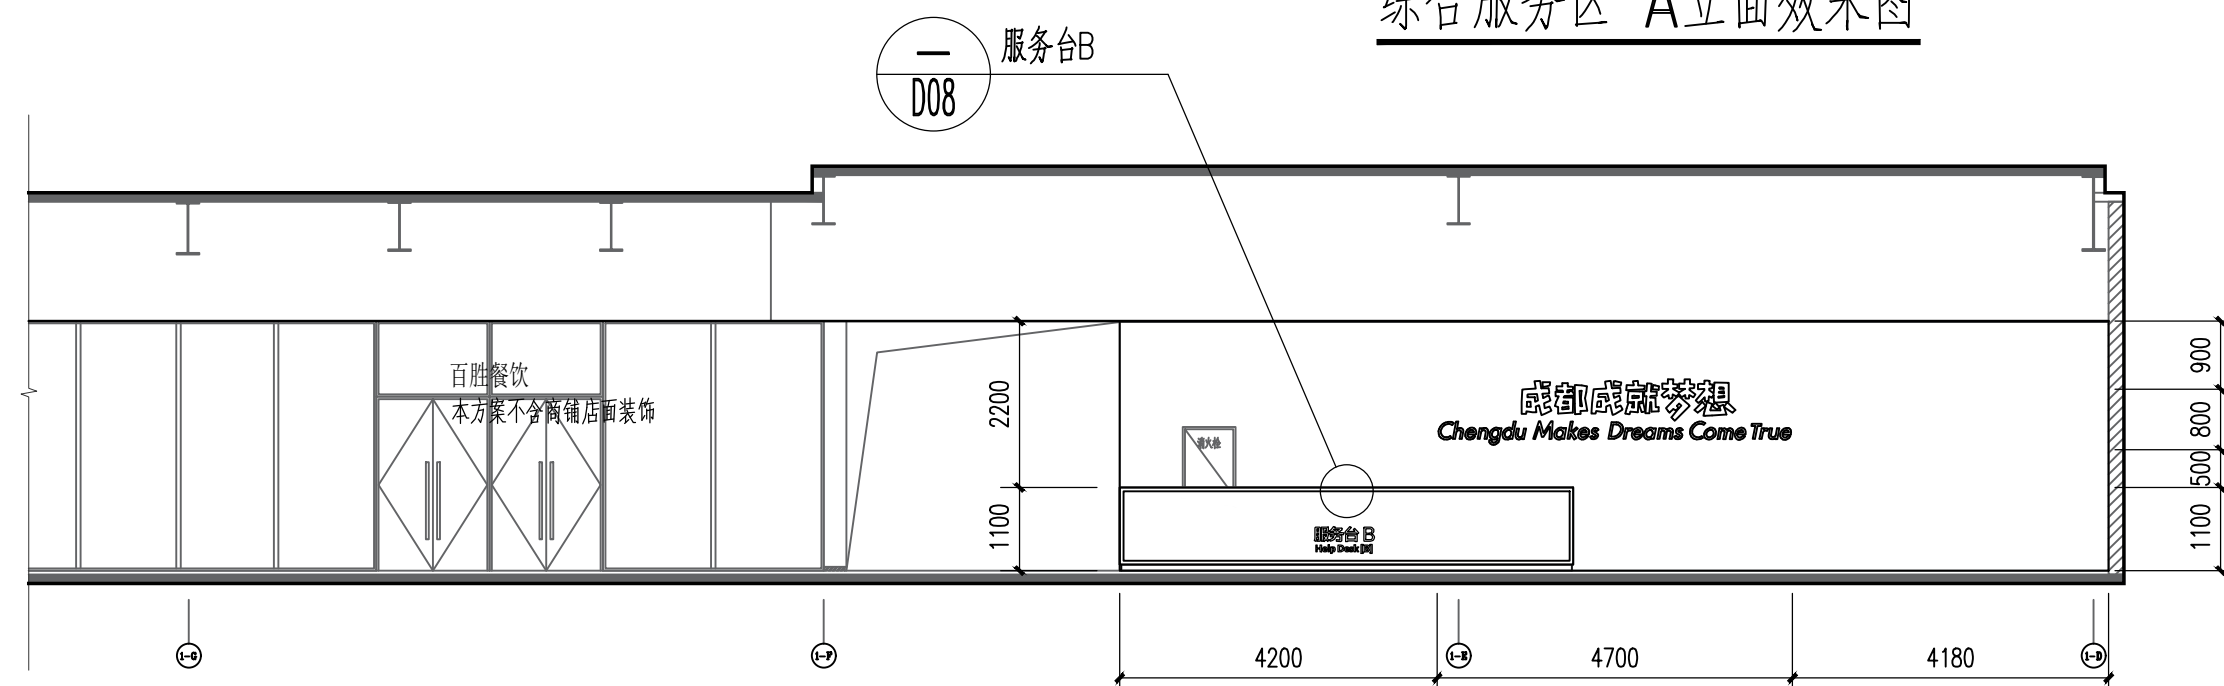


综合服务区 B立面图 1:100

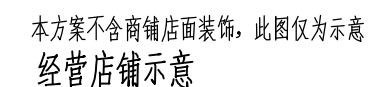


综合服务区 B立面效果图

大运会标语雕刻字

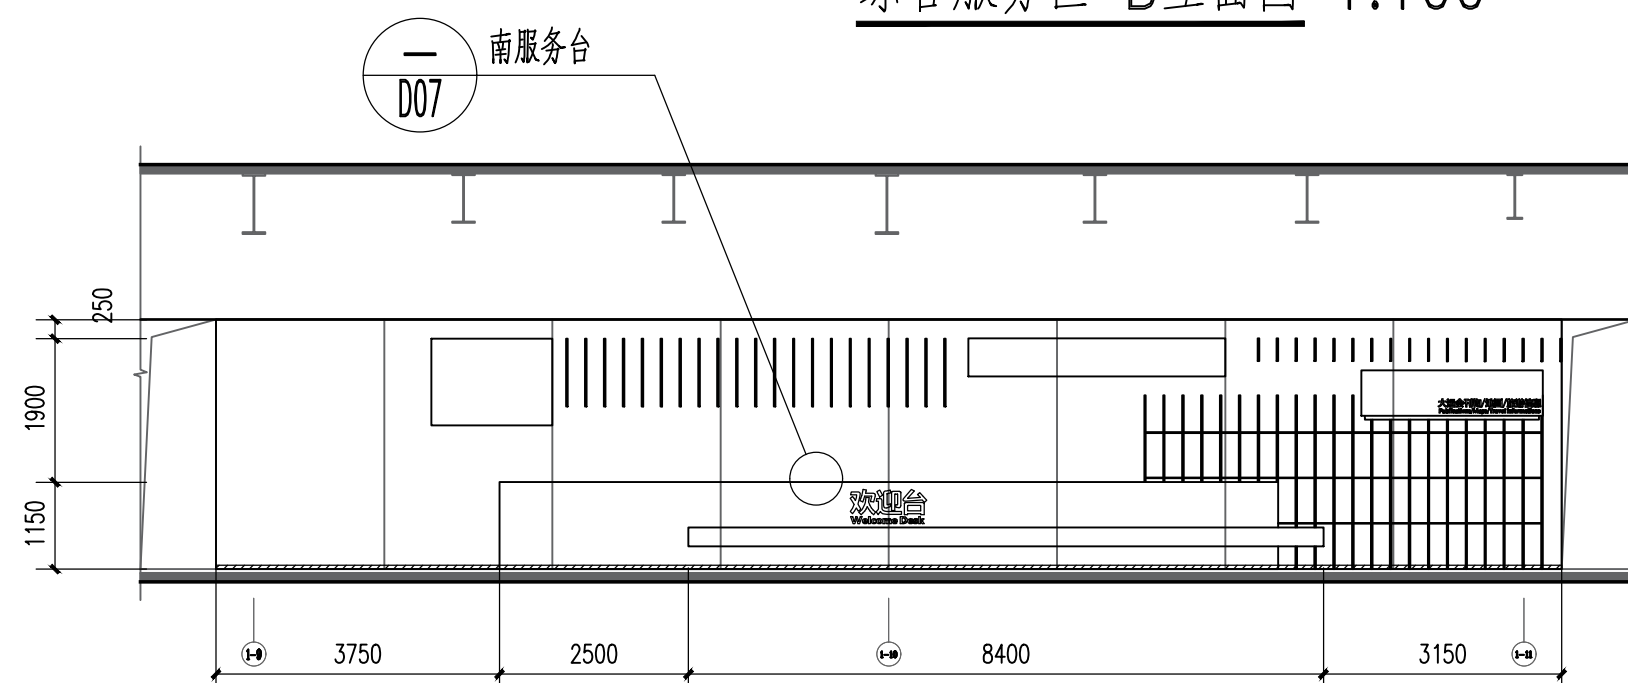


综合服务区 C立面图 1:100

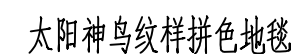

综合服务区 C立面效果图

[illegible]

采暖通风					
总图					

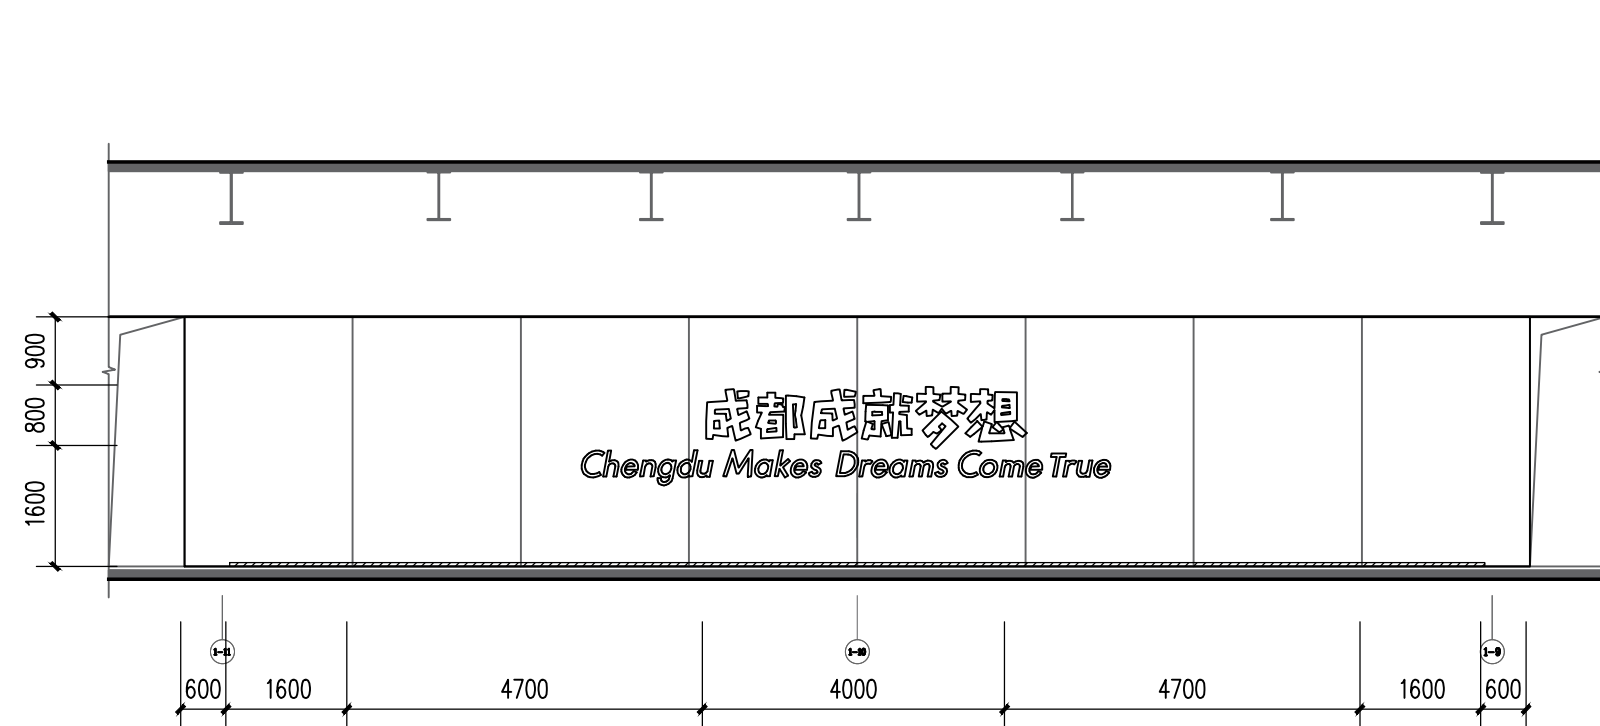


综合服务区 D立面图 1:100



综合服务区 D立面效果图



综合服务区 E立面效果图

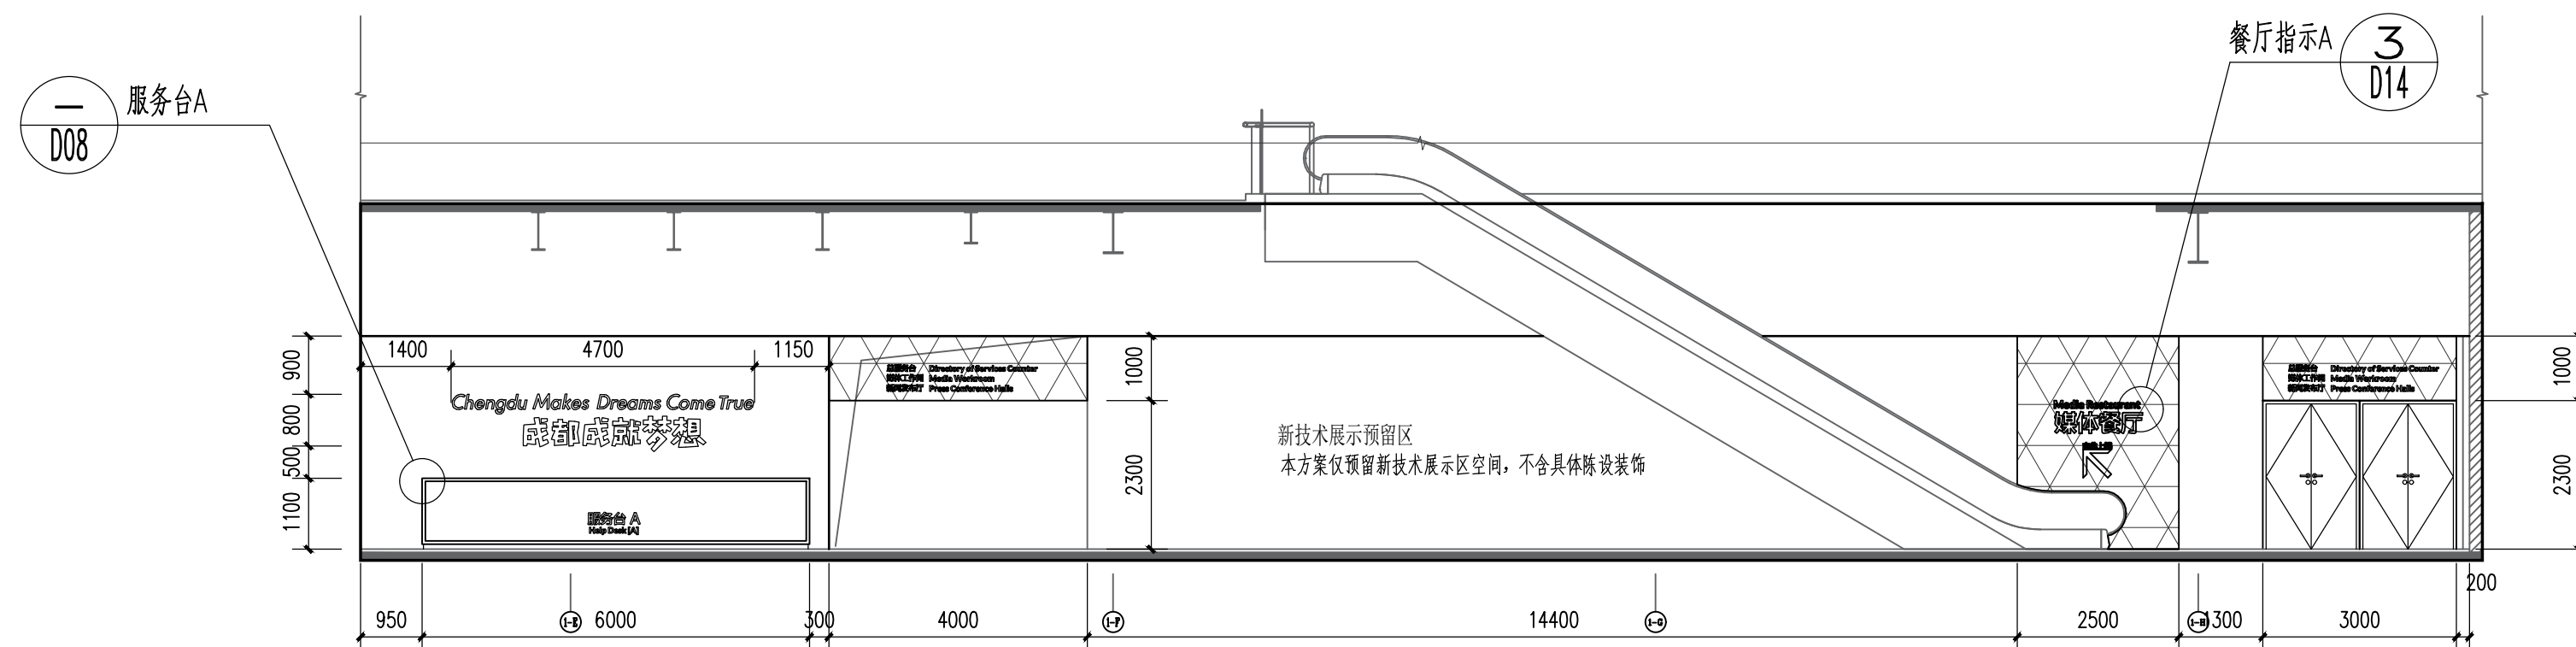


综合服务区 E立面图 1:100


出图记录			ISSUE NOTES		
版 本 REV.	日 期 DATE	备 注 REMARK			
A	2022.02				
注册执业栏					
REGISTERED ARCHITECT/ENGINEER					
姓 名					NAME
注册证书号码					REGISTRATION CERTIFICATE NO.
注册印章号码					STAMP NO.
设计号: CD-20212856-F001					JOB NO.
工程名称					PROJECT TITLE
成都大运会主新闻中心装饰搭建					
子项名称					SUB ITEM
建设单位					CLIENT
成都博雅文瑞文化传播有限公司					
图 名					DRAWING TITLE
综合服务区立面图（二）					
单 位	mm	UNIT	图 号	室 施	DWG. CATEGORY
比 例	1:100	SCALE	图 号	E08	DWG. NO.
日 期	2022.02	DATE	版 本	A	VER. NO.
制 图	肖子颖				
设 计	肖子颖				
校 对	李耀文				
专业负责人	肖子颖				
设计总负责人	张峻				
审 核	张峻				
审 定	华轲				
成都基准方中建筑设计股份有限公司					
Chengdu JZJZ Architectural Design Co., Ltd.					
中国 成都市 琉璃路8号华润广场A座7-14楼					
电话: +86(28) 86333800 传真: +86(28) 86582990					
7-15F, Tower A, Criland Plaza, No.8, Liuli Road , Chengdu, P.R.C					
tel. +86(28) 86333800 fax. +86(28) 86582990					
工程设计资质证书编号: A151016191					
CAD FILENAME					
电子文档编号: -					
版 权 说 明					
COPYRIGHT DECLARATION					
此图版权为成都基准方中建筑设计股份有限公司所有, 未经许可不得使用。					





媒体餐厅 A 立面效果图

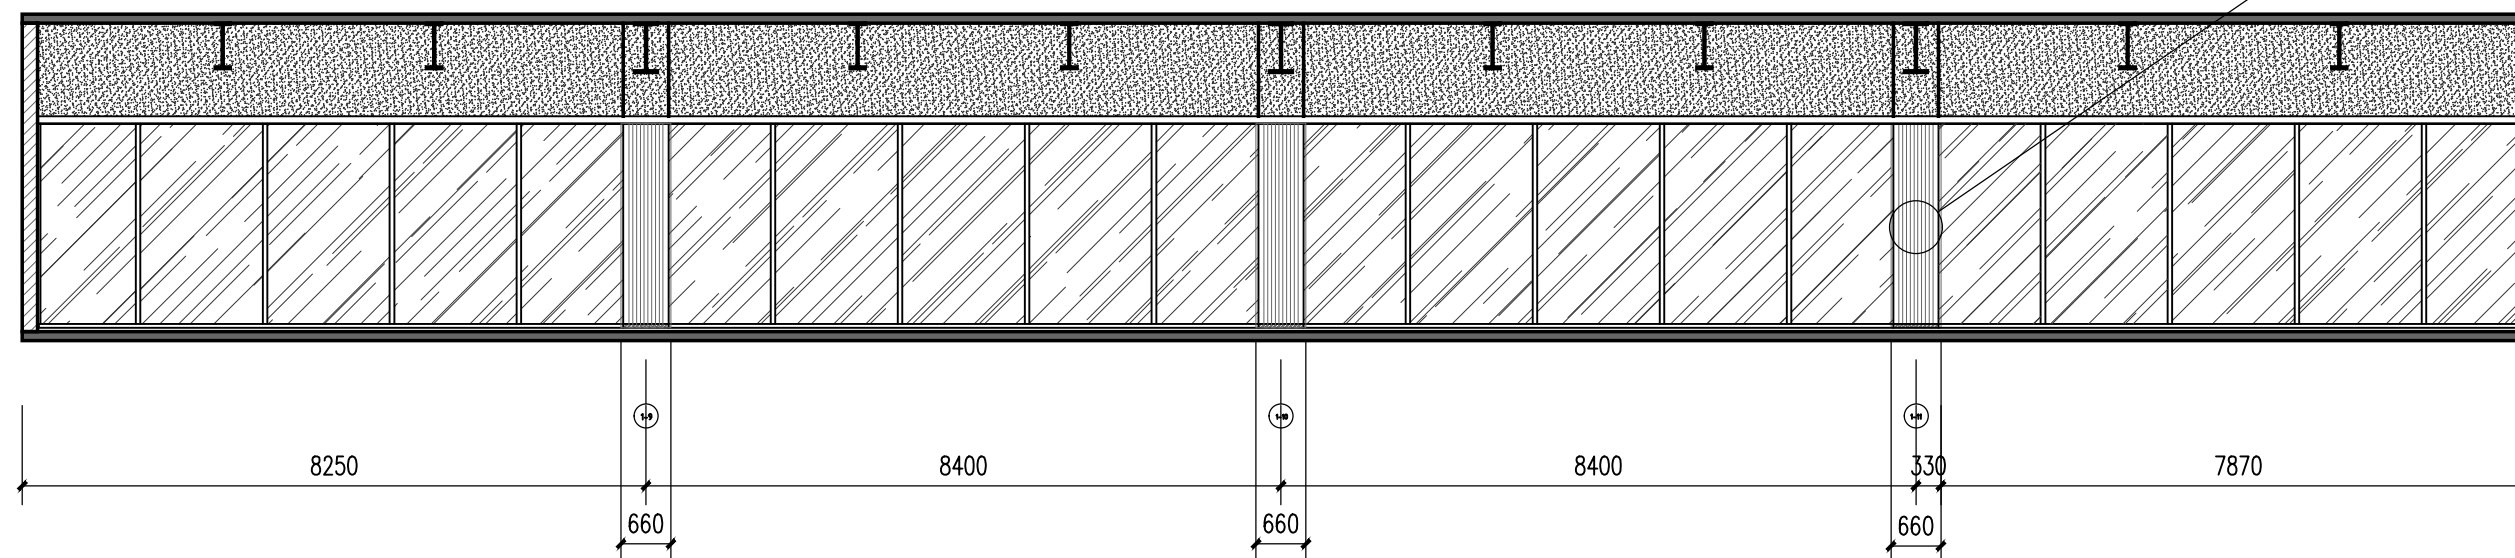



媒体餐厅 A立面图 1:100

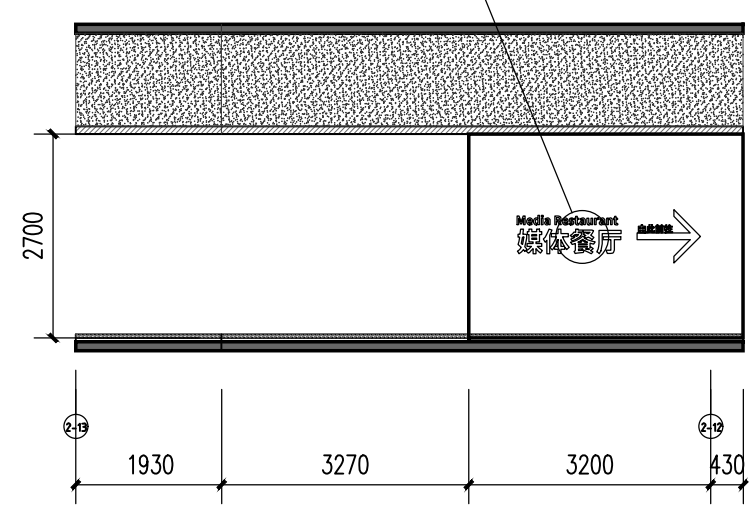



媒体餐厅 B立面图 1:100

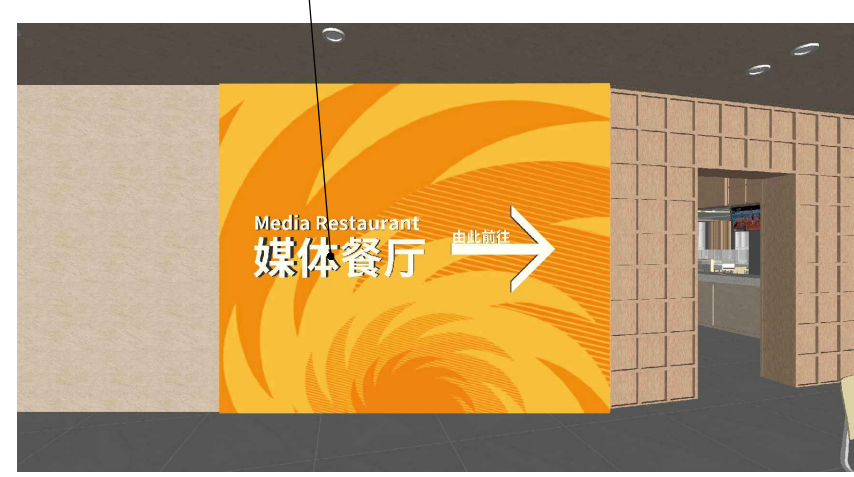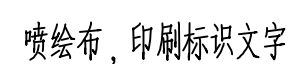


媒体餐厅 B立面效果图

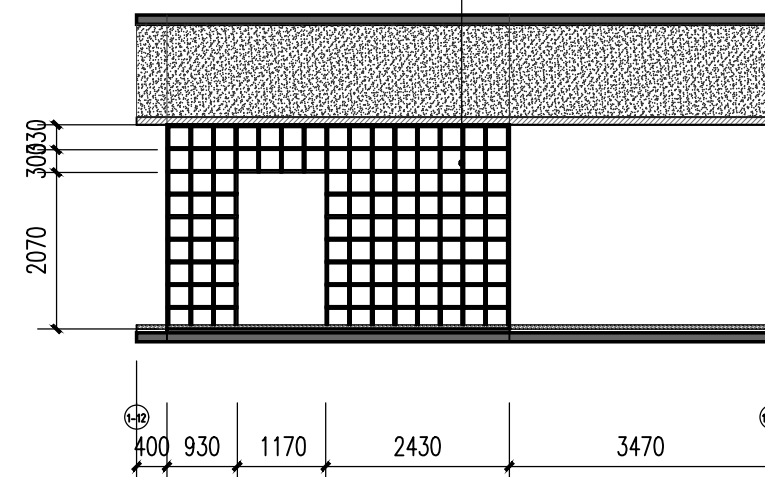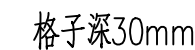


媒体餐厅 C立面图 1:100

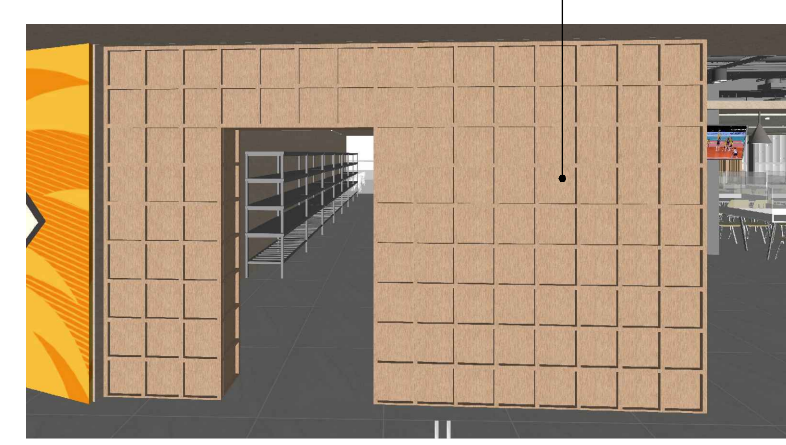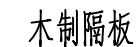

媒体餐厅 C立面效果图

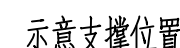

根据餐饮服务提供商窗口需求调整支撑位置与数量

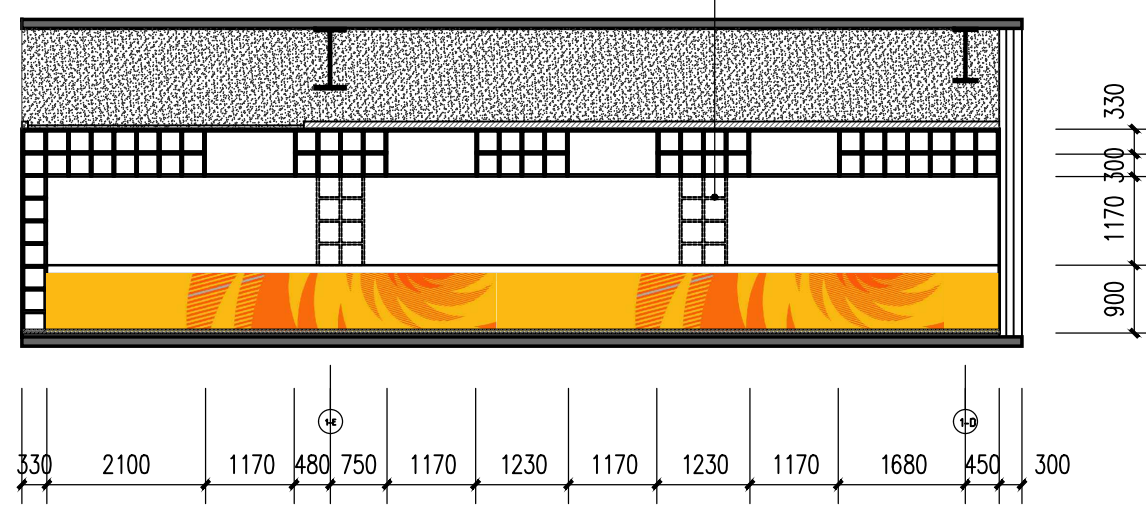


媒体餐厅 D立面图 1:100




媒体餐厅 D立面效果图

出图记录			ISSUE NOTES		
版 本 REV.	日 期 DATE	备 注 REMARK			
A	2022.02				
注册执业栏					
REGISTERED ARCHITECT/ENGINEER					
姓 名					NAME
注册证书号码					REGISTRATION CERTIFICATE NO.
注册印章号码					STAMP NO.
设计号					JOB NO.
CD-20212856-F001					
工程名称					PROJECT TITLE
成都大运会主新闻中心装饰搭建					
子项名称					SUB ITEM
建设单位					CLIENT
成都博雅文瑞文化传播有限公司					
图 名					DRAWING TITLE
媒体餐厅立面图（一）					
单 位	mm	UNIT	图 别	室 施	DWG. CATEGORY
比 例	1:100	SCALE	图 号	E09	DWG. NO.
日 期	2022.02	DATE	版 本	A	VER. NO.
制 图	雷鑫鹏				
DESIGNED BY	雷鑫鹏				
校 对	李耀文				
CHECKED BY	李耀文				
专业负责人	肖子颖				
DISCIPLINE CHIEF	肖子颖				
设计总负责人	张竣				
PROJECT CHIEF	张竣				
审 核	张竣				
AUDIT	张竣				
审 定	华轲				
APPROVED BY	华轲				
成都基准方中建筑设计股份有限公司					
Chengdu JZJZ Architectural Design Co., Ltd.					
中国·成都市·琉璃路8号华润广场A座7-15楼					
电话：+86 (28) 86333800 传真：+86 (28) 86582990					
7-15F, Tower A, Crystal Plaza, No.8Jinli Road, Chengdu, P.R.C					
tel. +86(28) 86333800 fax. +86(28) 86582990					
工程注册资质证书编号： A151016191					
电子文档编号： -					
CAD FILENAME					
版 权 说 明					
COPYRIGHT DECLARATION					
此图版权为成都基准方中建筑设计股份有限公司所有，未经许可不得使用。					

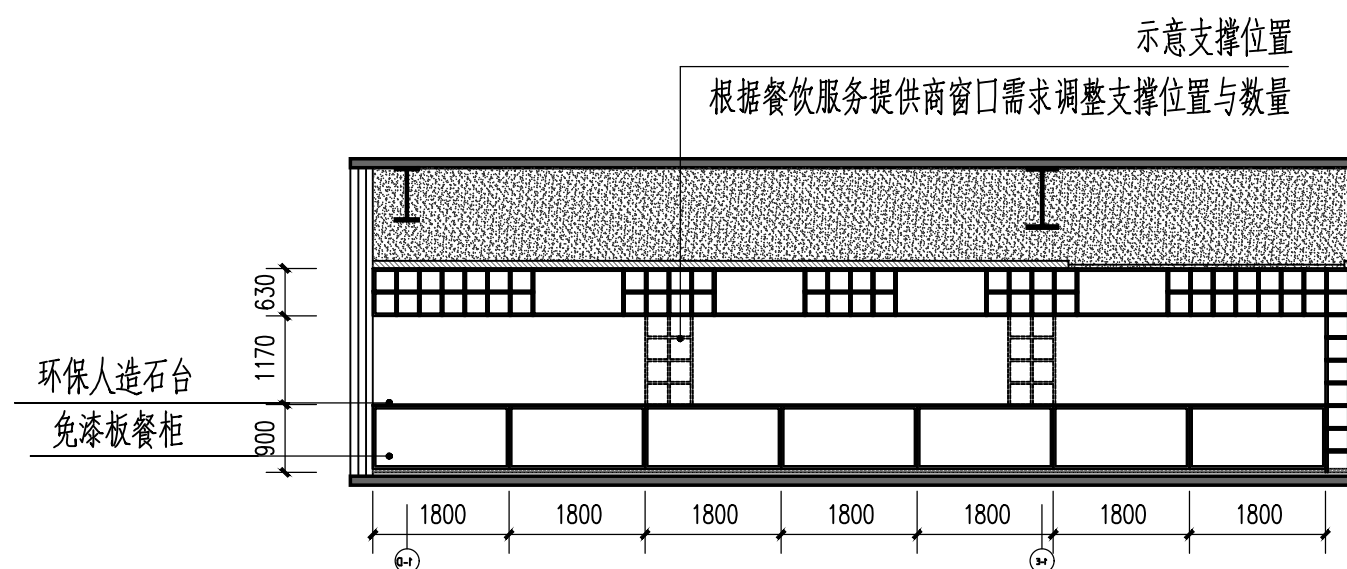

媒体餐厅 E立面图 1:100

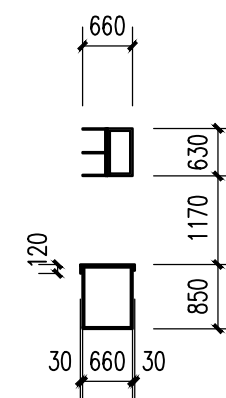


媒体餐厅取餐台剖面图 1:100




媒体餐厅 E立面效果图




媒体餐厅 F立面效果图

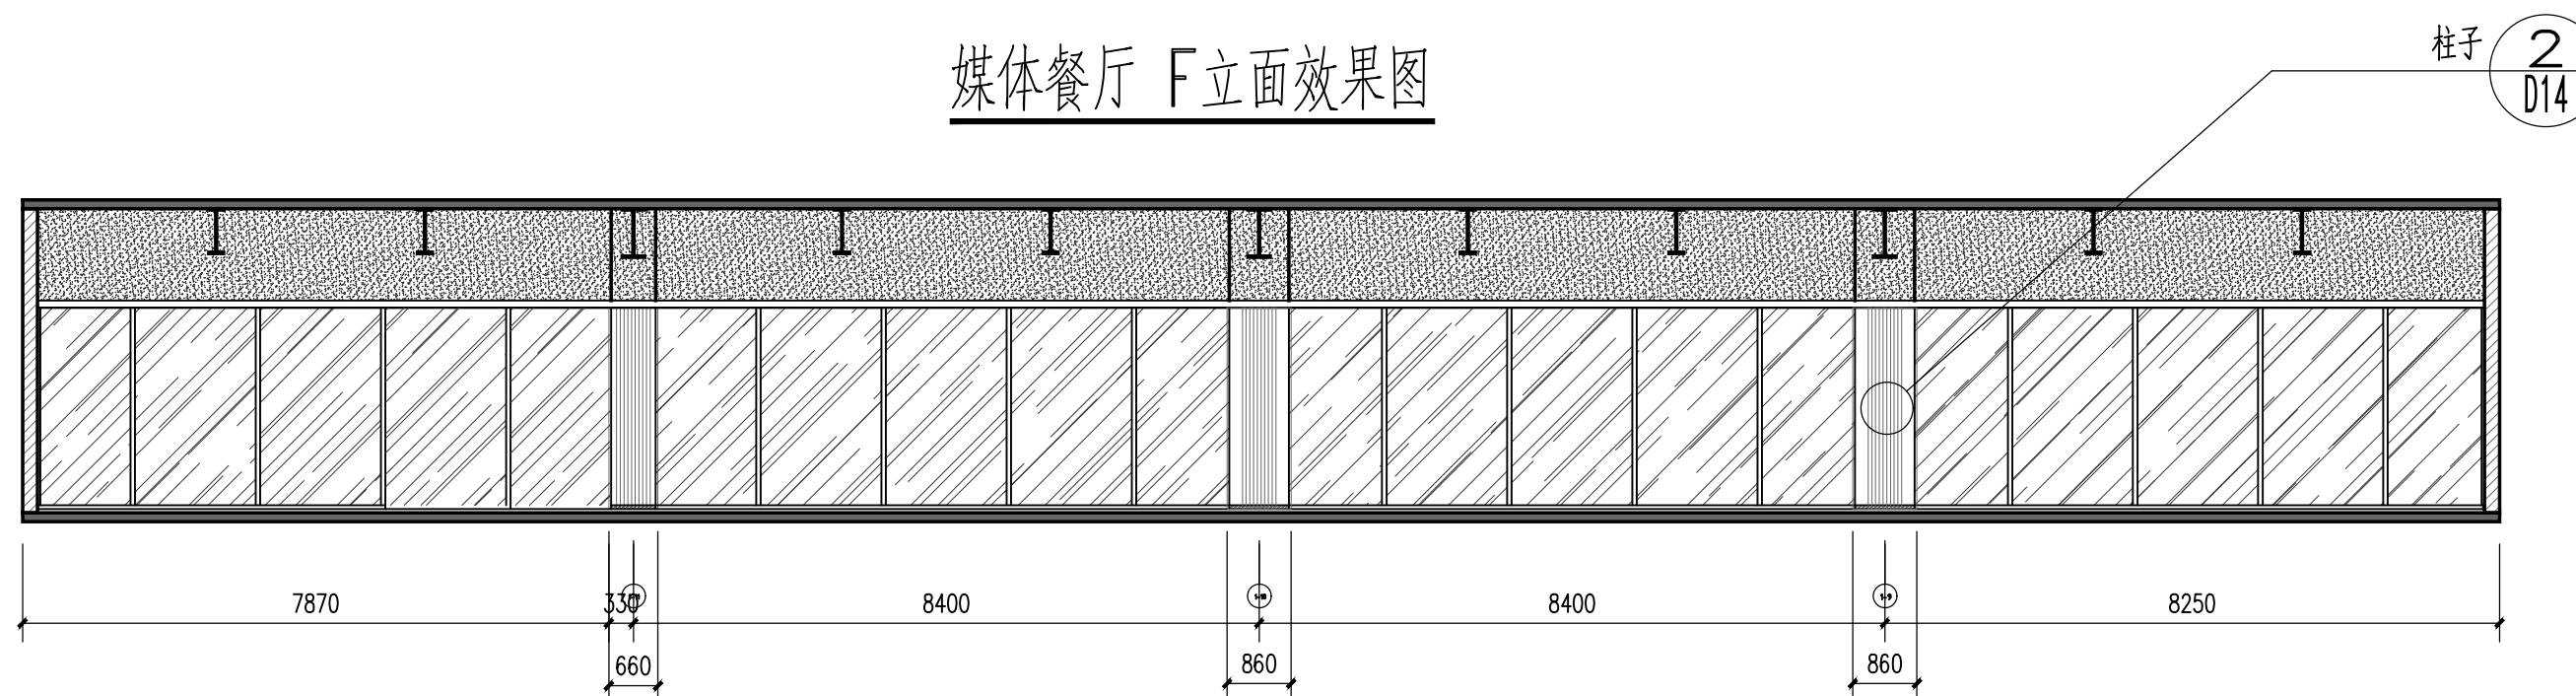

媒体餐厅 F立面图 1:100

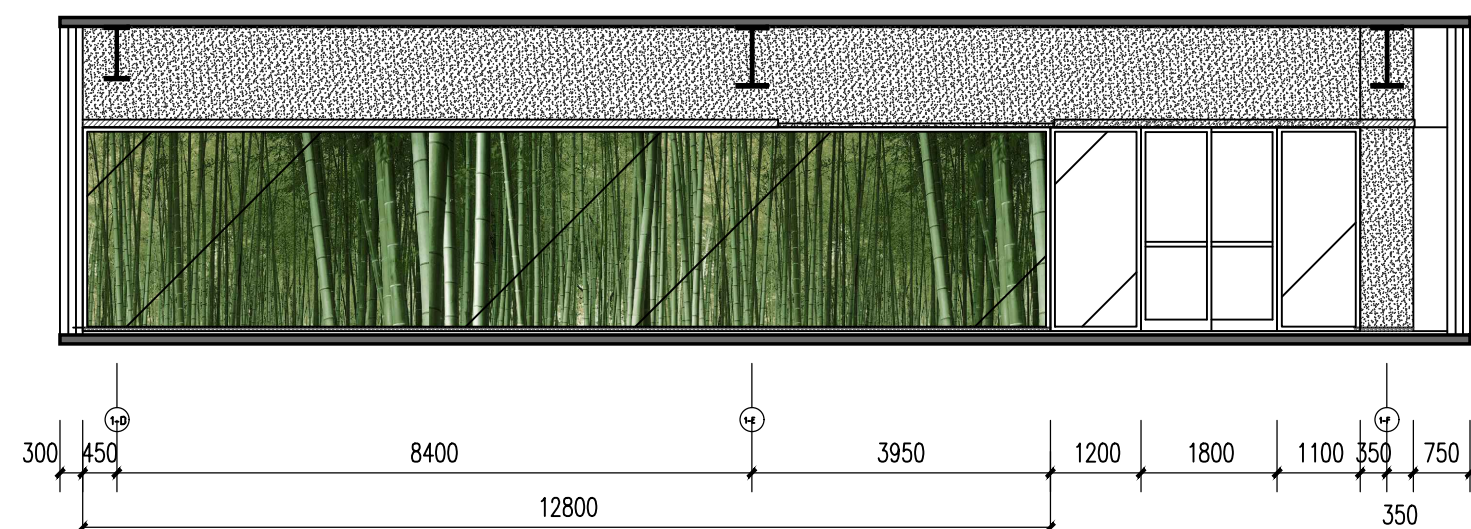


媒体餐厅 G立面图 1:100

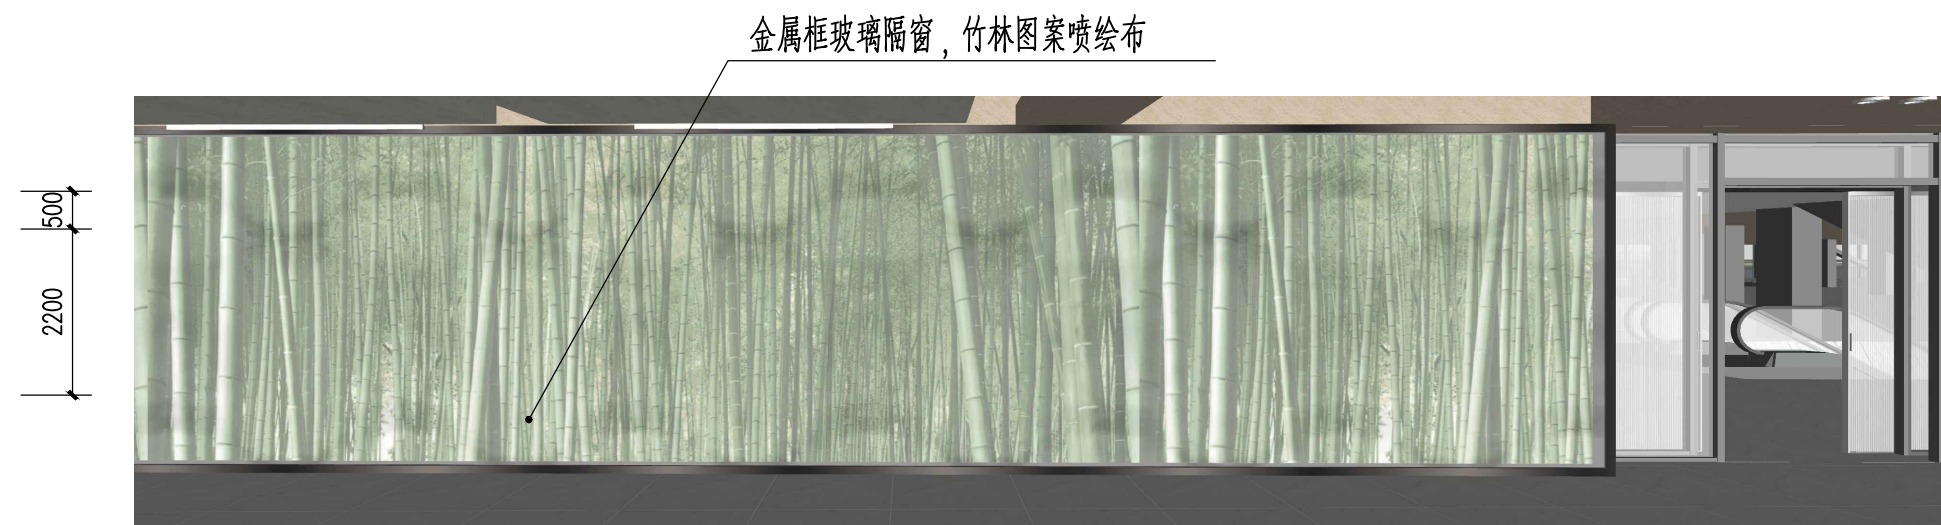

媒体餐厅 G立面效果图

出图记录		ISSUE NOTES			
版 本 REV.	日 期 DATE	备 注 REMARK			
A	2022.02				
注册执业栏 REGISTERED ARCHITECT/ENGINEER					
姓 名		NAME			
注册证书号码		REGISTRATION CERTIFICATE NO.			
注册印章号码		STAMP NO.			
设计号:	CD-20212856-F001	JOB NO.			
工程名称		PROJECT TITLE			
成都大运会主新闻中心装饰搭建					
子项名称		SUB ITEM			
建设单位		CLIENT			
成都博雅文瑞文化传播有限公司					
图 名		DRAWING TITLE			
媒体餐厅立面图（二）					
单 位	mm	UNIT	图 别	室 施	DWG. CATEGORY
比 例	1:100	SCALE	图 号	E10	DWG. NO.
日 期	2022.02	DATE	版 本	A	VER. NO.
制 图	雷鑫鹏				
设 计	雷鑫鹏				
校 对	李灏文				
专业负责人	肖子颖				
设计总负责人	张峻				
审 核	张峻				
审 定	华柯				
图 基准方中					
成都基准方中建筑设计股份有限公司					
Chengdu JZfz Architectural Design Co., Ltd.					
中国 成都市 琉璃路8号华润广场A座7-15楼					
电话: +86(28) 86333800 传真: +86(28) 86582990					
7-15F, Tower A, Criland Plaza, No.8, Liuli Road , Chengdu, P.R.C					
tel. +86(28) 86333800 fax. +86(28) 86582990					
工程注册资质证书编号: A151016191					
电子文档编号: -					
CAD FILENAME					
版 权 说 明					
COPYRIGHT DECLARATION					
此图版权为成都基准方中建筑设计股份有限公司所有，未经许可不得使用。					

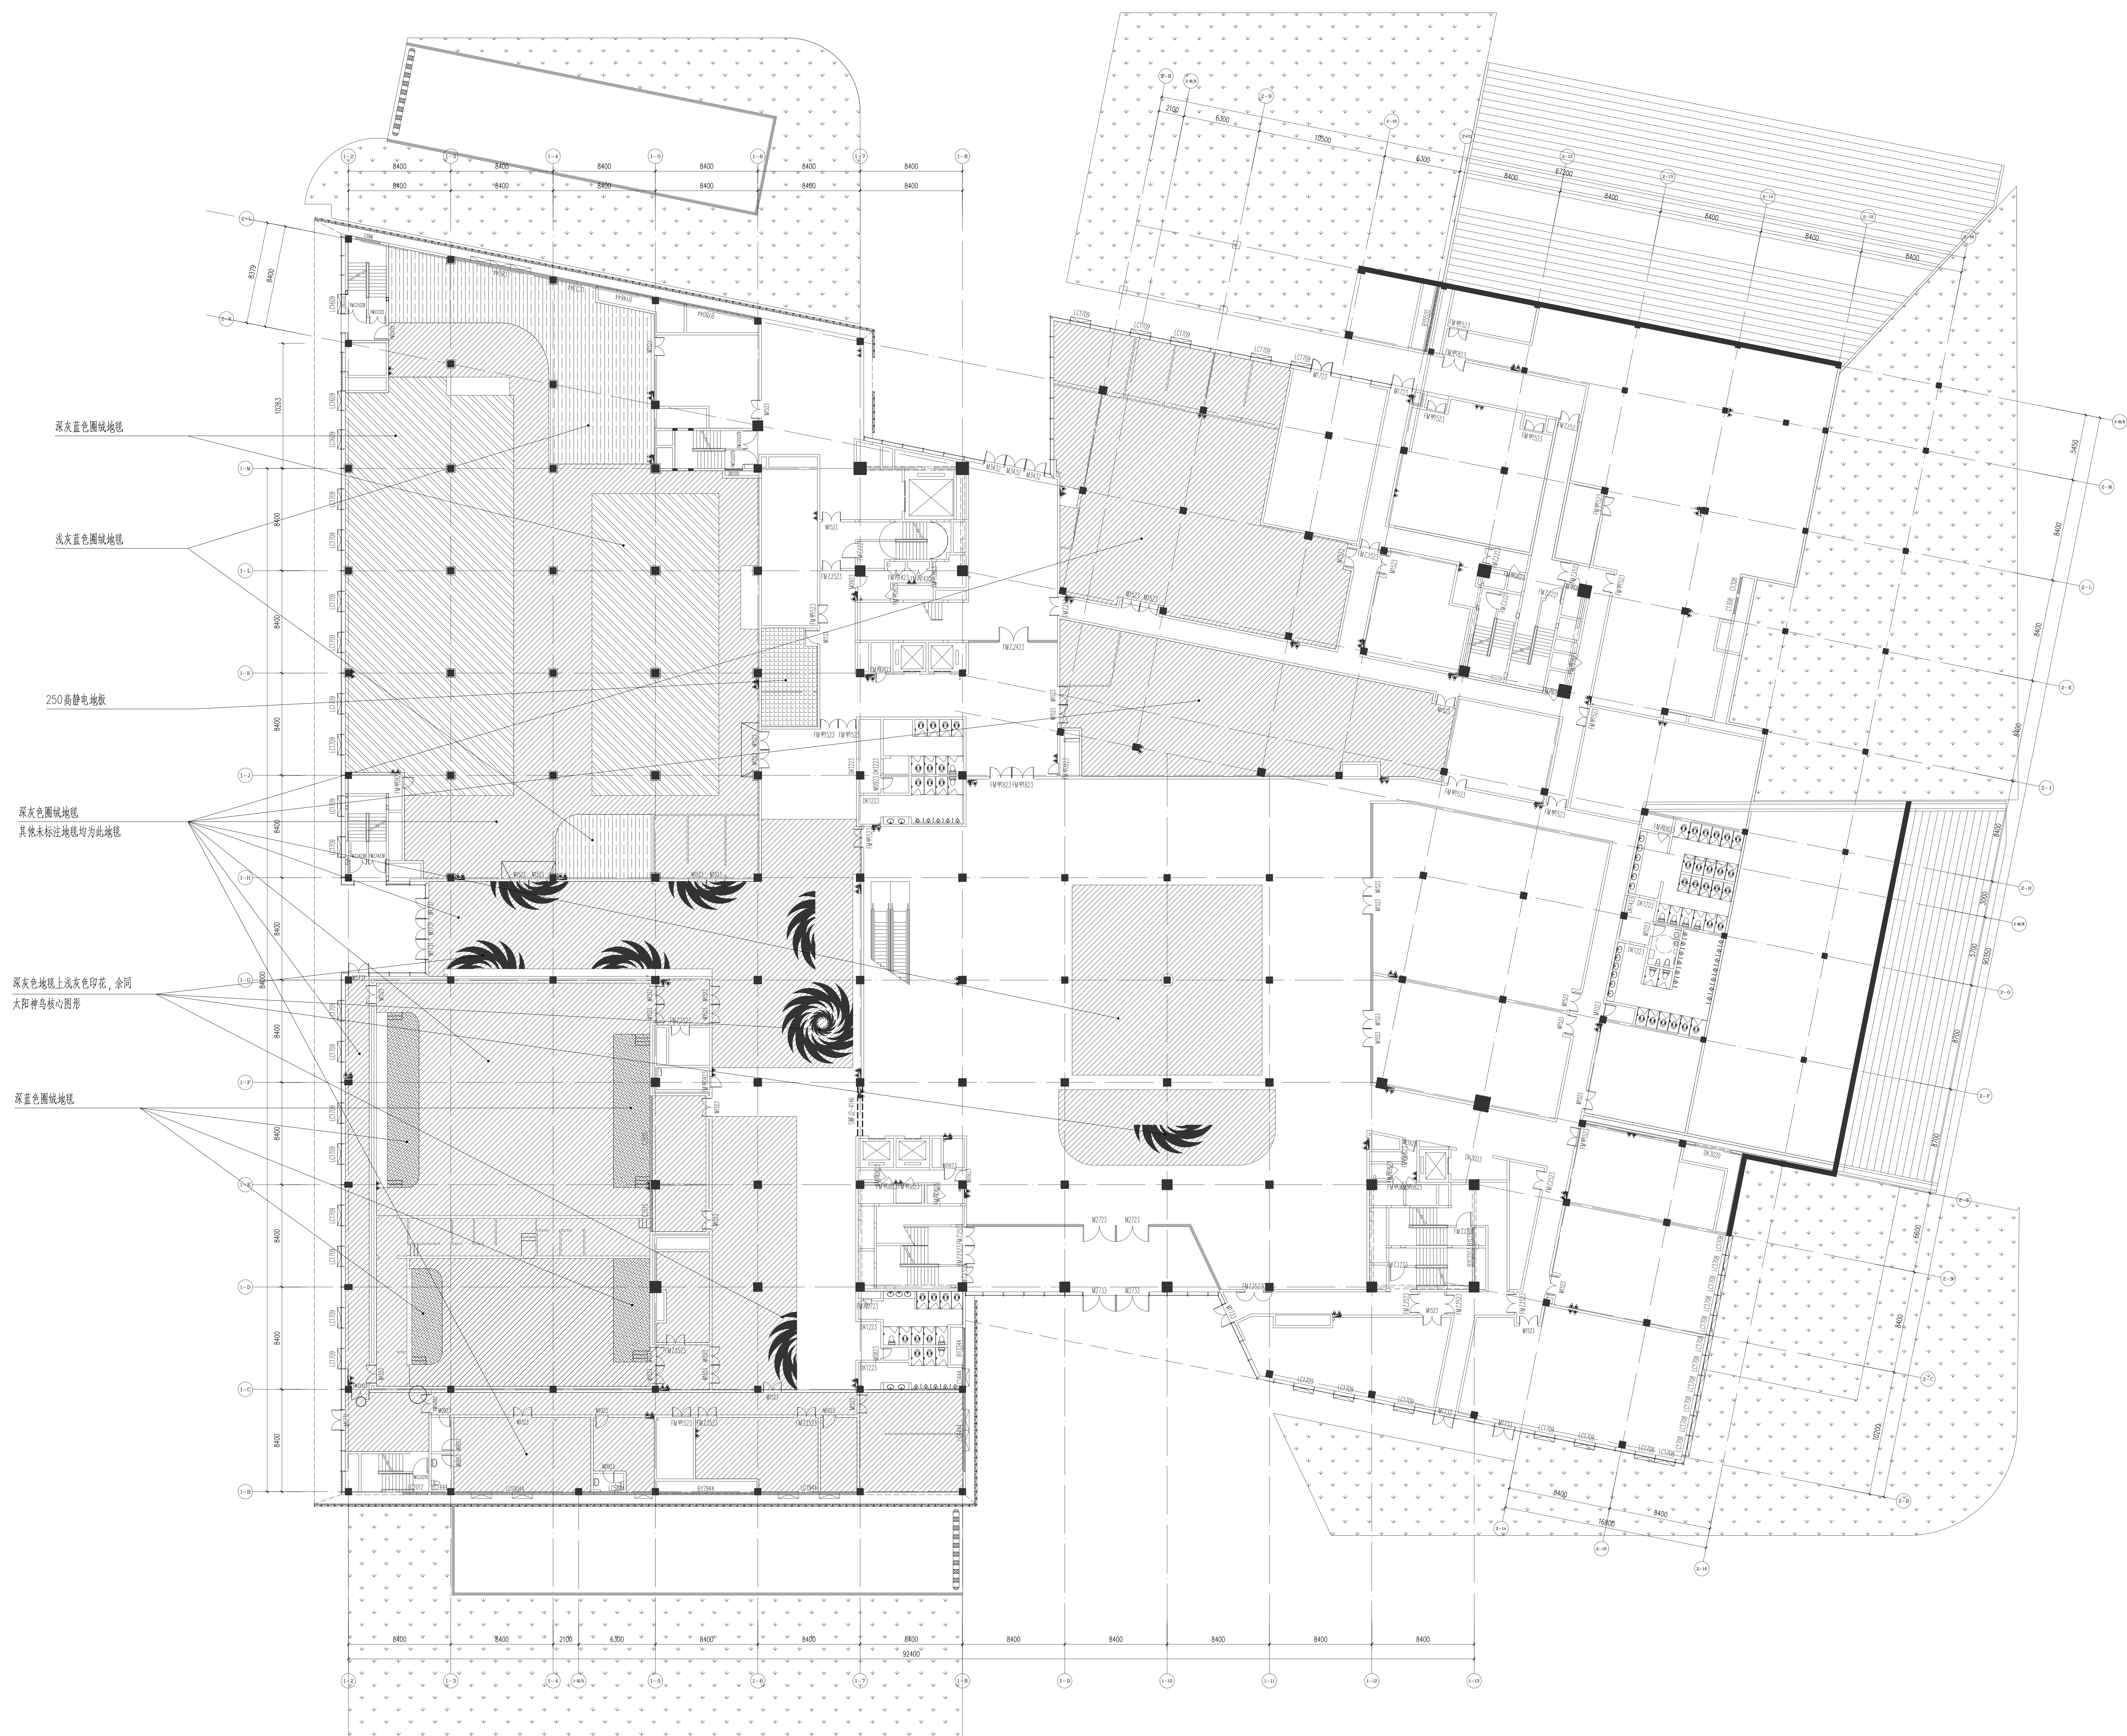

一层地面铺装图 1:200

[illegible]

注册执业栏	REGISTERED ARCHITECT/ENGINEER
姓 名	NAME
注册证书号	REGISTERED CERTIFICATE NO.
注册印章号	STAMP NO.
设计号	DESIGN NO.
工程名称	PROJECT TITLE
设计单位	DESIGN UNIT
建设单位	CLIENT
成都博雅文瑞文化传播有限公司	CHENGDU BOYAWENRUI CULTURE COMMUNICATIONS CO., LTD.
图 章	STAMP

一层地面铺装图			
单位	mm	图号	工程名称
比例	1:200	图号	F01
日期	2022.02	版本	A
制图	陈	审核	
设计	陈子颖		
设计	陈子颖		
设计	李婉文		
专业负责人	陈子颖		
SIGNATURE SHEET			
设计总负责人	张强		
PROJECT SHEET			
审核	张强		
APPROVED BY	李树		



二层地面铺装图			
单位	mm	图 纸	工程类别
比例	1:200	图 号	F02 (附 属)
日 期	2022.02	版 本	A (共 1 版)
设计	设计	材料	
审核	审核	材料	
专业负责人	专业负责人	材料	
设计负责人	设计负责人	材料	
项目经理	项目经理	材料	
审 核	审 核	材料	
审 定	审 定	材料	

中 方 基 准

成都基准方中建筑设计股份有限公司
Chengdu JZFZ Architectural Design Co., Ltd.


中国 成都市 国槐溪路4号中法大厦15-16楼
电话: +86-28-86533399 传真: +86-28-86533399
T: +86, Tower A Grand Plaza, No.42 Jialin Road, Chengdu, P.R.C
E: +8628 86533399 Fax: +8628 86533399

工程设计资质认定编号: A151016191

电子文件编号: —

版 权 说 明
COPYRIGHT DECLARATION

此图所有权为成都基准方中建筑设计股份有限公司所有。未经许可不得使用。

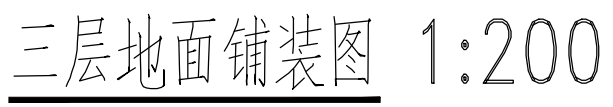

注册执业单位	REGISTERED ARCHITECT/ENGINEER
姓 名	NAME
注册证书号码	REGISTERED NO./CERTIFICATE NO.
注册印章号码	STAMP NO.
设计号	DESIGN NO.
工程名称	PROJECT TITLE
子项名称	SUB ITEM
建设单位	CLIENT
成都博雅文瑞文化傳播有限公司	
图 名	DRAWING TITLE

中 方 基 准

成都基准方中建筑设计股份有限公司
Chengdu JZFZ Architectural Design Co., Ltd.


中国 成都市 武侯区新加坡路156号2-15楼
电话: +86 (28) 85033000 传真: +86 (28) 85032990
2-15F, Tower A Grand Plaza, No.156 Jiali Road, Chengdu, P.R.C
电: +86(28) 85033000 fax: +86(28) 85032990

工程设计资质证书编号: A151016191

电子文档编号: -


版 权 说 明
COPYRIGHT DECLARATION

此图所有权为成都基准方中建筑设计股份有限公司所有。未经许可不得使用。

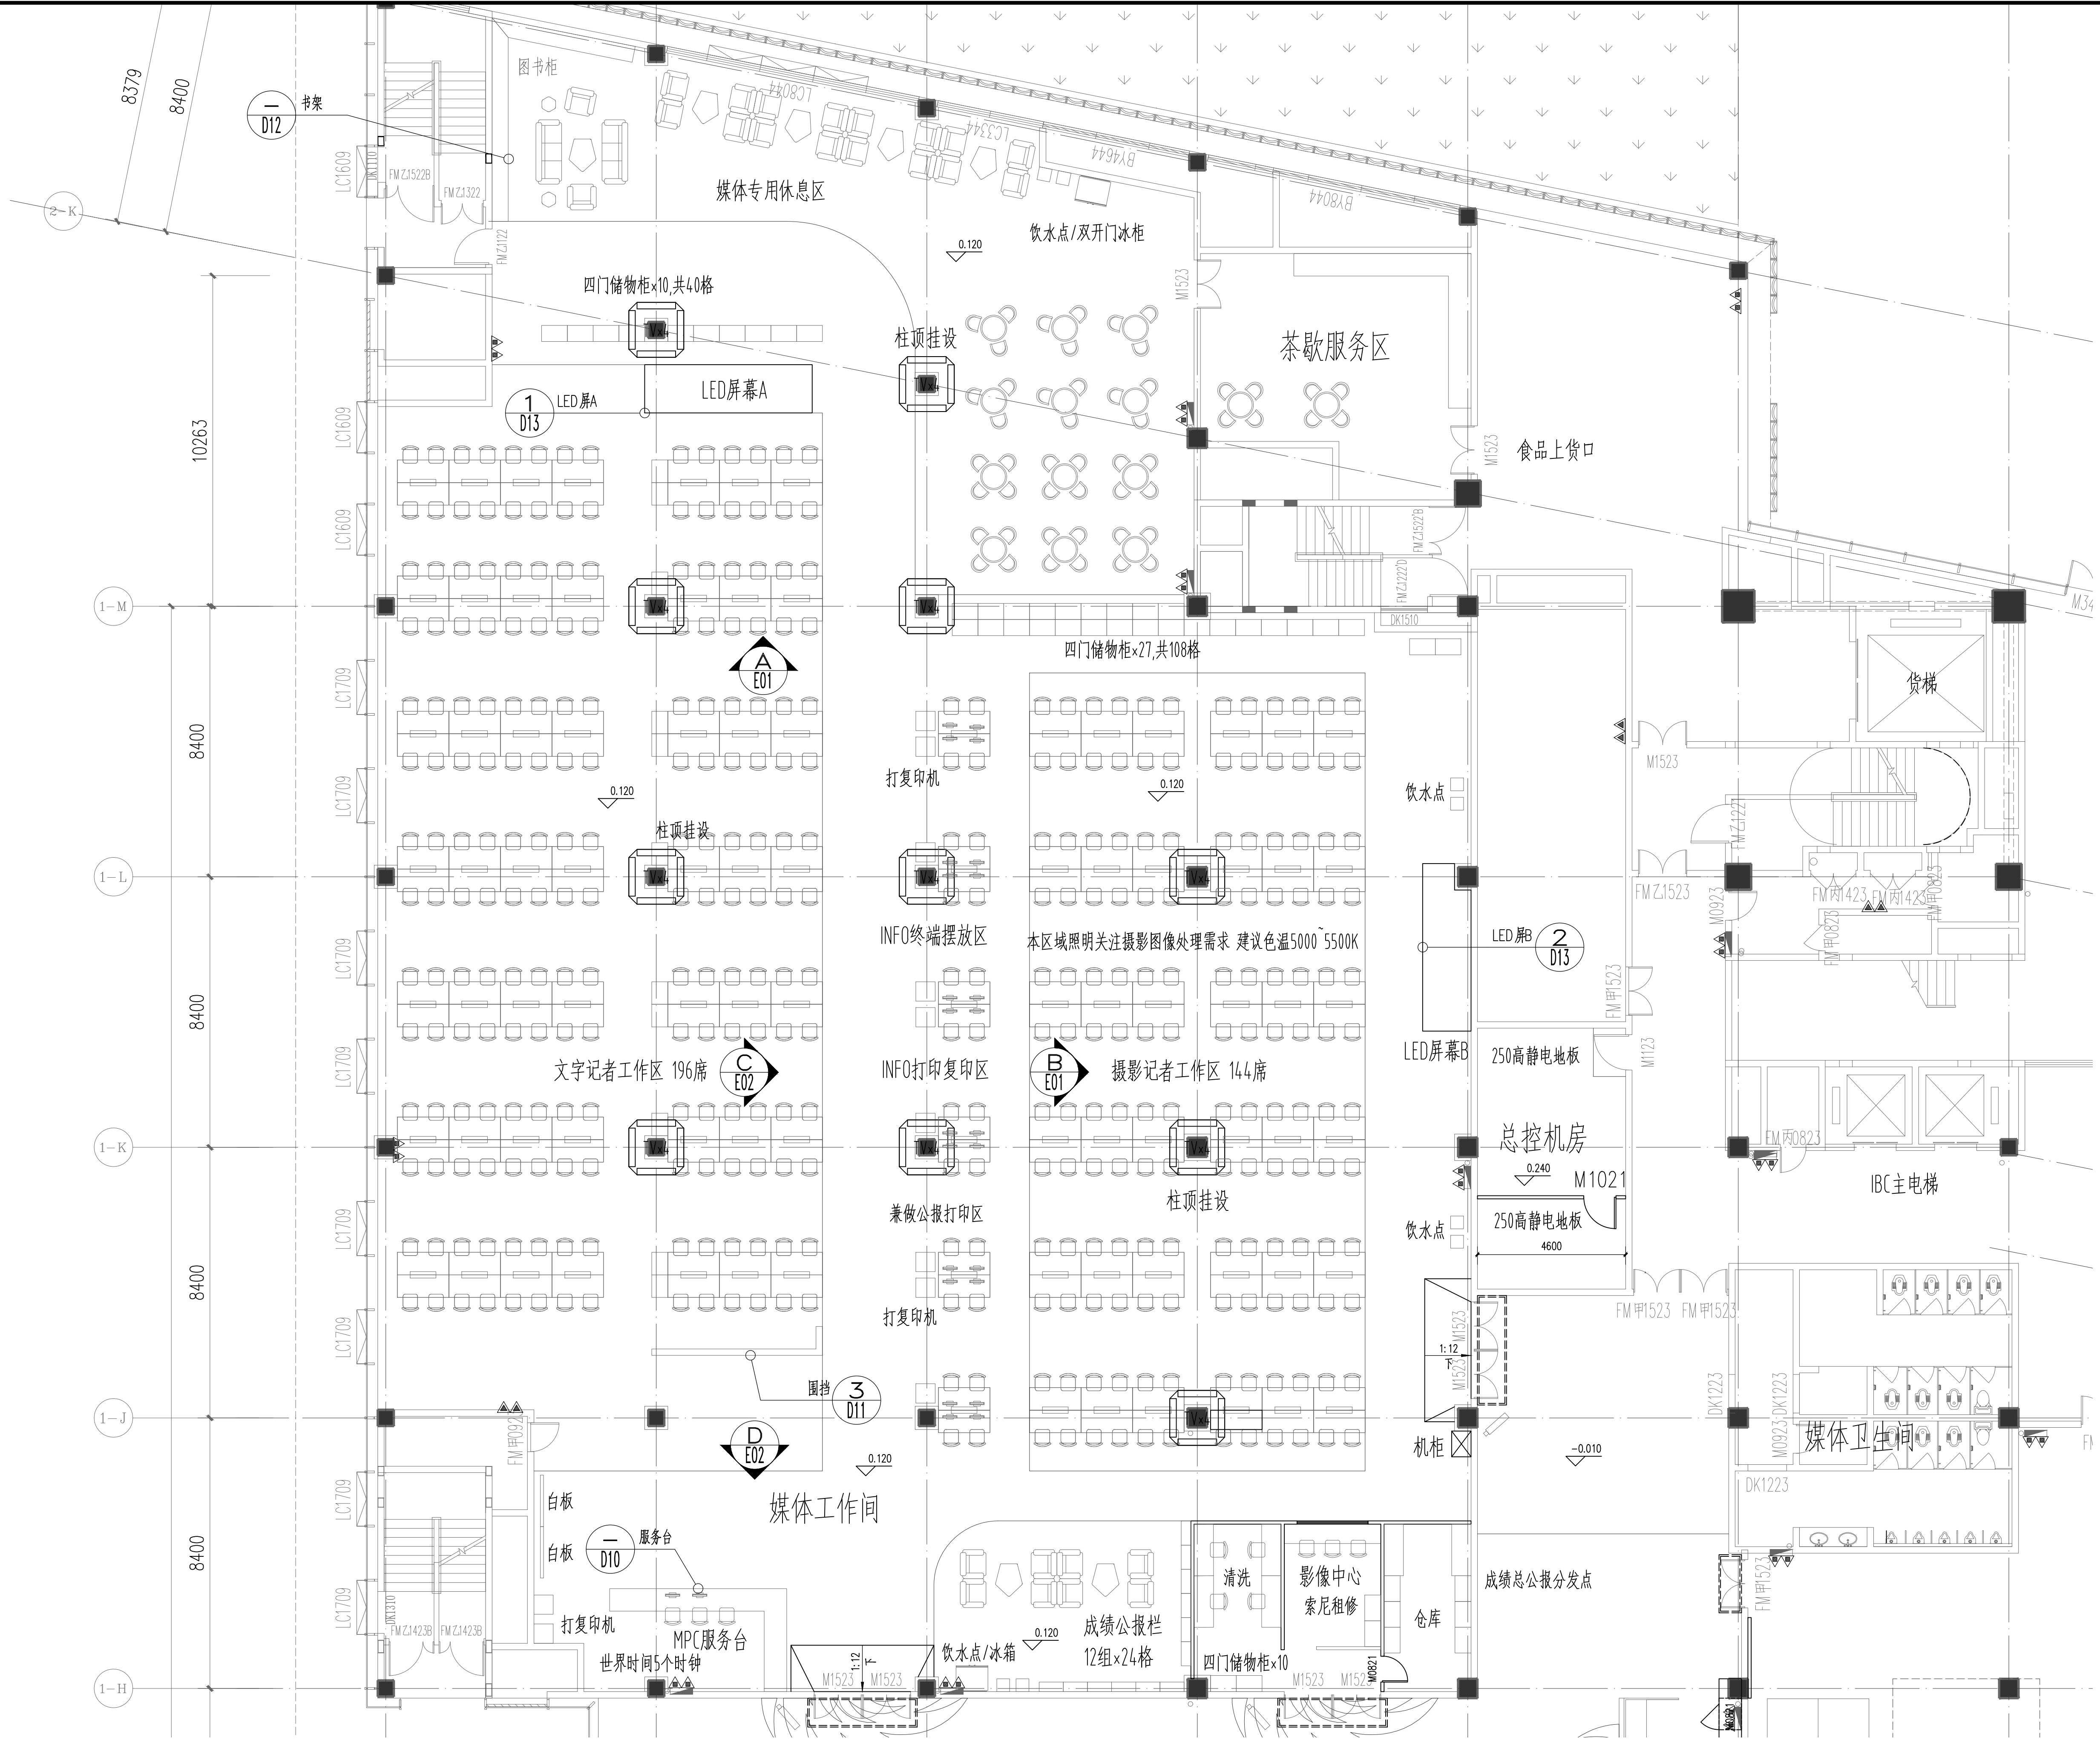

媒体工作间放大平面图 1:100

平面示意图		KEY PLAN	
注册执业栏		REGISTERED ARCHITECT/ENGINEER	
注册证书号码		REGISTRATION CERTIFICATE NO.	
注册印章号码		STAMP NO.	
设计号		JOB NO.	
工程名称		PROJECT TITLE	
事项名称		SUB-TITLE	
建设单位		CLIENT	
图名		DRAWING TITLE	
单位		UNIT	
比例		SCALE	
日期		DATE	
图号		DRAWING NO.	
版本		VERSION	
设计		DESIGNED BY	
校核		CHECKED BY	
专业负责人		DISCIPLINE CHIEF	
设计总负责人		PROJECT CHIEF	
审核		REVIEWED BY	
审定		APPROVED BY	
CAD FILENAME			
版 权 说 明 COPYRIGHT DECLARATION			
此图版权归成都基准方中建筑设计股份有限公司所有，未经许可不得使用。			

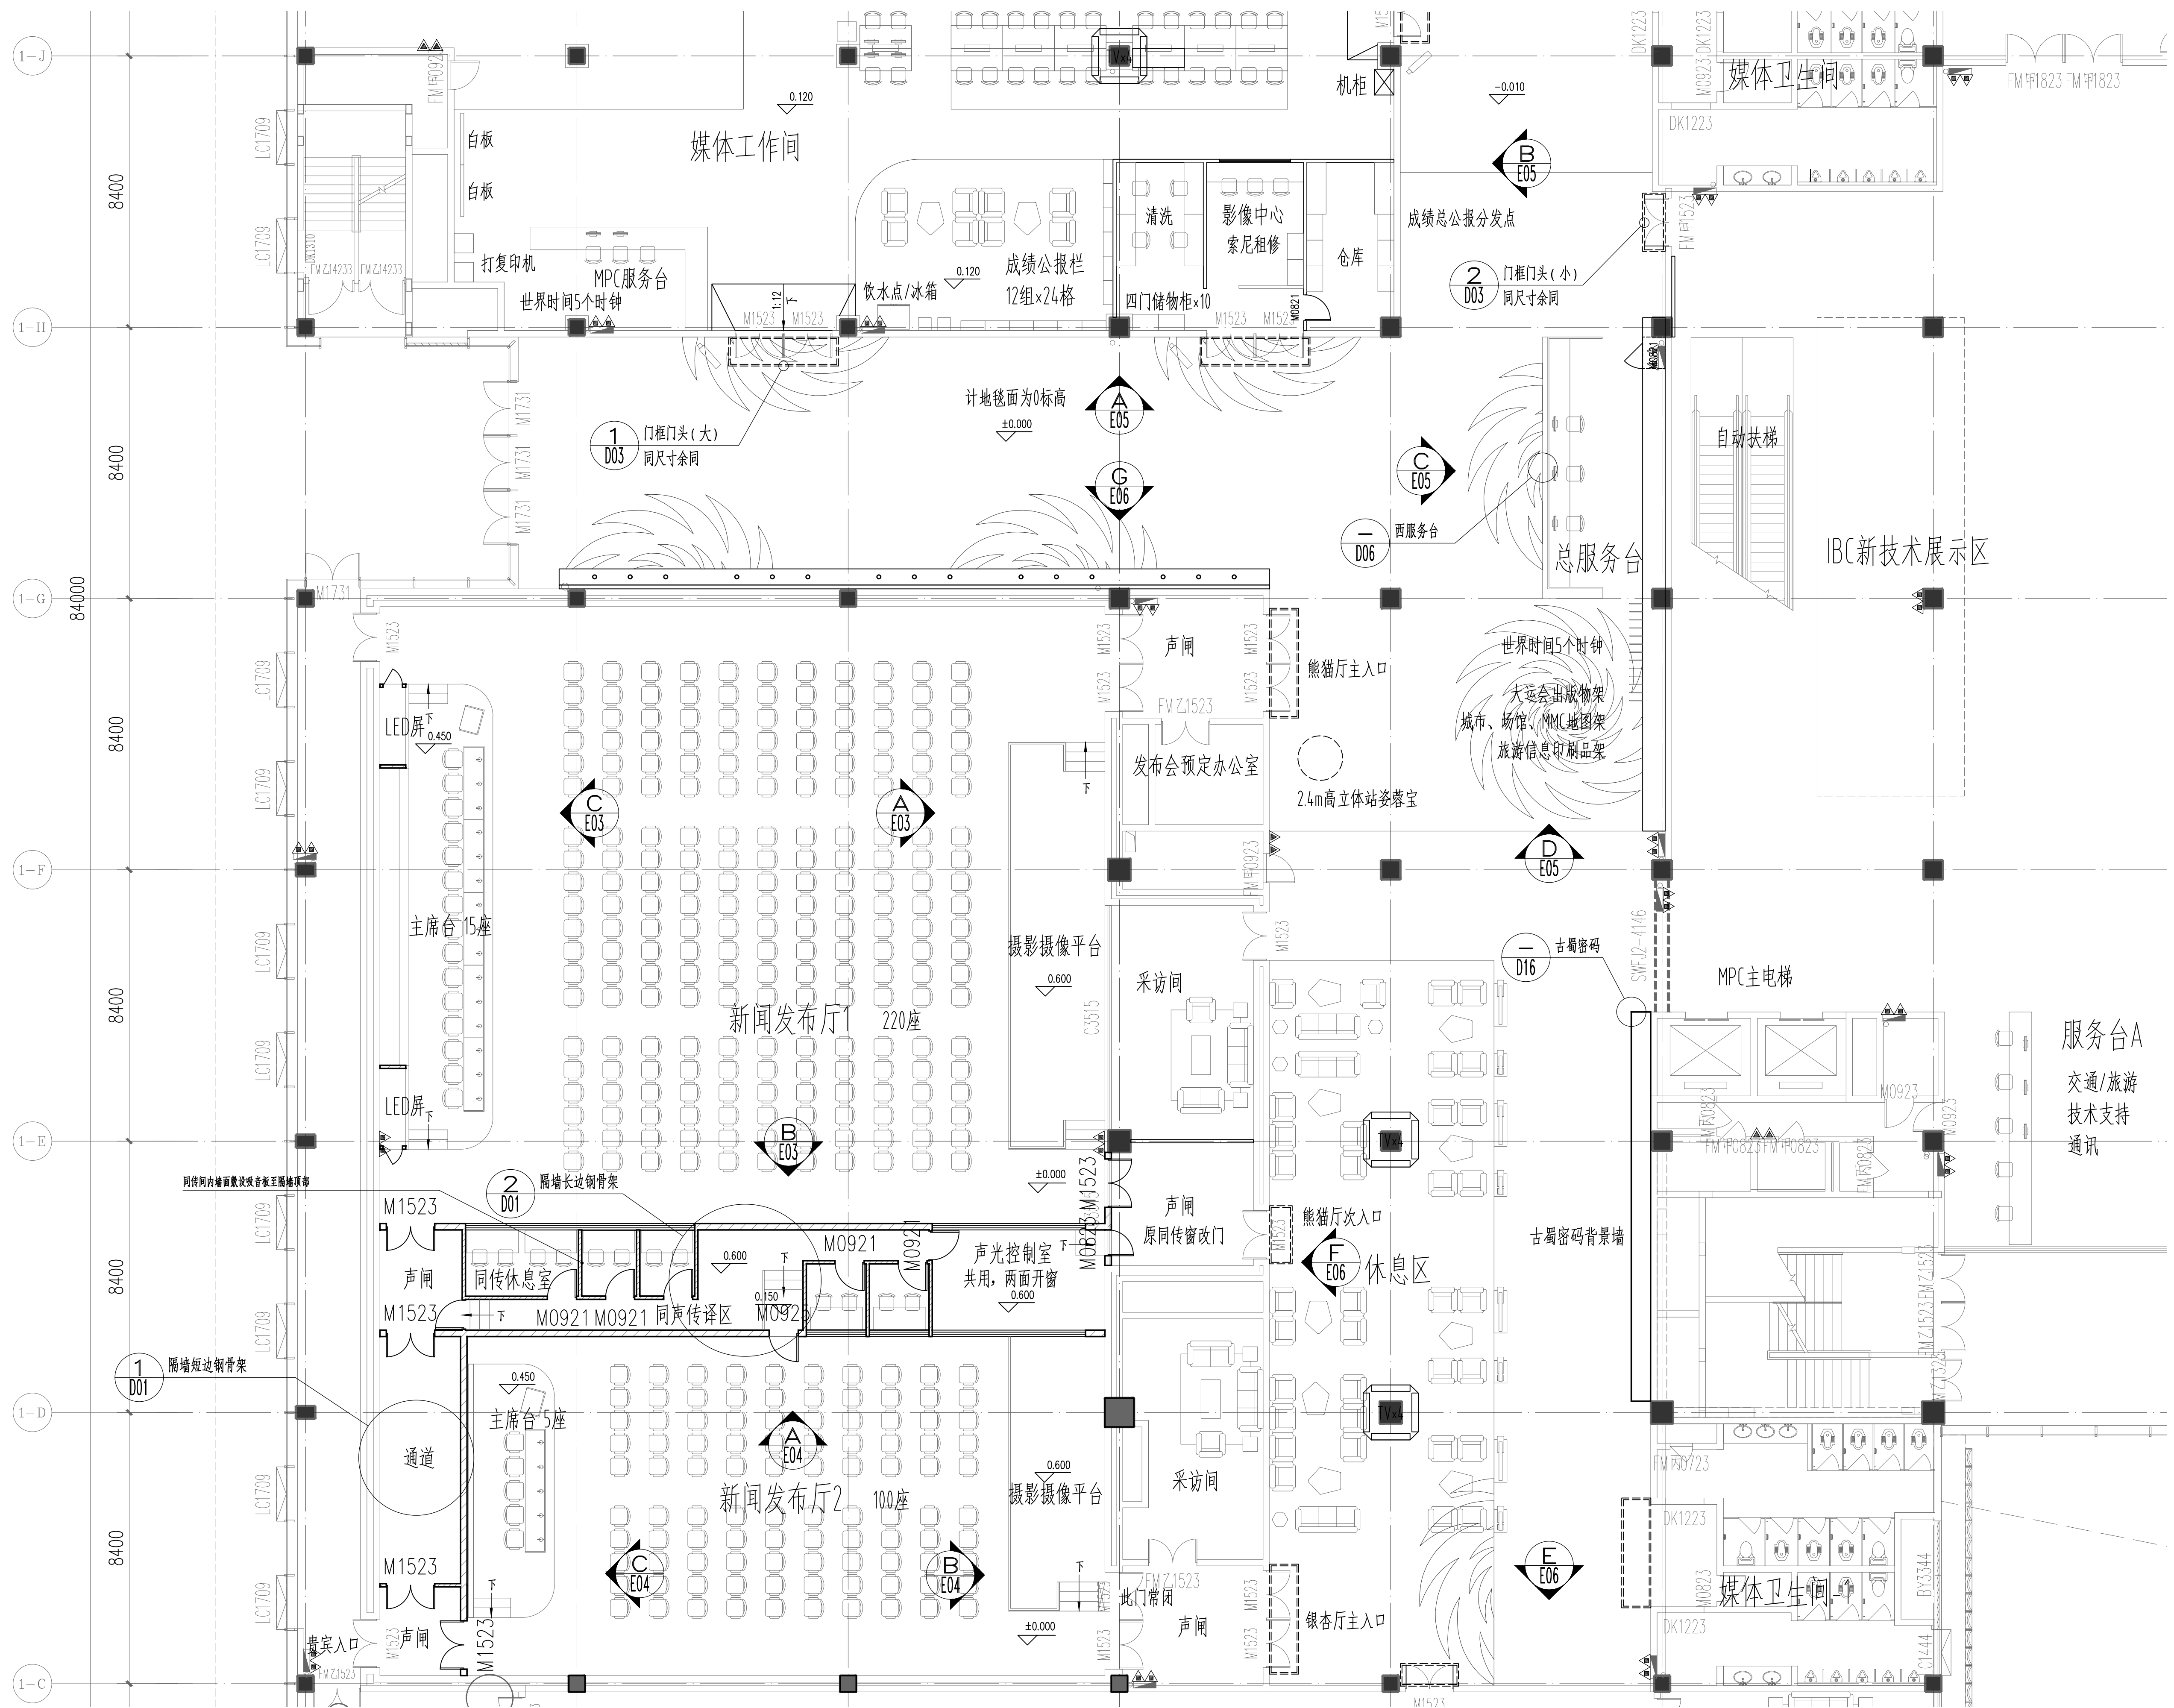

发布厅及其外侧公共通道放大平面图 1:100

平面示意: KEY PLAN

[illegible]

注册执业栏		REGISTERED ARCHITECT/ENGINEER
姓 名	NAME	
注册证书号码	REGISTRATION CERTIFICATE NO.	
注册印章号码	STAMP NO.	
设计号	CD-20212856-F001	JOB NO.
工程名称	PROJECT TITLE	
成都大运会主新闻中心装饰搭建		
子项名称	SUB ITEM	
建设单位	CLIENT	
成都博雅艾瑞文文化传播有限公司		
图 名	DRAWING TITLE	

发布厅及其外侧公共通道放大平面图			
单位	mm	图 号	室 类
比 例	1:100	图 号:	MO2
日 期	2022.02	版 本:	A
制 图	王 颖		
设 计	肖子颖		
DESIGNED BY	肖子颖		
校 对	李婧文		
CHECKED BY	李婧文		
专业负责人	肖子颖		
DISCIPLINE CHIEF	肖子颖		
设计总负责人	张 璇		
PROJECT CHIEF	张 璇		
审 核	张 璇		
AUDIT	张 璇		
审 定	华 轲		
APPROVED BY	华 轲		

国 基准方中

成都基准方中建筑设计股份有限公司

Chengdu JZFY Architectural Design Co., Ltd.

中国 成都市 琉璃场8号华联广场A座7-15楼
电话: +86(28) 86333800 传真: +86(28) 86582990

7-15F, Tower A, Grand Plaza, No.8Jialu Road, Chengdu, P.R.C
电话: +86(28) 86333800 fax: +86(28) 86582990


工程设计资质证书编号: A151016191

电子文档编号: --

CAD FILENAME

版 权 说 明
COPYRIGHT DECLARATION

此图版权为成都基准方中建筑设计股份有限公司所有，未经许可不得使用。

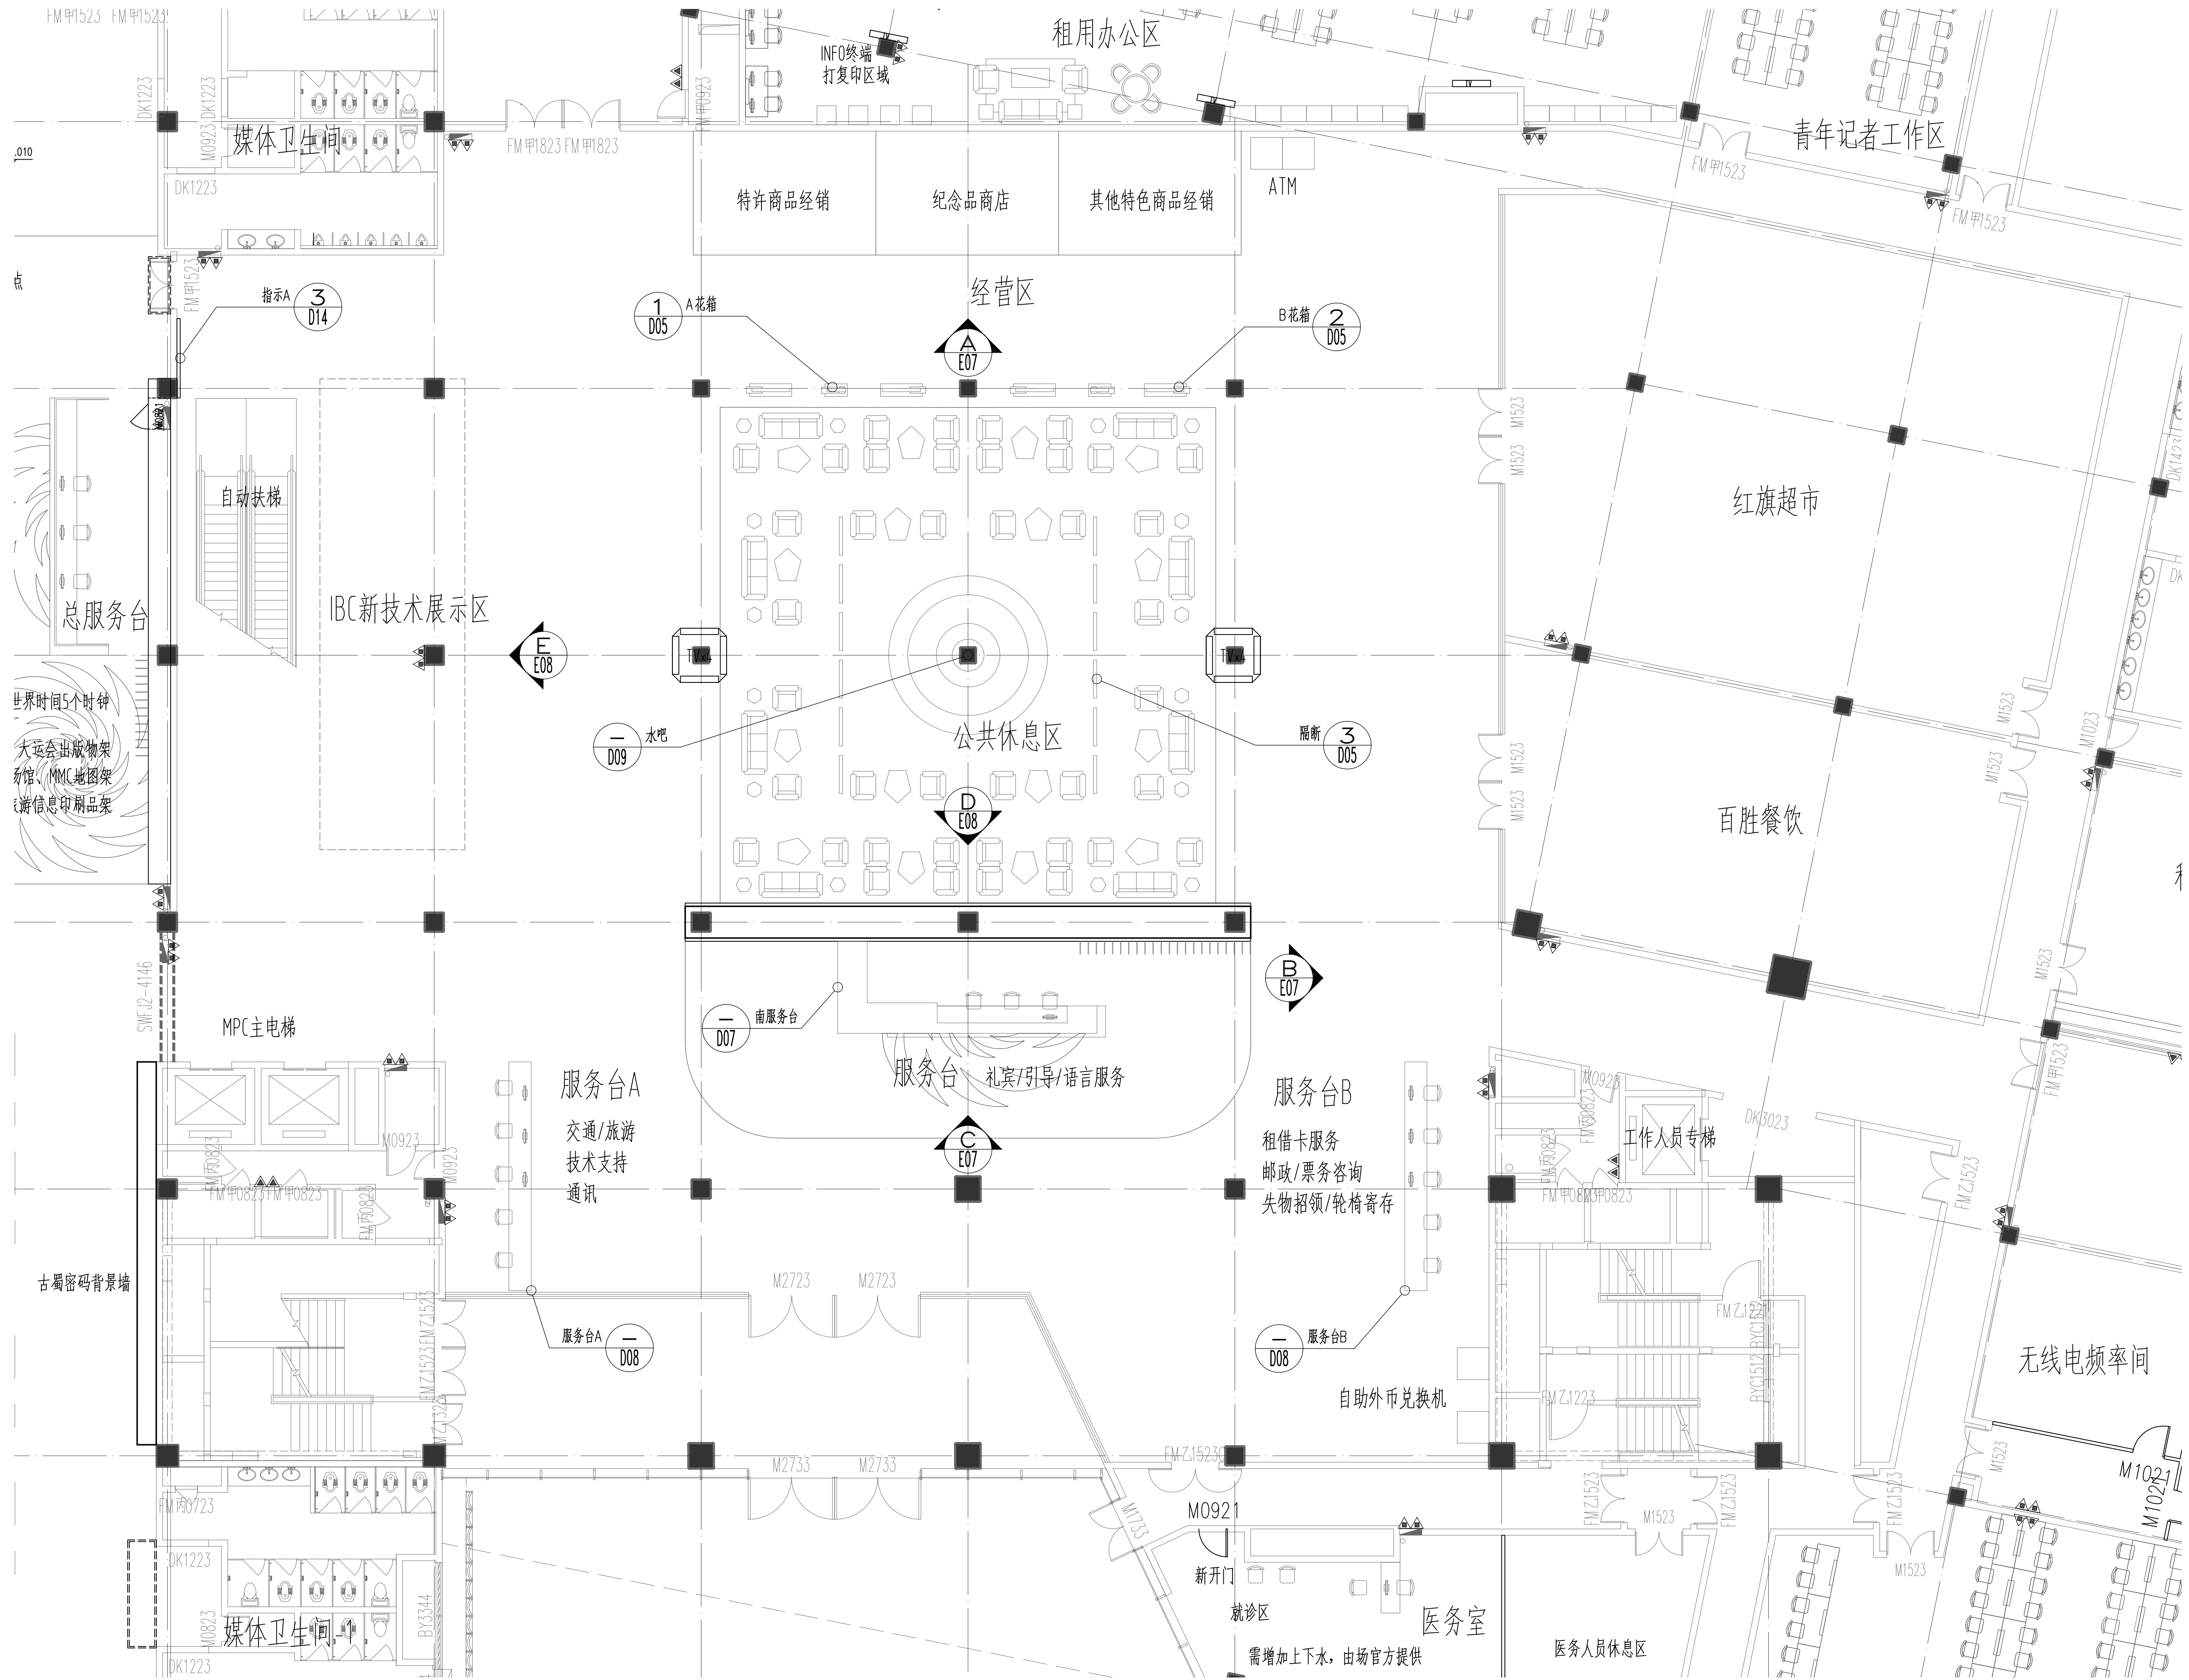

综合服务区放大平面图 1:100

平面示意图 KEY PLAN

出图记录 ISSUE NOTES

版本	日期	备注
REV	DATE	REMARKS
A	2022.02	

注册执业栏 REGISTERED ARCHITECT/OWNER

姓名	NAME
注册证书号码	REGISTRATION CERTIFICATE NO.
注册印章号码	STAMP NO.
设计号	DESIGN NO.
工程名称	PROJECT TITLE
子项名称	SUB ITEM

建设单位 CLIENT

成都博雅文瑞文化传播有限公司


综合服务区放大平面图

单位	mm	UNIT	图例	室施	DWG CATEGORY
比例	1:100	SCALE	图号	M03	DWG NO.
日期	2022.02	DATE	版本	A	VER. NO.
制图	肖子颖	DRAWN BY	设计	肖子颖	DESIGNED BY
校对	李耀文	CHECKED BY	专业负责人	肖子颖	DISCIPLINE CHIEF
设计负责人	张健	PROJECT CHIEF	审核	张健	AUDIT
审定	华树	APPROVED BY			

基准方中
成都基准方中建筑设计股份有限公司
Chengdu JZfZ Architectural Design Co., Ltd.
中国 成都市 国槐路8号华润广场A座7-15楼
电话: +86(28) 86333800 传真: +86(28) 86582990
7-15F, Tower A, Grand Plaza, No.8JiJi Road, Chengdu, P.R.C
Tel: +86(28) 86333800 Fax: +86(28) 86582990
工程设计资质证书编号: A151016191
电子文档编号: -

版权说明 COPYRIGHT DECLARATION

此图版权为成都基准方中建筑设计股份有限公司所有, 未经许可不得复用。

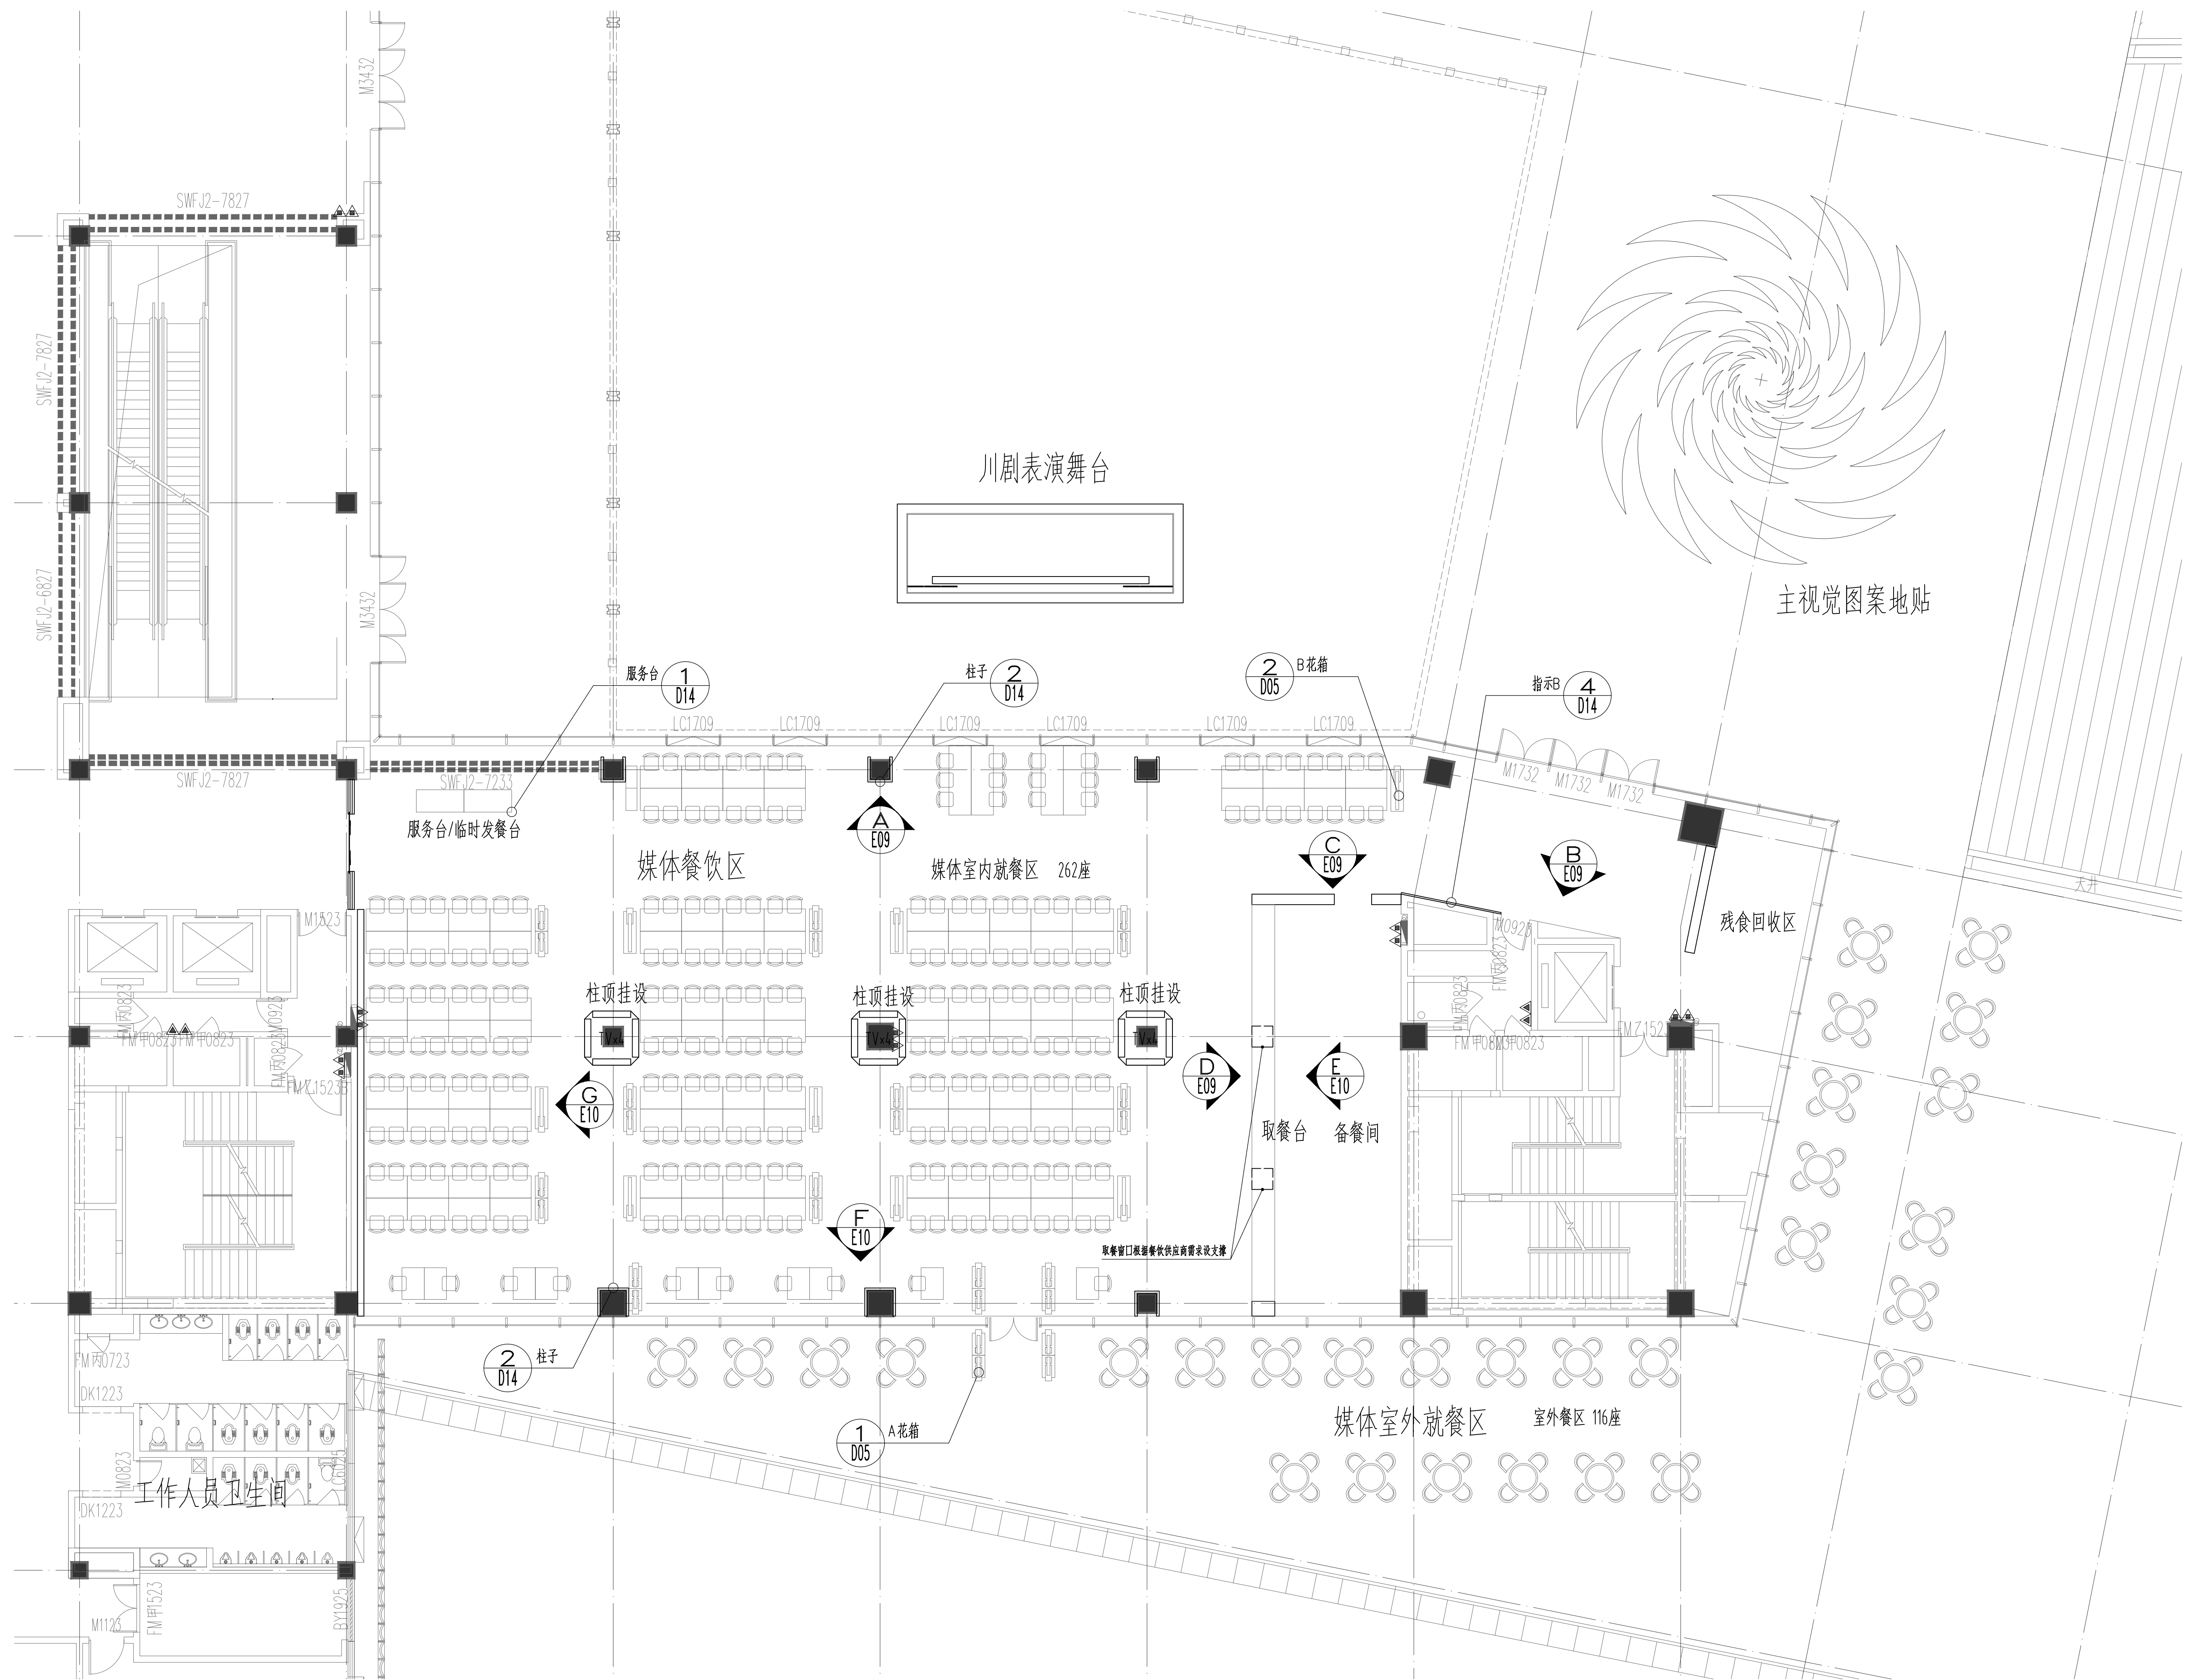

媒体餐厅放大平面图 1:100

平面示意: KEY PLAN

[illegible]

注册执业栏		REGISTERED ARCHITECT/ENGINEER
姓 名	NAME	
注册证书号码	REGISTRATION CERTIFICATE NO.	
注册印章号码	STAMP NO.	
设计号	CD-20212856-F001	JOB NO.
工程名称	PROJECT TITLE	
成都大运会主新闻中心装饰搭建		
子项名称	SUB ITEM	
建设单位	CLIENT	
成都博雅文瑞文化傳播有限公司		
图 名	DRAWING TITLE	

单位	mm	UNIT	图 纸	室 施	DWG. CATEGORY
比例	1:100	SCALE	图 号:	MO4	DWG. NO.
日 期	2022.02	DATE	版 本	A	REV. NO.
制 图	肖子颖				
DRAWN BY	肖子颖				
设 计	肖子颖				
DESIGNED BY	肖子颖				
校 对	李璐文				
CHECKED BY	肖子颖				
专业负责人					
DISCIPLINE CHIEF					
设计总负责人	张峻				
PROJECT CHIEF	张峻				
审 核	张峻				
AUDIT	张峻				
审 定	华树				
APPROVED BY	华树				

基准方中

成都基准方中建筑设计股份有限公司
Chengdu JZfz Architectural Design Co., Ltd.

中国 成都市 琉璃路8号华润广场A座7-15楼
电话: +86 (28) 86533800 传真: +86 (28) 86582990
7-15F, Tower A, Citland Plaza, No.8, Liuli Road, Chengdu, P.R.C

工程设计资质证书编号: A151016191

电子文档编号: — CAD FILENAME

版 权 说 明
COPYRIGHT DECLARATION

此图版权为成都基准方中建筑设计股份有限公司所有，未经许可不得使用。

采暖通风			图
			总
电	气		水
建	筑		构
合	建		社

图纸目录

序号	分项	图名	图号	图纸尺寸	版本号	出图时间	修改	备注
01	目录与说明	图纸目录	N01	A2	A	2022. 2		
02		设计总说明（一）	N02	A2	A	2022. 2		
03		设计总说明（二）	N03	A2	A	2022. 2		
04		设计总说明（三）	N04	A2	A	2022. 2		
05		设计总说明（四）	N05	A2	A	2022. 2		
06	平面系统图	负一层平面布置图	P01	A0	A	2022. 2		
07		一层平面布置图	P02	A0	A	2022. 2		
08		二层平面布置图	P03	A0	A	2022. 2		
09		三层平面布置图	P04	A0	A	2022. 2		
10		一层地面铺装图	F01	A0	A	2022. 2		
11		二层地面铺装图	F02	A0	A	2022. 2		
12		三层地面铺装图	F03	A0	A	2022. 2		
13		一层天花、灯具布置图	C01	A0	A	2022. 2		
14		二层天花、灯具布置图	C02	A0	A	2022. 2		
15		媒体工作间放大平面图	M01	A1	A	2022. 2		
16		发布厅及其外侧公共通道放大平面图	M02	A1	A	2022. 2		
17		综合服务区放大平面图	M03	A1	A	2022. 2		
18		媒体餐厅放大平面图	M04	A1	A	2022. 2		
19	立面图	媒体工作间立面图（一）	E01	A2	A	2022. 2		
20		媒体工作间立面图（二）	E02	A2	A	2022. 2		
21		新闻发布厅1立面图	E03	A2	A	2022. 2		
22		新闻发布厅2立面图	E04	A2	A	2022. 2		
23		西入口区域立面图（一）	E05	A2	A	2022. 2		
24		西入口区域立面图（二）	E06	A2	A	2022. 2		
25		综合服务区立面图（一）	E07	A2	A	2022. 2		
26		综合服务区立面图（二）	E08	A2	A	2022. 2		
27		媒体餐厅立面图（一）	E09	A2	A	2022. 2		
28		媒体餐厅立面图（二）	E10	A2	A	2022. 2		
29	做法大样图	新闻发布厅隔墙钢骨架排布图	D01	A2	A	2022. 2		
30		西入口门头、南立面标识大样图	D02	A2	A	2022. 2		
31		西入口通道与发布厅外侧通道门框大样图、吊旗大样图	D03	A2	A	2022. 2		
32		落地发光字大样图	D04	A2	A	2022. 2		
33		花箱及隔断大样图	D05	A2	A	2022. 2		
34		西服务台大样图	D06	A2	A	2022. 2		
35		南服务台大样图	D07	A2	A	2022. 2		
36		服务台A、B大样图	D08	A2	A	2022. 2		
37		水吧大样图	D09	A2	A	2022. 2		
38		MPC服务台大样图	D10	A2	A	2022. 2		
39		媒体工作间指示及吊旗大样图	D11	A2	A	2022. 2		
40		媒体工作间书架大样图	D12	A2	A	2022. 2		
41		媒体工作间LED屏大样图	D13	A2	A	2022. 2		
42		餐厅服务台、柱饰面及指示大样图	D14	A2	A	2022. 2		
43		直播/采访间采访台大样图	D15	A2	A	2022. 2		
44		古蜀密码大样图	D16	A2	A	2022. 2		
45		大运友谊墙大样图	D17	A2	A	2022. 2		
46		川剧表演舞台大样图	D18	A2	A	2022. 2		

出图记录		ISSUE NOTES
版 本	日 期	备 注
REV.	DATE	REMARK
A	2022.02	
注册执业栏		REGISTERED ARCHITECT/ENGINEER
姓 名		NAME
注册证书号码		REGISTRATION CERTIFICATE NO.
注册印章号码		STAMP NO.
设计号: CD-20212856-F001		JOB NO.
工程名称		PROJECT TITLE
成都大运会主新闻中心装饰搭建		
子项名称		SUB ITEM
建设单位		CLIENT
成都博雅文瑞文化传播有限公司		
图 名		DRAWING TITLE
图纸目录		
单 位	mm	UNIT
图 别	室施	DWG. CATEGORY
比 例	—	SCALE
图 号	N01	DWG. NO.
日 期	2022.02	DATE
版 本	A	VER. NO.
制 图	方岑	
设 计	方岑	
校 对	李肅文	
专业负责人	肖子颖	
DISCIPLINE CHIEF		
设计总负责人	张峻	
PROJECT CHIEF		
审 核	张峻	
AUDIT		
审 定	华柯	
APPROVED BY		
成都基准方中		
成都基准方中建筑设计股份有限公司		
Chengdu JZFZ Architectural Design Co., Ltd.		
中国 成都市 琉璃路8号华润广场A座7-15楼		
电话: +86 (28) 86333800 传真: +86 (28) 86582990		
7-15F, Tower A, Crland Plaza, No.8, Liuli Road , Chengdu, P.R.C		
tel. +86(28) 86333800 fax. +86(28) 86582990		
工程设计资质证书编号:		A151016191
电子文档编号: -		CAD FILENAME
版 权 说 明		
COPYRIGHT DECLARATION		
此图版权为成都基准方中建筑设计股份有限 公司所有，未经许可不得使用。		

采暖通风	图		
	总		
电	气	给	排
	水		
质	构		
建	筑		
结	构		
位	位	社	

1. 项目概况

- 1.1 项目名称：成都大运会主新闻中心装饰搭建服务项目
- 1.2 项目性质：现有建筑临时装饰搭建
- 1.3 项目规模：1.6 万平方米
- 1.4 建设地点：成都市龙泉驿区东安湖南岸，环湖南路北侧
- 1.5 设计范围：设计范围包含大运会主媒体中心（东安书院）地下一层部分区域（预留功能房间及车库区域），一、二层全部区域，及三层直播间区域

2. 设计依据

- 2.1. 国家与地方现行各种规范、规程：
《民用建筑设计统一标准》GB50352-2019
《成都市城市规划管理技术规定》（2017 年版）
《建筑内部装修设计防火规范》GB50222-2017
《建筑设计防火规范》（GB50016-2014）2018 年版
《建筑地面工程施工规范》（GB50209-2010）
《建筑装饰装修工程质量验收规范》（GB50210-2018）
《建筑工程施工质量验收统一标准》GB 50300--2001
《公共建筑节能设计标准》GB50189-2015
《民用建筑设计统一标准》GB50352-2019
《建筑工程施工质量验收统一标准》（GB50300-2013）
《室内装饰装修材料内墙涂料中有害物质限量》（GB18582-2008）
《民用建筑工程室内环境污染控制规范》GB 50325—2010
《室内装饰装修材料人造板及制品中甲醛释放限量》GB18580-2001
《室内装饰装修材料溶剂型木器涂料中有限物质限量》GB18581-2009
《民用建筑工程室内环境污染控制标准》（GB50325-2020）
《工程建设标准强制性条文（房屋建筑部分）》（2013 年版
《建筑照明设计标准》（GB 50034-2013）
《建筑内部装饰防火设计施工及验收规范》（GB50354-2005）
《办公建筑设计规范》 JGJ67-2006
《旅馆建筑设计规范》JGJ62-90
《建筑装饰装修工程质量验收标准》GB50210-2018

除以上规范外的其他现行国家、行业及地方相关规范标准。上述规范如有最新版本和新的相关规范和标准，则按最新的和新增加相关规范和标准执行。

- 2.2. 建设方提供的项目基础资料，包括但不限于东安书院原始图纸、成都第 31 届世界大学生夏季运动会视觉标准手册、成都大运会电气运行导则、成都第 31 届世界大学生夏季运动会场馆媒体中心媒体工作间指导意见、第 31 届世界大学生夏季运动会主媒体中心运行实施总体方案、新华社新闻信息服务团队 MPC 办公需求。
- 2.3. 在项目设计过程中建设方提出的条件、意见和要求，以及建设方对各阶段设计图纸的评审意见、会议纪要等。
- 2.4. 双方签定的设计合同内所包含的服务性条款及要求。
- 2.5. 设计任务书。
- 2.6. 未详细提及之处均应按照国家与地方有关法规、规范进行设计。
- 2.7. 材料标准

2.7.1. 乳胶漆

- 执行的国家规范、标准（国家、行业、地方标准）
- 《建筑用外墙涂料中有害物质限量》GB 24408-2009
- 《色漆和清漆低 VOC 乳胶漆中挥发性有机化合物（罐内 VOC）含量的测定》GB/T 23984-2009
- 《乳胶漆耐冻融性的测定》GB/T 9268-2008
- 《建筑内外墙用底漆》JG/T 210-2007
- 《合成树脂乳液内墙涂料》GB/T 9756-2009
- 《室内装饰装修材料内墙涂料中有害物质限量》GB/18582-2008
- 《环境标志产品技术要求水性涂料》HJ2537-2014

2.7.2. 矿棉板、穿孔矿棉吸音板

- 执行的国家规范、标准（国家、行业、地方标准）
- 除另有注明外，本材料须符合国家、地方、及行业标准，主要包括但不限于：
- GB/T 5480-2008 《矿物棉及其制品试验方法》
- GB/T 25998-2010 《矿物棉装饰吸声板》
- GB/T 26746-2011 《矿物棉喷涂绝热层》

设计总说明（一）

- GB 6566-2010 《建筑材料放射性核素限量》
- GB 8624-2012《建筑材料及制品燃烧性能分级》
- GB/T 10294-2008 《绝热材料稳态热阻及有关特性的测定防护热板法》
- GB/T 10295-2008 《绝热材料稳态热阻及有关特性的测定热流计法》
- GB/T 17657-2013 《人造板及饰面人造板理化性能试验方法》
- GB/T 18696.1-2004 《声学阻抗管中吸声系数和声阻抗的测量》
- GB/T 20247-2006 《声学混响室吸声测量》
- GB/T 20313-2006 《建筑材料及制品的湿热性能》
- HJ/T 206-2005 《环境产品的技术要求无石棉建筑制品》
- GB50354-2005 《建筑内部装修防火施工及验收规范》
- GB18580-2001 《室内装饰装修材料人造板及其制品中甲醛释放限量》
- GB50325-2010 《民用建筑工程室内环境污染控制规范》

2.7.3. 纸面石膏板

- 执行的国家规范、标准（国家、行业、地方标准）
- GB/T 26204-2010 《纸面石膏板护面纸板》
- GB/T 9775-2008 《纸面石膏板》
- JC/T 2077-2011 《复合保温石膏板》
- JC/T 443-2007《纸面石膏板护面纸》
- JC/T 799-2007 《装饰石膏板》
- JC/T 800-2007《嵌装式装饰石膏板》
- JC/T803-2007 《吸声穿孔石膏板》
- JC/T997-2006 《装饰纸面石膏板》
- QB/T2699-2005 《纸面石膏板面纸板》
- 07CJ03-1《轻钢龙骨石膏板隔墙、吊顶》
- 07SJ507《轻钢龙骨布面石膏板、布面洁净布隔墙及吊顶》

2.7.4. 穿孔铝板、铝单板

- 执行的国家规范、标准（国家、行业、地方标准）
- 除另有注明外，本材料须符合国家、地方、及行业标准，主要包括但不限于：
- 铝板带国家标准（GB/T 3880-2006）

2.7.5. PVC 地板

- 执行的国家规范、标准（国家、行业、地方标准）
- 除另有注明外，本材料须符合国家、地方、及行业标准，主要包括但不限于：
- 《半硬质聚氯乙烯块状地板》 GB/T4085-2005
- 《建筑材料及制品燃烧性能分级》 GB8624-2006

2.7.6. 人造石

- 执行的国家规范、标准（国家、行业、地方标准）
- 除另有注明外，本材料须符合国家、地方、及行业标准，主要包括但不限于：
- JC/T 908-2013 《人造石》
- GB/T 3352-2012 《人造石英晶体规范与使用指南》
- JG/T 463-2014 《建筑装饰用人造石英石板》

- EN 14617-16：2005 《人造合成石试验方法第 16 部分：尺寸的测定，几何特性和模块化的瓷砖表面质量》
- EN14617-1：2013 《烧结石料. 试验方法. 表观密度和吸水率的测定》
- EN14617-2：2008 《烧结石料. 试验方法. 第 2 部分：挠性强度（挠度的测定）》
- EN14617-10：2012 《烧结石料. 试验方法. 第 10 部分：耐化学性测定》
- GB 6566-2010 《建筑材料放射性核素限量》
- JC/T 2300-2014《人造石加工、装饰与施工质量验收规范》

JC/T 2325-2015 《异型人造石制品》

2.7.7. 木地板

- 执行的国家规范、标准（国家、行业、地方标准）：
- GB/T 18103-2013 《实木复合地板》
- GB 50206-2012 《木结构工程施工质量验收规范》
- GB18580-2001 《室内装饰装修材料人造板及其制品中甲醛释放限量》
- WB/T1017-2006 《木地板保修期内面层检验规范》
- GB 50222-1995 《建筑内部装修设计防火规范》
- WBT 1050-2012 《木地板铺设辅料》
- WBT 1016-2002 《木地板铺设面层验收规范》
- LYT 1738-2008 《实木复合地板用胶合板》
- GBT 24509-2009 《阻燃木质复合地板》

2.7.8. 不锈钢

- 执行的国家规范、标准（国家、行业、地方标准）
- 除另有注明外，本材料须符合国家、地方、及行业标准，主要包括但不限于：

出图记录		ISSUE NOTES
版 本	日 期	备 注
REV.	DATE	REMARK
A	2022.02	
注册执业栏		REGISTERED ARCHITECT/ENGINEER
姓 名		NAME
注册证书号码		REGISTRATION CERTIFICATE NO.
注册印章号码		STAMP NO.
设计号: CD-20212856-F001		JOB NO.
工程名称		PROJECT TITLE
成都大运会主新闻中心装饰搭建		
子项名称		SUB ITEM
建设单位:		CLIENT
成都博雅文瑞文化传播有限公司		
图 名		DRAWING TITLE
设计总说明(一)		
单 位	mm	UNIT
图 别	室 施	DWG. CATEGORY
比 例	—	SCALE
图 号	N02	DWG. NO.
日 期	2022.02	DATE
版 本	A	VER. NO.
制 图	方 苓	
DRAWN BY		
设 计	方 苓	
DESIGNED BY		
校 对	李 肅 文	
CHECKED BY		
专业负责人	肖子颖	
DISCIPLINE CHIEF		
设计总负责人	张 峻	
PROJECT CHIEF		
审 核	张 峻	
AUDIT		
审 定	华 柯	
APPROVED BY		
成都基准方中		
成都基准方中建筑设计股份有限公司		
Chengdu JZfz Architectural Design Co., Ltd.		
中国 成都市 琉璃路8号华润广场A座7-15楼		
电话: +86 (28) 86333800 传真: +86 (28) 86582990		
7-15F, Tower A, Citland Plaza, No.8, Luli Road , Chengdu, P.R.C		
tel. +86(28) 86333800 fax. +86(28) 86582990		
工程设计资质证书编号: A151016191		
电子文档编号: —		CAD FILENAME
版 权 说 明		
COPYRIGHT DECLARATION		
此图版权为成都基准方中建筑设计股份有限		
公司所有, 未经许可不得使用。		

[illegible]

出图记录							ISSUE NOTES					
版 本 REV.		日 期 DATE		备 注 REMARK								
A		2022.02										
注册执业栏 REGISTERED ARCHITECT/ENGINEER												
姓 名NAME												
注册证书号码REGISTRATION CERTIFICATE NO.												
注册印章号码STAMP NO.												
设计号：CD-20212856-F001JOB NO.												
工程名称PROJECT TITLE												
成都大运会主新闻中心装饰搭建												
子项名称SUB ITEM												
建设单位CLIENT												
成都博雅文瑞文化传播有限公司												
图 名DRAWING TITLE												
设计总说明(二)												
单 位mmUNIT		图 别图 施DWG. CATEGORY										
比 例—SCALE		图 号NO3DWG. NO.										
日期2022.02DATE		版本AVER. NO.										
制 图DRAWN BY		方岑										
设 计DESIGNED BY		方岑										
校 对CHECKED BY		李翔文										
专业负责人DISCIPLINE CHIEF		肖子颖										
设计总负责人PROJECT CHIEF		张峻										
审 核AUDIT		张峻										
审 定APPROVED BY		华轲										
 基准方中 成都基准方中建筑设计股份有限公司 Chengdu JZFW Architectural Design Co., Ltd.												
中国 成都市 琉璃路8号华润广场A座7-15楼 电话：+86(28) 86333800 传真：+86(28) 86582990 7-15F, Tower A, Crand Plaza, No.8,LinLi Road , Chengdu, P.R.C tel. +86(28) 86333800 fax. +86(28) 86582990												
工程设计资质证书编号：A151016191												
CAD FILENAME												
电 子 文 档 编 号： —												
版 权 说 明 COPYRIGHT DECLARATION												
此图版权为成都基准方中建筑设计股份有限公司所有，未经许可不得使用。												

合 格 栏	建 筑		电 气		采暖通风	
	结 构		给排水		总 图	

设计总说明（三）

- 5.2.3.2. 安装框顶部限位槽:限位槽的宽应大于门框厚度 2-4mm,槽深为 10-20mm。安装时,先由所弹中凡线引出两条金属装饰板边线,然后按边线进行门框顶部限位槽的安装。
- 5.2.3.3. 安装金属饰面的木底托:先把方木固定在地面上,然后再用万能胶将金属饰面板粘在木上,方木可采用直接钉在预埋木砖上,或通过膨胀螺栓连接的方法固定。
- 5.2.3.4. 安装竖向门框:按所弹中心线钉立门框方木,然后用胶合板确定门框柱的外形和位置,最后外包金属饰面。
- 5.2.3.5. 安装发光门:由 2-3 人将厚玻璃板抬起,移至安装位置。
- 5.2.3.6. 固定门体:在底托方木上的内外钉两根小方木条把门定住,方木条距门板面 4mm 左右,然后在方木条上涂刷万能胶,将饰面金属粘卡在方木条上。
- 5.2.3.7. 注胶封口:在顶部限位槽和底部托槽口的两侧,以及门框柱的对缝处等各缝隙处,注入玻璃胶封口。

5.3. 西入口总服务台

5.3.1. 背景墙、服务台施工:

- 5.3.1.1. 墙体基础结构参照前面西入口区域。
- 5.3.1.2. 墙面要平整，可以是水泥墙，石膏板墙，腻子墙，油漆墙，木板墙等，甚至平整的瓷砖或者玻璃上都可

- 5.3.1.3. 哑光可移黑胶张贴首次安装要先根据图纸，在地上拼一次，拼的完整了之后再开始上墙贴；
- 5.3.1.4. 用中性透明玻璃胶涂抹几点在每块哑光可移黑胶张贴背后（切记不要涂满）面积过大的，背面可再贴几条质双面胶，然后贴到墙上，一支玻璃胶可以贴 1-2 平米，有金属件的直接用热熔胶粘就可以了。
- 5.3.1.5. 发光字体参照前面西入口区域

5.3.2. 顶部格栅施工:

- 5.3.2.1. 首先应弹出标高线、造型位置线、吊挂点布局线和灯具安装位置线。格栅顶部吊点固定有两种方法：一种是用直径 5 毫米以上的射钉直接将角铁或扁铁固定在顶部。另一种是在顶部打眼，用膨胀螺栓固定铁件或木方做吊点。都应保证吊点牢固、安全。格栅吊顶安装完毕，应进行质量检测与验收，才可进行饰面板的安装，格栅吊顶饰面要求板面平整，无凹凸，无断裂，边角整齐。饰面板的安装方法主要有圆钉固定法和木螺丝固定法两种，其中圆钉固定法主要用于木材饰面板安装，施工速度快；木螺丝固定法主要用于石膏板饰面板，以提高板材执钉能力。
- 5.3.2.2. 安装饰面板应与墙面完全吻合，有装饰角线的可留有缝隙，饰面板之间接缝应紧密。
- 5.3.2.3. 吊顶时应在安装饰面板时预留出灯口位置。饰面板安装完毕，还需进行饰面的终饰作业，常用的材料为乳胶漆及壁纸，其施工方法同墙面施工。
- 5.3.3. 吊顶灯箱施工：
- 5.3.3.1. 使用方管焊接龙骨。不容易容易导致结构变形。
- 5.3.3.2. 施工中注意伸缩缝。每道接缝处都应留有伸缩缝，并倒成 45 度角，以免应力累积。
- 5.3.3.3. 龙骨安装平整，间距规范。
- 5.3.3.4. 自攻钉要均匀分布，保证每颗自攻钉承受的力接近，否则易形成边锁反应使结构失去稳定性而产生变形开裂。

- 5.3.3.5. 在龙骨上设过渡连接件,以便调整理件误差,可与理件钉、焊、拧穿。吊杆、吊索与过渡连接件连接。
- 5.3.3.6. 吊杆、吊索直接钉、拧于次搁栅上,或采用上述板面穿孔的方法连接在立润栅上。或吊于次搁栅间另加的上。

5.3.4. 书架施工施工:

- 5.3.4.1. 根据设计书架的图纸尺寸要求，在施工现场进行放线定位，如发现图纸尺寸与施工现场尺寸不符，必须以现场进行调整的为准。
- 5.3.4.2. 书架的用料材质：亚克力板，竖板:2.44m*0.4m*2cm 厚*23 块；横板：2.44m*0.235m*1cm 厚*12 块。
- 5.3.4.3. 书架在施工制作过程中尽量减少钉眼，表面没有胶水、无污痕。保证书柜表面清洁。切不可将饰面板的木皮刨掉。

5.4. 休息大厅

5.4.1. 透明灯箱

- | | |
|----------|--|
| 5.4.1.1. | 用 M10*160*4 的化学锚栓把 80*80*6mm 的钢板与建筑物外墙固定, 把箱体焊接在 80*80*6mm 的预埋钢板上。 |
| 5.4.1.2. | 先对箱体钢架做除锈处理, 然后刷两遍防锈漆灯箱侧立墙板的固定方法 |
| 5.4.1.3. | 灯箱四周的侧立墙板用 1.2mm 厚的 304 拉丝不锈钢机压成型, 用不锈钢螺丝把侧立墙板固定在侧面的方管框架上 |
| 5.4.1.4. | 对箱体和墙体之间的连接处做防水处理。 |
| 5.4.1.5. | 做好防漏电及接地处理。 |

5.4.2. 红墙标语立体字施工

- 5.4.2.1. 安装字体：龙骨安装完后进行隐蔽工程验收，由工厂加工完成的字体运至工地后，进行分层分块充分考虑安装先后顺序问题，把检查合格的铝板分配至各层的每个安装部位，横料竖料安装完成后即可挂贴已经做好铝塑板块。节点调整系统的安装依靠铝型材的配合，严格控制安装尺寸，同时控制板块位置使之达到最佳，并确保接缝之间的间隙。
- 5.4.2.2. 打胶、清洁与保养：板块安装完毕后在缝中嵌入泡沫条，进行打胶，胶缝要求均匀一致，表面光滑。

5.4.3. 波纹压克力隔断

- 5.4.3.1. 现场测量放线：施工前需对现场高度测量，根据二次设计及工艺要求对隔墙进行放线，按照净化间内施工基准线，用盘尺测量确定地轨位置并画点使用尼龙线与 3M 胶带连成线，然后用线坠或返点仪将墙体位置返至顶上。
- 5.4.3.2. 亚克力安装：亚克力板安装前，需将地轨里的灰尘和杂物用吸尘器清理干净。安装亚克力板时，应从下向

上安装,将亚克力板插入龙骨槽内后安装横龙骨并使用连接件锁紧,在竖向亚克力板安装完成后安装另一侧竖龙骨。安装工序以此类推。

- 5.4.3.3. 收边:力求整齐一致,连接处要求无缝隙,与天轨及转角接口处尤其注意,更做到没有缝隙。
- 5.4.3.4. 地龙骨打胶:亚克力板隔墙施工完成后使用中性密封胶(有特殊要求时使用无硅密封胶)对地龙骨进行打

5.5. 媒体餐厅墙面导视标识

5.5.1 哑光可移黑胶张贴双面技术要求:反光标识在逆反射性能及均匀性,耐候性能,耐盐雾腐蚀性能,抗溶剂性能,抗冲击性能,耐温性能,附着性能,耐水性能,耐弯曲性能等方面均应满足公共安全行业标准《车身反光标识》GA406—2002)要求。

5.5.2 亚克力标牌加工的要求:亚克力出模热弯成形,尺寸及形状一致,表面无气泡及划痕。热弯成形后表面经过粗砂、细砂、碾磨处理,保证其表面平滑无台阶。完成后表面光泽柔和均匀、无颗粒状物、无气泡、透光均匀。

5.5.3. 不锈钢工艺要求：不锈钢板须刨坑折弯焊接（不锈钢板须先刨坑后折弯，以保证边缘挺拔度）；保证折弯处圆弧角 $R < 1\text{mm}$ 。焊接前清除表面油污，减少焊缝形成的虚焊、气孔、裂纹等缺陷。焊接完后将所有可见焊缝打磨光滑，与周围表面一样平滑，无明显划痕。

5.5.4. 完工外观要求:安装完成后标识牌外观精美,表面无螺钉,无划痕、气泡及明显的颜色不均匀,烤漆须无明显色差,所用材料符合设计方案要求。标牌安装方式易方便面板更换及维护。

5.6. 报告厅外围

5.6.1. 熊猫厅门、墙体施工

- 5.6.1.1. 墙面要求平整。如墙面平整误差在 10 毫米以内,可采取抹灰修整的办法;如误差大于 10 毫米,可在墙面与龙骨之间加垫木块。
- 5.6.1.2. 根据护墙板高度和房间大小钉做经骨,整片或分片安装,在墙裙底部安装踢脚板,将踢脚板固定在垫木及墙板上,踢脚板高度 150 毫米,冒头用木线条固定在护墙板上。
- 5.6.1.3. 根据面板厚度确定龙骨间尺寸,横龙骨一般在 400 毫米左右,竖龙骨一般在 600 毫米。面板厚度 1 毫米以上时,横龙骨间距可适当放大。

- 5.6.1.4. 墙裙安装后,应立即进行饰面处理,涂刷清油一遍,以防止其他工种污染板面。
- 5.6.1.5. 装饰墙体安装:
- 5.6.1.6. 安装工序流程:测量、放线→清除基体→安装固定墙体→自检→清洁
- 5.6.1.7. 按照设计在基体上确定安装位置,使用水平仪和标准钢卷尺等引出标高线。
- 5.6.1.8. 测量时误差不能超过 $\pm 2\text{ mm}$
- 5.6.1.9. 用羊毛刷清楚表面灰尘,若有油物用酒精擦拭。
- 5.6.1.10. 安装中先用确定墙体位置,确定横平竖直后在进行墙体的固定固定。
- 5.6.1.11. 哑光可移黑胶车贴双面技术要求:反光标识在逆反射性能及均匀性,耐候性能,耐盐雾腐蚀性能,抗溶剂

性能,抗冲击性能,耐温性能,附着性能,耐水性能,耐弯曲性能等方面均应满足公共安全行业标准《车身反光标识》GA406—2002)要求。

- 5.6.1.12. 美工字 PVC: 将喷绘撕开底纸 2—5 厘米, 折叠底纸然后将其沿板材的边缘对齐, 用干布轻轻压下使其与板面紧密贴合。左手置于喷绘下方轻轻掀起折叠的底纸, 右手用干布上下擦动, 用力均匀, 直到粘贴完毕 (一般这种贴法叫干贴)。若宽底纸超过 1 米就需两人合作粘贴将其完成, 水贴是将底板和撕下底纸后喷绘背面洒上洗衣粉水或洗洁净水, 然后用布包好的刮板进行刮平。

5.7. 南入口服务台

5.7.1. 顶部

- 5.7.1.1. 首先应弹出标高线、造型位置线、吊挂点布局线和灯具安装位置线。
- 5.7.1.2. 格栅顶部吊点固定有两种方法：一种是用直径 5 毫米以上的射钉直接将角铁或扁铁固定在顶部。另一种是在顶部打眼，用膨胀螺栓固定铁件或木方做吊点。都应保证吊点牢固、安全。
- 5.7.1.3. 格栅吊顶安装完毕，应进行质量检测与验收，才可进行饰面板的安装。
- 5.7.1.4. 格栅吊顶饰面要求板面平整，无凹凸，无断裂，边角整齐。
- 5.7.1.5. 饰面板的安装方法主要有圆钉固定法和木螺丝固定法两种，其中圆钉固定法主要用于木材饰面板安装，施工速度快；木螺丝固定法主要用于石膏板饰面板，以提高板材执钉能力。

- 5.7.1.6. 安装饰面板应与墙面完全吻合,有装饰角线的可留有缝隙,饰面板之间缝应严密。
- 5.7.1.7. 吊顶时应在安装饰面板时预留出灯口位置。饰面板安装完毕,还需进行饰面的终饰作业,常用的材料为乳胶漆。

漆及壁纸,其施工方法同墙面施工。

5.7.2. 总服务台吊顶灯箱、大运会刊物吊顶灯箱

- 5.7.2.1. 使用方管焊接龙骨。容易导致结构变形，工中注意伸缩缝。每道接缝处都应留有伸缩缝，并倒成 45 度角，以免应力累积。龙骨安装平整，间距规范，攻钉要均匀分布，保证每颗自攻钉承受的力接近，否则易形成连锁反应使结构失去稳定性而产生变形裂缝，龙骨上设过渡连接件，以便调整零件误差，可与埋件钉、焊、拧、穿。吊杆、吊索与过渡连接件连接，杆、吊索直接钉、拧于次搁栅上，或采用上述板面穿孔的方法连接在主搁栅上。或吊于次搁栅间另加的十字搁栅上。

5.8. 南入口东服务台

5.8.1. 背景墙、服务台施工:

- 5.8.1.1. 墙体基础结构参照前面西入口区域。墙面要平整，可以是水泥墙，石膏板墙，腻子墙，油漆墙，木工板墙等，甚至平整的瓷砖或者玻璃上都可以贴；哑光可移黑胶车贴首次安装要先根据图纸，在地上拼一次，拼的完整了之后再开始上墙贴；用中性透明玻璃胶涂抹几点在每块哑光可移黑胶车贴背后（切记不要涂满）面积过大的，背面可再贴几条 2MM 厚棉质双面胶，然后贴到墙上，一支玻璃胶可以贴 1-2 平米，有金属件的直接用热熔胶粘就可以了。发光字体参照前面西入口区域

5.9. 南入口西服务台

[illegible]

注册执业栏		REGISTERED ARCHITECT/ENGINEER	
姓 名	NAME		
注册证书号码	REGISTRATION CERTIFICATE NO.		
注册印章号码	STAMP NO.		
设计号	CD-20212856-F001	JOB NO.	
工程名称	PROJECT TITLE		
成都大运会主新闻中心装饰搭建			
子项名称	SUB ITEM		

建设单位:		CLIENT	
成都博雅文瑞文化传播有限公司			
图 名		DRAWING TITLE	
设计总说明(三)			
单 位	mm	UNIT	图 别 室 施
比 例	—	SCALE	图 号: NO4
日 期	2022.02	DATE	版 本 A
			VER. NO.

制图 DRAWN BY	方苓	
设计 DESIGNED BY	方苓	
校对 CHECKED BY	李璐文	
专业负责人 DISCIPLINE CHIEF	肖子颖	
设计总负责人 PROJECT CHIEF	张峻	
审核 AUDIT	张峻	
审定 APPROVED BY	华柯	

中 方 基 准	
成都基准方中建筑设计股份有限公司 Chengdu JZFC Architectural Design Co., Ltd.	
中国 成都市 琉璃场8号华润广场A座7-15楼 电话: +86(28) 86333800 传真: +86(28) 86582990 7-15F, Tower A, Ctrland Plaza, No.8,Liuli Field, Chengdu, P.R.C tel. +86(28) 86333800 fax. +86(28) 86582990	
工程设计资质证书编号: A151016191	
电子文档编号: - CAD FILENAME	
版 权 说 明 COPYRIGHT DECLARATION	
此图版权归成都基准方中建筑设计股份有限公司所有, 未经许可不得使用。	

采暖通风	图	号	
电	气	水	给排水
筑	构		
建			
筑			

5.9.1. 背景墙、服务台施工：

墙体基础结构参照前面西入口区域，面要平整，可以是水泥墙，石膏板墙，腻子墙，油漆墙，木工板墙等，甚至平整的瓷砖或者玻璃上都可以贴;哑光可移黑胶车贴首次安装要先根据图纸，在地上拼一次，拼的完整了之后再开始上墙贴；

5.9.2. 背景墙正面美工

PVC 雕刻字施工要点被涂表面应平整、干燥、无污物及松脱附着物。基层不平处可用外墙耐水腻子刮平，建水泥墙面应充分干燥后，涂刷水性封底漆一遍，旧涂层的墙面，应将已粉化剥落的漆膜清除干净，再涂以适当水性封底漆一遍。泛碱严重的水泥基层，应将其表面的渗出物清洗干净，待完全干燥后涂以高渗透底漆一遍涂料配套:建议使用水性抗碱外墙底漆，有利于封闭墙面碱性，提高面漆附着力和表面效果。涂料配套:使用前必须充分搅拌均匀。太稠时，可酌情加水调节，以不超过规定用量为原则。无气喷涂加水量为 0~5%。

5.9.3. 电路铺设

设计布线时，执行强电走上，弱电走下，横平竖直，避免交叉，美观实用的原则。开槽深度应一致，一般是 PVC 管直径大于 1cm 左右深入墙面 5cm 左右，电源线配线时，所有等线截面积应满足用电设备的输出功率，一般情况照时 1.5 或 2.5 平方，空调挂机插座 2.5 平方，空调、厨房、浴房热水器 4 平方米，进户 10 平方，暗线铺设，必须配阻 PVC 管，正常插座用平方管，照明 3 分管，当管径长度超过 15 米或有两个直角弯头时，增设拉线盒，开棚的灯具位置设拉线盒固定，PVC 管应用卡固定，PVC 农牧民接头均用配套接头，用 PVC 润色水粘牢，弯头均用弹簧弯曲暗盒与 PVC 管用锣接固定，PVC 管安装好后，统一穿电线，同一回路电线应穿入同一根管内，但管内总根数不应超过 4 分管 5 根，3 分管 3 根，电线管总截面积（包括绝缘外皮）不应超过管内截面积的 40%必须分色，导线不应直接头扭线现象。

5.10. 拆除与恢复

拆除工程施工细则由施工单位自行拟定，需确保安全环保，并对搭建过程中破坏的界面按原始接收状态进行恢复，场馆提供方认可的无需恢复的部分除外。

6. 施工注意事项

- 6.1. 在施工前应对设计图纸进行必要的校对，发现的问题应及时通知设计解决。
- 6.2. 本工程在施工过程中，施工单位应严格按照施工图尺寸进行施工。施工过程中应遵循先放样后施工的原则，墙地面同为石材或砖的区域，原则上应采取墙、地对缝。重点空间施工单位应根据图纸排布原则，根据现场实际尺寸进行放样排版，排版图经设计单位认可后，方可安排下料进货施工。遇到现场尺寸与图纸尺寸不符处，应针对现场尺寸与施工图进行调整，并及时通知设计单位，提出相应解决措施，在设计单位同意后做相应调整，不得以丈量图纸为依据取得数据。
- 6.3. 所有装修材料在施工前，施工单位应按设计要求组织实物选择。在建设单位、设计单位、监理单位三方共同确定选择、封样后方可供货施工。
- 6.4. 施工过程中，建设单位如因工程造价或其他原因欲对设计施工图纸进行更改，应召集设计单位共同协调，达成一致意见并由建设单位发文，由设计单位对相关图纸进行调整，并以修改设计通知单或升版图纸的方式交付建设单位，由建设单位下发，施工单位方可进行施工；施工单位不能擅自更改装修材料、装修造型以及安装方式。
- 6.5. 施工过程中，如遇到现场实际困难无法按设计施工图纸施工的情况，须由施工单位提前上报建设单位和设计单位，并解决相关事宜，否则设计不承担相关责任。
- 6.6. 所有隐蔽钢构件及露明吊挂、支撑钢杆件、预埋件等铁件均应为镀锌钢件或做防锈处理，（镀锌或刷防锈漆三道。不锈钢除外。防锈漆需选用配套的防锈底漆，防锈底漆应当在彻底，除锈之后再刷，镀锌主龙骨涂层平均厚度不低于 85um,横梁镀锌涂层平均厚度不低于 70um。
- 6.7. 现场手工电弧焊接用 E431X 系列碳素钢焊条应符合《非合金钢及细晶粒钢焊条》(GB/15117-2012)的要求。
- 6.8. 承重结构采用的钢材应具有抗拉强度，伸长率，屈服强度和硫磷含量的合格保证，对焊接结构尚应具有含碳量的合格保证。焊接承重结构以及重要的非焊接承重结构采用的钢材还应具有冷弯试验的合格保证。
- 6.9. 所有木装修均需事先在板背及龙骨上按规范要求涂刷防火涂料三遍。

7. 单位尺寸专业代码

- 7.1. 本施工图所标注尺寸单位为毫米，标高单位为米；
- 7.2. 本图所示尺寸与现场尺寸不符时，均以现场尺寸复核为准。

8. 图纸代码含义表


序号	含义	代码
1	图纸目录与设计说明	N
2	平面布置图	D
3	地面铺装图	F
4	天花、灯具布置图	C
5	放大平面图	M
6	立面图	E
7	大样图	D

设计总说明（四）

9. 主要材料性能及燃烧等级说明表

空间	部位	材料	规格参数	防火等级
一层整体	地面	圈绒地毯		B1
负一层二次缓冲区	隔断	轻钢龙骨		A
		阻燃胶合板	5mm-18mm 厚	B1
		热镀锌方矩管		A
负一层厨房及工作间	隔断	轻钢龙骨		A
		阻燃胶合板	5mm-18mm 厚	B1
		热镀锌方矩管		A
		普通纸面石膏板	9.5mm 厚	B1
一层新闻发布厅	吊顶	钢板网		A
	隔墙	轻钢龙骨		A
		阻燃胶合板	5mm-18mm 厚	B1
		聚酯纤维吸音板		B1
		普通纸面石膏板	9.5mm 厚	B1
		热镀锌方矩管		A
		玻璃棉板	100 厚	A
	地台	木框架		B2
	舞台	热镀锌方矩管		A
		阻燃胶合板	5mm-18mm 厚	B1
	摄像台	热镀锌方矩管		A
		阻燃胶合板	5mm-18mm 厚	B1
一层媒体工作间	隔断	轻钢龙骨		A
		阻燃胶合板	5mm-18mm 厚	B1
	墙面	木龙骨		B2
一层新华社专用	隔断	轻钢龙骨		A
		阻燃胶合板	5mm-18mm 厚	B1
		玻璃棉板	100 厚	A
		聚酯纤维吸音板		B1
		普通纸面石膏板	9.5mm 厚	B1
一层无线电工作间	隔断	轻钢龙骨		A
		阻燃胶合板	5mm-18mm 厚	B1
		普通纸面石膏板	9.5mm 厚	B1
一层公共区域	墙面	木龙骨		B2
		阻燃胶合板	5mm-18mm 厚	B1
二层整体	地面	圈绒地毯		B1
二层媒体工作间	隔断	轻钢龙骨		A
		阻燃胶合板	5mm-18mm 厚	B1
		热镀锌方矩管		A
二层餐厅	墙面	普通纸面石膏板	9.5mm 厚	B1
		木龙骨		B2
		阻燃胶合板	5mm-18mm 厚	B1
三层整体	地面	圈绒地毯		B1

出图记录		ISSUE NOTES
版 本	日 期	备 注
REV.	DATE	REMARK
A	2022.02	
注册执业栏		REGISTERED ARCHITECT/ENGINEER
姓 名		NAME
注册证书号码		REGISTRATION CERTIFICATE NO.
注册印章号码		STAMP NO.
设计号: CD-20212856-F001		JOB NO.
工程名称		PROJECT TITLE
成都大运会主新闻中心装饰搭建		
子项名称		SUB ITEM
建设单位		CLIENT
成都博雅文瑞文化传播有限公司		
图 名		DRAWING TITLE
设计总说明(四)		
单 位	mm	UNIT
图 别	室 施	DWG. CATEGORY
比 例	-	SCALE
图 号	N05	DWG. NO.
日 期	2022.02	DATE
版 本	A	VER. NO.
制 图	方 苓	
DESIGNED BY	方 苓	
校 对	李 灏 文	
CHECKED BY	李 灏 文	
专业负责人	肖子顺	
DISCIPLINE CHIEF		
设计总负责人	张 竣	
PROJECT CHIEF		
审 核	张 竣	
AUDIT	张 竣	
审 定	华 柯	
APPROVED BY	华 柯	
国 基准方中		
成都基准方中建筑设计股份有限公司		
Chengdu JZfz Architectural Design Co., Ltd.		
中国 成都市 琉璃路8号华润广场A座7-15楼		
电话：+86 (28) 86333800 传真：+86 (28) 86582990		
7-15F, Tower A, Crland Plaza, No.8, Liuli Road , Chengdu, P.R.C		
tel. +86(28) 86333800 fax. +86(28) 86582990		
工程设计资质证书编号： A151016191		
电子文档编号： -		
CAD FILENAME		
版 权 说 明		
COPYRIGHT DECLARATION		
此图版权为成都基准方中建筑设计股份有限		
公司所有，未经许可不得使用。		

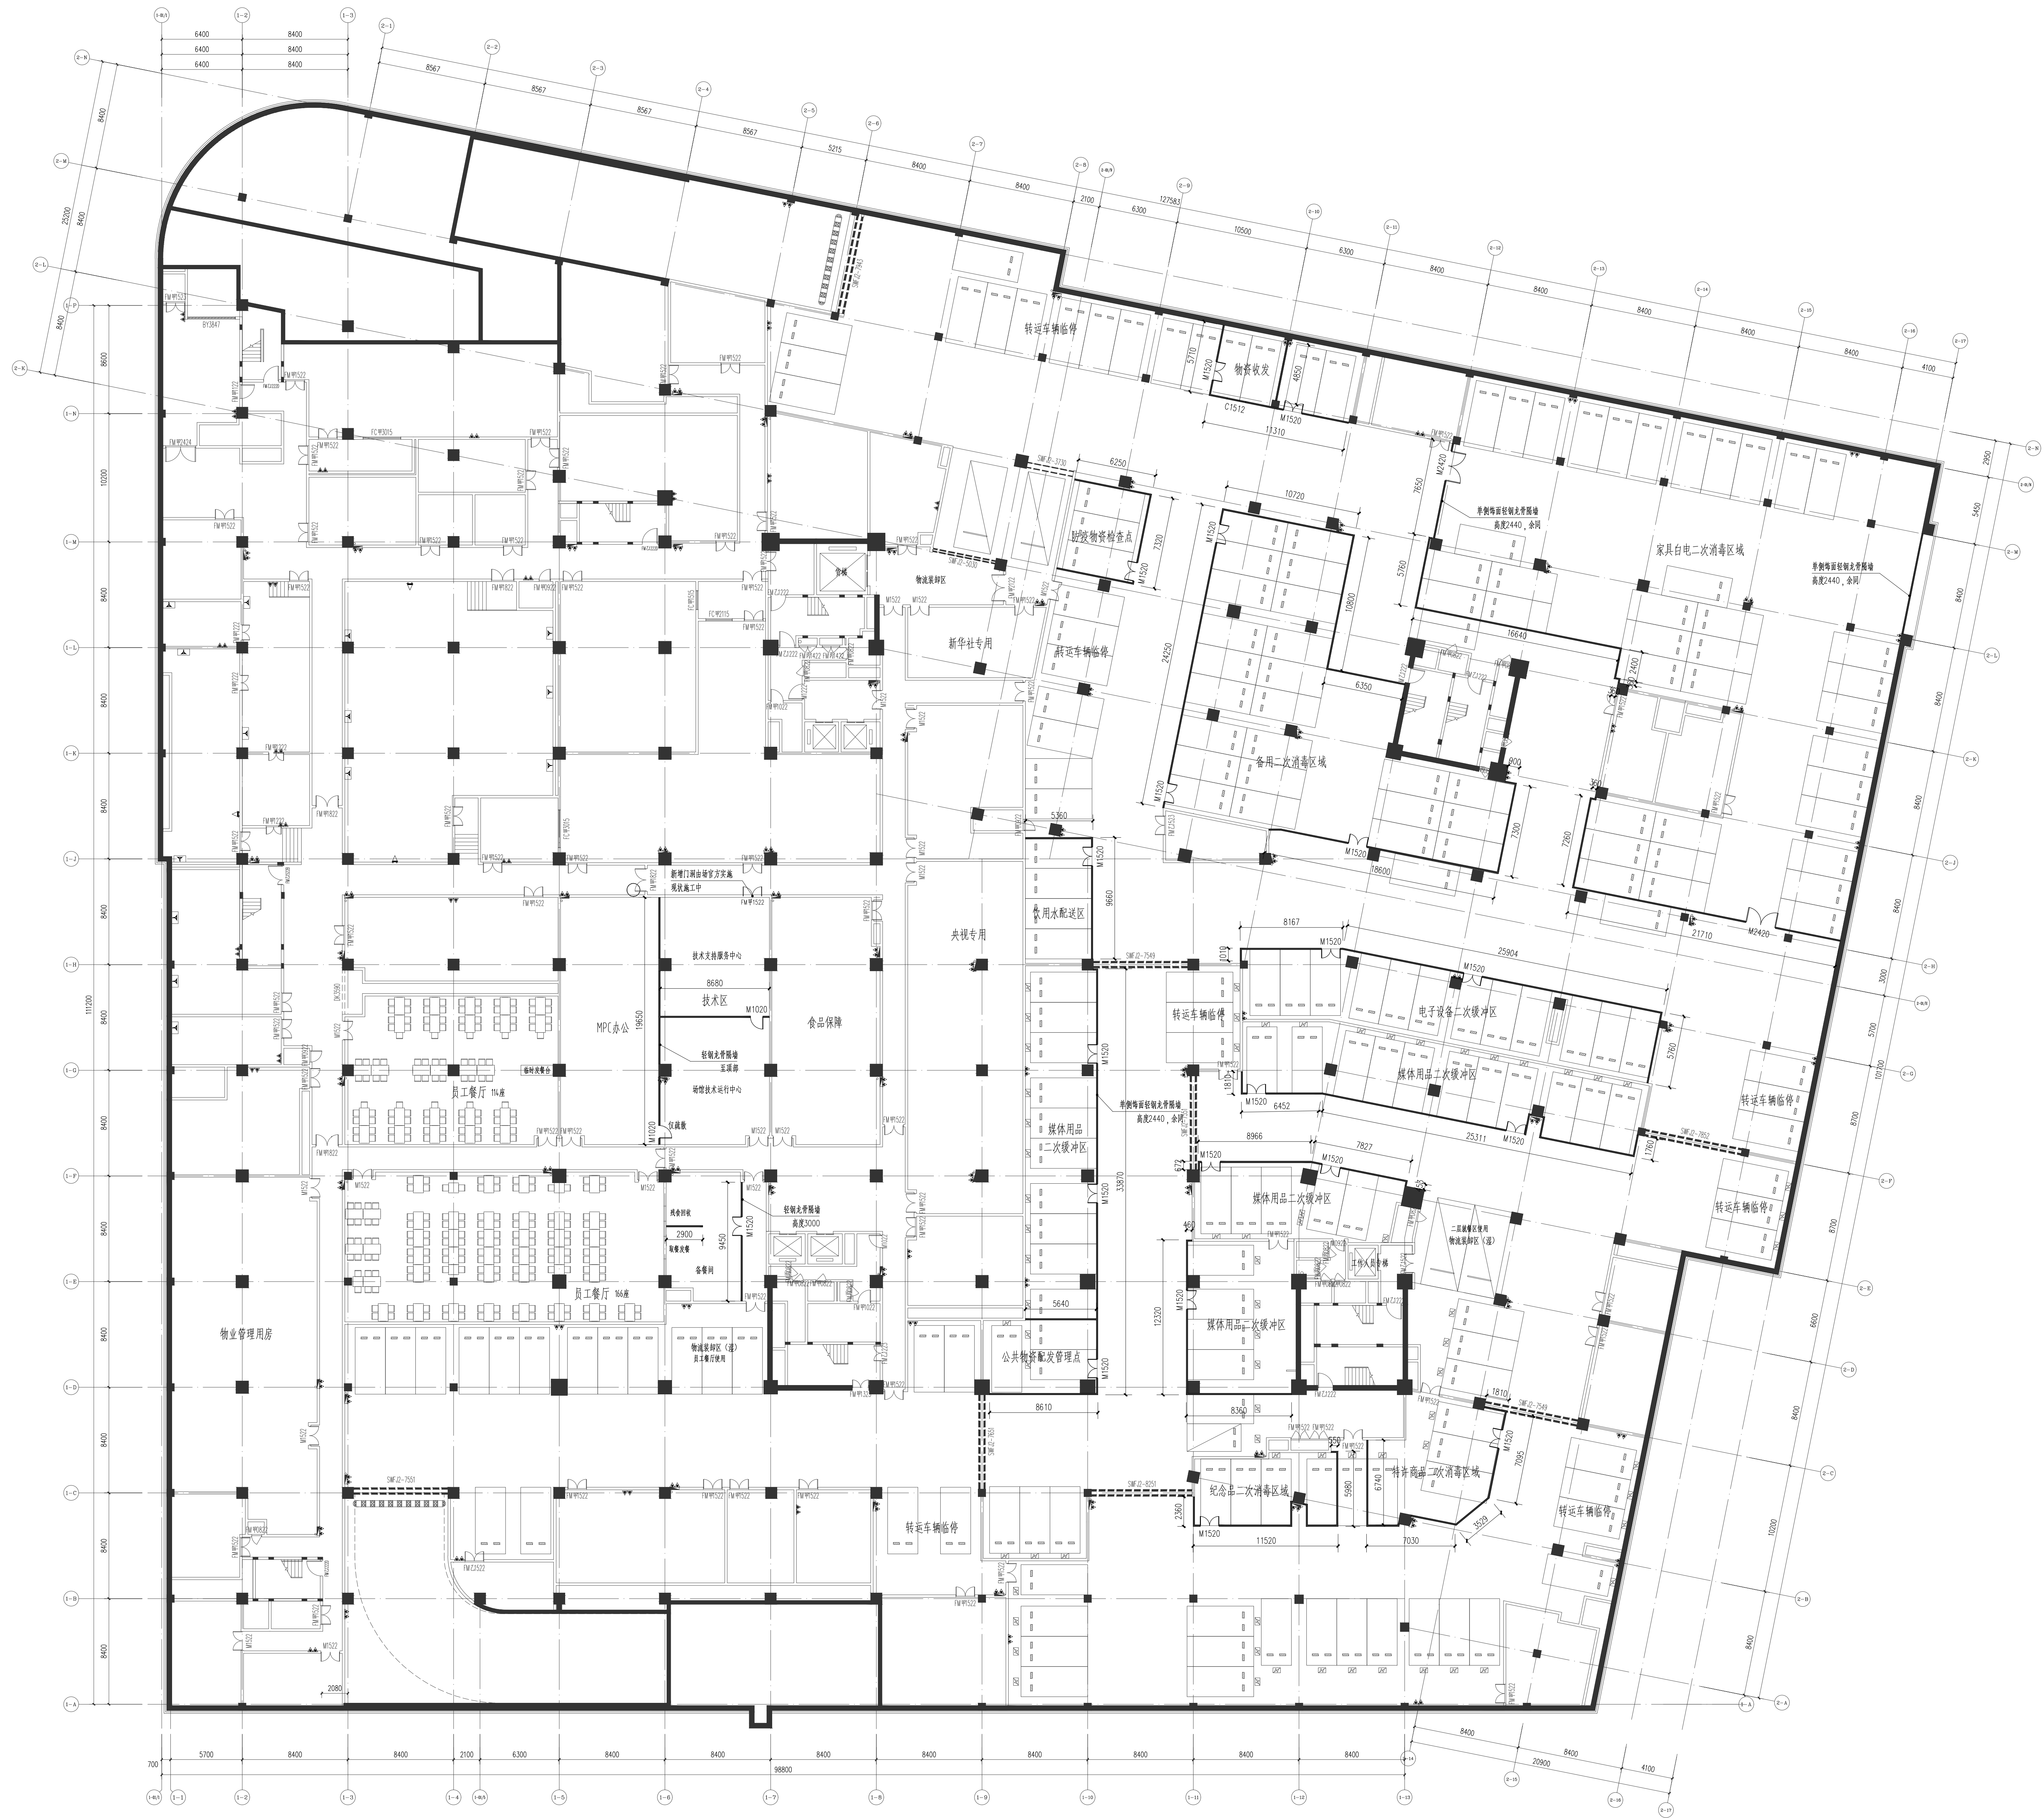

负一层平面布置图 1:200

[illegible]

注册执业栏	REGISTERED ARCHITECT/ENGINEER
姓名	NAME
资质证书号码	REGISTERED NO. (CERTIFICATE NO.)
注册印章号码	STAMP NO.
号: CD-20212856-F001	NO.
成都大运会主新闻中心装饰搭建	PROJECT TITLE
负责人	SUB ITEM
及单位	CLIENT
成都博雅文瑞文化传播有限公司	
表	DRAWING TITLE

负一层平面布置图					
位	mm	UNIT	附注	说明	DWG CATEGORY
号	1:200		图号	P-01	DWG NO.
编	2022.02	DATE	版本	A	ISS. NO.
设计	陈子颖				
校核	陈子颖				
审核	李露文				
专业负责人	陈子颖				
项目负责人	张媛				
审批	张媛				
签字	李树				

成都基准方中
成都基准方中建筑设计股份有限公司
Chengdu JZFC Architectural Design Co., Ltd.

中国 成都市 琉璃场8号中国广场A座7-14楼
 电话: +86 (28) 86533800 传真: +86 (28) 86582999
 17-15F, Tower A, Grand Plaza, No.8 Lili Road, Chengdu, P.R.C
 Tel: +86 (28) 86533800 Fax: +86 (28) 86582999

工程设计资质证书编号: A151016191

版 权 说 明
COPYRIGHT DECLARATION

此图版权为成都基准方中建筑设计股份有限公司所有,未经许可不得使用。

[illegible]

注册执业栏	REGISTERED ARCHITECT/ENGINEER
姓 名	NAME
注册证书号码	REGISTERED CERTIFICATE NO.
注册印章号码	STAMP NO.
设计号 CD-20121856-F001	JOB NO.
工程名称	PROJECT TITLE
成都大运会主新闻中心装饰搭建	
子项名称	SUB ITEM
建设单位	CLIENT
成都博雅文瑞文化传播有限公司	
图 名	DRAWING TITLE

三层平面布置图			
单位	mm	DBT	图号
比例	1:200	SCALE	图号
日期	2022.02	DATE	版本
设计	张子颖		
校核	张子颖		
审核	李源文		
专业负责人	张子颖		
设计负责人	张颖		
审核	张颖		
审定	李华		

中 方 基 准

成都基准方中建筑设计股份有限公司
Chengdu JZFZ Architectural Design Co., Ltd.

中国 成都市 武侯区新加坡路156号2-15楼
电话: +86 (28) 85533000 传真: +86 (28) 85530990
2-15F, Tower A Grand Plaza, No.156 Jiali Road, Chengdu, P.R.C
电: +86(28) 85533000 fax: +86(28) 85530990

工程设计资质证书编号: A151016191

电子文档编号: -

版 权 说 明
COPYRIGHT DECLARATION

此图所有权为成都基准方中建筑设计股份有限公司所有。未经许可不得使用。